




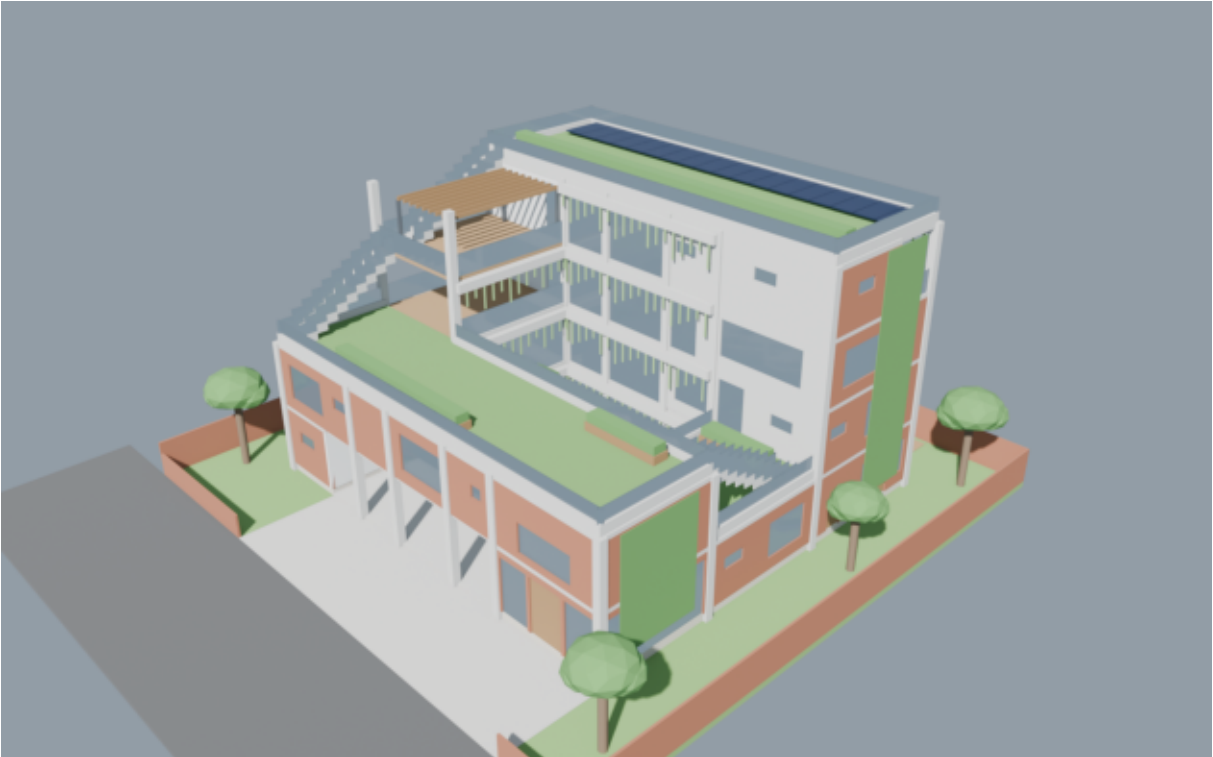

มุมมองทิศตะวันตกเฉียงเหนือ — ปกคลุมชั้นแบบเกลียว: W 1 ชั้น -> N 2 ชั้น -> E 3 ชั้น -> S 4 ชั้น ทุกหลังคาเป็นสวน + บันไดนอก

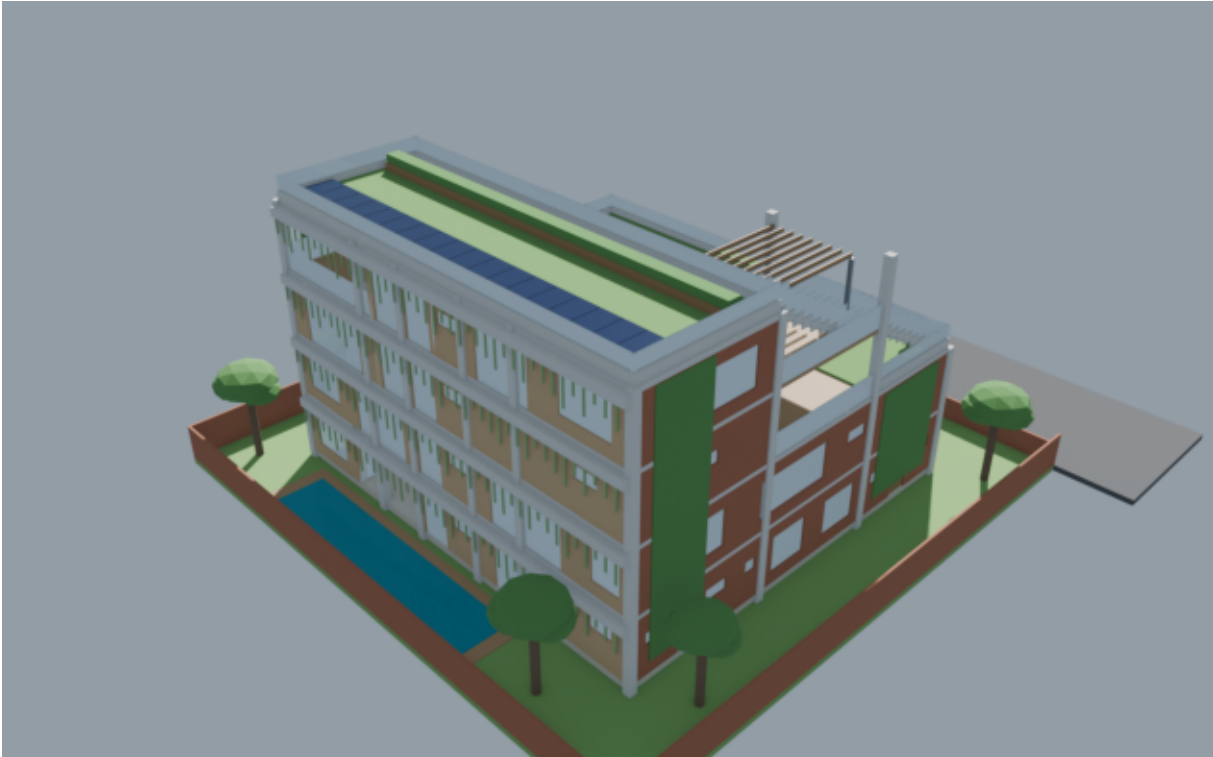

มุมมองทิศตะวันออกเฉียงใต้ — ปกติ 4 ชั้นหันสระ รางต้นไม้ห้อยหูกขอบขึ้น ผนังอิฐโชว์ + สวนแนวตั้ง

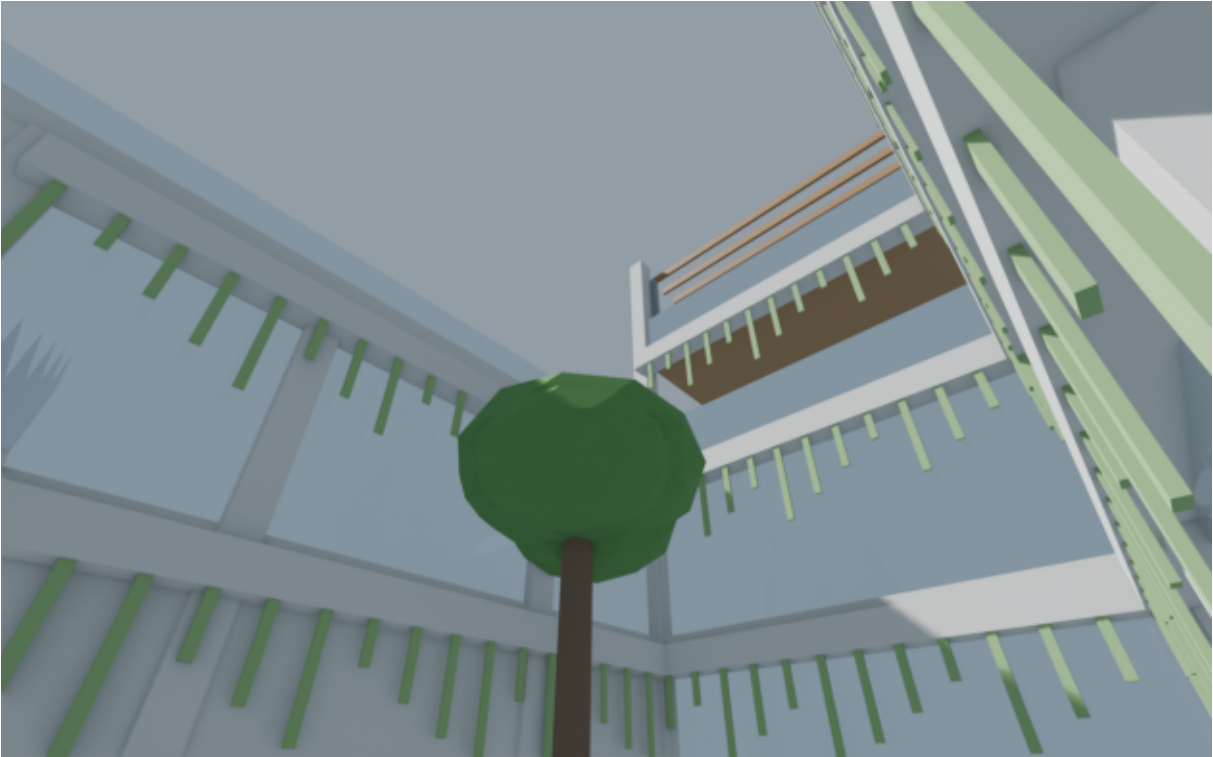



ในคอร์ตกลาง — มองขึ้นผ่านขอบพื้นที่ต้นไม้ห้อย ลาน BBQ ชั้น 4 และบันไดนอก



จากถนนทิศเหนือ — ปกติ 2 ชั้น (โรงรถ + Junior Suite) ผนังอิฐ หลังคาสวน และปกติดูด้านหลัง

โฉงแกรนเกลียว (1:250): ปกติ W-N-E-S สูง 1-2-3-4 ชั้น; บันไดนอก H1-H4 (แดง) ใต้สวนหลังคาตามเข็มนาฬิกา

โฉงแกรนรูปตัด A-A (y = 15.00, 1:250): คอร์ตเป็นบอลลูน + บันไดนอกใต้ชั้นสวนหลังคา

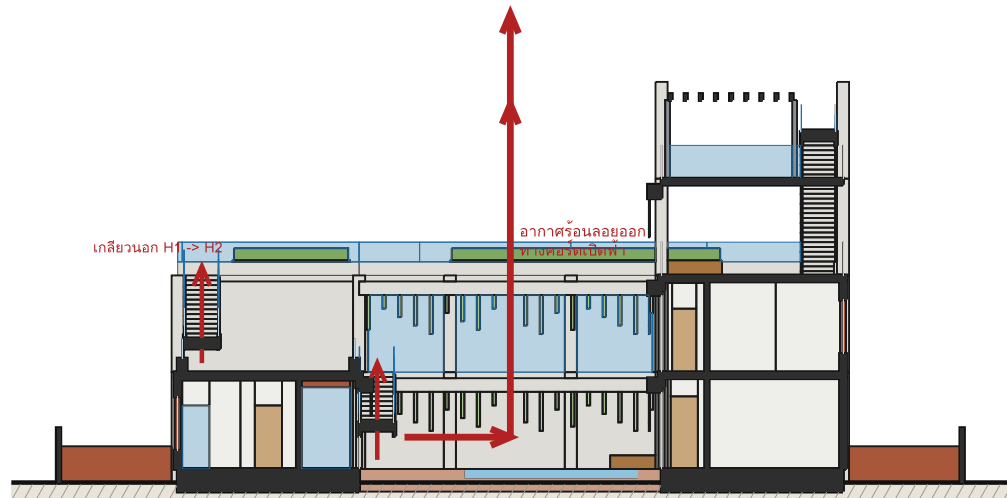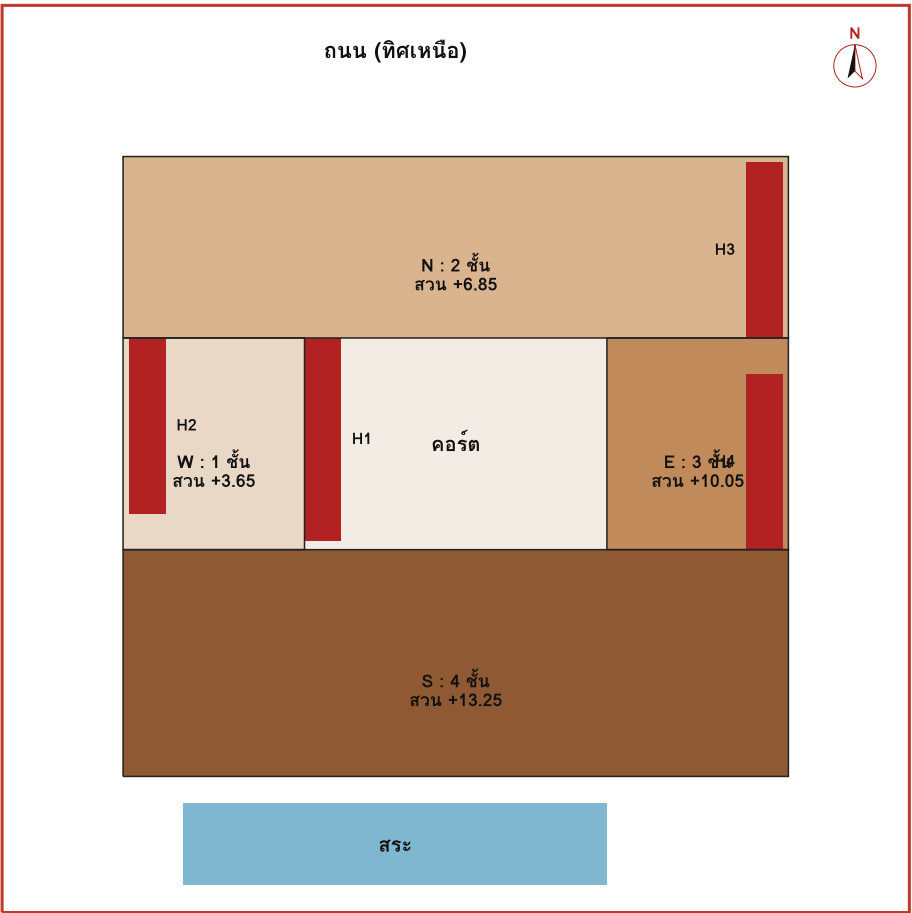

ลูกศร = เจตนารมณ์ออกแบบ (ลมปะจ่ากรุงเพทฯ ฤดูร้อน S/SW) — ยังไม่ได้พิสูจน์ด้วย CFD/การจำลองความร้อน

Rivera Paradise — ข้อเท็จจริงที่ควรจำได้

หัวข้อ	ข้อเท็จจริงจาก Archilizer / ArchDaily (ข้อความ + ภาพ)
ผู้ออกแบบ	AtelierM (สถาปนิกหลัก Mallas Mosquera) · ภูมิสถาปัตย์ Valeria Lennon
ที่ตั้ง / ปี / ขนาด	ย่าน Coghlan ปับโตโมเรส อาร์เจนตินา · 2026 · 200 ตร.ม. (ArchDaily)
ข้อจำกัดพิเศษ	ที่ดินแคบระหว่างอาคารข้างเคียง ในเขตอนุรักษ์ (APH) ต้องลดอาคารเดิม 30%
สิ่งที่ท้าทาย	ผนังอิฐโชว์ร่วมกับเพื่อนบ้าน (party walls) และเพดานโค้งสูง 2 ชั้นของเดิม
คอร์ต	"a large central courtyard that articulates the entire house" — แสง ลม ความลึก + บานกระจกเลื่อน + เสาสะท้อนน้ำ
การสัญจร	ได้แรงบันดาลใจจากบันไดเกลียวคู่ Château de Chambord · ทางในลานขึ้น + ทางนอกใต้ชั้นลานหลังคาสวนชั้นบันได (อิสระแต่ซ้อนกัน)
สีเขียว	หลังคาเขียว + สวนแนวตั้ง เปลี่ยนผนังข้างเคียงเป็นสวน สร้าง microclimate
จากภาพ / แบบ	คอร์ตอิฐ กระเบื้องต้นไม้ ต้นไม้ห้อยจากขอบขึ้นคอนกรีตโค้งมน ผนังไม้ เพดานอิฐ · ผิดชั้นล่าง / ขึ้นลอย / ขึ้นบน

การตีความ -> แบบบ้านหลังนี้

องค์ประกอบ	การตีความของเรา (ไม่ใช่คำอธิบายของสถาปนิก)
คอร์ตกลาง	คอร์ต 10.00 x 7.00 ม. เบ็ดหน้า อิฐ สะท้อนแสง ต้นไม้ · ทุกปีกหักกระจกเริ่มบานเข้าคอร์ต
เกลียวใน = บันไดหลัก + ลิฟต์ในปกติ	เกลียวนอก = บันไดนอก H1-H4 ใต้สวนหลังคาคอร์ต
หลังคาสวนชั้นบันได	ปกคลุมชั้นแบบเกลียว: W 1 ชั้น (สวน +3.65) -> N 2 ชั้น (+6.85) -> E 3 ชั้น (ลาน BBQ +10.05) -> S 4 ชั้น (ศาลาฟ้า +13.25)
อิฐเดิม 30%	ไม่มีอาคารเดิม: ผนังอิฐโชว์ด้านข้าง E/W + เพดานโค้งอิฐเหนือโถงสูง 2 ชั้น (ช่องใหม่ เป็นการอ้างถึง)
ต้นไม้ห้อย / แนวตั้ง	รางต้นไม้ขอบขึ้นทุกชั้น (ด้านใต้ + รอบคอร์ต) + สวนแนวตั้งบนผนังอิฐ
ไม่นำมาใช้	ขอบขึ้นโค้งมน (แบบต้นมูจาก — ต้องพัฒนาในแบบขยาย) · ขึ้นลอยแบบทวนหัวเตาแบบ

รายงานข้อจำกัด (ตรงไปตรงมา)

- ต้นแบบเป็นบ้าน 200 ตร.ม. บนที่ดินแคบในเขตอนุรักษ์ — บ้านนี้ใหญ่กว่าราว 5 เท่าและไม่มีอาคารเดิม อิฐ/โค้งอิฐเป็นการตีความของเรา
- โปรแกรมขัดกัน: Master ชั้น 3 แฉ Closet + Terrace ชั้น 4 -> Master duplex มีบันไดส่วนตัว; Party ชั้น 3 ย้ายไปชั้น 2 ติดครัว
- GFA 1098.00 vs โปรแกรม 984.70 (+11.5%); ส่วนเกิน = ห้องพิเศษ 36 + ห้องเครื่องสระ 18 (ชั้น 1) + ลอยเชิญชั้น 3 42 ตร.ม. (รองรับลาน BBQ) — ผลจากปวงแหวน
- เล็กกว่าโปรแกรมเกิน 10%: ครัวโชว์ -29%, ระเบียง Master -27%, ซักรีด -25%, Papry -17%, Walk-in -16%, โรงรถ 12%; ใหญ่กว่าโง่งตื้นรับ +50%, MEP +50%, แม่น้ำ +43%
- ทางหนีไฟ = บันไดนอกเกลียว H4->H1 ผ่านสวนหลังคา ลงดอร์ต -> ศาลา -> สวน; ดอยยืนข้อ 27 กับเขวาวอยรับสันทางผานลาดฟ้าคอร์ตโด
- บันไดนอกข้างถึงทุกชั้นจากสวน: ประตูสวนหลังคาคือช่องอากาศภายในแต่เปิดออกได้ทันที (slat) + ไฟส่องสว่างยกโล
- ชั้น 3: Walk-in และ Spa คู่มือพักของแบบบันได ต้องเพิ่มน้ำหนักประตู (ชั้น 3 ใช้เฉพาะ Master)
- หลังเปิดด้านเดียวลึกเกิน 4.20 ม. (ยกเว้นพร้อมเหตุผล) 10 ห้อง; ห้องที่ซ่อนเปิดไม่ถึง 10% ใช้พัดลมระบาย 12 ห้อง (A-12)
- หลังคาสวน 339 ตร.ม. ดินยี่น้ำ ~250-300 กก./ตร.ม. + กับซึมกับรากทุกชั้น; คอร์ตเปิดลม 4 ด้าน; ต้องมีท่อระบายและบ่อพักของตัวเอง
- ผนังอิฐหิติดะวันออก/ตะวันตกรับแดดบ่าย ต้องมีช่องอากาศ + ฉนวน; รางต้นไม้ห้อยต้องมีระบบน้ำหยดและทางเข้าดูแล
- ความกว้างถนนเดิม 8.00 ม.; ทางลาดโรงรถ +0.15 -> +0.45 ยังไม่เขียน; ไม่ทราบผังเมืองรวม/ข้อบัญญัติท้องถิ่น

แหล่งข้อมูลอ้างอิง

· archilizer.com/projects/rivera-paradise (ลิงก์ให้ใช้ใหม่) · archdaily.com/1054061 (ข้อมูลโครงการ + ภาพแบบ)
· ไม่ได้รับแบบร่างของโครงการ — ทุกมิติในชุดนี้ออกแบบใหม่

H3A DESIGN AND BUILD

X-UNIT Architecture Lab

โครงการ

WELL-RIVERA 30x30

Executive Luxury Villa
บ้านเดี่ยว 4 ชั้น ผ่านเกณฑ์
WELL for Residential (เจดนา)

ที่ดิน 30.00 x 30.00 ม. = 225 ตร.ว.
ถนนสาธารณะทิศเหนือ (ถนนติ 8.00 ม.)

แนวคิด

ตีความจาก Rivera Paradise (AtelierM):
คอร์ตกลาง + บันไดเกลียวคู่ (ใน/นอก)
+ ปกคลุมชั้นแบบเกลียว หลังคาสวนทุกชั้น
+ ผนังอิฐโชว์ + เพดานโค้งอิฐ

ระดับ

±0.00 ถนน · F1 +0.45 · F2 +3.65
F3 +6.85 · F4 +10.05
ลาดฟ้า +13.25 · ราว +14.35
โค้งอิฐ สปริง +5.45 ยอด +6.65

หมายเหตุ


- หน่วยเป็นมิลลิเมตร เว้นแต่ระบุ
- ระดับอ้างอิงถนนที่พื้น ±0.00
- ห้ามวัดขนาดจากแบบ ใช้ตัวเลขกำกับ
- แบบระดับ Design Development
- ต้องให้สถาปนิกและวิศวกรผู้ได้รับใบอนุญาตตรวจสอบและลงนามก่อนยื่นขออนุญาต

ชื่อแผ่น

แนวคิด Rivera Paradise
-> บ้านเกลียวคู่รอบคอร์ต + ข้อจำกัด

มาตราส่วน: ไม่มีมาตราส่วน

วันที่ 6 ต.ค. 2569 ฉบับ v1 / DD

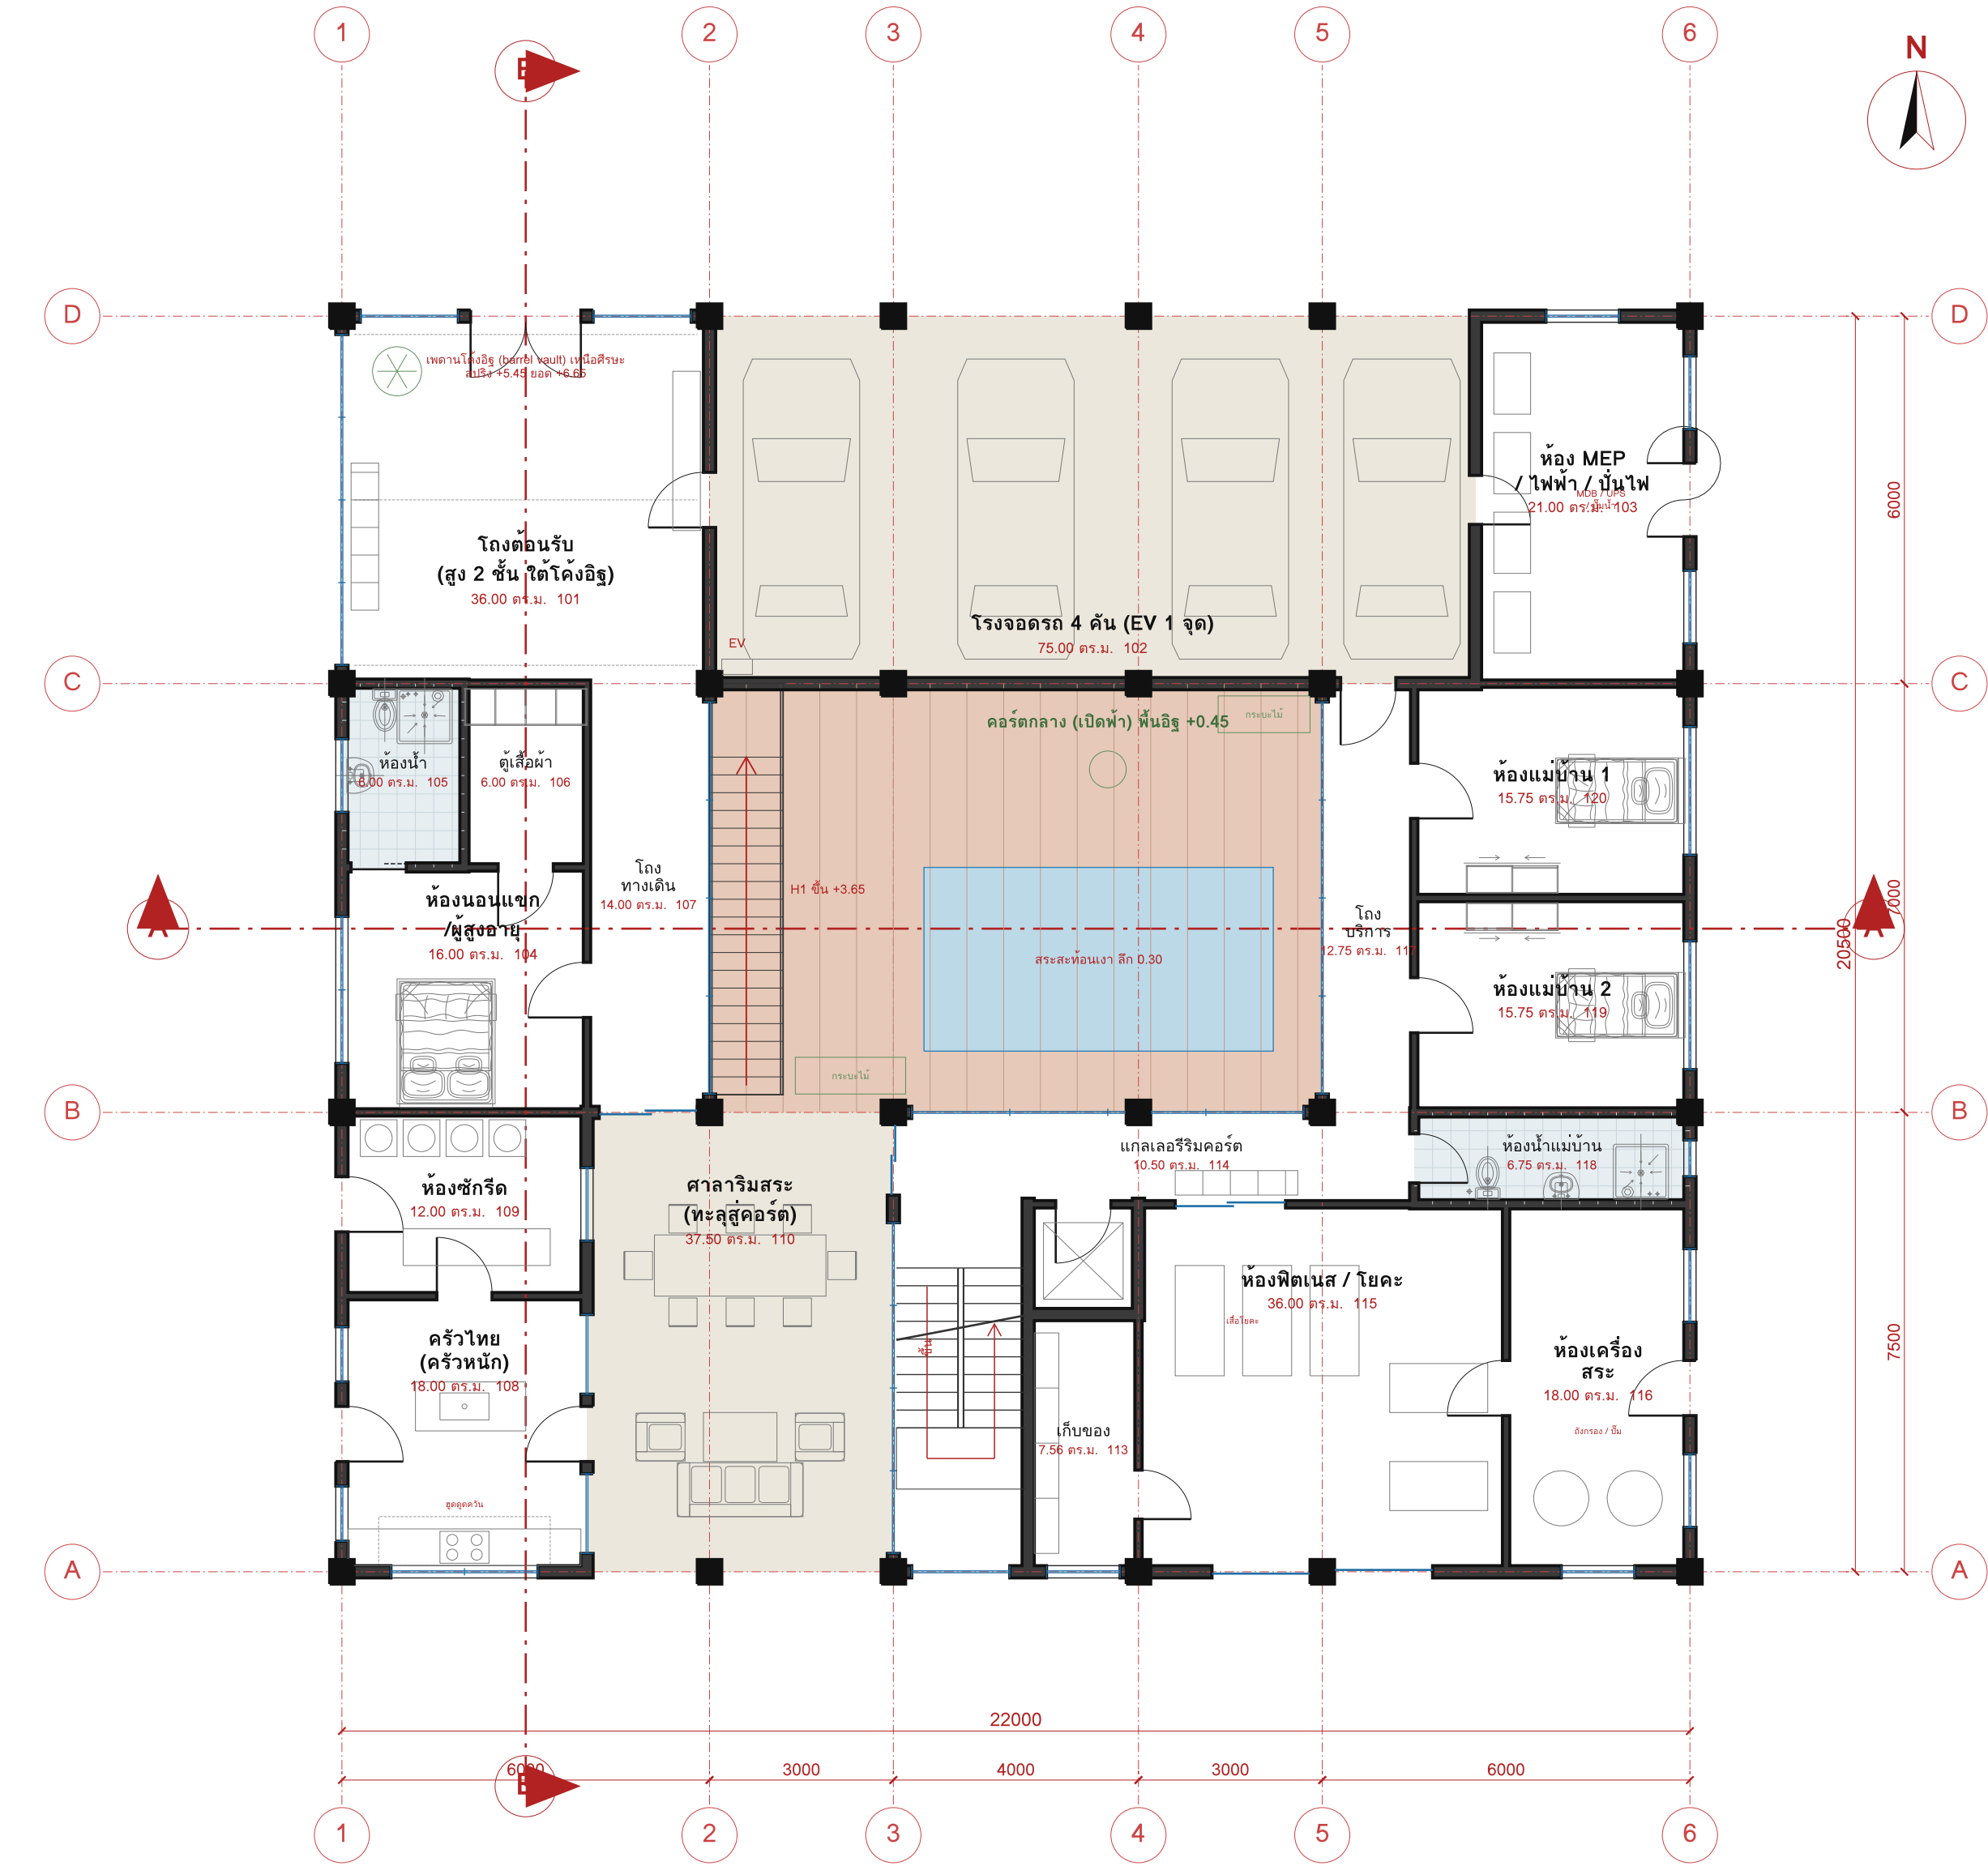

ผังพื้นชั้น 1 (FFL +0.45) 1:100



ตารางห้อง ชั้น 1

รหัส	ห้อง	ขนาด ม.	ตร.ม. ประเภท
101	โถงต้อนรับโดโงง (สูง 2 ชั้น)	6.00 x 6.00	36.00 สี่เหลี่ยม
102	โรงจอดรถ 4 คัน	12.50 x 6.00	75.00 จอดรถ
103	ห้อง MEP / ไฟฟ้า / เครื่องปรับอากาศ	3.50 x 6.00	21.00 บริการ
104	ห้องนอนแขก/ผู้สูงอายุ	4.00 x 4.00	16.00 ห้องใช้งาน
105	ห้องน้ำห้องแขก	2.00 x 3.00	6.00 ห้องน้ำแขก
106	ตู้เสื้อผ้าห้องแขก	2.00 x 3.00	6.00 บริการ
107	โถงทางเดินรีนคอร์ (ตะวันออก)	2.00 x 7.00	14.00 สี่เหลี่ยม
108	ครัวไทย (ครัวหลัก)	4.00 x 4.50	18.00 ห้องใช้งาน
109	ห้องซักล้าง	4.00 x 3.00	12.00 บริการ
110	ศาลาริมสระ (ทะเลสาบ)	5.00 x 7.50	37.50 ที่ภายนอก
111	บันไดที่พัก (บันไดใน)	2.20 x 6.00	13.20 บันได
112	ลิฟต์บ้าน	1.80 x 1.80	3.24 ลิฟต์
113	ห้องเก็บของ / อุปกรณ์สระ	1.80 x 4.20	7.56 บริการ
114	แกลเลอรีรีนคอร์ ชั้น 1	7.00 x 1.50	10.50 สี่เหลี่ยม
115	ห้องพิตเนซ / โยคะ รีนสระ	6.00 x 6.00	36.00 ห้องใช้งาน
116	ห้องเครื่องสระ / เก็บของ	3.00 x 6.00	18.00 บริการ
117	โถงบริการ (ตะวันออก)	1.50 x 8.50	12.75 สี่เหลี่ยม
118	ห้องน้ำแม่บ้าน	4.50 x 1.50	6.75 ห้องน้ำแขก
119	ห้องแม่บ้าน 2	4.50 x 3.50	15.75 ห้องใช้งาน
120	ห้องแม่บ้าน 1	4.50 x 3.50	15.75 ห้องใช้งาน

ภาพชั้น 1	ตร.ม.
พื้นที่จอดรถ	268.50
ที่ภายนอก	37.50
จอดรถ	75.00
รวม	381.00
บันไดหนีไฟภายนอก (ไม่รวม)	0.00

หมายเหตุ

- ทางเข้าที่ดิน -> โถงต้อนรับสูง 2 ชั้นใต้โถงโดโงง -> โถงทางเดินรีนคอร์ -> ศาลาริมสระ -> แกลเลอรี -> บันไดหลัก/ลิฟต์
- คอร์ตกลาง 10.00 x 7.00 ม. เปิดฟ้า ขึ้นบันได สระห้องนาง ดันไม้ - บันไดนอก H1 เริ่มที่คอร์ตชั้นสวนหลังคาปีกตะวันออก
- ศาลาริมสระทะลุจากสระรีนคอร์ (ทางบันได-เหนือ) - ห้องพิตเนซ/โยคะรีนสระ (ไม่อยู่ในโปรแกรม - ส่วนเกินจากงบประมาณ)
- สิ่งบริการระเนรก: แม่บ้าน 2 ห้อง ห้องน้ำ ห้องเครื่องสระ ต่อโรงรถ - ครัวไทย/ซักล้างเปิดสู่ลานบริการทิศตะวันออก
- โรงจอดรถ 4 คัน @3.10 ม. ลึก 6.00 ม. + จุดชาร์จ EV (WELL R-A09); ทางลาด 1:12 ต้องเพิ่ม

H3A DESIGN AND BUILD

X-UNIT Architecture Lab

โครงการ

WELL-RIVERA 30x30

Executive Luxury Villa

บ้านเดี่ยว 4 ชั้น ผ่านเกณฑ์

WELL for Residential (เจดนา)

ที่ดิน 30.00 x 30.00 ม. = 225 ตร.ว.

ถนนสาธารณะที่ดิน (สมมติ 8.00 ม.)

แนวคิด

ตีความจาก Rivera Paradise (AtelierM):

คอร์ตกลาง + บันไดเกลียวคู่ (ใน/นอก)

+ ปกคลุมแบบเกลียว หลังคาส่วนทุกชั้น

+ ผนังอิฐโชว์ + เพดานโดโงง

ระดับ

±0.00 ถนน - F1 +0.45 - F2 +3.65

F3 +6.85 - F4 +10.05

ลาดฟ้า +13.25 - ราว +14.35

โดโงง สบึง +5.45 ยอด +6.65

หมายเหตุ

- หน่วยเป็นมิลลิเมตร เว้นแต่ระบุ
- ระบับ้างลิ้นถนนที่ ±0.00
- ห้ามวัดขนาดจากแบบ ใช้ตัวเลขกำกับ
- แบบระดับ Design Development
- ต้องให้สถาปนิกและวิศวกรผู้ได้รับใบอนุญาตตรวจสอบและลงนามก่อนยื่นขออนุญาต


ชื่อแผ่น

ผังพื้นชั้น 1

(FFL +0.45)

มาตราส่วน 1:100

วันที่ 6 ต.ค. 2569 ฉบับ v1 / DD

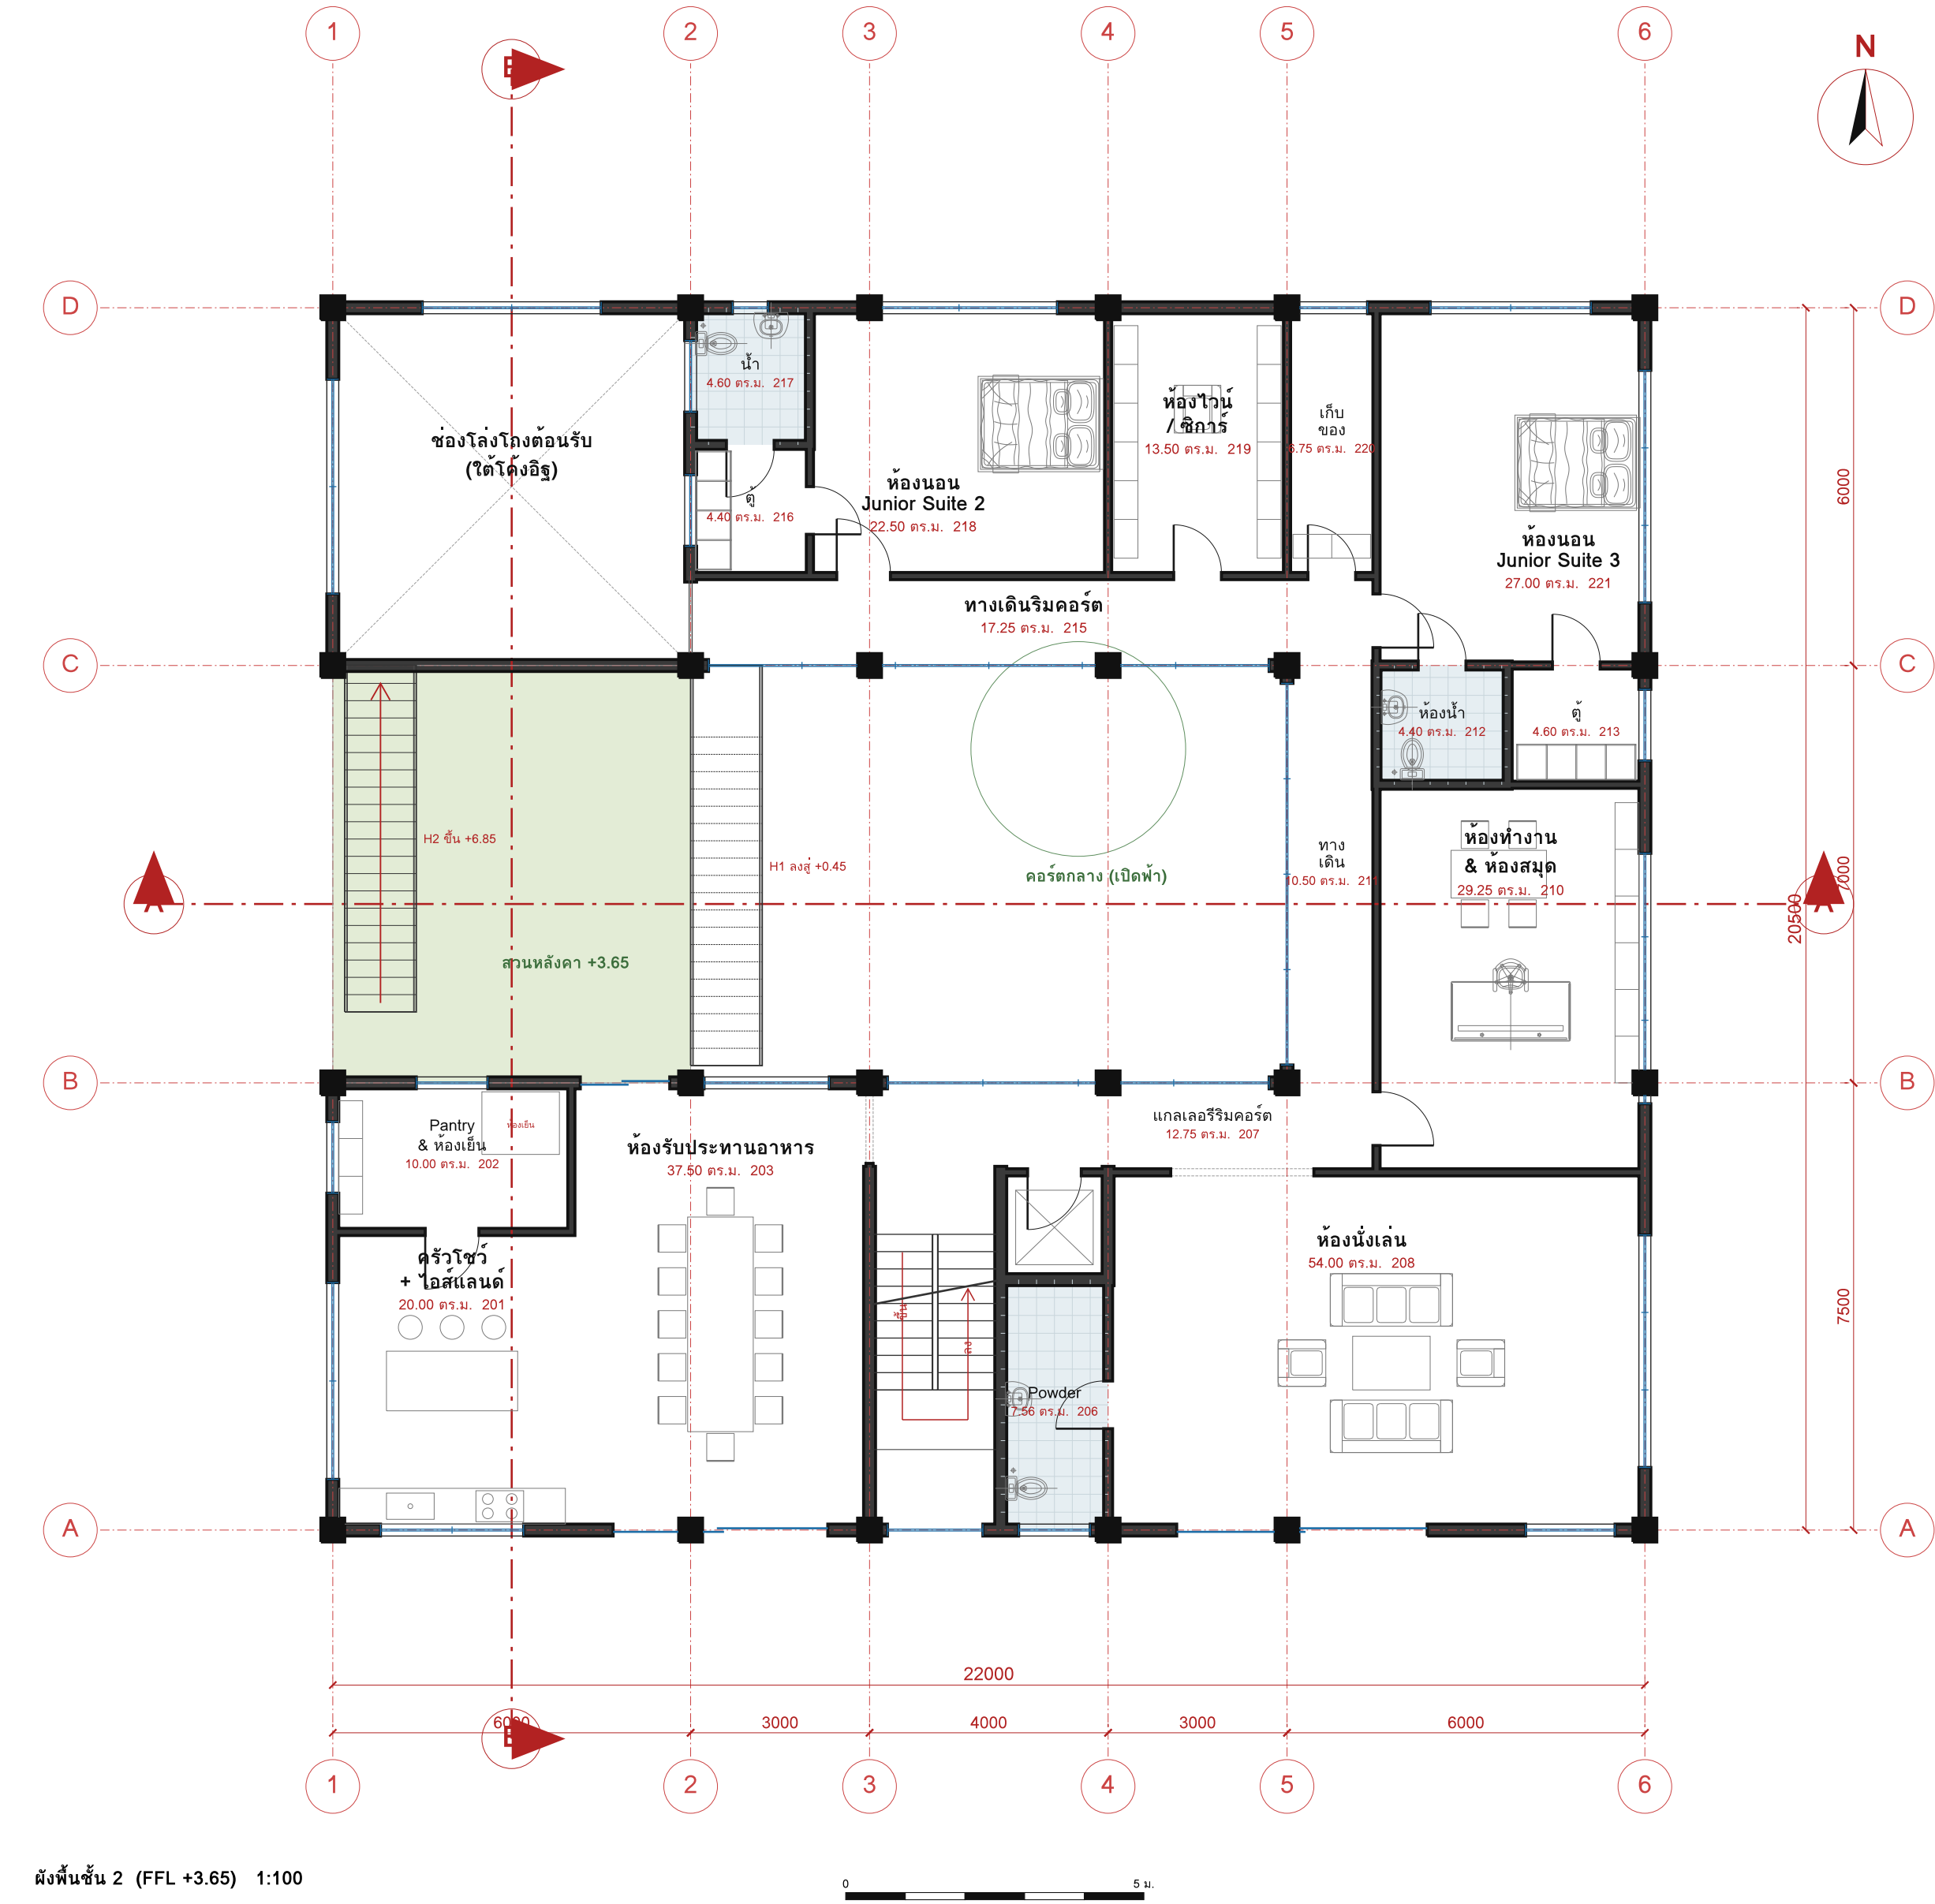

ผังพื้นชั้น 2 (FFL +3.65) 1:100

ตารางห้อง ชั้น 2

รหัส	ห้อง	ขนาด ม.	ตร.ม.	ประเภท
201	ครัวโชว์ + ไอส์แลนด์	4.00 x 5.00	20.00	ห้องใช้งาน
202	Walk-in Pantry & ห้องเย็น	4.00 x 2.50	10.00	บริการ
203	ห้องรับประทานอาหาร	5.00 x 7.50	37.50	ห้องใช้งาน
204	บันไดหลัก (เกสยาวใน)	2.20 x 6.00	13.20	บันได
205	ลิฟต์บ้าน	1.80 x 1.90	3.24	ลิฟต์
206	ห้องน้ำเชก (Powder)	1.80 x 4.20	7.56	ห้องโถงเปิด
207	เกสเลิฟริมคอร์ต ชั้น 2	8.50 x 1.50	12.75	บริการ
208	ห้องนั่งเล่น	6.50 x 6.00	54.00	ห้องใช้งาน
210	ห้องทำงาน & ห้องสมุด	4.50 x 6.50	29.25	ห้องใช้งาน
211	ทางเดินคอร์ต (สวนนอก) ชั้น 2	1.50 x 7.00	10.50	บริการ
212	ห้องน้ำ Junior Suite 3	2.20 x 2.00	4.40	ห้องโถงเปิด
213	ตู้เสื้อผ้า Junior Suite 3	2.30 x 2.00	4.60	บริการ
214	ห้องโถงคอร์ตชั้นรับ (โถงฮอลล์)	6.00 x 6.00	36.00	โถงโถง
215	ทางเดินคอร์ตชั้นรับ (โถงฮอลล์) ชั้น 2	11.50 x 1.50	17.25	บริการ
216	ตู้เสื้อผ้า Junior Suite 2	2.00 x 2.20	4.40	บริการ
217	ห้องน้ำ Junior Suite 2	2.00 x 2.30	4.60	ห้องโถงเปิด
218	ห้องนอน Junior Suite 2	5.00 x 4.50	22.50	ห้องใช้งาน
219	ห้องรับ / บริการ	3.00 x 4.50	13.50	บริการ
220	ห้องเก็บของชั้น 2	1.50 x 4.50	6.75	บริการ
221	ห้องนอน Junior Suite 3	4.50 x 6.00	27.00	ห้องใช้งาน

ภาพชั้น 2	ตร.ม.
พื้นที่ปิดล้อม	303.00
ที่ภายนอก	0.00
จอดรถ	0.00
รวม	303.00
บันไดหนีไฟภายนอก (ไม่รวม)	0.00

หมายเหตุ

- ปกติ: ครัวโชว์ -> ห้องอาหาร 12 ที่นั่ง -> เกสเลิฟ -> ห้องนั่งเล่น หันหน้าบ้านเชื่อมติดกับ -> กระจกเต็มบานสู่คอร์ต
- ห้องอาหารเปิดสู่สวนหลังคาปีกตะวันตก (+3.65) = จุดเชื่อมกับสวนนอก H2 -> Pantry ย้ายจากชั้น 3 มาติดครัว
- ปกติ: Junior Suite 2-3 ห้องรับ ห้องเก็บของ เข้าจากทางเดินกระจกคอร์ต -> ห้องโถงคอร์ตชั้นรับโถงโถง
- ปกติ: สวนนอก: ทางเดินริมคอร์ต + ห้องทำงาน & ห้องสมุด (มุมตะวันออกเฉียงใต้)

H3A DESIGN AND BUILD

X-UNIT Architecture Lab

โครงการ

WELL-RIVERA 30x30

Executive Luxury Villa

บ้านเดี่ยว 4 ชั้น ผ่านเกณฑ์

WELL for Residential (เจดนา)

ที่ดิน 30.00 x 30.00 ม. = 225 ตร.ว.

ถนนสาธารณะที่ดินเนื้อ (สมมติ 8.00 ม.)

แนวคิด

ตีความจาก Rivera Paradise (AtelierM):

คอร์ตกลาง + บันไดเกสยาวคู่ (ใน/นอก)

+ ปกติชั้นแบบเกสยาว หลังคาส่วนทุกชั้น

+ ผนังโชว์ + เพดานโถงฮอลล์

ระดับ

±0.00 ถนน -> F1 +0.45 -> F2 +3.65

F3 +6.85 -> F4 +10.05

ลาดหน้า +13.25 -> ราว +14.35

โถงฮอลล์ สปริง +5.45 ยอด +6.65

หมายเหตุ

- หน่วยงานเป็นผลิตภัณฑ์ เว้นแต่ระบุ
- ระดับอ้างอิงถนนพื้นที่ดิน ±0.00
- ห้ามวัดขนาดจากแบบ ใช้ตัวเลขกำกับ
- แบบระดับ Design Development
- ต้องให้สถาปนิกและวิศวกรผู้ได้รับใบอนุญาตตรวจสอบและลงนามก่อนยื่นขออนุญาต


ชื่อแผ่น

ผังพื้นชั้น 2

(FFL +3.65)

มาตราส่วน 1:100

วันที่ 6 ค.ศ. 2569 ฉบับ v1 / DD

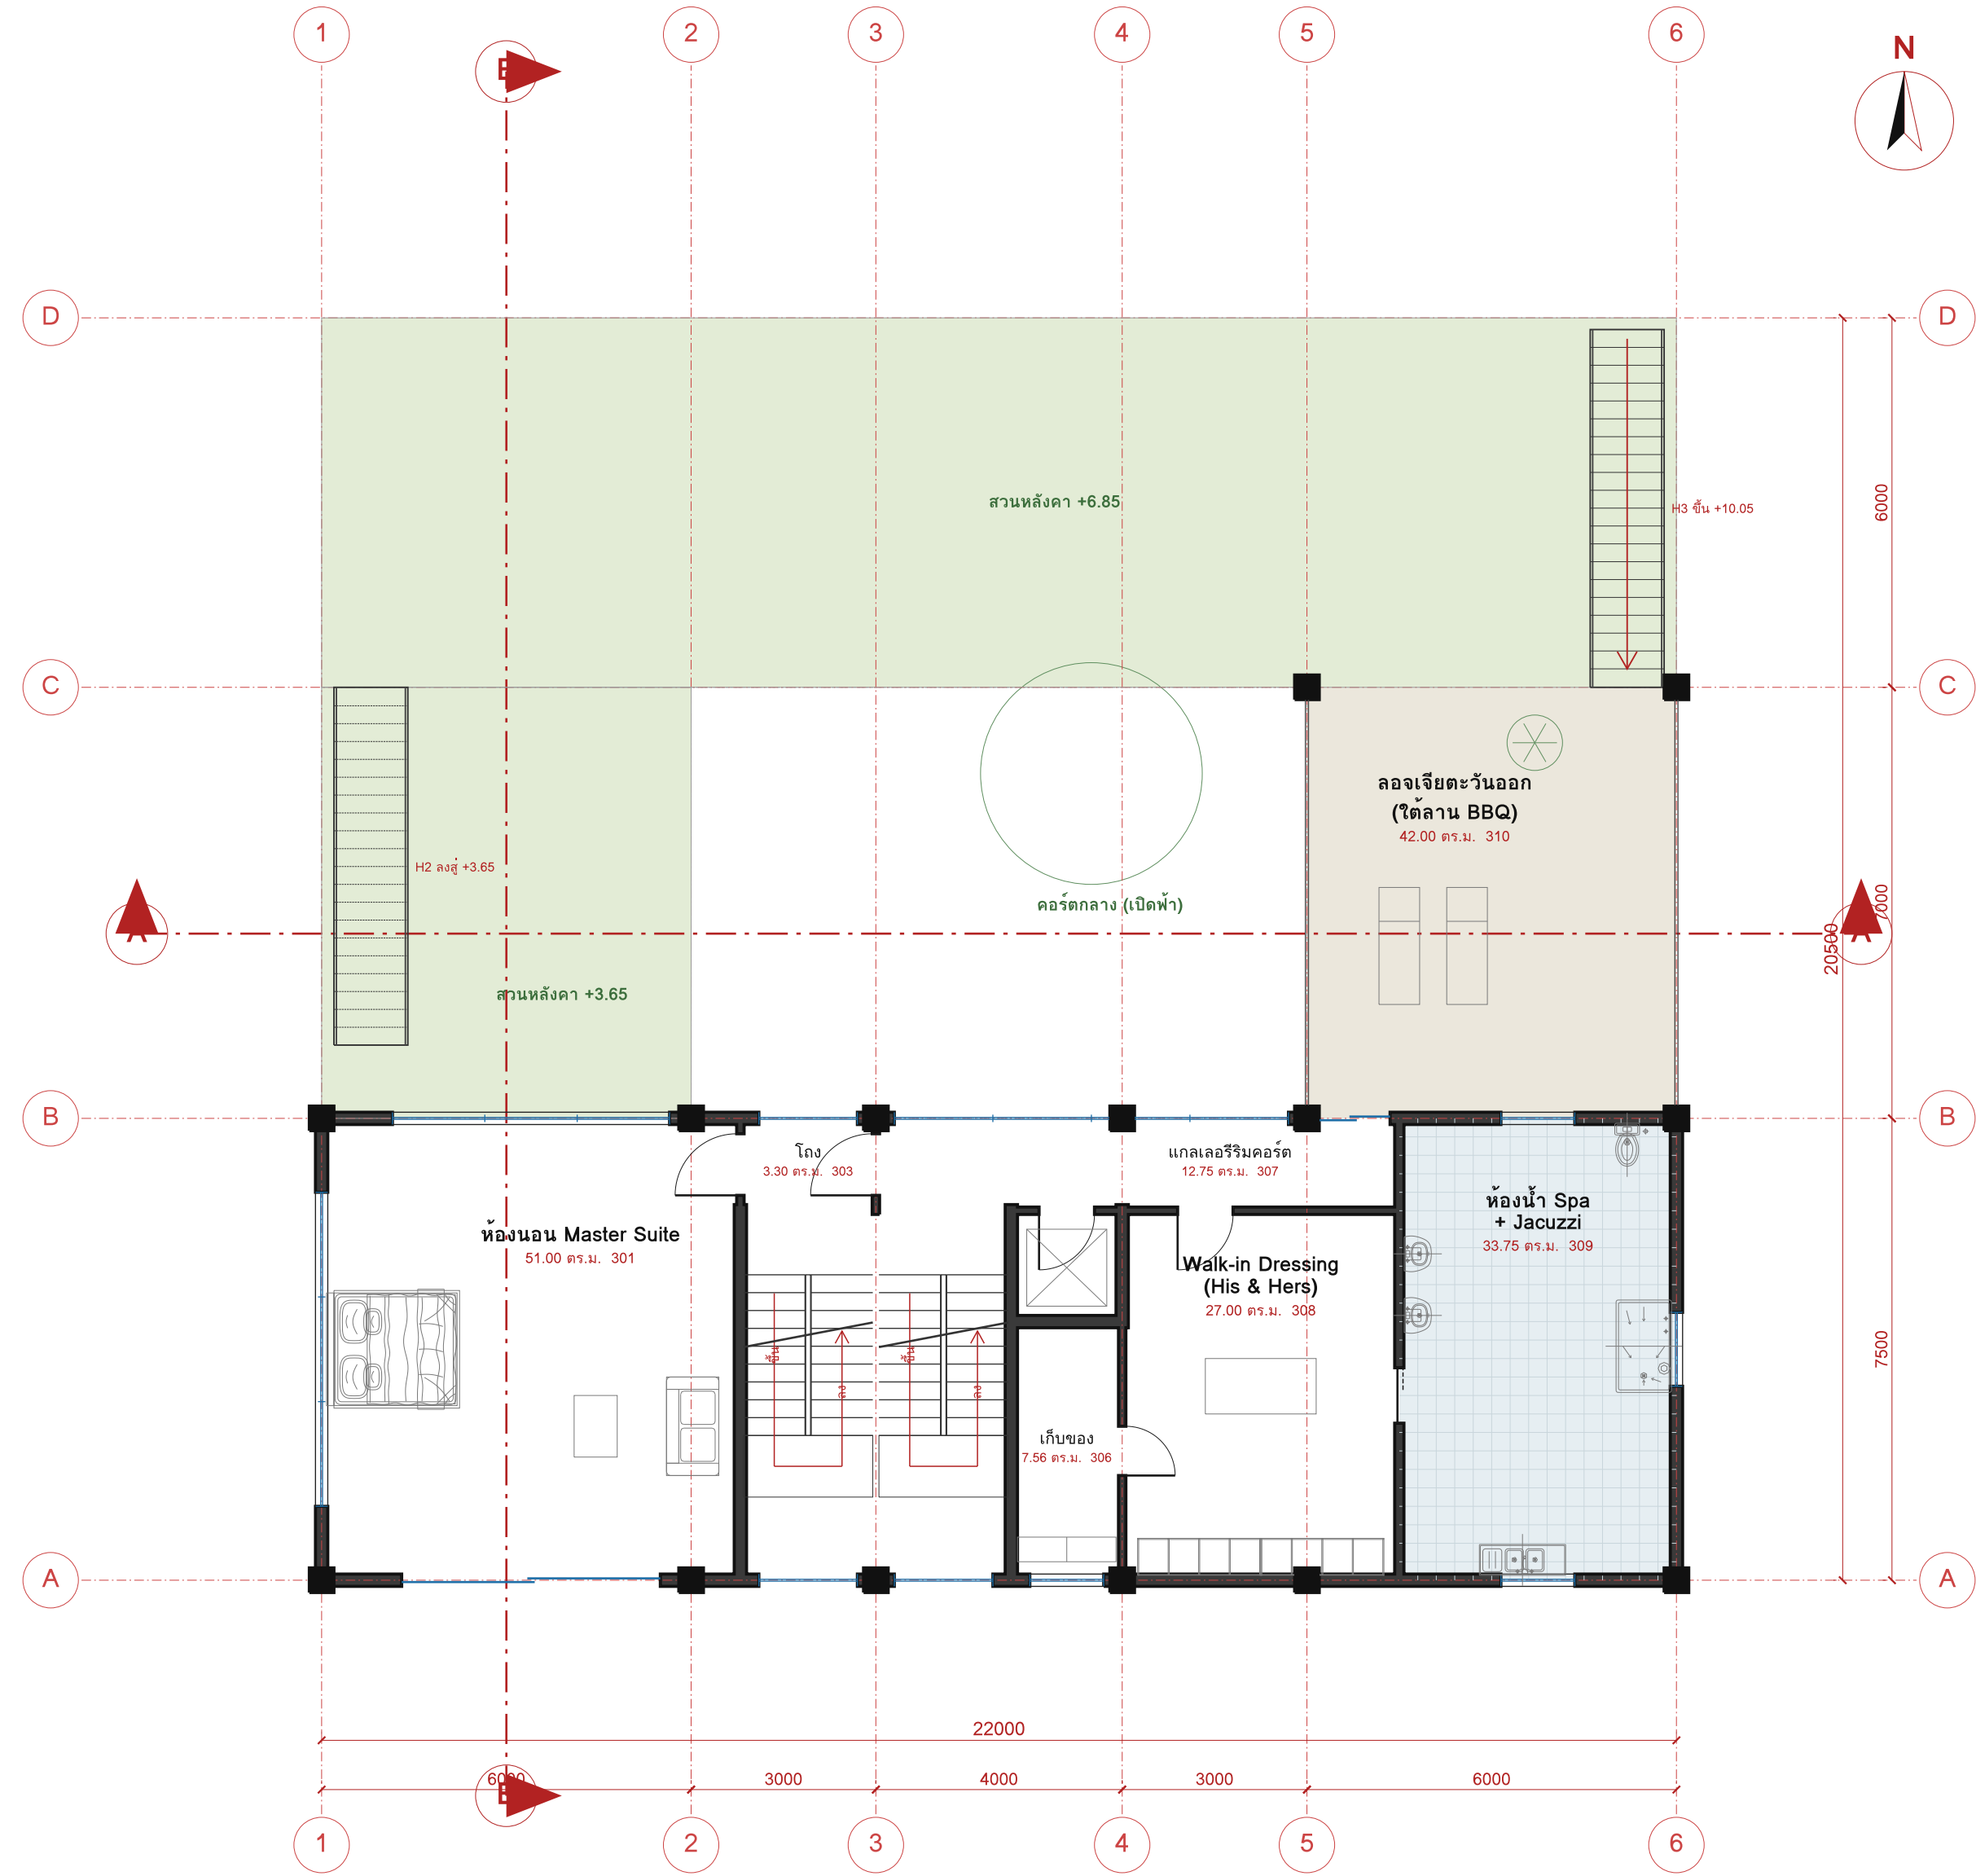

ผังพื้นชั้น 3 (FFL +6.85) 1:100



ตารางห้อง ชั้น 3

รหัส	ห้อง	ขนาด ม.	ตร.ม.	ประเภท
301	ห้องนอน Master Suite	6.80 x 7.50	51.00	ห้องใช้งาน
302	บันไดส่วนค้ำ Master	2.20 x 6.00	13.20	บันได
303	โถงห้อง Master	2.20 x 1.50	3.30	สัญจร
304	บันไดหลัก (เกสยาวใน)	2.20 x 6.00	13.20	บันได
305	ลิฟต์บ้าน	1.80 x 1.90	3.24	ลิฟต์
306	ห้องเก็บของชั้น 3	1.80 x 4.20	7.56	บริการ
307	แกลเลอรีริมคอร์ต ชั้น 3	8.50 x 1.50	12.75	สัญจร
308	Walk-in Dressing (His & Hers)	4.50 x 6.00	27.00	บริการ
309	ห้องน้ำ Spa + Jacuzzi	4.50 x 7.50	33.75	ห้องใช้สอย
310	ลounge ระเบียงนอก (ใต้ถุน BBQ)	6.00 x 7.00	42.00	ที่ภายนอก

ส่วนชั้น 3	ตร.ม.
พื้นที่ใช้สอย	165.00
ที่ภายนอก	42.00
จอยท์	0.00
รวม	207.00
บันไดหนีไฟภายนอก (ไม่รวม)	0.00

หมายเหตุ

- ชั้น Master: ห้องนอน (สว.วันค) — เกมบันได — Walk-in + Spa (สว.วันค) ต่อกับด้วยแกลเลอรีริมคอร์ต; บันไดส่วนค้ำขึ้นชั้น 4
- ส่วนหลังคาเปิด (+6.85) เพื่อดูวิวและใช้สอย; บันไดนอก H3 ขึ้นลาน BBQ
- ลounge ระเบียงนอกใต้ถุน BBQ (ส่วนเก็บโปรแกรม) เชื่อมแกลเลอรีกับส่วนหลังคาเหนือ = ทางหนีไฟชั้น 3
- ห้องที่เห็นคอร์ตโรมานอฟลิ้มเพื่อความเป็นส่วนตัวจากบันไดนอก

H3A DESIGN AND BUILD

X-UNIT Architecture Lab

โครงการ

WELL-RIVERA 30x30

Executive Luxury Villa
บ้านเดี่ยว 4 ชั้น ผ่านเกณฑ์
WELL for Residential (เจดนา)

ที่ดิน 30.00 x 30.00 ม. = 225 ตร.ว.
ถนนสาธารณะที่ดิน (สมมติ 8.00 ม.)

แนวคิด

ตีความจาก Rivera Paradise (AtelierM):
คอร์ตกลาง + บันไดเกสยาวคู่ (ใน/นอก)
+ ปกติชั้นแบบเกสยาว หลังคาส่วนทุกชั้น
+ ผนังอิฐโชว์ + เพดานโค้งอิฐ

ระดับ

±0.00 ถนน · F1 +0.45 · F2 +3.65
F3 +6.85 · F4 +10.05
ลาดฟ้า +13.25 · ราว +14.35
โค้งอิฐ สปริง +5.45 ยอด +6.65

หมายเหตุ

- ผนังเป็นอิฐลิมสเตอร์ เว้นแต่ระบุ
- ระดับล่างลิ้นถนนที่พื้น ±0.00
- ห้ามวัดขนาดจากแบบ ใช้ตัวเลขกำกับ
- แบบระดับ Design Development
- ต้องให้สถาปนิกและวิศวกรผู้ได้รับใบอนุญาตตรวจสอบและลงนามก่อนยื่นขออนุญาต

ชื่อแผ่น

ผังพื้นชั้น 3
(FFL +6.85)

มาตราส่วน 1:100

วันที่ 6 ต.ค. 2569 ฉบับ v1 / DD



สรุปชั้น 4	คร. ม.
พื้นที่ปิดล้อม	144.60
ถึงภายนอก	62.40
จัดสรร	0.00
รวม	207.00
บันทึกหนี้ไฟภายนอก (ไม่รวม)	0.00

Master duplex: บันไดส่วนตัว -> Closet -> ระเบียง Master ในบริเวณใต้ (อ่าแป๊ะ)
Upper Gallery -> ห้องนั่งเล่นครอบครัว / ห้องโซฟาเชอร์รี่ / ลาน BBQ บนหลังคาจากทิศตะวันออก (+10.05, pergola)
บันไดนอก H4 จากลาน BBQ ขึ้นลานคาเฟ่ +13.25 (แผงโซลาร์ 18 แผง 9.0 kWp)
ทางหนีไฟขึ้น 4: แกลเลอรี -> ลาน BBQ -> H3 -> H2 -> H1 -> คลอง -> ศาลา -> ลาน

X-UNIT Architecture Lab

WELL for Residential (เจตนา)

ที่ดิน 30.00 x 30.00 ม. = 225 ตร.ว.
ถนนสาธารณะทิศเหนือ (สมบัติ 8.00 ม.)


ตีความจาก Rivera Paradise (AtelierM):
 คอร์รถกลาง + บ้านโตเกเลียควู้ (ใน/นอก)
 + ปีกลดชั้นแบบเกลียว หลังคาสวนทุกชั้น
 + ผืนหญ้าริเวอร์ + เพดานโค้งอิฐ

±0.00 ถนน · F1 +0.45 · F2 +3.65
F3 +6.85 · F4 +10.05
ลาดฟ้า +13.25 · ราว +14.35
โค้งอิฐ สปริง +5.45 ยอด +6.65

หน่วยเป็นมิลลิเมตร เว้นแต่ระบุ
ระดับอ้างอิงบนหน้าทีดิน ± 0.00
ห้ามวัดขนาดจากแบบ ใช้ตัวเลขกำกับ
แบบระดับ Design Development
ต้องให้สถาปนิกและวิศวกรผู้ได้รับ
ใบอนุญาตตรวจสอบและลงนาม
ก่อนยื่นขออนุญาต

ผังพื้นที่ชั้น 4
(FFL +10.05)

วันที่ 6 ต.ค. 2569 ฉบับ v1 / DD

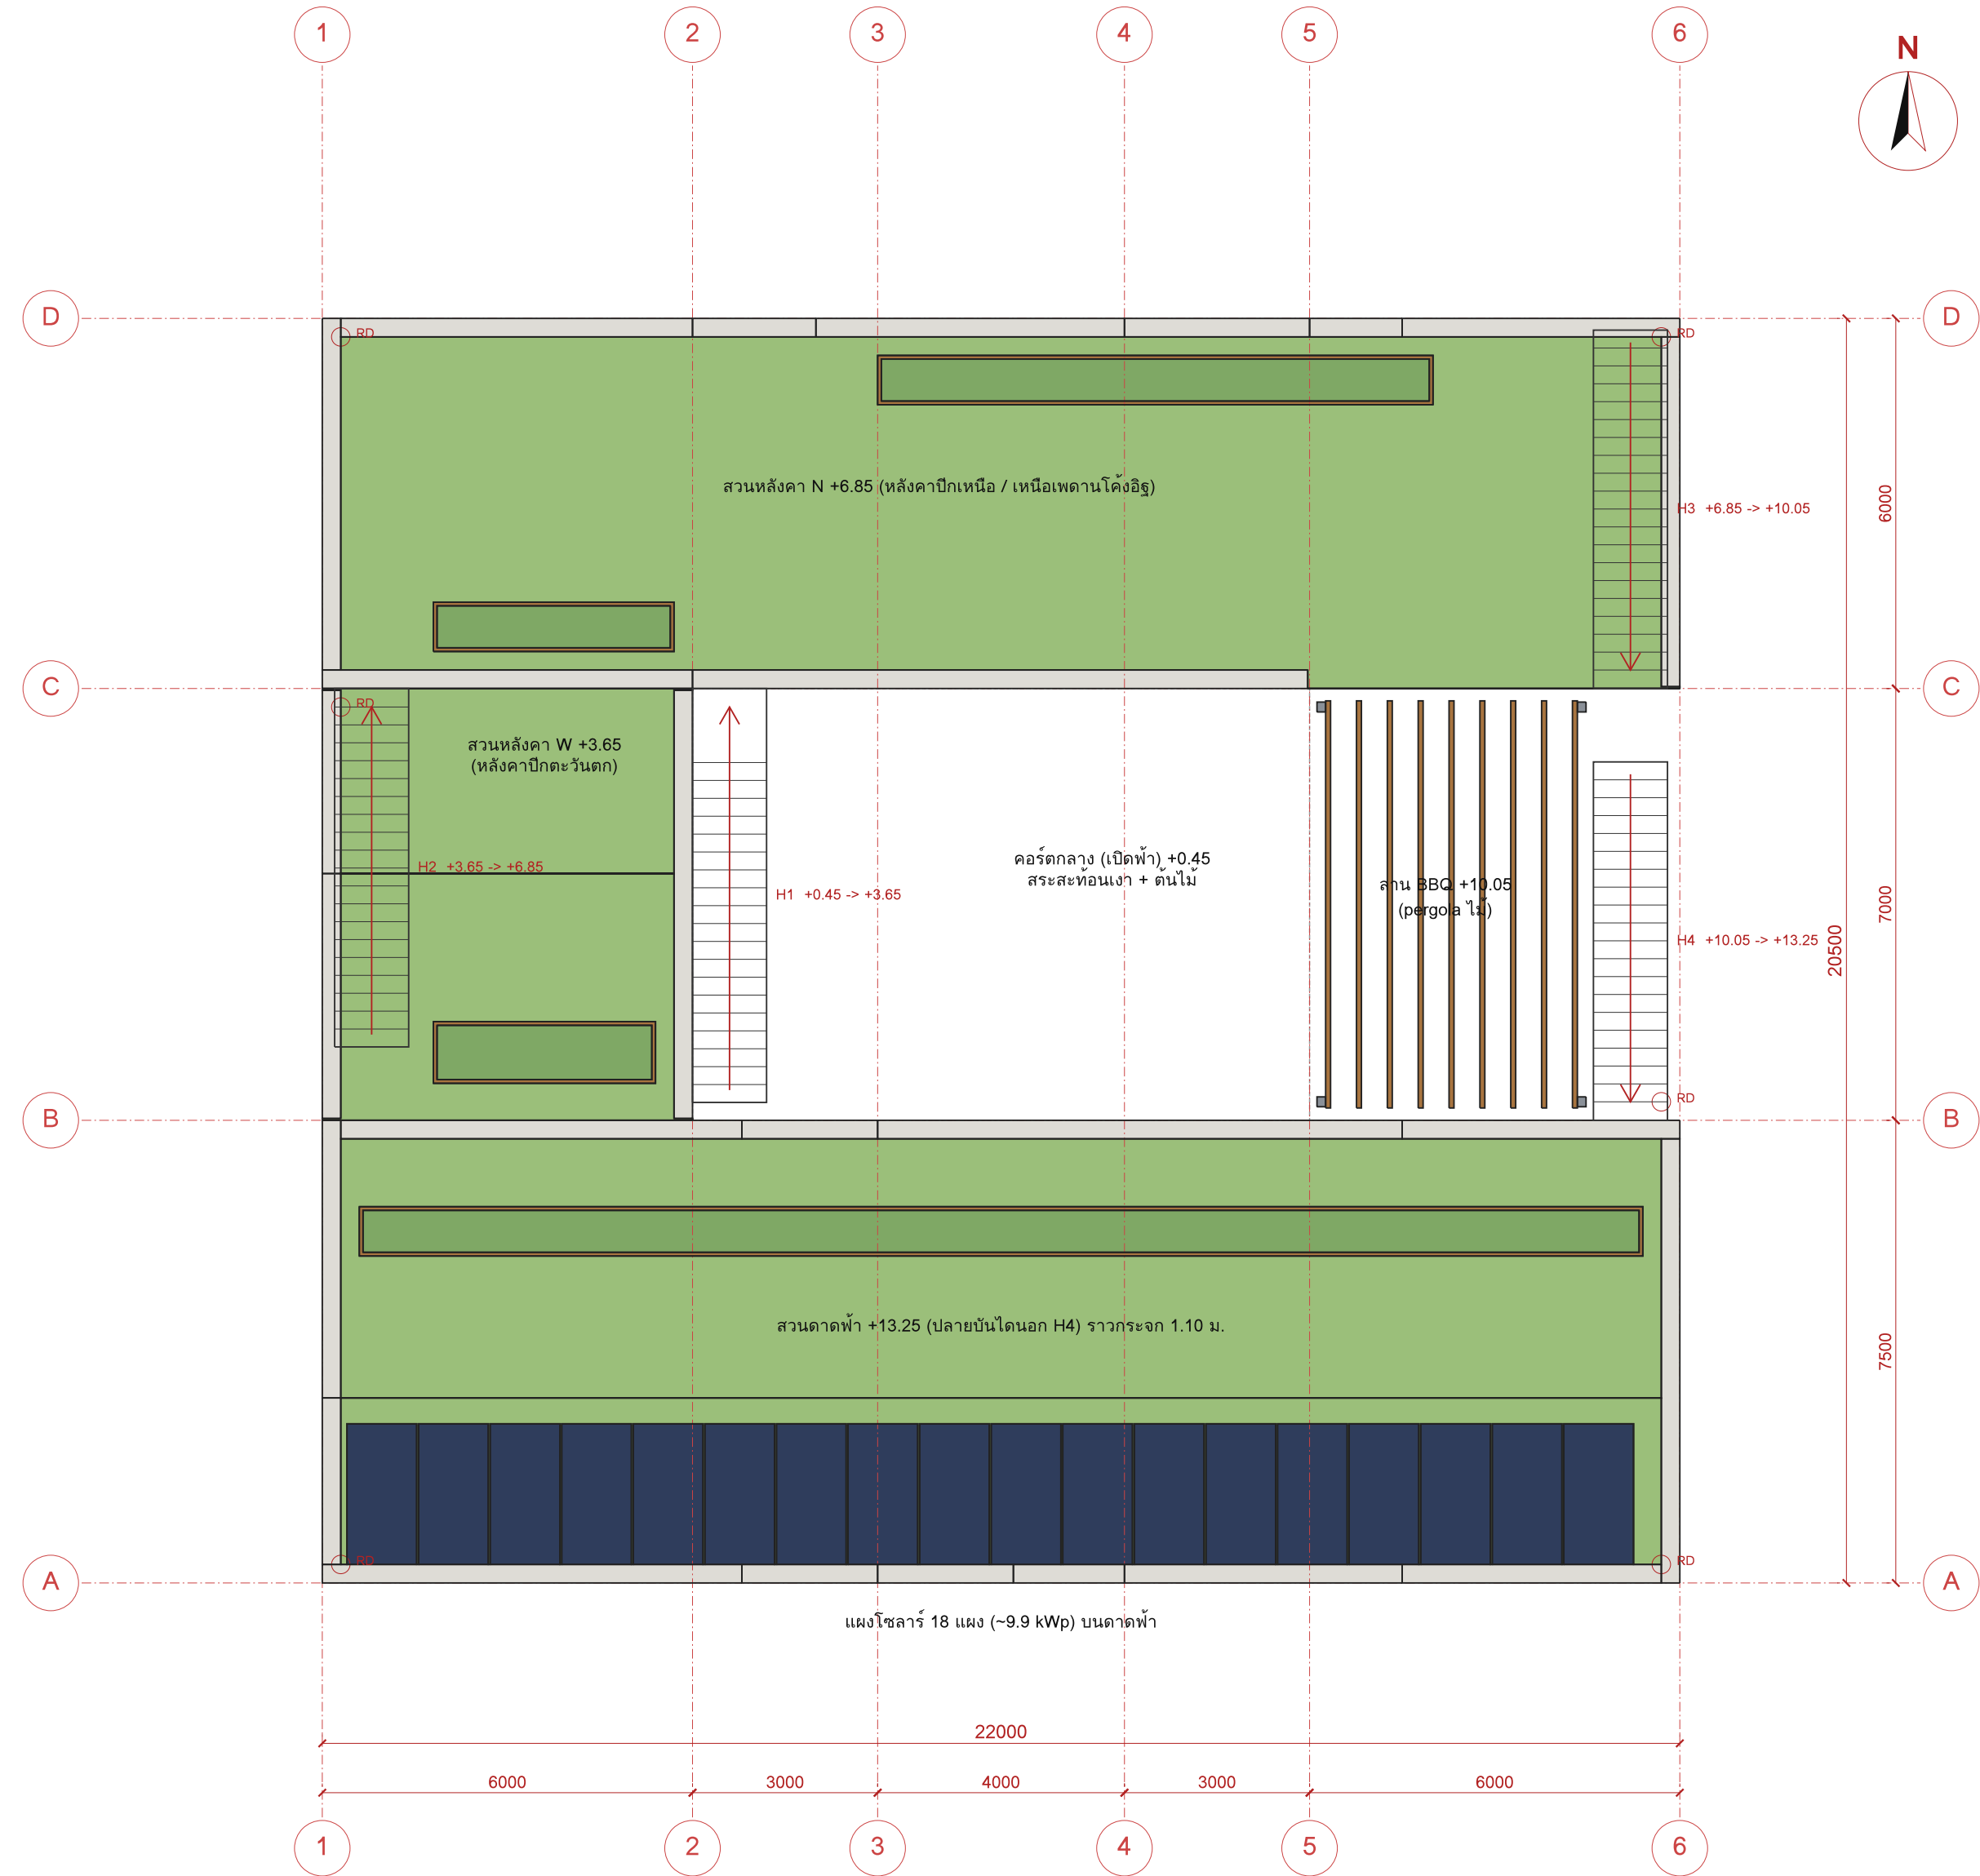

แปลนหลังคา ROOF PLAN 1:100

พื้นที่หลังคา

หลังคา	จ.ร.ม.
สวนหลังคา W +3.65 (ปีกตะวันตก)	42.00
สวนหลังคา N +6.85 (ปีกเหนือ)	132.00
ลาน BBQ E +10.05 (พื้นไม้ บนหลังคาชั้น 3)	42.00
สวนคาเฟ่ S +13.25 (รวมแผงโซลาร์)	165.00
รวมหลังคาส่วน	339.00
คอร์ตกลาง (เปิดฟ้า ไม่มีหลังคา)	70.00

น้ำฝน พลังงาน บันไดนอก

รายการ	ค่า
ระบายน้ำจากหลังคา (ประมาณ)	~1,500 มม./ปี
น้ำฝนจากหลังคาส่วน (C=0.4) + คอร์ต (C=0.9)	298 ลบ.ม./ปี
ถังเก็บน้ำฝนใต้ดิน 240 x 3.00 ม.	~12 ลบ.ม. (รองรับชักโครก)
แผงโซลาร์ 18 x 550 Wp	9.90 kWp ~ 12,900 kWh/ปี*
บันไดนอก H1-H4	กว้าง 1.20 ม. 20 ลูกตั้ง x 160 / 290 มม.

ชั้นหลังคาส่วน

- ติดดาวน์ดาวน์ไม้พื้น + สันลูก 150-450 มม. + แผ่นโกลกรอง + แผ่นระบายน้ำ 20 มม. + แผ่นกันราก + กันซึม 2 ชั้น + ค.ส.ล. ลาด 1:100
- ขอบส่วน: คอนกรีตสูง 0.45 + ราวกระจก laminated 1.10 ม. · กรอบไม้ปูลาดดินไม้ใหญ่
- ลาน BBQ: พื้นไม้แบบซาดิง + pergola ไม้ + เสา BBQ แก๊ส/ไฟฟ้า
- ทุกส่วนหลังคาใช้เป็นเส้นทางหนีไฟ — ทำแนวถังถังค้ำวางบนแนวบันไดนอก
- RD = ทุกระเบียงน้ำฝน ลงรางระบายอาคาร -> ถังน้ำฝน: คอร์ตมีรางระบายรอบ + บ่อพัก
- PV ~1,300 kWh/kWp/ปี ติดตั้งเอียง 10° บนคาเฟ่ — ต้องคำนวณเงาจากอาคารข้างเคียง

H3A DESIGN AND BUILD

X-UNIT Architecture Lab

โครงการ

WELL-RIVERA 30x30

Executive Luxury Villa
บ้านเดี่ยว 4 ชั้น ผ่านเกณฑ์
WELL for Residential (เจดนา)

ที่ดิน 30.00 x 30.00 ม. = 225 ตร.ว.
ถนนสาธารณะติดเหนือ (สมมติ 8.00 ม.)

แนวคิด

ตีความจาก Rivera Paradise (AtelierM):
คอร์ตกลาง + บันไดเกสยาวคู่ (ใน/นอก)
+ ปกคลุมชั้นแบบเกสยาว หลังคาส่วนทุกชั้น
+ ผังอินทรีย์ + เพดานโค้งอูฐ

ระดับ

±0.00 ถนน · F1 +0.45 · F2 +3.65
F3 +6.85 · F4 +10.05
คาเฟ่ +13.25 · ราว +14.35
โค้งอูฐ สปริง +5.45 ยอด +6.65

หมายเหตุ

- หน่วยงานเป็นผลิตภัณฑ์ เวนแต่ละรูป
- ระดับล่างถึงถนนหน้าที่ดิน ±0.00
- ทำแนววัดขนาดจากแบบ ใช้ตัวเลขกำกับ
- แบบระดับ Design Development
- ต้องให้สถาปนิกและวิศวกรผู้ได้รับใบอนุญาตตรวจสอบและลงนามก่อนยื่นขออนุญาต

ชื่อแผ่น

แปลนหลังคา
(สวนหลังคาแบบเกสยาว)

มาตรฐาน 1:100

วันที่ 6 ต.ค. 2569 ฉบับ v1 / DD

รูปด้านทิศเหนือ (ถนน — ปีกเหนือ 2 ชั้น / ปีกใต้ด้านหลัง) 1:100



วัสดุผิว (ระดับแนวคิด)

- ค่าเฉลี่ย E/W และค่าถ่านหิน: อธิบายข้อเท็จจริง (ของอากาศ + แนวทางด้านใน) + ส่วนแนวตั้ง
- หน่วย: ไม่นานแล้ว + กระดาษเปลี่ยน + ข้อเท็จจริง/ข้อเท็จจริง: คอนกรีตเปลี่ยนสีขาว
- ราคาต่อไมโครเมตรคือ 0.45 m. ทุกๆเศษ 1 ไม่นานแล้ว (ระดับแนวคิด)
- ชนิดโหนด: คอนกรีตหรือ + ราคาต่อ 1.00 m. + ราคาส่วนหนึ่ง: ราคา 1.10 m.
- กระเบื้อง Low-E laminated กรอบอลูมิเนียมสีฟ้า + ลาน BBQ: pergola 1

X-UNIT Architecture Lab

โครงการ

WELL-RIVERA 30x30

Executive Luxury Villa
บ้านเดี่ยว 4 ชั้น ผ่านเกณฑ์
WELL for Residential (เจตนา)

ที่ดิน 30.00 x 30.00 ม. = 225 ตร.ว.
ถนนสาธารณะทิศเหนือ (สมบัติ 8.00 ม.)

แนวคิด

ตีความจาก Rivera Paradise (AtelierM):
คอร์ตกลาง + บ้านโคกลีญาตุ้ (ใน/นอก)
+ ปีกลดชั้นแบบเกลียว หลังคาสวนทุกชั้น
+ ผนังอิฐโชว์ + เพดานโค้งอิฐ

ระดับ

±0.00 ถนน · F1 +0.45 · F2 +3.65
F3 +6.85 · F4 +10.05
ศาลฟ้า +13.25 · ราว +14.35
โค้งอิฐ สปริง +5.45 ยอด +6.65

หมายเหตุ

- หน่วยเป็นมิลลิเมตร เว้นแต่ระบุ
- ระดับอ้างอิงถนนหน้าที่ดิน ± 0.00
- ห้ามวัดขนาดจากแบบ ใช้ตัวเลขกำกับ
- แบบระดับ Design Development
ต้องให้สถาปนิกและวิศวกรผู้ได้รับ
ใบอนุญาตตรวจสอบและลงนาม
ก่อนยื่นขออนุญาต

ชื่อแผ่น

รูปด้านทิศใต้
+ รูปด้านทิศเหนือ

มาตราส่วน 1:100


วันที่ 6 ต.ค. 2569 ฉบับ v1 / DD

A-08

รูปด้านทิศตะวันออก (ชั้นเกลียว + บันไดนอก H3/H4) 1:100



รูปด้านทิศตะวันตก (ชั้นเกลียว + บันไดนอก H2) 1:100

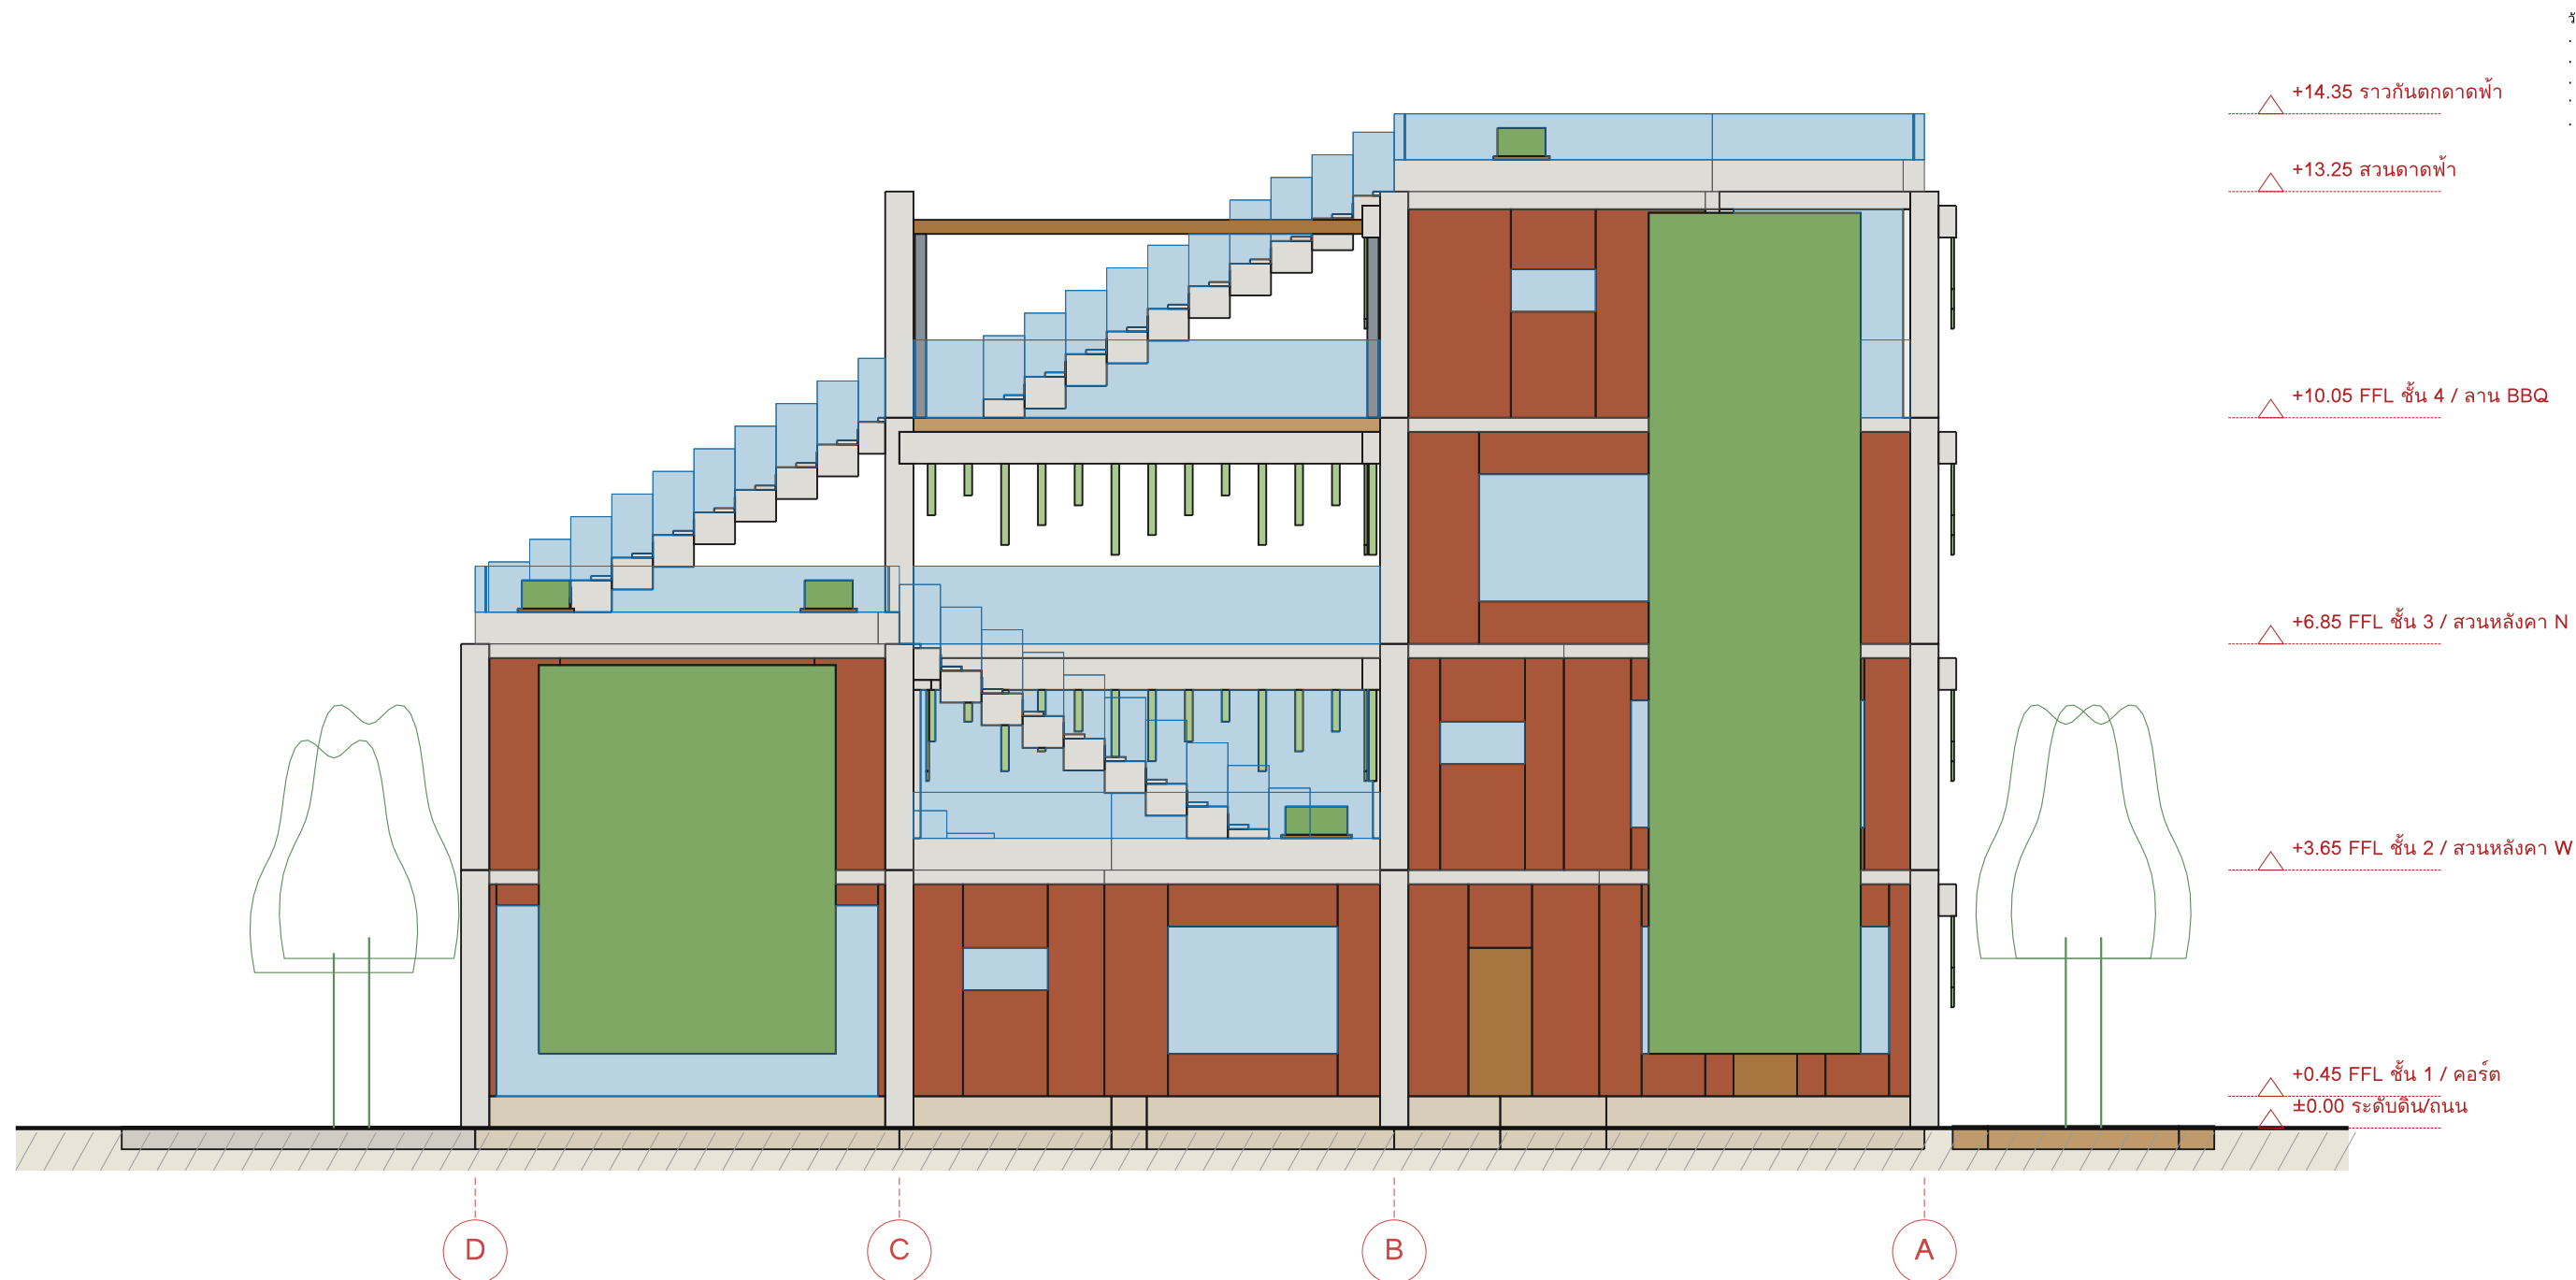

วัสดุผิว (ระดับบนแล้วคือ)

- ผนังทำด้วย EW และฉนวนกันชน อีพ็อกซีโพรพิลเนว (ช่องอากาศ 2 นิ้วจนด้านใน + ส่วนแนวตั้งด้านละ 3 นิ้ว)
- พื้นทำด้วย ไม้อัดทึบสี + กระจกบานเลื่อน + ขอบที่ทนไฟแล้วด้วย ดมกริลเปปเปอร์สีขาว
- รางบันไดไม้คอนกรีตยี่ห้อ 0.45 นิ้ว ทุกขอบพื้น + ไม้เหล็กรอบยี่ห้อ (ระบบน้ำหยด)
- พื้นใบนอก ดมกริลเปปเปอร์ + ราวกระจกใส 1.00 นิ้ว . ราวบานหลังด้าน : กระจก 1.10 นิ้ว . กระจก Low-E laminated กรอบอลูมิเนียมสีเทา . ราวบันได BQ: pergola 1 นิ้ว

0 5 μm

โครงการ

WELL-RIVERA 30x30

Executive Luxury Villa
บ้านเดี่ยว 4 ชั้น ผ่านเกณฑ์
WELL for Residential (เจตนา)

ที่ดิน 30.00 x 30.00 ม. = 225 ตร.ว.
ถนนสาธารณะทิศเหนือ (สมมติ 8.00 ม.)

แนวคิด

ตีความจาก Rivera Paradise (AtelierM):
คอร์ตกลาง + บ้านโคกเกียวกู้ (ใน/นอก)
+ ปีกลดชั้นแบบเกลียว หลังคาสวนทุกชั้น
+ ผนังอิฐโชว์ + เพดานโค้งอิฐ

ระดับ

±0.00 ถนน · F1 +0.45 · F2 +3.65
F3 +6.85 · F4 +10.05
ศาลฟ้า +13.25 · ราว +14.35
โค้งอิฐ สปริง +5.45 ยอด +6.65

หมายเหตุ

- หน่วยเป็นมิลลิเมตร เว้นแต่ระบุ
- ระบุอ้างอิงถนนหน้าที่ดิน ± 0.00
- ห้ามวัดขนาดจากแบบ ใช้ตัวเลขกำกับ
- แบบระดับ Design Development
ต้องให้สถาปนิกและวิศวกรผู้ได้รับ
ใบอนุญาตตรวจสอบและลงนาม
ก่อนยื่นขออนุญาต

ชื่อแผ่น

รูปด้านทิศตะวันออก
+ รูปด้านทิศตะวันตก

มาตราส่วน 1:100

วันที่ 6 ต.ค. 2569 ฉบับ v1 / DD

WELL-RIVERA 30x30 · Executive Luxury Villa · บ้านเดี่ยว 4 ชั้น รอบคอร์ทกลาง ปกคลุมแบบเกลียว + บนโดเกลียวคู่ (ใน/นอก) + หลังคาสวนหุบหิน (แนวคดจาก Rivera Paradise / AtelierM)

ที่ดิน 30.00 x 30.00 ม. (225 ตร.ว.) · ถนน (สมมติ 8.00 ม.) ที่ดินเดิม · โปรแกรม ARCHISPACE 6 ต.ค. 2569

ตารางของเปิด (123 รายการ) — หน่วย มม. วัดจาก FFL

รหัส	ชั้น	ชนิด	กว้าง	ขอบล่าง	ขอบบน	ค่าหนึ่ง
D01	F1	ประตูลิฟต์	900	0	2100	ลิฟต์บ้าน แกลเลอรีบันได
D02	F1	ประตูบานเปิดเดี่ยว	1800	0	2700	โถงต้อนรับได้ใจ ภายนอก-N
D03	F1	ประตูบานเปิดเดี่ยว	900	0	2400	โถงต้อนรับได้ใจ โรงจอดรถ 4 คัน
SD01	F1	ประตูบานเลื่อนกระจก	1600	0	2700	โถงทางเดินบันได ศาลารับแขก (ท)
SD02	F1	ประตูบานเลื่อนกระจก	1200	0	2700	ศาลารับแขก (ท) แกลเลอรีบันได
SD03	F1	ประตูบานเลื่อนเดี่ยว	900	0	2100	ห้องนอนแขกคู่ ห้องน้ำห้องแขก
D04	F1	ประตูบานเปิดเดี่ยว	900	0	2100	ห้องนอนแขกคู่ ตู้เสื้อผ้า
D05	F1	ประตูบานเปิดเดี่ยว	900	0	2100	ครัวไทย (ครัวหัว) ภายนอก-W
D06	F1	ประตูบานเปิดเดี่ยว	900	0	2100	ห้องซักผ้า ภายนอก-W
D07	F1	ประตูบานเปิดเดี่ยว	900	0	2100	ครัวไทย (ครัวหัว) ห้องซักผ้า
SD04	F1	ประตูบานเลื่อนกระจก	1800	0	2700	แกลเลอรีบันได โถงพักผ่อน / T
SD05	F1	ประตูบานเลื่อนกระจก	3600	0	2700	ห้องพักผ่อน / โถง ภายนอก-S
D08	F1	ประตูบานเปิดเดี่ยว	900	0	2100	ห้องพักผ่อน / โถง ห้องเครื่องสระ
D09	F1	ประตูบานเปิดเดี่ยว	800	0	2100	ห้องเก็บของ / ู ห้องพักผ่อน / T
D10	F1	ประตูบานเปิดเดี่ยว	900	0	2100	ห้องเครื่องสระ / ภายนอก-E
D11	F1	ประตูบานเปิดเดี่ยว	900	0	2400	โรงจอดรถ 4 คัน โถงบริการ (คว)
D12	F1	ประตูบานเปิดคู่	1200	0	2100	ห้อง MEP / ไฟฟ้า ภายนอก-E
W01	F1	หน้าต่าง	2400	600	2400	ห้องนอนแขกคู่ ภายนอก-W
D13	F1	ประตูบานเปิดเดี่ยว	900	0	2400	ห้องนอนแขกคู่ โถงทางเดินบันได
D14	F1	ประตูบานเปิดเดี่ยว	900	0	2400	ครัวไทย (ครัวหัว) ศาลารับแขก (ท)
D15	F1	ประตูบานเปิดเดี่ยว	800	0	2100	โถงบริการ (คว) ห้องนั่งเล่นบ้าน
D16	F1	ประตูบานเปิดเดี่ยว	900	0	2400	โถงบริการ (คว) ห้องนั่งเล่น 2
D17	F1	ประตูบานเปิดเดี่ยว	900	0	2400	โถงบริการ (คว) ห้องนั่งเล่น 1
D18	F1	ประตูบานเปิดเดี่ยว	800	0	2100	โรงจอดรถ 4 คัน ห้อง MEP / ไฟ
W02	F1	ผนังกระจก	1300	0	2700	ครัวไทย (ครัวหัว) ศาลารับแขก (ท)
W03	F1	ผนังกระจก	1300	0	2700	ครัวไทย (ครัวหัว) ศาลารับแขก (ท)
W04	F1	หน้าต่าง	1200	1500	2100	ห้องซักผ้า ศาลารับแขก (ท)
W05	F1	ผนังกระจก	5400	0	3000	ศาลารับแขก (ท) อินโฟล็กซ์ (เก)
W06	F1	ผนังกระจก	1600	0	2700	โถงต้อนรับได้ใจ ภายนอก-N
W07	F1	ผนังกระจก	1600	0	2700	โถงต้อนรับได้ใจ ภายนอก-N
W08	F1	ผนังกระจก	5400	0	2700	โถงต้อนรับได้ใจ ภายนอก-W
W09	F1	หน้าต่าง	1200	1500	2100	ห้อง MEP / ไฟฟ้า ภายนอก-N
W10	F1	หน้าต่าง	1200	1500	2100	ห้อง MEP / ไฟฟ้า ภายนอก-E
W11	F1	หน้าต่าง	1200	1500	2100	ห้อง MEP / ไฟฟ้า ภายนอก-E
W12	F1	หน้าต่าง	1200	1500	2100	ห้องน้ำห้องแขก ภายนอก-W
W13	F1	ผนังกระจก	6400	0	2700	โถงทางเดินบันได ภายนอก-E
W14	F1	หน้าต่าง	2400	600	2400	ครัวไทย (ครัวหัว) ภายนอก-S
W15	F1	หน้าต่าง	900	600	2400	ครัวไทย (ครัวหัว) ภายนอก-W
W16	F1	หน้าต่าง	900	600	2400	ครัวไทย (ครัวหัว) ภายนอก-W
W17	F1	ผนังกระจก	1600	0	3000	บันไดหลัก (เกลียว) ภายนอก-S
W18	F1	หน้าต่าง	1200	1500	2100	ห้องเก็บของ / ู ภายนอก-S
W19	F1	ผนังกระจก	6400	0	2700	แกลเลอรีบันได ภายนอก-N
W20	F1	หน้าต่าง	1200	1500	2100	ห้องเครื่องสระ / ภายนอก-S
W21	F1	หน้าต่าง	1200	1500	2100	ห้องเครื่องสระ / ภายนอก-E
W22	F1	หน้าต่าง	1200	1500	2100	ห้องเครื่องสระ / ภายนอก-E
W23	F1	ผนังกระจก	6400	0	2700	โถงบริการ (คว) ภายนอก-W
W24	F1	หน้าต่าง	600	1500	2100	ห้องนั่งเล่นบ้าน ภายนอก-E
W25	F1	หน้าต่าง	2100	600	2400	ห้องนั่งเล่น 2 ภายนอก-E
W26	F1	หน้าต่าง	2100	600	2400	ห้องนั่งเล่น 1 ภายนอก-E
D19	F2	ประตูลิฟต์	900	0	2100	ลิฟต์บ้าน แกลเลอรีบันได
SD06	F2	ประตูบานเลื่อนกระจก	1500	0	2700	ห้องรับแขกทางเข้า ภายนอก-N
D20	F2	ประตูบานเปิดเดี่ยว	900	0	2100	ครัวไทย + โถง Walk-in Pantry
D21	F2	ประตูบานเปิดเดี่ยว	800	0	2100	ห้องน้ำแขก (Pow) ห้องนั่งเล่น
SD07	F2	ประตูบานเลื่อนกระจก	4200	0	2700	ห้องนั่งเล่น ภายนอก-S
SD08	F2	ประตูบานเลื่อนกระจก	3600	0	2700	ห้องรับแขกทางเข้า ภายนอก-S
D22	F2	ประตูบานเปิดเดี่ยว	800	0	2100	ห้องน้ำ Junior S ห้องนอน Junior
D23	F2	ประตูบานเปิดเดี่ยว	800	0	2100	ตู้เสื้อผ้า Juni ห้องนอน Junior
D24	F2	ประตูบานเปิดเดี่ยว	800	0	2100	ตู้เสื้อผ้า Juni ห้องนอน Junior
D25	F2	ประตูบานเปิดเดี่ยว	800	0	2100	ตู้เสื้อผ้า Juni ห้องน้ำ Junior
W27	F2	หน้าต่าง	3600	300	1700	ห้องโถงโถงต้อนรับ ภายนอก-W
W28	F2	หน้าต่าง	3000	300	1700	ห้องโถงโถงต้อนรับ ภายนอก-N
D26	F2	ประตูบานเปิดเดี่ยว	900	0	2400	แกลเลอรีบันได ห้องทำงาน & ห้

รหัส	ชั้น	ชนิด	กว้าง	ขอบล่าง	ขอบบน	ค่าหนึ่ง
D27	F2	ประตูบานเปิดเดี่ยว	900	0	2400	ทางเดินบันได ห้องนอน Junior
D28	F2	ประตูบานเปิดเดี่ยว	800	0	2100	ทางเดินบันได ห้องน้ำ / ซัก
D29	F2	ประตูบานเปิดเดี่ยว	800	0	2100	ทางเดินบันได ห้องเก็บของ
D30	F2	ประตูบานเปิดเดี่ยว	900	0	2400	ทางเดินบันได ห้องนอน Junior
W29	F2	หน้าต่าง	1200	1500	2100	ห้องโถงโถงต้อนรับ ตู้เสื้อผ้า Juni
W30	F2	หน้าต่าง	1200	1500	2100	ห้องโถงโถงต้อนรับ ห้องน้ำ Junior
W31	F2	หน้าต่าง	2400	600	2400	ครัวไทย + โถง ภายนอก-S
W32	F2	หน้าต่าง	3300	600	2400	ครัวไทย + โถง ภายนอก-W
W33	F2	หน้าต่าง	1200	1500	2100	Walk-in Pantry & ภายนอก-N
W34	F2	หน้าต่าง	1200	1500	2100	Walk-in Pantry & ภายนอก-W
W35	F2	หน้าต่าง	2100	600	2400	ห้องรับแขกทางเข้า ภายนอก-N
W36	F2	ผนังกระจก	1600	0	3000	บันไดหลัก (เกลียว) ภายนอก-S
W37	F2	หน้าต่าง	1200	1500	2100	ห้องน้ำแขก (Pow) ภายนอก-S
W38	F2	ผนังกระจก	6400	0	2700	แกลเลอรีบันได ภายนอก-N
W39	F2	หน้าต่าง	1500	600	2400	ห้องนั่งเล่น (S) ภายนอก-S
W40	F2	หน้าต่าง	3900	600	2400	ห้องนั่งเล่น (S) ภายนอก-E
W41	F2	หน้าต่าง	4200	600	2400	ห้องทำงาน & ห้อง ภายนอก-E
W42	F2	ผนังกระจก	6400	0	2700	ทางเดินบันได ภายนอก-W
W43	F2	หน้าต่าง	1200	1500	2100	ตู้เสื้อผ้า Juni ภายนอก-E
W44	F2	ผนังกระจก	9400	0	2700	ทางเดินบันได ภายนอก-S
W45	F2	หน้าต่าง	600	1500	2100	ห้องน้ำ Junior S ภายนอก-N
W46	F2	หน้าต่าง	3300	600	2400	ห้องนอน Junior S ภายนอก-N
W47	F2	หน้าต่าง	1200	1500	2100	ห้องเก็บของ ภายนอก-N
W48	F2	หน้าต่าง	2700	600	2400	ห้องนอน Junior S ภายนอก-N
W49	F2	หน้าต่าง	3900	600	2400	ห้องนอน Junior S ภายนอก-E
D31	F3	ประตูลิฟต์	900	0	2100	ลิฟต์บ้าน แกลเลอรีบันได
D32	F3	ประตูบานเปิดเดี่ยว	1000	0	2400	ห้องนอน Master S โถงห้อง Master
D33	F3	ประตูบานเปิดเดี่ยว	1000	0	2400	โถงห้อง Master แกลเลอรีบันได
D34	F3	ประตูบานเปิดเดี่ยว	900	0	2400	แกลเลอรีบันได Walk-in Dressi
SD09	F3	ประตูบานเลื่อนเดี่ยว	900	0	2400	Walk-in Dressing ห้องน้ำ Spa +
D35	F3	ประตูบานเปิดเดี่ยว	800	0	2100	ห้องเก็บของ Walk-in Dressi
SD10	F3	ประตูบานเลื่อนกระจก	1200	0	2700	แกลเลอรีบันได ลอยเตียง-วัง
SD11	F3	ประตูบานเลื่อนกระจก	4200	0	2700	ห้องนอน Master S ภายนอก-S
W50	F3	หน้าต่าง	1200	1500	2100	ห้องน้ำ Spa + Ja ลอยเตียง-วัง
W51	F3	หน้าต่าง	4500	600	2400	ห้องนอน Master S ภายนอก-N
W52	F3	หน้าต่าง	5100	600	2400	ห้องนอน Master S ภายนอก-W
W53	F3	ผนังกระจก	1600	0	3000	บันไดด้านซ้าย Mas ภายนอก-S
W54	F3	ผนังกระจก	1600	0	2700	โถงห้อง Master ภายนอก-N
W55	F3	ผนังกระจก	1600	0	3000	บันไดหลัก (เกลียว) ภายนอก-S
W56	F3	หน้าต่าง	1200	1500	2100	ห้องเก็บของ ภายนอก-S
W57	F3	ผนังกระจก	6400	0	2700	แกลเลอรีบันได ภายนอก-N
W58	F3	หน้าต่าง	1200	1500	2100	ห้องน้ำ Spa + Ja ภายนอก-S
W59	F3	หน้าต่าง	1200	1500	2100	ห้องน้ำ Spa + Ja ภายนอก-E
D36	F4	ประตูลิฟต์	900	0	2100	ลิฟต์บ้าน Upper Gallery
SD12	F4	ประตูบานเลื่อนกระจก	2400	0	2700	ระเบียง Master (Master Walk-in
D37	F4	ประตูบานเปิดเดี่ยว	800	0	2100	ห้องน้ำชั้น 4 ห้องนั่งเล่น
SD13	F4	ประตูบานเลื่อนกระจก	1200	0	2700	Upper Gallery (T) สวน BBQ บนหลัง
SD14	F4	ประตูบานเลื่อนกระจก	3000	0	2700	ห้องนั่งเล่นรอบ ภายนอก-S
D38	F4	ประตูบานเปิดเดี่ยว	900	0	2400	Upper Gallery (T) ห้องโถงระเบียง
W60	F4	หน้าต่าง	1200	1500	2100	ระเบียง Master (Master Walk-in
W61	F4	หน้าต่าง	1200	1500	2100	ระเบียง Master (Master Walk-in
W62	F4	ผนังกระจก	2400	0	3000	ระเบียง Master (บันไดด้านซ้าย M
W63	F4	หน้าต่าง	1200	1500	2100	Master Walk-in C ภายนอก-N
W64	F4	หน้าต่าง	1200	1500	2100	Master Walk-in C ภายนอก-W
W65	F4	ผนังกระจก	1600	0	3000	บันไดด้านซ้าย Mas ภายนอก-S
W66	F4	หน้าต่าง	1200	1500	2100	Master Walk-in C ภายนอก-N
W67	F4	ผนังกระจก	1600	0	3000	บันไดหลัก (เกลียว) ภายนอก-S
W68	F4	หน้าต่าง	1200	1500	2100	ห้องน้ำชั้น 4 ภายนอก-S
W69	F4	ผนังกระจก	6400	0	2700	Upper Gallery (T) ภายนอก-N
W70	F4	หน้าต่าง	2700	600	2400	ห้องโถงระเบียง ภายนอก-S
W71	F4	หน้าต่าง	5100	600	2400	ห้องโถงระเบียง ภายนอก-E

๐.39 ข้อ 6 ของเปิด >= 10% ของพื้นที่ห้อง

ห้อง	ข้อเปิดพื้นที่ห้อง	ผล
F1 ห้อง MEP / ไฟฟ้า / เครื่องปรับอากาศ	22.3% (4.66/21.00)	ผ่าน
F1 ห้องนอนแขก/ผู้สูงอายุ	27.0% (4.32/16.00)	ผ่าน
F1 ห้องน้ำห้องแขก	12.0% (0.72/6.00)	ผ่าน
F1 ตู้เสื้อผ้าห้องแขก	0.0% (0.00/6.00) -> ปิดประตูบานอากาศ (ข้อ 6 วรร	ผ่าน
F1 ครัวไทย (ครัวหัว)	96.2% (17.31/18.00)	ผ่าน
F1 ห้องซักผ้า	10.7% (1.29/12.00)	ผ่าน
F1 ห้องเก็บของ / อุปกรณ์สระ	9.5% (0.72/7.56) -> ปิดประตูบานอากาศ (ข้อ 6 วรร	ผ่าน
F1 ห้องพักผ่อน / โถง รับแขก	27.0% (3.78/15.00)	ผ่าน
F1 ห้องเครื่องสระ / เก็บของ	15.1% (2.73/18.00)	ผ่าน
F1 ห้องนั่งเล่นบ้าน	5.3% (0.36/6.75) -> ปิดประตูบานอากาศ (ข้อ 6 วรร	ผ่าน
F1 ห้องนั่งเล่น 2	24.0% (3.78/15.75)	ผ่าน
F1 ห้องนั่งเล่น 1	24.0% (3.78/15.75)	ผ่าน
F2 ครัวไทย + โถงนั่งเล่น	51.3% (10.26/20.00)	ผ่าน
F2 Walk-in Pantry & ห้องอื่น	14.4% (1.44/10.00)	ผ่าน
F2 ห้องรับแขกทางอาหาร	46.8% (17.55/37.50)	ผ่าน
F2 ห้องน้ำแขก (Powder)	9.5% (0.72/7.56) -> ปิดประตูบานอากาศ (ข้อ 6 วรร	ผ่าน
F2 ห้องนั่งเล่น	39.0% (21.06/54.00)	ผ่าน
F2 ห้องทำงาน & ห้องสุขา	25.8% (7.56/29.25)	ผ่าน
F2 ห้องน้ำ Junior Suite 3	0.0% (0.00/4.40) -> ปิดประตูบานอากาศ (ข้อ 6 วรร	ผ่าน
F2 ตู้เสื้อผ้า Junior Suite 3	15.7% (0.72/4.60)	ผ่าน
F2 ตู้เสื้อผ้า Junior Suite 2	0.0% (0.00/4.40) -> ปิดประตูบานอากาศ (ข้อ 6 วรร	ผ่าน
F2 ห้องน้ำ Junior Suite 2	7.8% (0.36/4.60) -> ปิดประตูบานอากาศ (ข้อ 6 วรร	ผ่าน
F2 ห้องนอน Junior Suite 2	26.4% (5.94/22.50)	ผ่าน
F2 ห้องน้ำ / ซัก	0.0% (0.00/13.50) -> ปิดประตูบานอากาศ (ข้อ 6 วรร	ผ่าน
F2 ห้องเก็บของชั้น 2	10.7% (0.72/6.75)	ผ่าน
F2 ห้องนอน Junior Suite 3	44.0% (11.88/27.00)	ผ่าน
F3 ห้องนอน Master Suite	56.1% (28.62/51.00)	ผ่าน
F3 ห้องเก็บของชั้น 3	9.5% (0.72/7.56) -> ปิดประตูบานอากาศ (ข้อ 6 วรร	ผ่าน
F3 Walk-in Dressing (His & Hers)	0.0% (0.00/27.00) -> ปิดประตูบานอากาศ (ข้อ 6 วรร	ผ่าน
F3 ห้องน้ำ Spa + Jacuzzi	6.4% (2.16/33.75) -> ปิดประตูบานอากาศ (ข้อ 6 วรร	ผ่าน
F4 Master Walk-in Closet ชั้น 4	29.7% (10.08/33.90)	ผ่าน
F4 ห้องน้ำชั้น 4	9.5% (0.72/7.56) -> ปิดประตูบานอากาศ (ข้อ 6 วรร	ผ่าน
F4 ห้องนั่งเล่นรอบครัว	30.0% (8.10/27.00)	ผ่าน
F4 ห้องโถงระเบียง	41.6% (14.04/33.75)	ผ่าน

ระบายอากาศ >= 2 แนวหนึ่ง (เกณฑ์ภายใน สบสนุน R-T06) / ลึก <= 4.20 ม.

ห้อง/ใช้งานประจำ	ข้อเปิด	ลึกจากผนังนอก	ผล
F1 ห้องนอนแขก/ผู้สูงอายุ	1 แนวหนึ่ง -> ยากัน ทร	3.75 ม.	ผ่าน
F1 ครัวไทย (ครัวหัว)	3 แนวหนึ่ง	1.95 ม.	ผ่าน
F1 ห้องพักผ่อน / โถง รับแขก	1 แนวหนึ่ง -> ยากัน ทร	5.85 ม. -> ยากัน บานเลื่อน	ผ่าน
F1 ห้องนั่งเล่น 2	1 แนวหนึ่ง -> ยากัน ทร	4.35 ม. -> ยากัน ลึก 4.35 ม.	ผ่าน
F1 ห้องนั่งเล่น 1	1 แนวหนึ่ง -> ยากัน ทร	4.35 ม. -> ยากัน ลึก 4.35 ม.	ผ่าน
F2 ครัวไทย + โถงนั่งเล่น	3 แนวหนึ่ง	3.75 ม.	ผ่าน
F2 ห้องรับแขกทางอาหาร	3 แนวหนึ่ง	3.75 ม.	ผ่าน
F2 ห้องนั่งเล่น	2 แนวหนึ่ง	5.85 ม. -> ยากัน บานเลื่อน	ผ่าน
F2 ห้องนั่งเล่น (ด้านหลังห้อง)	2 แนวหนึ่ง	2.35 ม.	ผ่าน
F2 ห้องทำงาน & ห้องสุขา	1 แนวหนึ่ง -> ยากัน ทร	4.35 ม. -> ยากัน ลึก 4.35 ม.	ผ่าน
F2 ห้องนอน Junior Suite 2	1 แนวหนึ่ง -> ยากัน ทร	4.35 ม. -> ยากัน ลึก 4.35 ม.	ผ่าน
F2 ห้องนอน Junior Suite 3	2 แนวหนึ่ง	4.35 ม. -> ยากัน มุมตะวันตก	ผ่าน
F3 ห้องนอน Master Suite	3 แนวหนึ่ง	3.75 ม.	ผ่าน
F4 ห้องนั่งเล่นรอบครัว	1 แนวหนึ่ง -> ยากัน ทร	5.85 ม. -> ยากัน บานเลื่อน	ผ่าน
F4 ห้องโถงระเบียง	2 แนวหนึ่ง	3.75 ม.	ผ่าน

ตารางขนาดเปิดของเปิด (ลอยฟ้า/บนหลัง) 21 รายการ: ผ่าน 21

เทียบโปรแกรม ARCHISPACE (ตร.ม.)


รายการโปรแกรม	ชั้น	โปรแกรม	ชั้นบน	แบบ	ค่า
Grand Double-Height Foyer	F1	24.00	F1	36.00	+12.00
Formal Living Room	F2	50.00	F2	54.00	+4.00
Dining Room (10-12 Seats)	F2	40.00	F2	37.50	-2.50
Powder Room	F2	6.00	F2	7.56	+1.56
Home Theater / AV Lounge	F4	36.00	F4	33.75	-2.25
Wine Cellar / Cigar Room	F2	14.00	F2	13.50	-0.50
Master Suite Bedroom	F3	48.00	F3	51.00	+3.00
Master Walk-in (His & Hers)	F3	32.00	F3	27.00	-5.00
Spa Master Bath + Jacuzzi	F3	28.00	F3	33.75	+5.75
Junior Suite 2 (bath+closet)	F2	34.00	F2	31.50	-2.50
Junior Suite 3 (bath+closet)	F2	34.00	F2	36.00	+2.00
Guest Suite (GF / elderly)	F1	30.00	F1	28.00	-2.00
Family Lounge & Upper Gallery	F4	36.00	F4	39.75	+3.75
Executive Home Office & Library	F2	26.00	F2	29.25	+3.25
Master Walk-in Closet (UL)	F4	36.00	F4	33.90	-2.10
Show Kitchen & Island Bar	F2	28.00	F2	20.00	-8.00
Heavy Thai Kitchen	F1	20.00	F1	18.00	-2.00
Walk-in Pantry & Cold Storage	F3	12.00	F2	10.00	-2.00
Laundry & Utility Room	F1	16.00	F1	12.00	-4.00
Maid Bedroom 1 & 2	F1	22.00	F1	31.50	+9.50
Maid Bathroom	F1	6.00	F1	6.75	+0.75
MEP / Electrical / Generator	F1	14.00	F1	21.00	+7.00
Covered Garage 3-4 cars	F1	85.00	F1	75.00	-10.00
Covered Veranda & BBQ	F4	45.00	F4	42.00	-3.00
Upper Master Terrace	F4	28.00	F4	20.40	-7.60
Poolside Pavilion	F1	35.00	F1	37.50	+2.50
รวม NUA		785.00		786.61	+1.61

กลยุทธ์ WELL for Residential (รหัสตาม Guidebook ก.พ. 2026)


Feature (WELL for Residential)	การตอบสนองในแบบ	สถานะ	หลักฐานที่ต้องมี
R-A01 ระบบระบายอากาศ	พัดลมดูดเฉพาะจุดครัว/ห้องน้ำห้องไม่มีหน้าต่าง 12 ห้อง + ERV ห้องนอน	ระบุในแบบงานระบบ	ต้องวัด
R-A05 ฉลกรรมาใหม่	ครัวโซว์ชั้น 2 เต้าไฟฟ้าเหนียวน้ำ; ครัวไทยชั้น 1 แยก มีชุด เปิดสู่ลานบริการ	ในแบบ	เอกสาร
R-A09 จุดชาร์จ EV	1 จุดในโรงจอดรถ (ห้องเสื้อ 4 ช่อง)	ในแบบ	ภาพถ่าย
R-W03 น้ำที่ไม่ใช่ น้ำดื่ม	ถังน้ำฝนใต้ดิน ~12 ลบ.ม. รดสวนหลังคา/ซักโครก + ระบบน้ำหยดวางต้นไม้	ในแบบ	แบบสุขาภิบาล
R-L01 แสงธรรมชาติ	41.2% (166.1/403.5 ตร.ม.) -> ระดับ 3	คำนวณแล้ว	ต้องตรวจแสงจ้า
R-L02 ควบคุมแสง	วงจแยกทุกห้อง + ม่านพับห้องนอน/เฮียเตอร์ + ม่านโปร้งด้านคอร์ต	ระบุ	แบบไฟฟ้า
R-T06 หน้าต่างเปิดได้	15/15 ห้อง	คำนวณแล้ว	นั่งลาด/ตัวล็อก
R-T07 ความร้อนภายนอก	หลังคาส่วน 339 ตร.ม. (100% ของหลังคา) + ส่วนแนวตั้ง + รางต้นไม้ + คอร์ตต้นไม้	ในแบบ	ภาพถ่าย
R-V04 พื้นที่กิจกรรมกลางแจ้ง	สวนหลังคา 4 ระดับ + คอร์ต + สระ 14.00 x 2.70 ม. + ลาน BBQ	ในแบบ	-
R-V07 ออกแบบบันได	บันไดหลักอยู่หน้าลิฟต์ทุกชั้น เปิดสู่เกลเลอร์ริมคอร์ต + บันไดนอกเกลียวไค่สวน	ในแบบ	ภาพถ่าย
R-M01 ธรรมชาติและสถานที่	คอร์ตต้นไม้ + หลังคาส่วนทุกชั้น + วัสดุ/ไม้ น้ำ ทุกห้องเห็นต้นไม้	ในแบบ	-
R-M04 พื้นที่จัดเก็บ	Walk-in 2 ชั้น (Master) + ตู้ทุกห้องนอน + Pantry + ห้องเก็บของทุกชั้น	ในแบบ	-
R-N01 การปรุงอาหาร	ครัว 2 ส่วน (โซว์/ไทย) + Pantry ห้องเย็นติดครัวโซว์ + กระบะผักสวนหลังคา	ในแบบ	-
R-S01 แนวกันเสียง	คอร์ตปิดล้อมสะท้อนเสียง -> ผ้าดูดซับเสียงเกลเลอร์ + กระจก 2 ชั้นห้องนอน	ต้องระบุ STC	ทดสอบ
R-C01 ออกแบบเพื่อทุกคน	ลิฟต์บ้านทุกชั้น + ห้องแขกชั้น 1; ทางลาด 1:12 ยังต้องเพิ่ม	บางส่วน	ดู A-01 ข้อ 11
R-C06 กายพิบัติ	ยกพื้น +0.45 + ทางหนีไฟเกลียวนอก + เครื่องปั่นไฟ	ในแบบ	ยืนยันข้อ 27
R-X02 วัสดุ	อิฐมอญ คอนกรีต ไม้รับรอง FSC สี VOC ต่ำ	สเปก	ใบสั่งซื้อ

สถานะ = เจตนาการออกแบบ ยังไม่ใช่คะแนนรับรอง WELL Residence ต้องลงทะเบียน JWBI ส่งเอกสาร และตรวจวัดจริงหลังก่อสร้าง
ห้องที่ใช้พัฒนาะบาย: ตู้เสื้อผ้าห้องแขก, ห้องเก็บของ / ตู้ปาร์ณี่สระ, ห้องน้ำแม่บ้าน, ห้องน้ำเชก (Powder), ห้องน้ำ Junior Suite 3, ตู้เสื้อผ้า Junior Suite 2, ห้องน้ำ Junior Suite 2, ห้องโน้ / ซัการ, ห้องเก็บของชั้น 3, Walk-in Dressing (His & Hers), ห้องน้ำ Spa + Jacuzzi, ห้องน้ำชั้น 4

จากสวนหลังคาปีกตะวันตก (+3.65) — มองคอร์ต ลาน BBQ และชั้นสวนที่สูงขึ้น

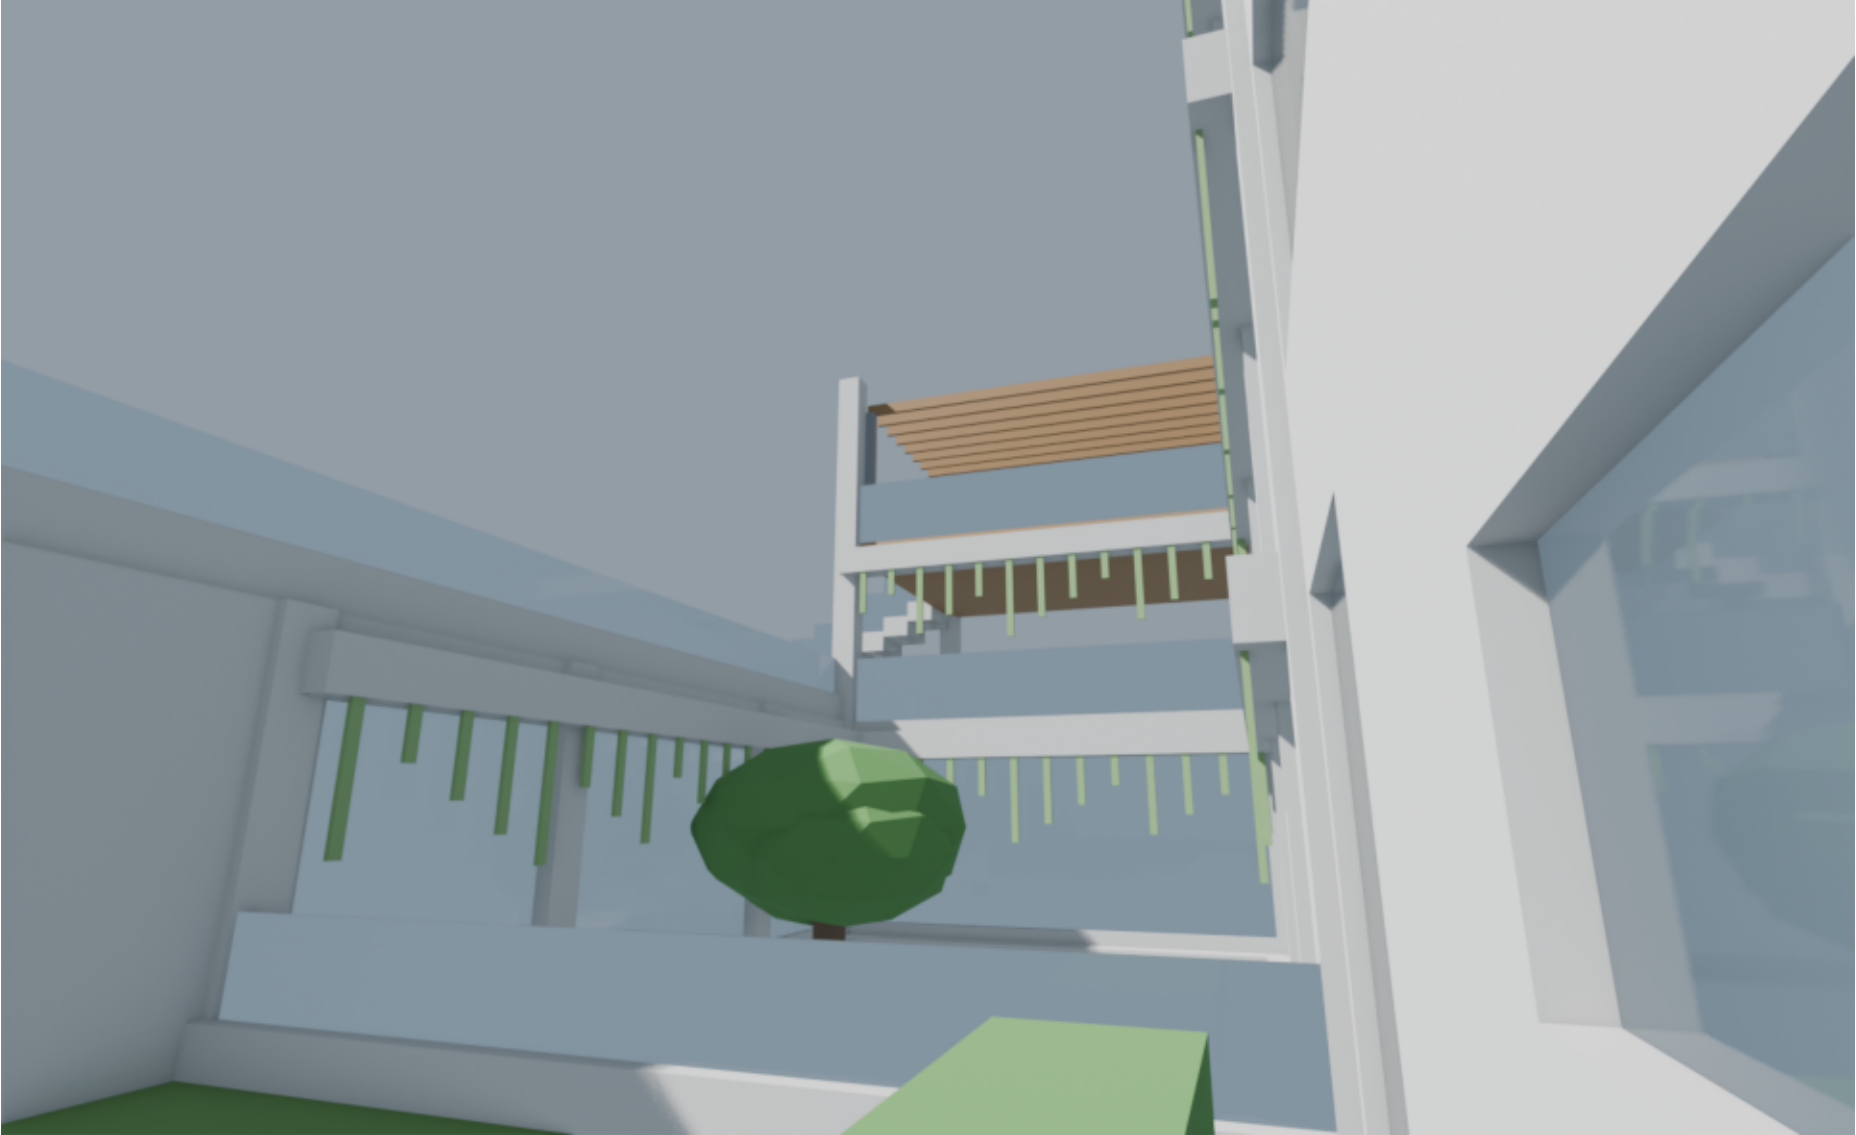

จากสวนทิศใต้ — ปีกใต้ 4 ชั้น รางต้นไม้ห้อยทุกขอบพื้น

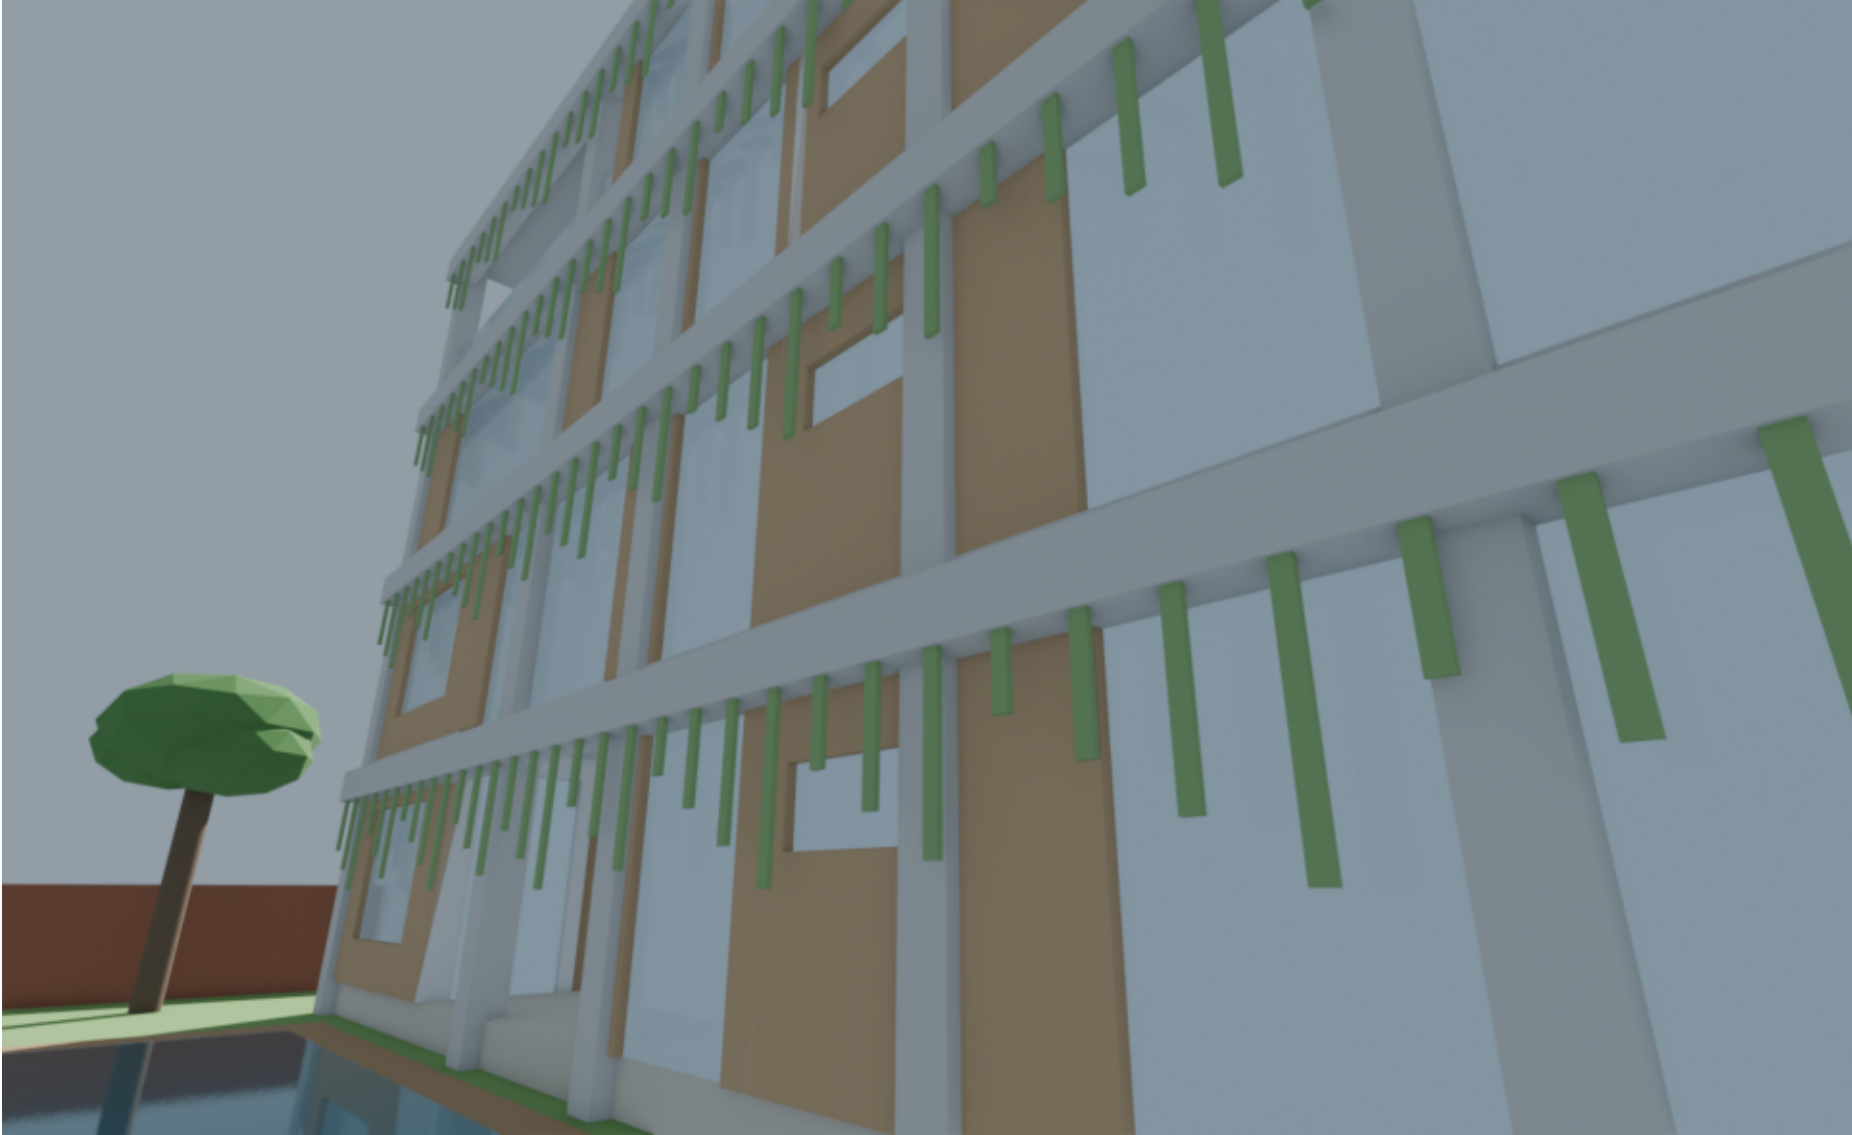

วัสดุหลัก

หมวด	ข้อกำหนด (ระดับแนวคิด)
โครงสร้าง	ค.ส.ล. เสา 0.40x0.40 กริด 6 x 4 แนว · พื้นคานแบน 0.20 · พื้นสวนหลังคารับน้ำหนักดินชั้นน้ำ · เสาเชื่อมเจาะ (รอมผลเจาะดิน)
ผนัง	ผนังข้าง/ด้านถนน อิฐมอญโซว์ 2 ชั้น + ช่องอากาศ · ด้านสระไม้กรุ · หน้าคอร์ตคอนกรีตเปลือย + กระงกบานเลื่อน · ภายนอก 120 / ห้องน้ำ 150
เพดานโค้งอิฐ	โค้งอิฐ (barrel vault) ช่วง 6.00 ม. สูงโค้ง 1.20 ม. บนคาน ค.ส.ล. รับแรงทับ — ต้องให้วิศวกรออกแบบ
สวน / ราง	สวนหลังคา 4 ระดับ + รางต้นไม้คอนกรีตขึ้น 0.45 ม. + สวนแนวตั้งบนโครงตะเอนเลส + น้ำหยดอัตโนมัติ
บันไดนอก	คอนกรีตหล่อ กว้าง 1.20 ม. ราวกระจก + มือจับ · ลีวกันสีน R11 · ไฟส่องทางทุกชั้น
กระจก	Low-E laminated · SHGC <= 0.25 ติดตะวันออก/ตะวันตก · กรอบอะลูมิเนียมสีฟ้า
พื้น	อิฐปูพื้น (คอร์ต/ศาลา) · ไม้เอ็นจิเนียร์ (ชั้น 2-4) · กระเบื้องกันลื่น R11
ภายนอก	สระน้ำเกลือ 14.00 x 2.70 สัก 1.40 ม. · สระสะท้อนเงาในคอร์ตสัก 0.30 ม. · รั้วอิฐ

สิ่งที่ต้องทำต่อ

- วิศวกรโครงสร้าง: พื้นสวนหลังคา (น้ำหนักดิน) + รางต้นไม้ยื่น + เพดานโค้งอิฐ + บันไดนอก 4 ช่วง + เสาเชื่อม
- วิศวกรงานระบบ: VRF + ERV, พัดลมระบาย, ระบบน้ำฝนไปหยด, ระบายน้ำคอร์ต, ขึ้นไฟ, โซลาร์ 9.90 kW
- ยืนยันกับสำนักงานเขต: ข้อ 27 (บันไดนอกผ่านสวนหลังคาเป็นทางหนีไฟ), ความกว้างถนน, ผังเมืองรวม
- จำลอง CFD/ความร้อน: คอร์ตเป็นปล่องลม (ยังเป็นลมมดีฐาน); จำลองแสง/แสงจ้าห้องชั้นคอร์ต
- แบบขยาย: ขอบพื้นที่คองมรอบคอร์ต, รางต้นไม้, บันไดนอก, ประตู panic ตู้สวน, เพดานโค้งอิฐ, ทางลาด 1:12
- ลงทะเบียน WELL Residence และเตรียมเอกสารตามตาราง
- ประมาณราคาละเอียด (BOQ) หลังได้แบบโครงสร้าง-งานระบบ

สรุปการตรวจ

ผลตรวจทั้งหมด 120 รายการ: ผ่าน 120 / ไม่ผ่าน 0 (รายการ "ยกเว้น" มีเหตุผลกำกับ ดู A-11)
แบบระดับ design development ต้องให้สถาปนิกและวิศวกรผู้ได้รับใบอนุญาตตรวจสอบและลงนามก่อนยื่นขออนุญาต

H3A DESIGN AND BUILD

X-UNIT Architecture Lab

โครงการ

WELL-RIVERA 30x30

Executive Luxury Villa
บ้านเดี่ยว 4 ชั้น ผ่านเกณฑ์
WELL for Residential (เจดนา)

ที่ดิน 30.00 x 30.00 ม. = 225 ตร.ว.
ถนนสาธารณะติดเหนือ (สมบัติ 8.00 ม.)

แนวคิด

ตีความจาก Rivera Paradise (AtelierM):
คอร์ตกลาง + บันไดเกลียวคู่ (ใน/นอก)
+ ปกคลุมชั้นแบบเกลียว หลังคาส่วนทุกชั้น
+ ผนังอิฐโซว์ + เพดานโค้งอิฐ

ระดับ

±0.00 ถนน · F1 +0.45 · F2 +3.65
F3 +6.85 · F4 +10.05
ลาดฟ้า +13.25 · ราว +14.35
โค้งอิฐ สปริง +5.45 ยอด +6.65

หมายเหตุ

- หน่วยเป็นมิลลิเมตร เว้นแต่ระบุ
- ระดับอ้างอิงถนนหน้าที่ดิน ±0.00
- ห้ามวัดขนาดจากแบบ ใช้ตัวเลขกำกับ
- แบบระดับ Design Development

ต้องให้สถาปนิกและวิศวกรผู้ได้รับ
ใบอนุญาตตรวจสอบและลงนาม
ก่อนยื่นขออนุญาต

ชื่อแผ่น

WELL for Residential
+ วัสดุ + สิ่งที่ต้องทำต่อ

มาตราส่วน ไม่มีมาตราส่วน

วันที่ 6 ค.ค. 2569 ฉบับ v1 / DD