


WELL-GBEACH 30x30 - Executive Luxury Villa - บ้านเดี่ยว 4 ชั้น "แท่งบนเสาลอย + หงกระบอกอิฐ" (แนวคิดจาก G-Beach Residence)

ที่ดิน 30.00 x 30.00 ม. (225 ตร.ว.) - ถนน (สมมติ 8.00 ม.) - ที่ดินเดิม - โปรแกรม ARCHISPACE 6 ต.ค. 2569

ภาพจากโมเดล Blender (WELL-GBEACH-30x30-model.blend) — โมเดลมวลอาคารระดับ DD สร้างจากข้อมูลชุดเดียวกันแบบ CAD

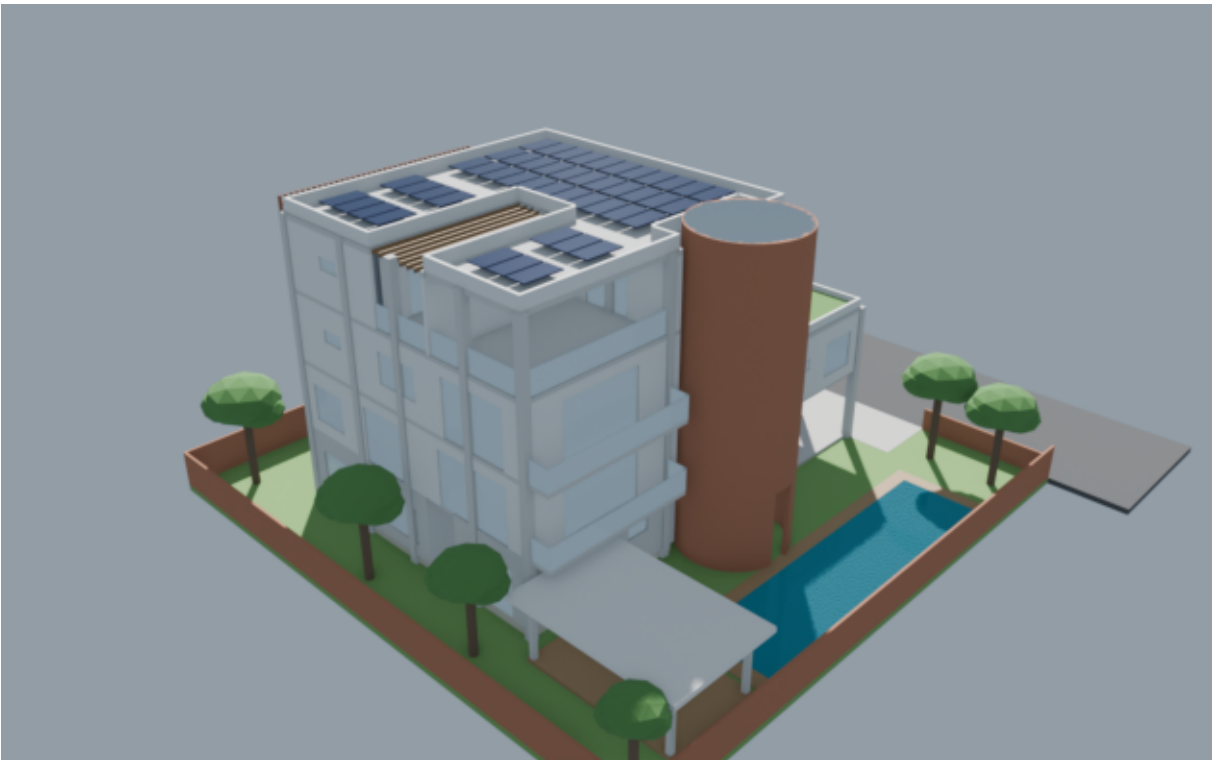


มุมมองทางอากาศ หิศตะวันตกเฉียงใต้ — แท่งอาคารบนเสาลอย, หงกระบอกอิฐ, ระเบียงหิศตะวันตก, สระ 3.80 x 16.00 ม.




จากถนนทิศเหนือ — โรงจอดรถใต้เสาลอย (Pilots) และโถงทางเข้า

โตะแกรมผัง (ชั้น 2, 1:250): แท่งบนเสาลอย + หงกระบอก + ผนังอิฐโปร่ง + สวนสระหิศตะวันตก

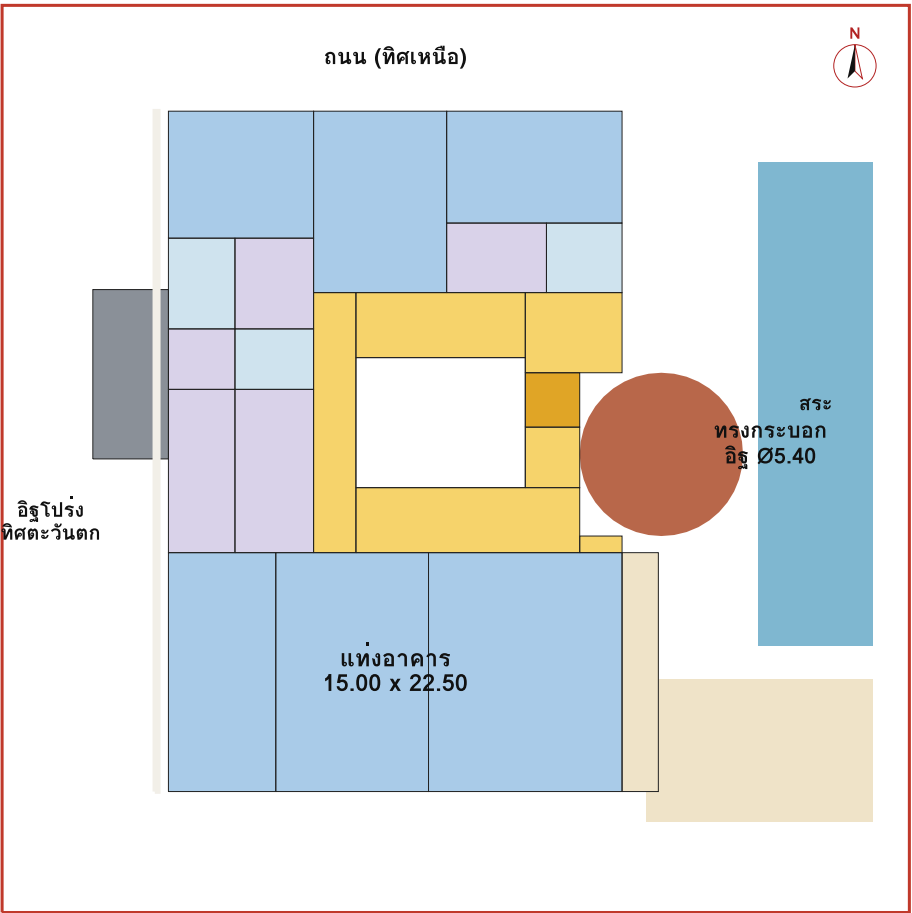


มุมมองหิศตะวันตกเฉียงใต้ — ผนังอิฐโปร่งหิศตะวันตก (บังแดดบ่าย) + บันไดหนีไฟเหล็กภายนอก

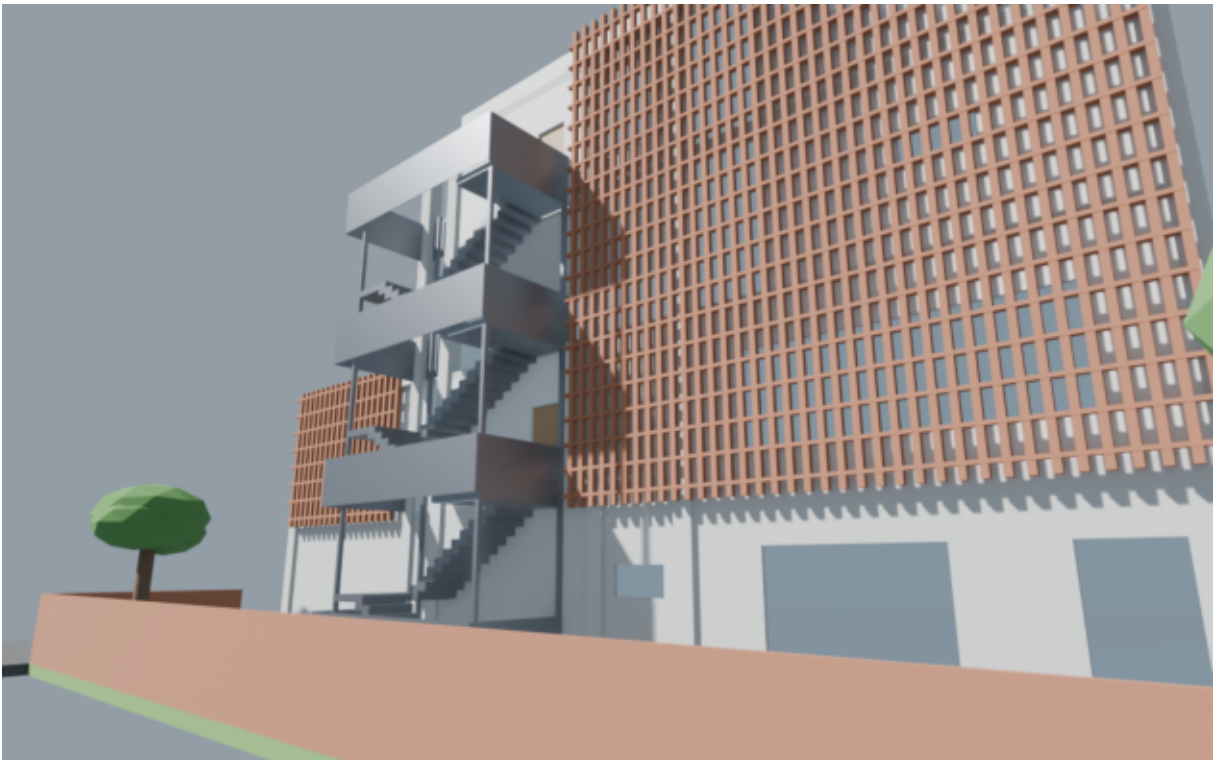

ผนังอิฐโปร่ง (ครึ่งอิฐ 115 มม. @290 + แบนบน @520) ทำหน้าอาคาร 0.34-0.45 ม.

โตะแกรมรูปตัด A-A (1:250): บังแดดตะวันตก / ระบายอากาศข้ามห้อง ตะวันออก-ตะวันตก

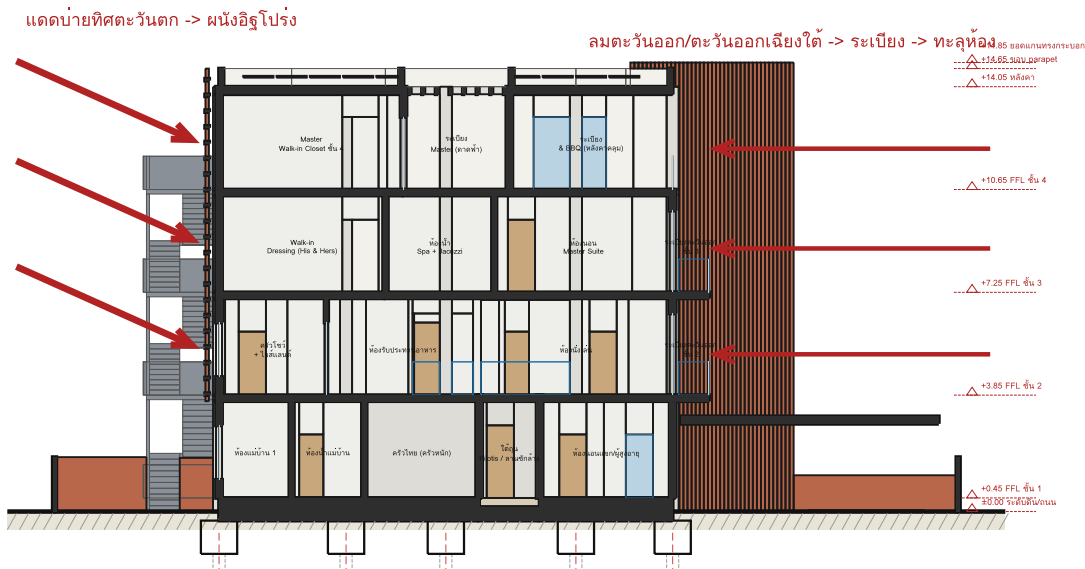

ลูกศร = เจดนามการออกแบบ (หิศลมประจักษ์ทุ่งเพชร ดูจุดอื่น S/SW, หน้า NE) — ยังไม่ได้พิสูจน์ด้วย CFD/การจำลองแสง

G-Beach Residence — ข้อเท็จจริงที่ตรวจได้

หัวข้อ	ข้อเท็จจริงจากแหล่งชี้แนะ (ArchDaily / whitemad / jidpi)
ที่ตั้ง / ปี	Jesolo อิตาลี - 2025 - 4,520 ตร.ม. (อาคารชุดพักอาศัย ไม่ใช้บ้านเดี่ยว)
ผู้ออกแบบ	B+D+M Architeti (Alex Braggion, GianPaolo Di Benedetto)
บริบท	ตั้งข้าง Hotel Bellevue (1956, Renzo Meneguzzo) ที่อ้างถึงห้องสมุด Belo Horizonte ของ Niemeyer
ผัง	แท่งยาว วางตั้งฉากกับโรงแรม ล้อมคอร์ต - ชั้นล่างกระจก บนเสาลอย (pilots)
ผิว / วัสดุ	คอนกรีต กระจก อิฐโชว์แนว - ผนังอิฐโปร่ง (openwork brick lattice)
องค์ประกอบ	แกนทรงระบอก - ระเบียงรอบ - loggia หิศตะวันตก - ลาดพาดมโโด 360° - ที่จอดรถใต้ดิน

การตีความ -> แบบบ้านหลังนี้

องค์ประกอบ	การตีความของผม (ไม่ใช่คำอธิบายของสถาปนิก)
แท่งบนเสาลอย	แท่ง 15.00 x 22.50 ม. วางแนวเหนือ-ใต้ ชั้น 1 เปิดโล่งเป็นโรงรถใต้ถุน ชั้น 3-4 ตั้งลงเหนือ 15.30 ม.
ทรงกระบอก	แกนบันได U อิฐโชว์ Ø5.40 ม. ยื่นออกหิศตะวันออก สูง +14.85 ช่องแสงระงกที่ยอด
อิฐโปร่ง	ย้ายมาไว้หิศตะวันตก = หิศแดดบ่ายของทุ่งเพชร หน้า loggia ชั้น 3 และผนังชั้น 2-4
ระเบียง / loggia	ระเบียงลึก 1.20 ม. หิศตะวันออก ชั้น 2-3 - loggia ตะวันตก+เหนือ ชั้น 3
ลาดพาด 360°	ชั้น 4: ระเบียง Master เบ็ดพาด + ระเบียง BBQ หลังคาคลุม
ไม่นำมาใช้	ที่จอดรถใต้ดิน (นำที่ดินสุดด้านซ้าย) -> จอดใต้ลาดมโโดที่ระดับดิน

รายงานข้อจำกัด (ตรงไปตรงมา)

- โปรแกรมขัดกัน: Master Suite ชั้น 3 แต่ Closet 36 + Terrace 28 ชั้น 4 -> ทำ Master duplex มีบันไดส่วนตัวชั้น 3-4 (ตามทีเลือก)
- Pantry โปรแกรมอยู่ชั้น 3 ห่างจากครัว -> ย้ายไปชั้น 2 ติดครัวโชว์ (ตามที่เลือก)
- ความสูงชั้น 2.80 ในโปรแกรม = ระเบียงโปร่ง; ใช้พื้นที่พื้น 3.40 ม. -> หลังคา +14.05, ยอดทรงระบอก +14.85 ต่ำกว่า 15.00 ม. แต่ 0.15 ม. (ห้ามเพิ่มลิ้งน้ำห้องบนหลังคา)
- GFA 1225.50 vs โปรแกรม 984.70 (+24.5%): หงกระบอก 4 ชั้น 91.6 + บันไดหนีไฟ 56.0 + สัญจร 206.7 + loggia ชั้น 3 83.3 (ชั้น 4 ต้องการพื้นที่มากกว่าชั้น 3 ในโปรแกรม จึงเหลือเป็น loggia)
- บันไดหนีไฟภายนอก (ฉ.55 ข้อ 27 สำหรับอาคาร 4 ชั้น) — ต้องยืนยันกับเจ้าพนักงานว่าบ้านเดี่ยวต้องมีหรือไม่; ชั้น 2 ทางหนีไฟผ่านครัวโชว์และ Pantry
- ค่าที่ขณกนทพอส: บันไดหนีไฟทางเขต 3.00 ม. (ข้อ 50), ซานพัก = ความกว้างบันได 1.00 ม., ทางลาด 1:12 ยังไม่ได้เขียน (โรงรถ +0.15 -> โถง +0.45)
- ความกว้างถนนไม่ทราบ — สมมติ 8.00 ม. (ระยะร่น 1/10 = 0.80 ม.; แบนบนจริง 3.50 ม.)
- ห้องลิกกิน 4.20 ม. (ยกเว้นพร้อมเหตุผล): ห้องอาหาร ห้องนั่งเล่น ห้องนอน Master ห้องนั่งเล่นครอบครัว ห้องทำงาน (แสงเหนือ+ช่องแสงหลังคา) เรียงเตอร์
- ห้องที่ช่องเปิดไม่ถึง 10% ใช้พัดลมระบาย (ฉ.39 ข้อ 6 วรรคสอง): 15 ห้อง (รายชื่อใน A-12)
- ทรงกระบอกอิฐ 4 ชั้น + ผนังอิฐโปร่ง -146 ตร.ม. ต้องมีโครเหล็ก/ค.ส.ล. รับแรงลม-แผ่นดินไหว (วิศวกรโครงสร้าง)
- ไม่ทราบผังเมืองรวม/ข้อบัญญัติท้องถิ่น (FAR/OSR/ความสูง) — ต้องตรวจก่อนยื่น

แหล่งข้อมูลอ้างอิง G-Beach

- archdaily.com/1042315 (G-Beach Residence / B+D+M Architeti)
- whitemad.pl (บทความโครงการ G-Beach)
- architectures.jidpi.com (G-Beach Residence)
- architizer.com/projects/g-beach-residence (ลิงก์ที่ใช้ให้มา)

ไม่ได้รับแบบจริงของโครงการ — สัดส่วน ขนาด และรายละเอียดทั้งหมดในชุดนี้เป็นกรออกแบบใหม่ ไม่ใช้การคัดลอกหรือย่อด้านอาคารต้นแบบ

H3A DESIGN AND BUILD

X-UNIT Architecture Lab

โครงการ

WELL-GBEACH 30x30

Executive Luxury Villa
บ้านเดี่ยว 4 ชั้น ผ่านเกณฑ์
WELL for Residential (เจดนา)

ที่ดิน 30.00 x 30.00 ม. = 225 ตร.ว.
ถนนสาธารณะหิศเหนือ (สมมติ 8.00 ม.)

แนวคิด

จาก G-Beach Residence (B+D+M):
แท่ง 15.00 x 22.50 ม. บนเสาลอย
+ แกนบันไดทรงกระบอกอิฐ Ø5.40
+ ผนังอิฐโปร่งหิศตะวันตก

ระดับ

±0.00 ถนน - F1 +0.45 - F2 +3.85
F3 +7.25 - F4 +10.65
หลังคา +14.05 - parapet +14.65
ยอดทรงระบอก +14.85

หมายเหตุ


- หน่วยเป็นมิลลิเมตร เว้นแต่ระบุ
- ระดับอ้างอิงถนนพื้นที่ดิน ±0.00
- ห้ามวัดขนาดจากแบบ ใช้ตัวเลขกำกับ
- แบบระดับ Design Development
- ต้องให้สถาปนิกและวิศวกรผู้ได้รับใบอนุญาตตรวจสอบและลงนามก่อนยื่นขออนุญาต

ชื่อแผ่น

แนวคิด G-Beach -> บ้าน 30x30
+ รายงานข้อจำกัด

มาตรฐาน ไม่มีมาตรฐาน

วันที่ 6 ต.ค. 2569 ฉบับ v1 / DD

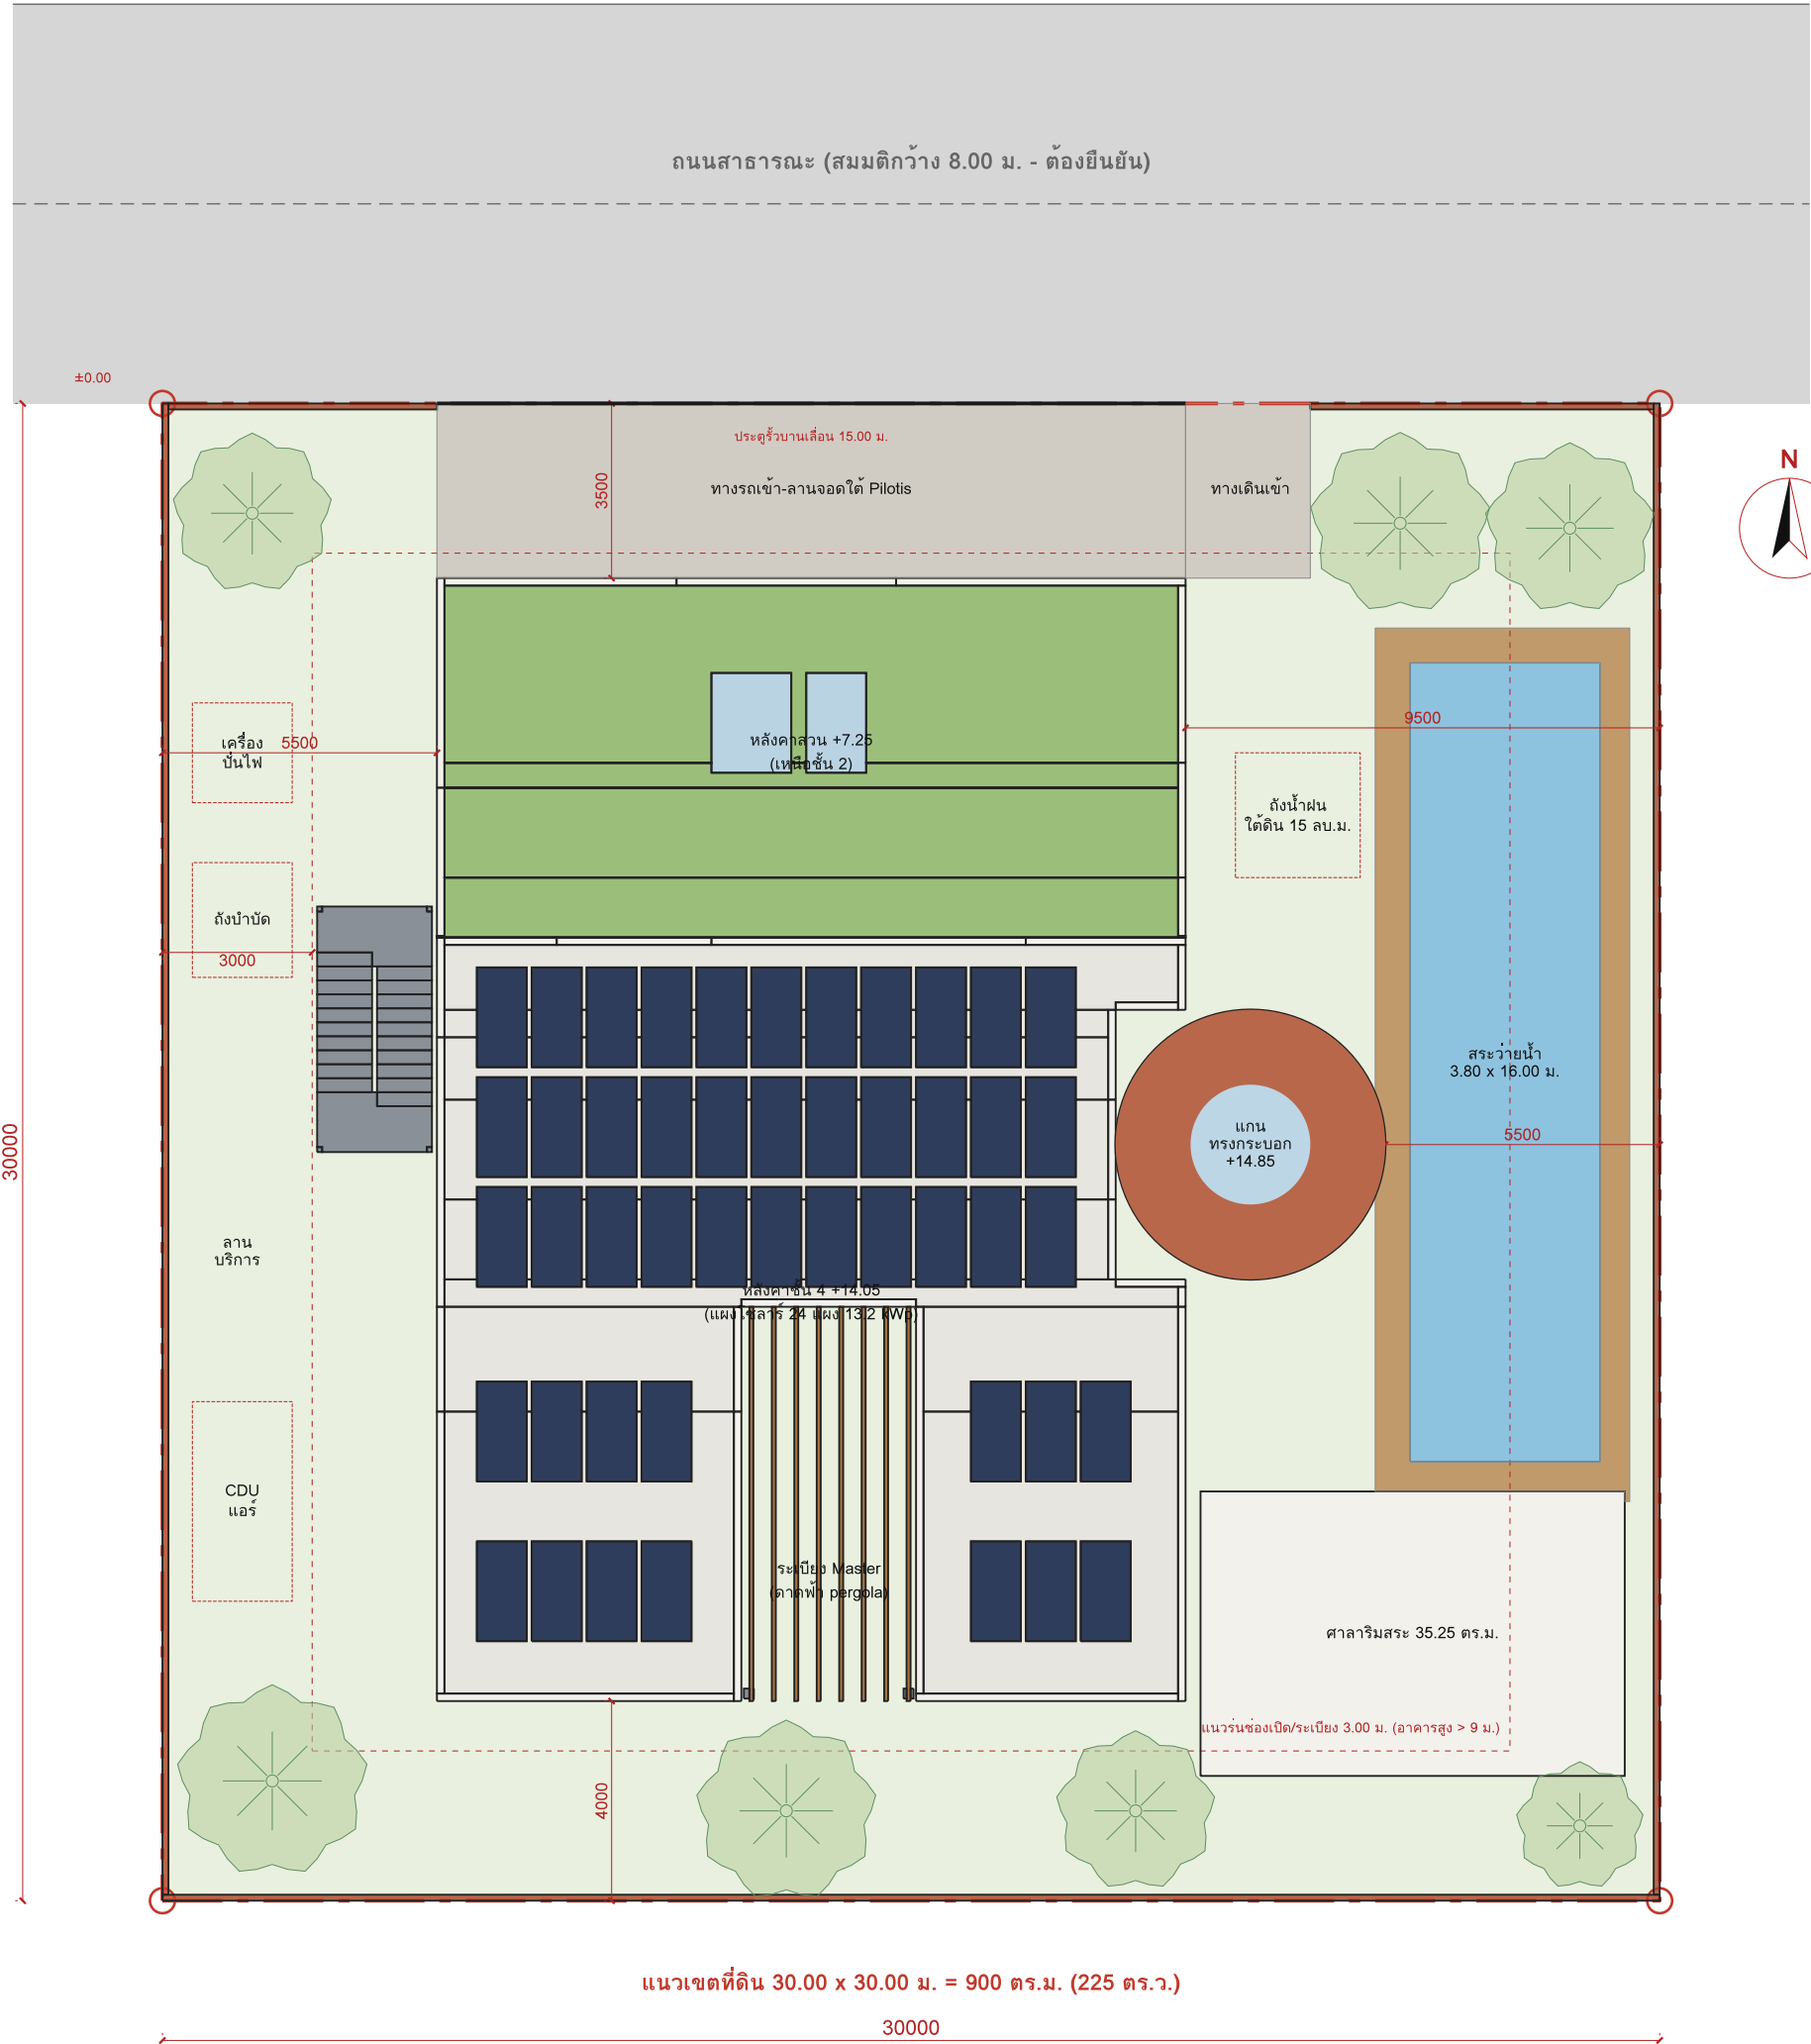

ผังบริเวณ SITE PLAN 1:150



ตารางกฎกระทรวง ฉบับที่ 55 (2543) และระยะเว้น

ชั้น	รายการ	ค่าในแบบ	เกณฑ์	ผล
ชั้น 20	ห้องนอน 2	11.52 ตร.ม. (ด้านแคบ 2.40)	>= 8.00 ตร.ม.	ผ่าน
ชั้น 20	ห้องนอน 1	11.76 ตร.ม. (ด้านแคบ 2.40)	>= 8.00 ตร.ม.	ผ่าน
ชั้น 20	ห้องนอนชายผู้สูงอายุ	19.36 ตร.ม. (ด้านแคบ 4.40)	>= 8.00 ตร.ม.	ผ่าน
ชั้น 20	ห้องนอน Junior Suite 2	20.16 ตร.ม. (ด้านแคบ 4.20)	>= 8.00 ตร.ม.	ผ่าน
ชั้น 20	ห้องนอน Junior Suite 3	21.46 ตร.ม. (ด้านแคบ 3.70)	>= 8.00 ตร.ม.	ผ่าน
ชั้น 20	ห้องนอน Master Suite	46.61 ตร.ม. (ด้านแคบ 5.90)	>= 8.00 ตร.ม.	ผ่าน
ชั้น 22	ความสูงโปร่ง (FF 3.40 - พื้น 0.20 - มั้วงา	2.80 ม.	>= 2.60 ม.	ผ่าน
ชั้น 22	โถงลิ้นชัก 2 ชั้น	6.20 ม.	>= 2.60 ม.	ผ่าน
ชั้น 23	บันไดเหล็ก (ในเกณฑ์กระทรวง): ลูกตั้ง / ลูกนอน	170 / 280 มม.	<= 200 / >= 220	ผ่าน
ชั้น 23	บันไดเหล็ก (ในเกณฑ์กระทรวง): ความกว้าง	1000 มม.	>= 800	ผ่าน
ชั้น 23	บันไดเหล็ก (ในเกณฑ์กระทรวง): ขานเหล็ก (ลึก)	1000 มม.	>= ความกว้าง 1000	ผ่าน
ชั้น 23	บันไดเลื่อน Master ชั้น 3-4: ลูกตั้ง / ลูกนอน	170 / 280 มม.	<= 200 / >= 220	ผ่าน
ชั้น 23	บันไดเลื่อน Master ชั้น 3-4: ความกว้าง	1000 มม.	>= 800	ผ่าน
ชั้น 23	บันไดเลื่อน Master ชั้น 3-4: ขานเหล็ก (ลึก)	1000 มม.	>= ความกว้าง 1000	ผ่าน
ชั้น 23	บันไดเลื่อน Master ชั้น 3-4: ลูกตั้ง / ลูกนอน	170 / 280 มม.	<= 200 / >= 220	ผ่าน
ชั้น 23	บันไดเลื่อน Master ชั้น 3-4: ความกว้าง	1100 มม.	>= 800	ผ่าน
ชั้น 23	บันไดเลื่อน Master ชั้น 3-4: ขานเหล็ก (ลึก)	1200 มม.	>= ความกว้าง 1100	ผ่าน
ชั้น 23	ช่องบันไดเลื่อนข้าง	1.70 ม. (10 ชั้น)	<= 3.00 ม.	ผ่าน
ชั้น 23	ระยะบันไดเลื่อนขึ้นบันได	>= 3.03 ม.	>= 1.90 ม.	ผ่าน
ชั้น 23	2R+T	620 มม.	600-650	ผ่าน
ชั้น 27	อาคาร 4 ชั้น: บันไดเหล็กที่ไม่ใช่แนวตั้ง	บันไดเหล็กภายนอก กว้าง 1.10 ม. ขึ้นบัน	ปี / กว้าง >= 0.80 / ขึ้น <	ผ่าน
ชั้น 27	ทางเข้าบันไดไฟฟ้าทุกชั้น	ชั้น 2: หน้าครัว>Pantry, ชั้น 3: ลอ	เข้าลิฟต์โดยไม่มีลิฟต์	ผ่าน
ชั้น 33	ที่ว่าง (ไม่คิดในอาคาร)	52.5% (คลุมดิน 427.25 ตร.ม.)	>= 30%	ผ่าน
ชั้น 33	ที่ว่าง (ไม่คิดในอาคาร)	52.5%	>= 30%	ผ่าน
ชั้น 50	ช่องเปิดลิ้นชักบันได (อาคารสูง 14.85 ม.)	3.50 ม. (W13 F2 ห้องนอน Junior Suite	>= 3.00 ม.	ผ่าน
ชั้น 50	ระยะบันไดเลื่อนขึ้นบันไดไฟฟ้า ลิ้นชัก	3.00 ม.	>= 3.00 ม.	ผ่าน
ชั้น 50	ชายคาบันไดบันไดบันได	0.70 ม.	>= 0.50 ม.	ผ่าน
ชั้น 50	บันไดบันไดบันไดบันได	3.50 ม.	>= 3.00 ม. (บันไดบันได, ส	ผ่าน
บันไดบันได	อาคารบันไดบันได (บันไดบันได 8.00 ม.)	3.50 ม.	>= 1/10 ความกว้างบันได < 0.8	ผ่าน

* รั้วแนวถนน: อาคารสูงไม่เกิน 15 ม. ถนนกว้าง 6-20 ม. รั้ว 1/10 ของความกว้างถนน (ความกว้างถนนเป็นค่าสมมติ — ตารางข้างต้นมีกฎบังคับทั้งเส้น)

พื้นที่อาคาร (คิดถึงแนวศูนย์กลางผนัง)

ชั้น	บิลลิเมนต์	พื้นที่ภายนอก	จอสถ	บันไดไฟฟ้า	รวม ตร.ม.
ชั้น 1	237.16	25.68	90.00	14.00	352.84
ชั้น 2	328.76	9.48	-	14.00	338.24
ชั้น 3	171.07	83.26	-	14.00	254.32
ชั้น 4	174.53	70.31	-	14.00	244.84
ศาลาริมสระ	-	35.25	-	-	35.25
รวม	911.52	223.98	90.00	56.00	1225.50
โปรแกรม					984.70
ส่วนต่าง					+240.80 (+24.5%)

* รวมเกณฑ์กระทรวง 22.90 ตร.ม./ชั้น (คิดเป็นจอสถ) - บันไดไฟฟ้าภายนอกไม่รวมใน GFA

ที่ว่างและการใช้ที่ดิน

รายการ	ค่า
พื้นที่ดิน	900.00 ตร.ม. (225 ตร.ว.)
พื้นที่อาคารคลุมดิน (รวมศาลา)	427.25 ตร.ม. (47.5%)
ที่ว่าง	52.5% (เกณฑ์ >= 30%)
FAR (GFA Decks / ที่ดิน)	1.01 : 1
ความสูงอาคาร	หลังคา 14.05 / parapet 14.65 / ยอดทรงระลอก 14.85 ม. (< 15.00)
ที่ดินชั้นล่างตามโปรแกรม	113 ตร.ว. — ที่ดินจริง 225 ตร.ว.

ประมาณราคาค่าก่อสร้าง (ระดับแนวคิด)

วัสดุ	สูตร (บาท/ตร.ม.)	คำนวณ
(ก) อัตราแยกมาตรฐาน	บิลลิเมนต์ 911.52 x 22,000 + ที่ภายนอก 223.98 x 11,000 + จอสถ 90.00 x 8,000	23.24
(ข) อัตราแยก luxury	บิลลิเมนต์ x 30,000 + ที่ภายนอก x 15,000 + จอสถ x 12,000	31.79
(ค) อัตราเดียว (ใช้เดียวกับโปรแกรม)	GFA 1225.50 x 30,000	36.76
งานแยกอาคาร	สระ 60.8 ตร.ม. x 35,000 + PV 25.85 kWp x 45,000 + ภูมิทัศน์ขั้น 1.80 + ลิฟต์ 0.90 + บันไดไฟฟ้า 1.20 ม.	7.19
โปรแกรม ARCHSPACE	984.70 x 30,000 (รวม 26.00-36.93 ล้าน)	29.54

อัตราแยก vs อัตราเดียว (ก) 23.24 ล้าน ค่าว่างโปรแกรม: (ข) 31.79 ล้าน อยู่ในช่วง 26.00-36.93; (ค) 36.76 ล้าน และขอบบนของช่วง เพราะ GFA มากกว่าโปรแกรม 24.5%

รวมงานแยกอาคาร: (ข)>7.19 = 38.98 ล้าน - (ค)>7.19 = 43.96 ล้าน (เกินขอบบนโปรแกรม)

ดังนั้นรวม: เลือกชั้นฐานราก (รวมและที่ดิน), เพอร์มิตเจอร์รี่ตัว, ภาษีค่าธรรมเนียม, ค่าออกแบบ

H3A DESIGN AND BUILD

X-UNIT Architecture Lab

โครงการ

WELL-GBEACH 30x30

Executive Luxury Villa

บ้านเดี่ยว 4 ชั้น ผ่านเกณฑ์

WELL for Residential (เจดนา)

ที่ดิน 30.00 x 30.00 ม. = 225 ตร.ว.
ถนนสาธารณะที่ดิน (สมมติ 8.00 ม.)

แนวคิด

จาก G-Beach Residence (B+D+M):

แห่ง 15.00 x 22.50 ม. บนเสาลอย

+ แกนบันไดทรงระลอกอิฐ Ø5.40

+ ผืนอิฐปูบันไดทิศตะวันตก

ระดับ

±0.00 ถนน - F1 +0.45 - F2 +3.85
F3 +7.25 - F4 +10.65
หลังคา +14.05 - parapet +14.65
ยอดทรงระลอก +14.85

หมายเหตุ

- หน่วยงานเป็นนิติบุคคล เว้นแต่ระบุ
- ระดับอ้างอิงถนนพื้นที่ดิน ±0.00
- หารั้วขุดดินจากแบบ ใช้ตัวเลขกำกับ
- แบบระดับ Design Development
- ต้องให้สถาปนิกและวิศวกรผู้ได้รับใบอนุญาตตรวจสอบและลงนามก่อนยื่นขออนุญาต

ชื่อแผ่น

ผังบริเวณ + ตารางกฎหมาย
+ ประมาณราคา

มาตราส่วน 1:150

วันที่ 6 ต.ค. 2569 ฉบับ v1 / DD



ลำดับ	ห้อง	ขนาด ม.	คร.ม.	ประเภท
101	โรงจอดรถ 4 คัน (ใต้ Pilotis)	15.00 x 6.00	90.00	จอดรถ
102	ห้องแม่บ้าน 2	4.80 x 2.40	11.52	ห้องใช้งาน
103	ห้องแม่บ้าน 1	2.40 x 4.90	11.76	ห้องใช้งาน
104	ห้องแม่บ้านบาน	2.40 x 2.50	6.00	ห้องนั่งเฝ้ายาม
105	ทางเดินบริการ	2.40 x 2.40	5.76	สัญจร
106	ห้องซักผ้า	4.80 x 3.40	16.32	บริการ
107	ห้อง MEP / ไฟฟ้า	4.80 x 2.90	13.92	บริการ
108	ห้องเก็บของ / ต้นข้าวรถ	4.80 x 2.90	13.92	บริการ
109	ครัวใหม่ (ครัวหน้าดิน)	3.80 x 5.30	20.14	ห้องใช้งาน
110	โถงบัน Pilotis / ลานซักผ้า	2.00 x 7.90	25.68	ลักษณะนอก
112	ห้องแม่บ้าน/ห้องอยู่อาศัย	4.40 x 4.40	19.36	บริการ
113	ตู้เสื้อผ้าห้องแขก	2.20 x 3.50	7.70	บริการ
114	ห้องน้ำในห้องแขก	2.20 x 3.50	7.70	ห้องนั่งเฝ้ายาม
115	โถงกลาง	8.80 x 2.15	19.69	สัญจร
117	ทางเดินบริการเหนือ	1.40 x 6.45	9.03	สัญจร
118	โถงคั่นบันจูง 2 ชั้น	5.60 x 4.30	24.08	สัญจร
119	โถงทางเข้า (Vestibule)	5.60 x 2.15	12.04	สัญจร
120	โถงลิฟต์	1.80 x 2.00	3.60	สัญจร
121	ห้องเก็บเสื้อผ้า	3.20 x 2.65	8.48	บริการ
122	แกนบันไดทรงระลอก	Ø 5.40	22.90	แกนบันได
123	ลิฟต์บ้าน	1.80 x 1.80	3.24	ลิฟต์
124	บันไดโคมไฟภายนอก	2.50 x 5.60	14.00	บันไดโคมไฟ

ตัวชี้วัด 1	ค.ร.ม.
พื้นที่ปิดล้อม (รวมแกน)	237.16
กิ่งภายนอก	25.68
จุดยอด	90.00
รวม	352.84
บันทึกพื้นที่ภายนอก (ไม่รวม)	14.00

ชั้น 1 = วิศวกรสายงาน (Pilots): โดเมนตรง 4 ชั้นใต้ห้องอาคาร (+0.15) และใต้ภูมิ/ลานข้างข้างใต้โถง เปิดโล่ง ระบบงาน โดเมนตรงช่วง 2 ชั้น (+0.45) เข้าจากตรงด้านหน้าห้องพักประตูดัง 2.00 ม.; ทางลาด 1:12 ยาว 3.60 ม. คองส์เพื่อในแบบขยายแบบแรกประตูดัง 0.5-0.6 (ภายใน 0.5-0.6) ปักสูง 170 / สูงตรง 280 กว้าง 1.00 ม. ประตูดัง 2.05* (โถง) และ 0° (ประตูระบิบการที่หัดระบิบ: ตัวโถง โถงแบบ 2 ห้อง 2 ชั้น MEP โถงกับของ/คนขับรถ – ออกกับบันไดใหม่/โถงภายนอกห้องนอนแบบ (ผู้สูงอายุ) ใต้ใต้-ระบิบ: ประตูดังแบบเข้าห้องนี้ โกลีฟิด

จุดชาร์จรถไฟฟ้า (EV) 1 จุดในโรงรถ (WELL R-A09)

X-UNIT Architecture Lab

WELL-GBEACH 30x30

ที่ดิน 30.00 x 30.00 ม. = 225 ตร.ว.
ถนนสาธารณะทิศเหนือ (สมบัติ 8.00 ม.)


จาก G-Beach Residence (B+D+M):
 แท่ง 15.00 x 22.50 ม. บนเสาหล่อ
 + แกนบันไดทรงกระบอกอิฐ Ø5.40
 + ผนังอิฐโปรงหิวดะวันตก

±0.00 ถนน · F1 +0.45 · F2 +3.85
F3 +7.25 · F4 +10.65
หลังคา +14.05 · parapet +14.65
ยอดทรงกระบอก +14.85

หน่วยเป็นมิลลิเมตร เว้นแต่ระบุ
ระดับอ้างอิงบนหน้าที่ดิน ± 0.00
ห้ามวัดขนาดจากแบบ ใช้ตัวเลขกำกับ
แบบระดับ Design Development
ต้องให้สถาปนิกและวิศวกรผู้ได้รับ
ใบอนุญาตตรวจสอบและลงนาม
ก่อนยื่นขออนุญาต

ผังพื้นชั้น 1
(FFL +0.45)

วันที่ 6 ต.ค. 2569 ฉบับ v1 / DD

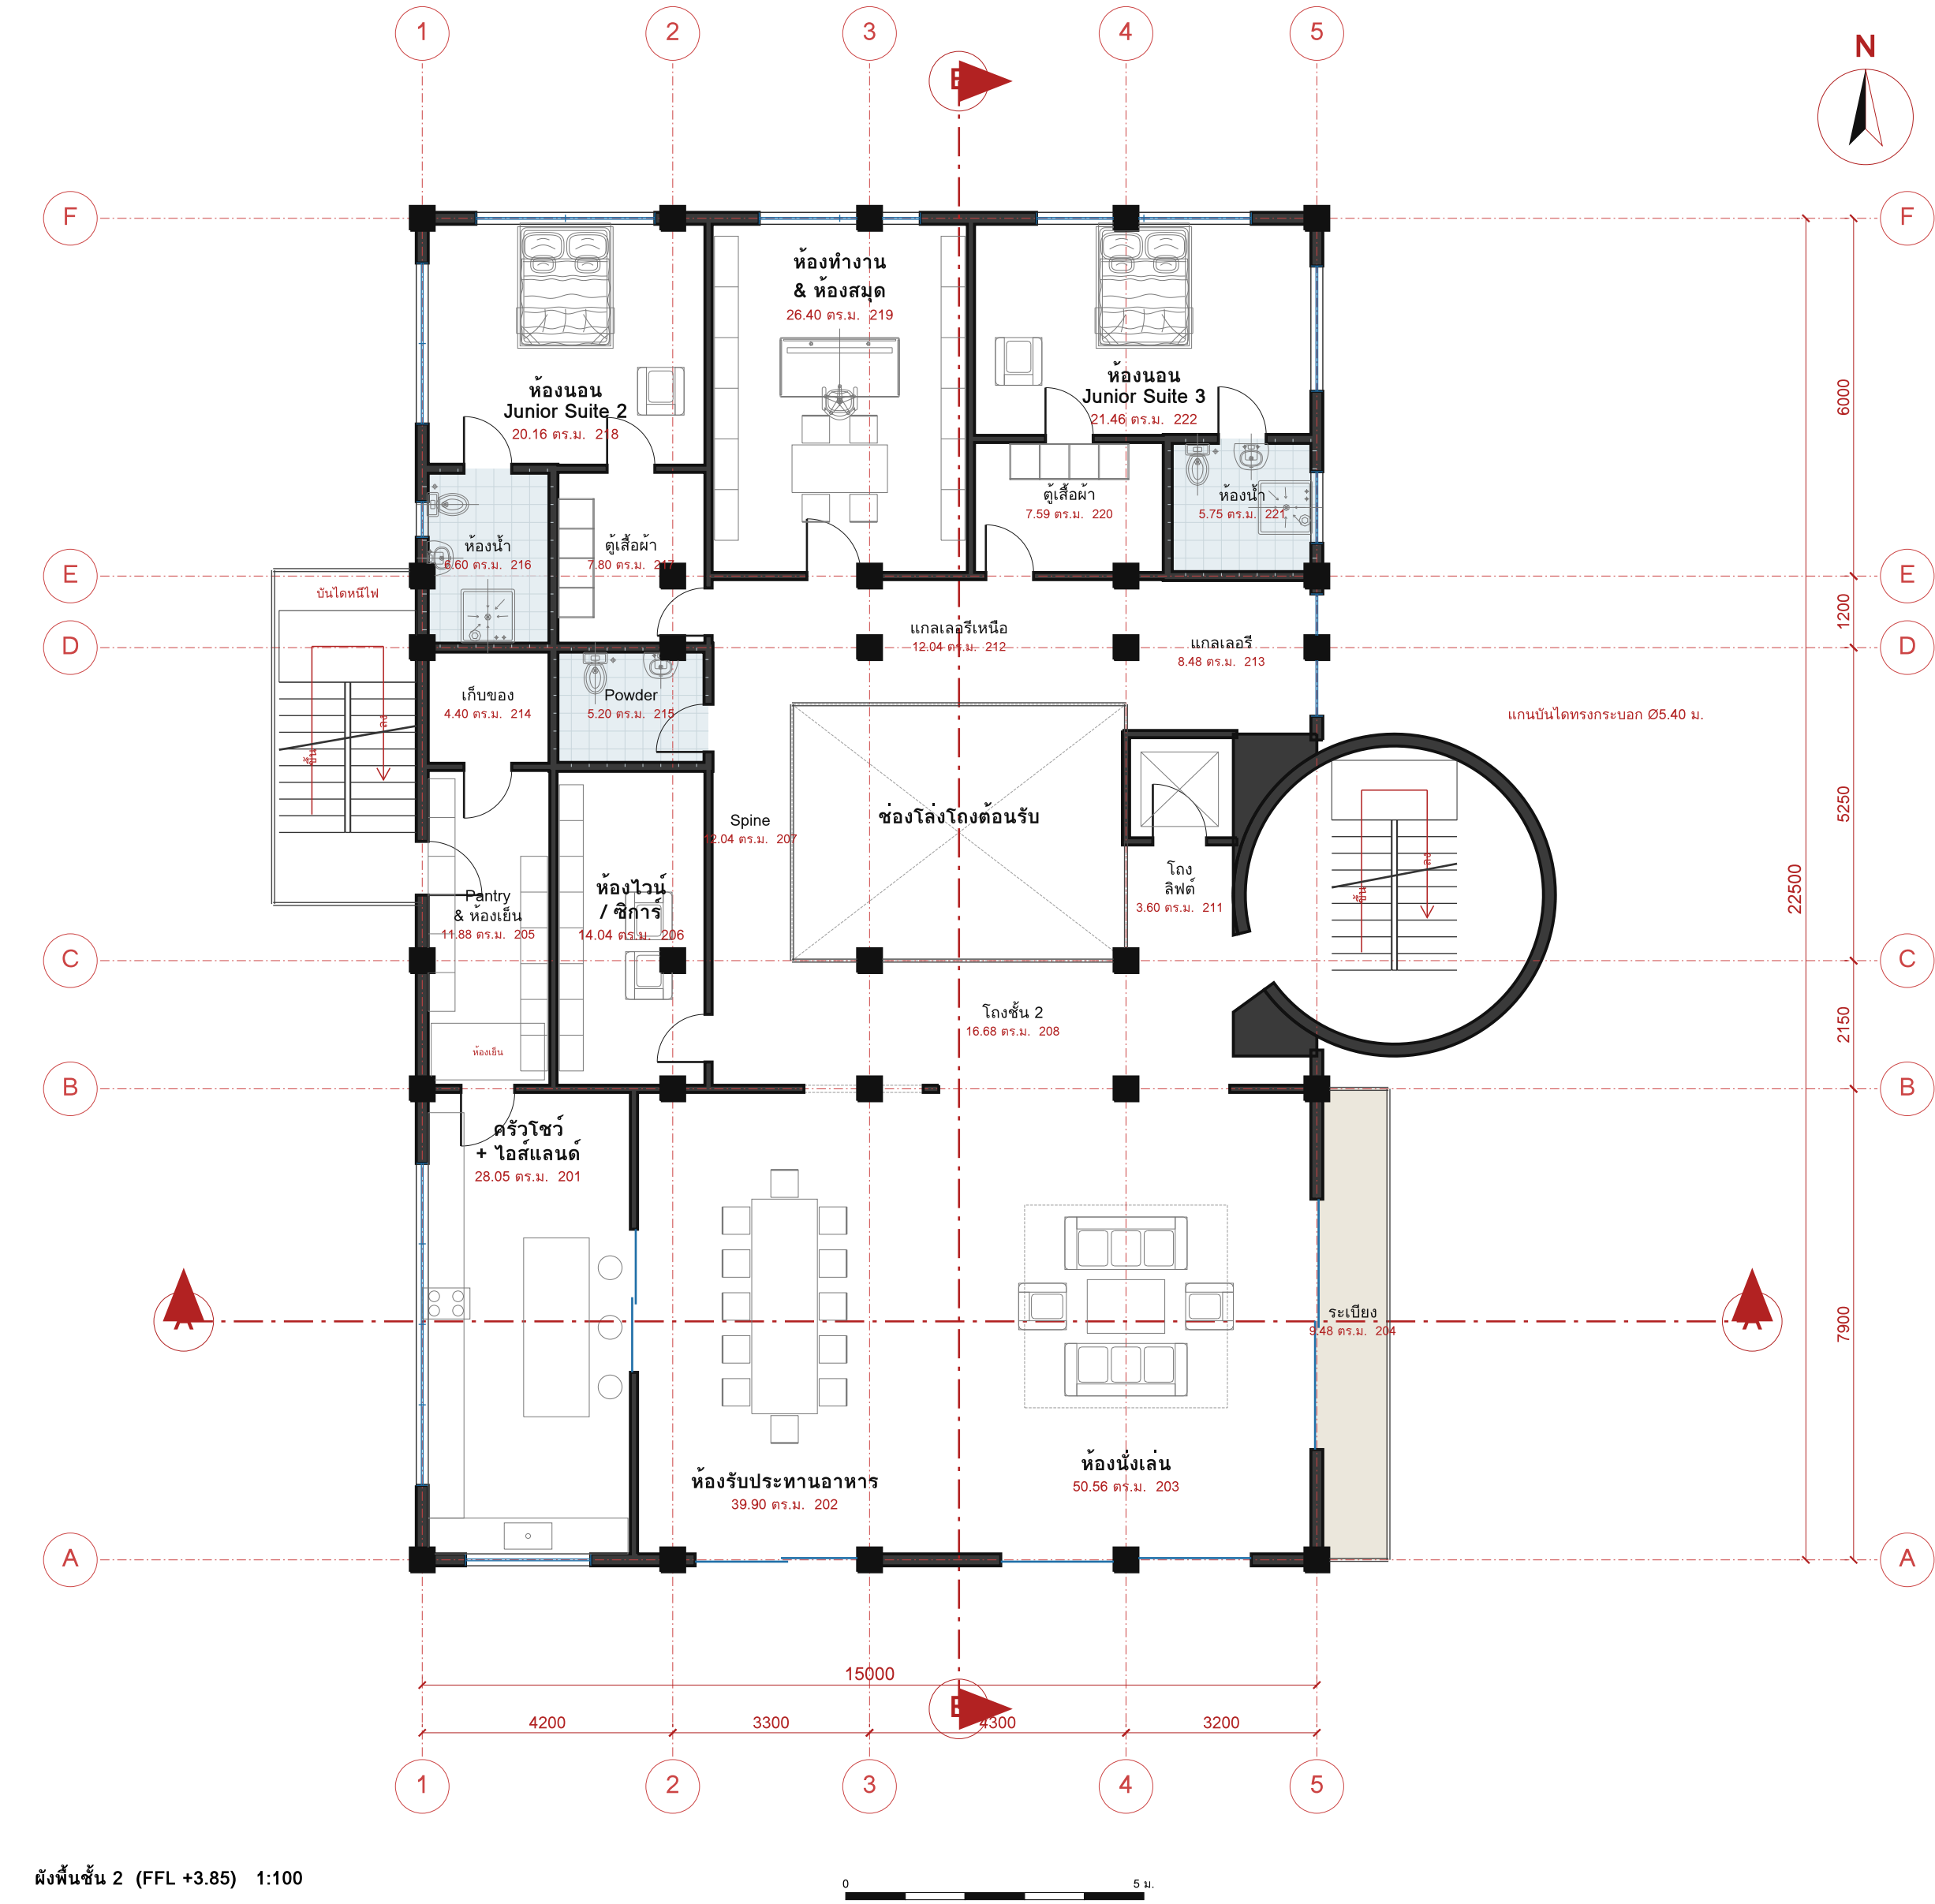

ตารางห้อง ชั้น 2			
รหัส	ห้อง	ขนาด ม.	ตร.ม. ประเภท
201	ครัวโชว์ + ไอส์แลนด์	3.55 x 7.90	28.05 ห้องใช้งาน
202	ห้องรับประทานอาหาร	5.05 x 7.90	39.90 ห้องใช้งาน
203	ห้องนั่งเล่น	6.40 x 7.90	50.56 ห้องใช้งาน
204	ระเบียงหน้าออก ชั้น 2	1.20 x 7.90	9.48 ภายนอก
205	Walk-in Pantry & ห้องเย็น	2.20 x 5.40	11.88 บริการ
206	ห้องโถง / ซิงก์	2.60 x 5.40	14.04 บริการ
207	ทางเดินแกน (Spine)	1.40 x 8.60	12.04 บริการ
208	โถงชั้น 2	7.40 x 2.15	16.68 บริการ
210	ช่องลิฟต์โถงต้อนรับ	5.60 x 4.30	24.08 ช่องลิฟต์
211	โถงลิฟต์ชั้น 2	1.80 x 2.00	3.60 บริการ
212	แกลเลอรีเหนือ	5.60 x 2.15	12.04 บริการ
213	แกลเลอรีหน้าออก	3.20 x 2.65	8.48 บริการ
214	ห้องเก็บของ (ต่อจาก Pantry)	2.20 x 2.00	4.40 บริการ
215	ห้องน้ำเย็น (Powder)	2.60 x 2.00	5.20 ห้องนั่งเียก
216	ห้องน้ำ Junior Suite 2	2.20 x 3.00	6.60 ห้องนั่งเียก
217	ตู้เสื้อผ้า Junior Suite 2	2.60 x 3.00	7.80 บริการ
218	ห้องนอน Junior Suite 2	4.80 x 4.20	20.16 ห้องใช้งาน
219	ห้องทำงาน & ห้องสมุด	4.40 x 6.00	26.40 ห้องใช้งาน
220	ตู้เสื้อผ้า Junior Suite 3	3.30 x 2.30	7.59 บริการ
221	ห้อง Junior Suite 3	2.50 x 2.30	5.75 ห้องนั่งเียก
222	ห้องนอน Junior Suite 3	5.80 x 3.70	21.46 ห้องใช้งาน
223	แกนบันไดทรงกระบอก	Ø 5.40	22.90 แกนบันได
224	ลิฟต์บ้าน	1.80 x 1.80	3.24 ลิฟต์
225	บันไดหนีไฟภายนอก	2.50 x 5.60	14.00 บันไดหนีไฟ

ตารางชั้น 2		ตร.ม.
พื้นที่อาคาร (รวมแกน)		328.76
ที่ภายนอก		9.48
จอดรถ		0.00
รวม		338.24
บันไดหนีไฟภายนอก (ไม่รวม)		14.00

- หมายเหตุ
- ส่วนรวมเรียกตามที่ดิน: ครัวโชว์ -> ห้องอาหาร -> ห้องนั่งเล่น -> ระเบียงหน้าออก 1.20 ม. (มองสระ)
 - Pantry ย้ายจากชั้น 3 (โปรแกรม) มาติดครัวโชว์ + ห้องเก็บของ: ห้องโถงซิงก์ / ไม่มีหน้าต่าง (ตั้งใจ ควบคุมอุณหภูมิ)
 - ช่องลิฟต์โถงต้อนรับ รวกรวจากช่อง 1.10 ม.; Gallery ติดเหนือ-ตะวันออก
 - Junior Suite 2-3 และห้องทำงานอยู่ใต้ห้องคานา +7.25 ที่เหนือ (ช่องแสงหลังคา 2 ชุดเหนือห้องทำงาน)
 - ทางหนีไฟชั้น 2: Pantry -> บันไดหนีไฟภายนอกทิศตะวันตก

H3A DESIGN AND BUILD

X-UNIT Architecture Lab

โครงการ

WELL-GBEACH 30x30

Executive Luxury Villa

บ้านเดี่ยว 4 ชั้น ผ่านเกณฑ์

WELL for Residential (เจดนา)

ที่ดิน 30.00 x 30.00 ม. = 225 ตร.ว.
ถนนสาธารณะที่ดิน (สมมติ 8.00 ม.)

แนวคิด

จาก G-Beach Residence (B+D+M):
แห่ง 15.00 x 22.50 ม. บนเสาทราย
+ แกนบันไดทรงกระบอกอิฐ Ø5.40
+ ผนังอิฐโปร่งทิศตะวันตก

ระดับ

±0.00 ถนน · F1 +0.45 · F2 +3.85
F3 +7.25 · F4 +10.65
หลังคา +14.05 · parapet +14.65
ยอดทรงกระบอก +14.85

หมายเหตุ

- หน่วยงานเป็นนิติบุคคล เว้นแต่ระบุ
- ระดับอ้างอิงถนนหน้าที่ดิน ±0.00
- ห้ามวัดขนาดจากถนน ใช้ตัวเลขกำกับ
- แบบระดับ Design Development
- ต้องให้สถาปนิกและวิศวกรผู้ได้รับใบอนุญาตตรวจสอบและลงนามก่อนยื่นขออนุญาต

ผังพื้นที่ชั้น 2 (FFL +3.85) 1:100


0 5 ม.

ชื่อแผ่น

ผังพื้นที่ชั้น 2
(FFL +3.85)

มาตราส่วน 1:100

วันที่ 6 ค.ศ. 2569 ฉบับ v1 / DD

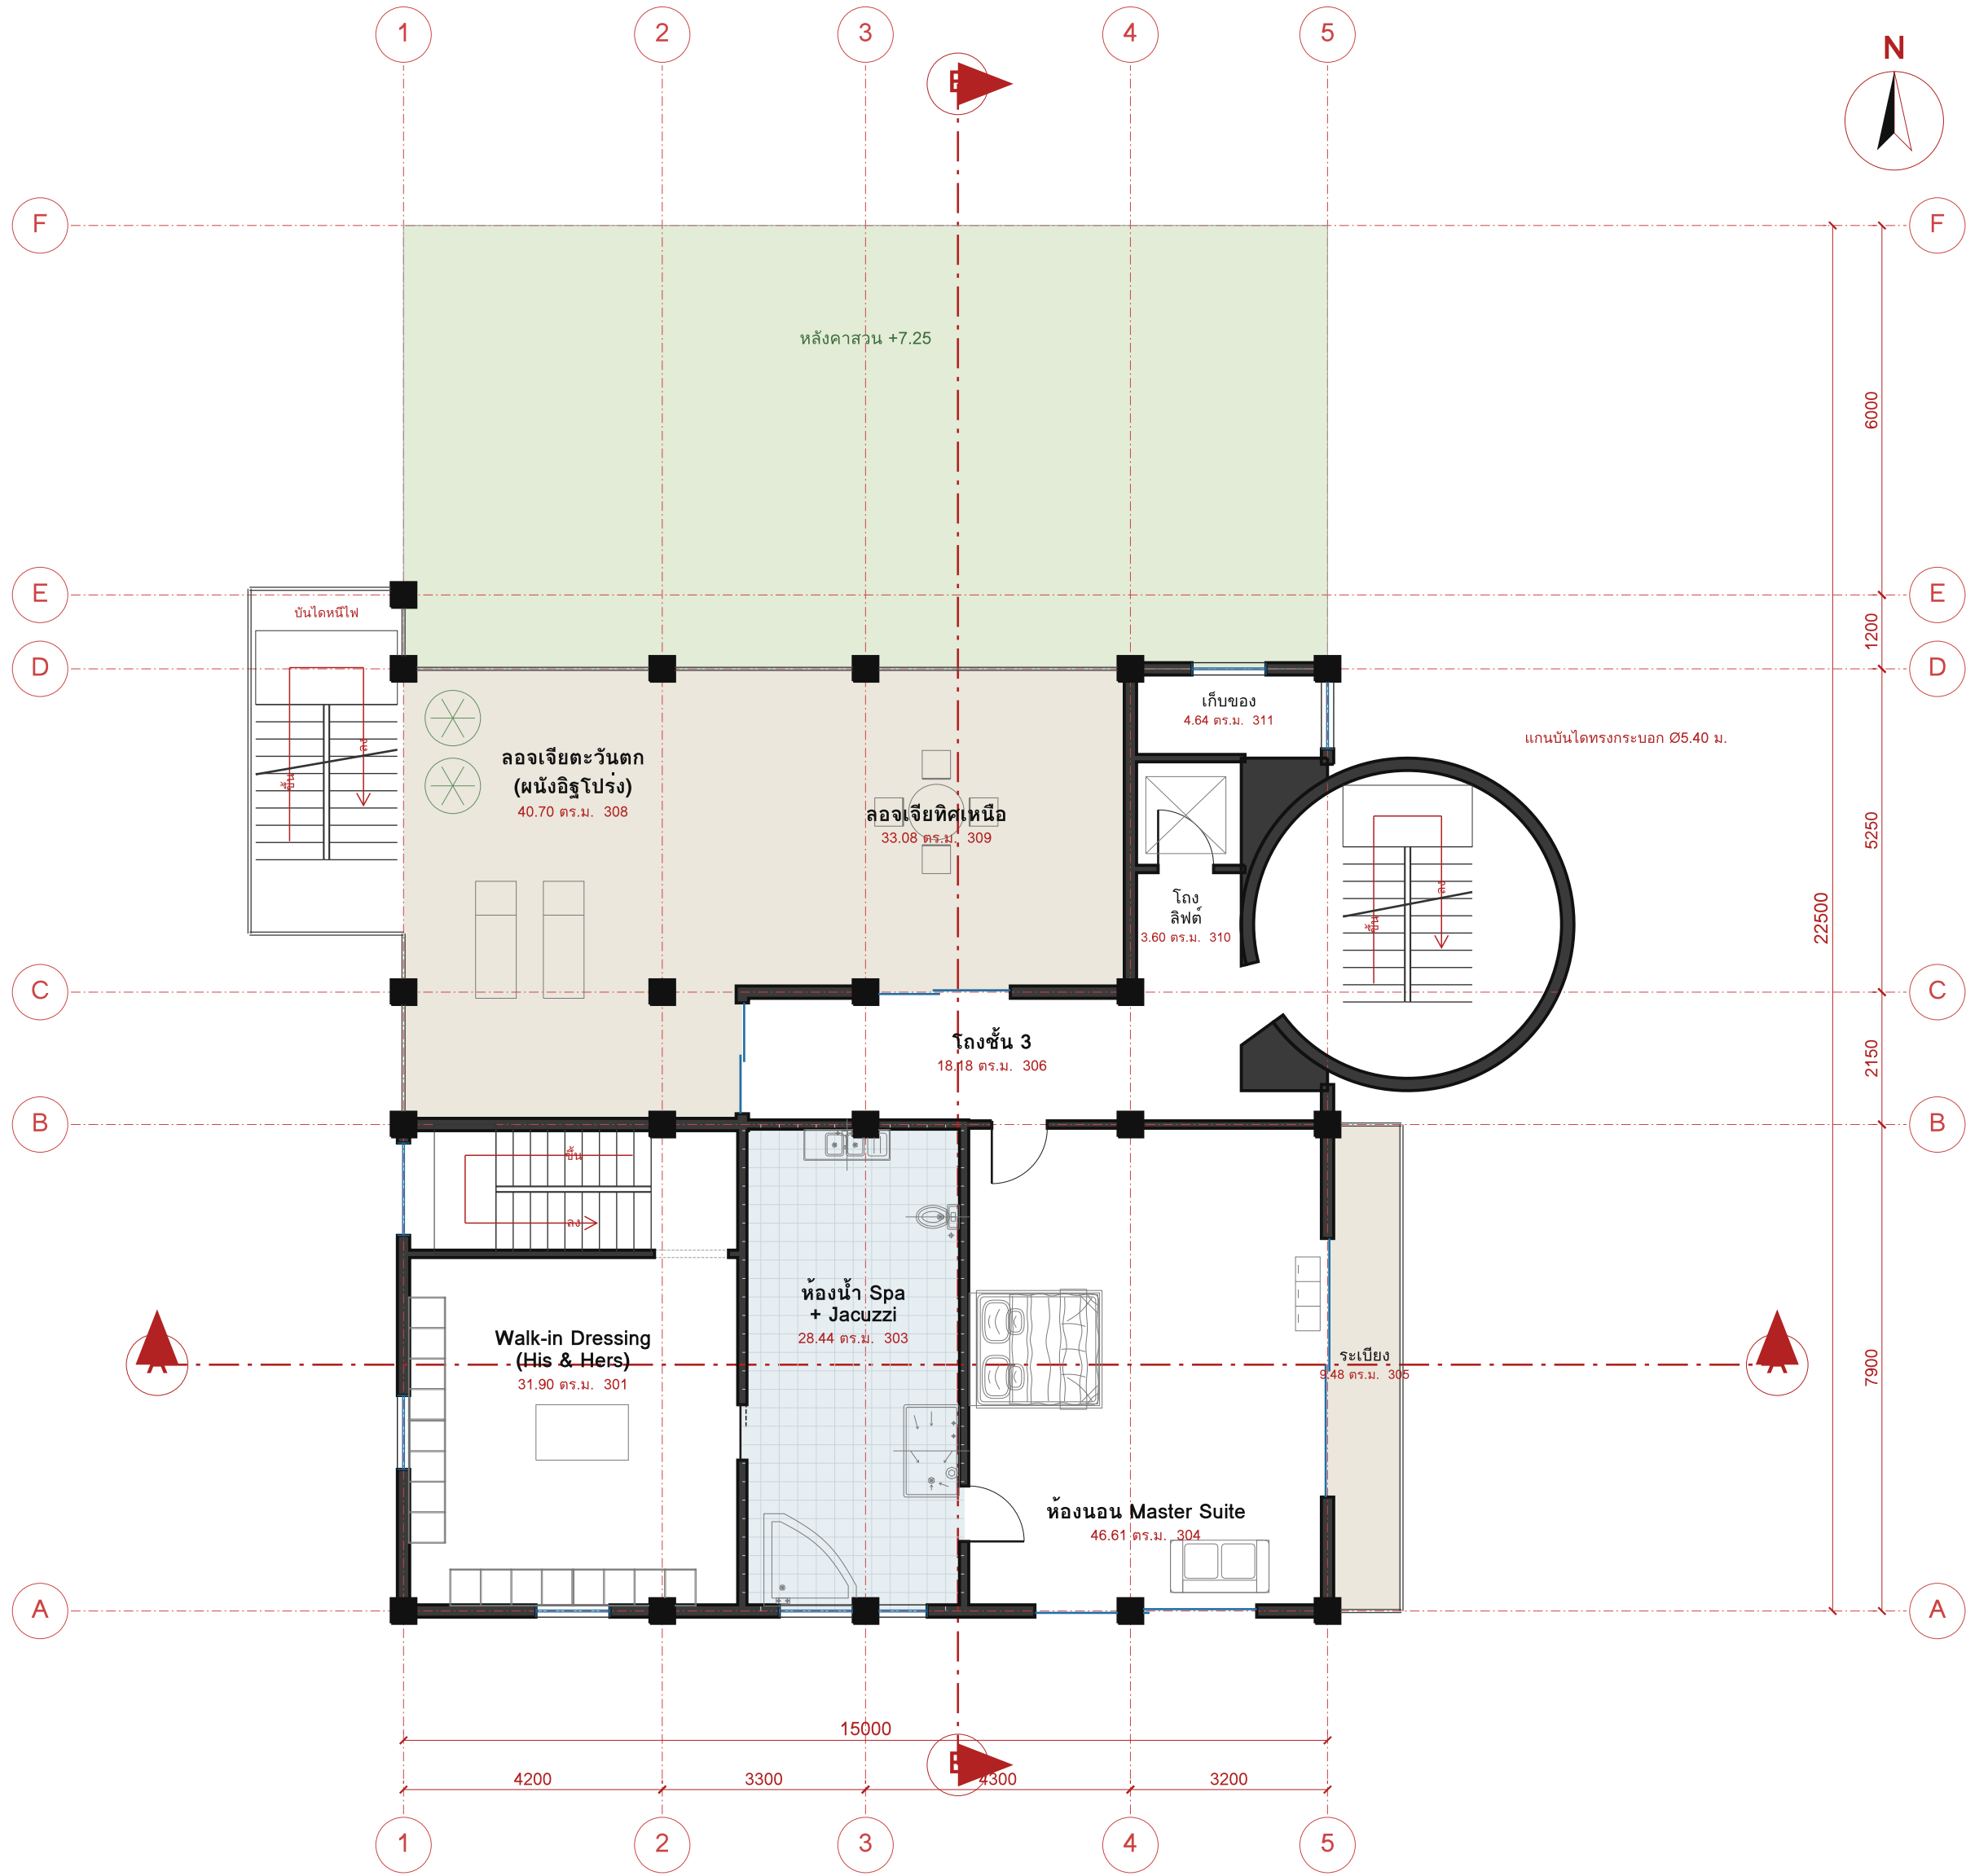

ผังพื้นชั้น 3 (FFL +7.25) 1:100

ตารางห้อง ชั้น 3

รหัส	ห้อง	ขนาด ม.	ตร.ม.	ประเภท
301	Walk-in Dressing (His & Hers)	5.50 x 5.80	31.90	บริการ
302	บันไดส่วนครัว Master	5.50 x 2.10	11.55	บันได
303	ห้องน้ำ Spa + Jacuzzi	3.60 x 7.90	28.44	ห้องน้ำ/สปา
304	ห้องนอน Master Suite	5.90 x 7.90	46.61	ห้องนอน
305	ระเบียงหน้าห้อง ชั้น 3	1.20 x 7.90	9.48	ที่ภายนอก
306	โถงชั้น 3	8.10 x 2.15	18.18	สัญจร
308	ห้องเจียตวันตก (ผนังอิฐโปร่ง)	5.50 x 7.40	40.70	ที่ภายนอก
309	ห้องเจียตวันตก	6.30 x 5.25	33.08	ที่ภายนอก
310	โถงลิฟต์ชั้น 3	1.80 x 2.00	3.60	สัญจร
311	ห้องเก็บของชั้น 3	3.20 x 1.45	4.64	บริการ
312	แกนบันไดทรงกระบอก	Ø 5.40	22.90	แกนบันได
313	ลิฟต์บ้าน	1.80 x 1.80	3.24	ลิฟต์
314	บันไดหนีไฟภายนอก	2.50 x 5.60	14.00	บันไดหนีไฟ

ฐานชั้น 3	ตร.ม.
พื้นที่ปิดล้อม (รวมแกน)	171.07
ที่ภายนอก	83.26
จอดรถ	0.00
รวม	254.32
บันไดหนีไฟภายนอก (ไม่รวม)	14.00

หมายเหตุ

- ชั้นส่วนครัว Master: Walk-in -> ห้องน้ำ Spa + Jacuzzi -> ห้องนอน Master -> ระเบียงหน้าห้อง
- บันไดส่วนครัว Master (ชั้น 3-4) ขึ้นสู่ Closet และระเบียงหน้าห้อง (Master duplex ตามที่เลือก)
- Loggia หินกระบอก (หลังผนังอิฐโปร่ง) และ Loggia หินกระบอก = ชั้นที่กั้นภายนอกบนหลังคาส่วนชั้น 2
- หลังคาส่วน +7.25 หนี Junior Suite/ห้องทำงาน หินกระบอก

H3A DESIGN AND BUILD

X-UNIT Architecture Lab

โครงการ

WELL-GBEACH 30x30

Executive Luxury Villa

บ้านเดี่ยว 4 ชั้น ผ่านเกณฑ์

WELL for Residential (เจดนา)

ที่ดิน 30.00 x 30.00 ม. = 225 ตร.ว.
ถนนสาธารณะหินกระบอก (สมมติ 8.00 ม.)

แนวคิด

จาก G-Beach Residence (B+D+M):
แห่ง 15.00 x 22.50 ม. บนเสาลอย
+ แกนบันไดทรงกระบอก Ø5.40
+ ผนังอิฐโปร่งหินกระบอก

ระดับ

±0.00 ถนน * F1 +0.45 * F2 +3.85
F3 +7.25 * F4 +10.65
หลังคา +14.05 * parapet +14.65
ยอดทรงกระบอก +14.85

หมายเหตุ


- หน่วยเป็นมิลลิเมตร เว้นแต่ระบุ
- ระดับอ้างอิงถนนหน้าที่ดิน ±0.00
- ห้ามวัดขนาดจากแบบ ใช้ตัวเลขกำกับ
- แบบระดับ Design Development
- ต้องให้สถาปนิกและวิศวกรผู้ได้รับใบอนุญาตตรวจสอบและลงนามก่อนยื่นขออนุญาต

ชื่อแผ่น

ผังพื้นชั้น 3
(FFL +7.25)

มาตราส่วน 1:100

วันที่ 6 ต.ค. 2569 ฉบับ v1 / DD

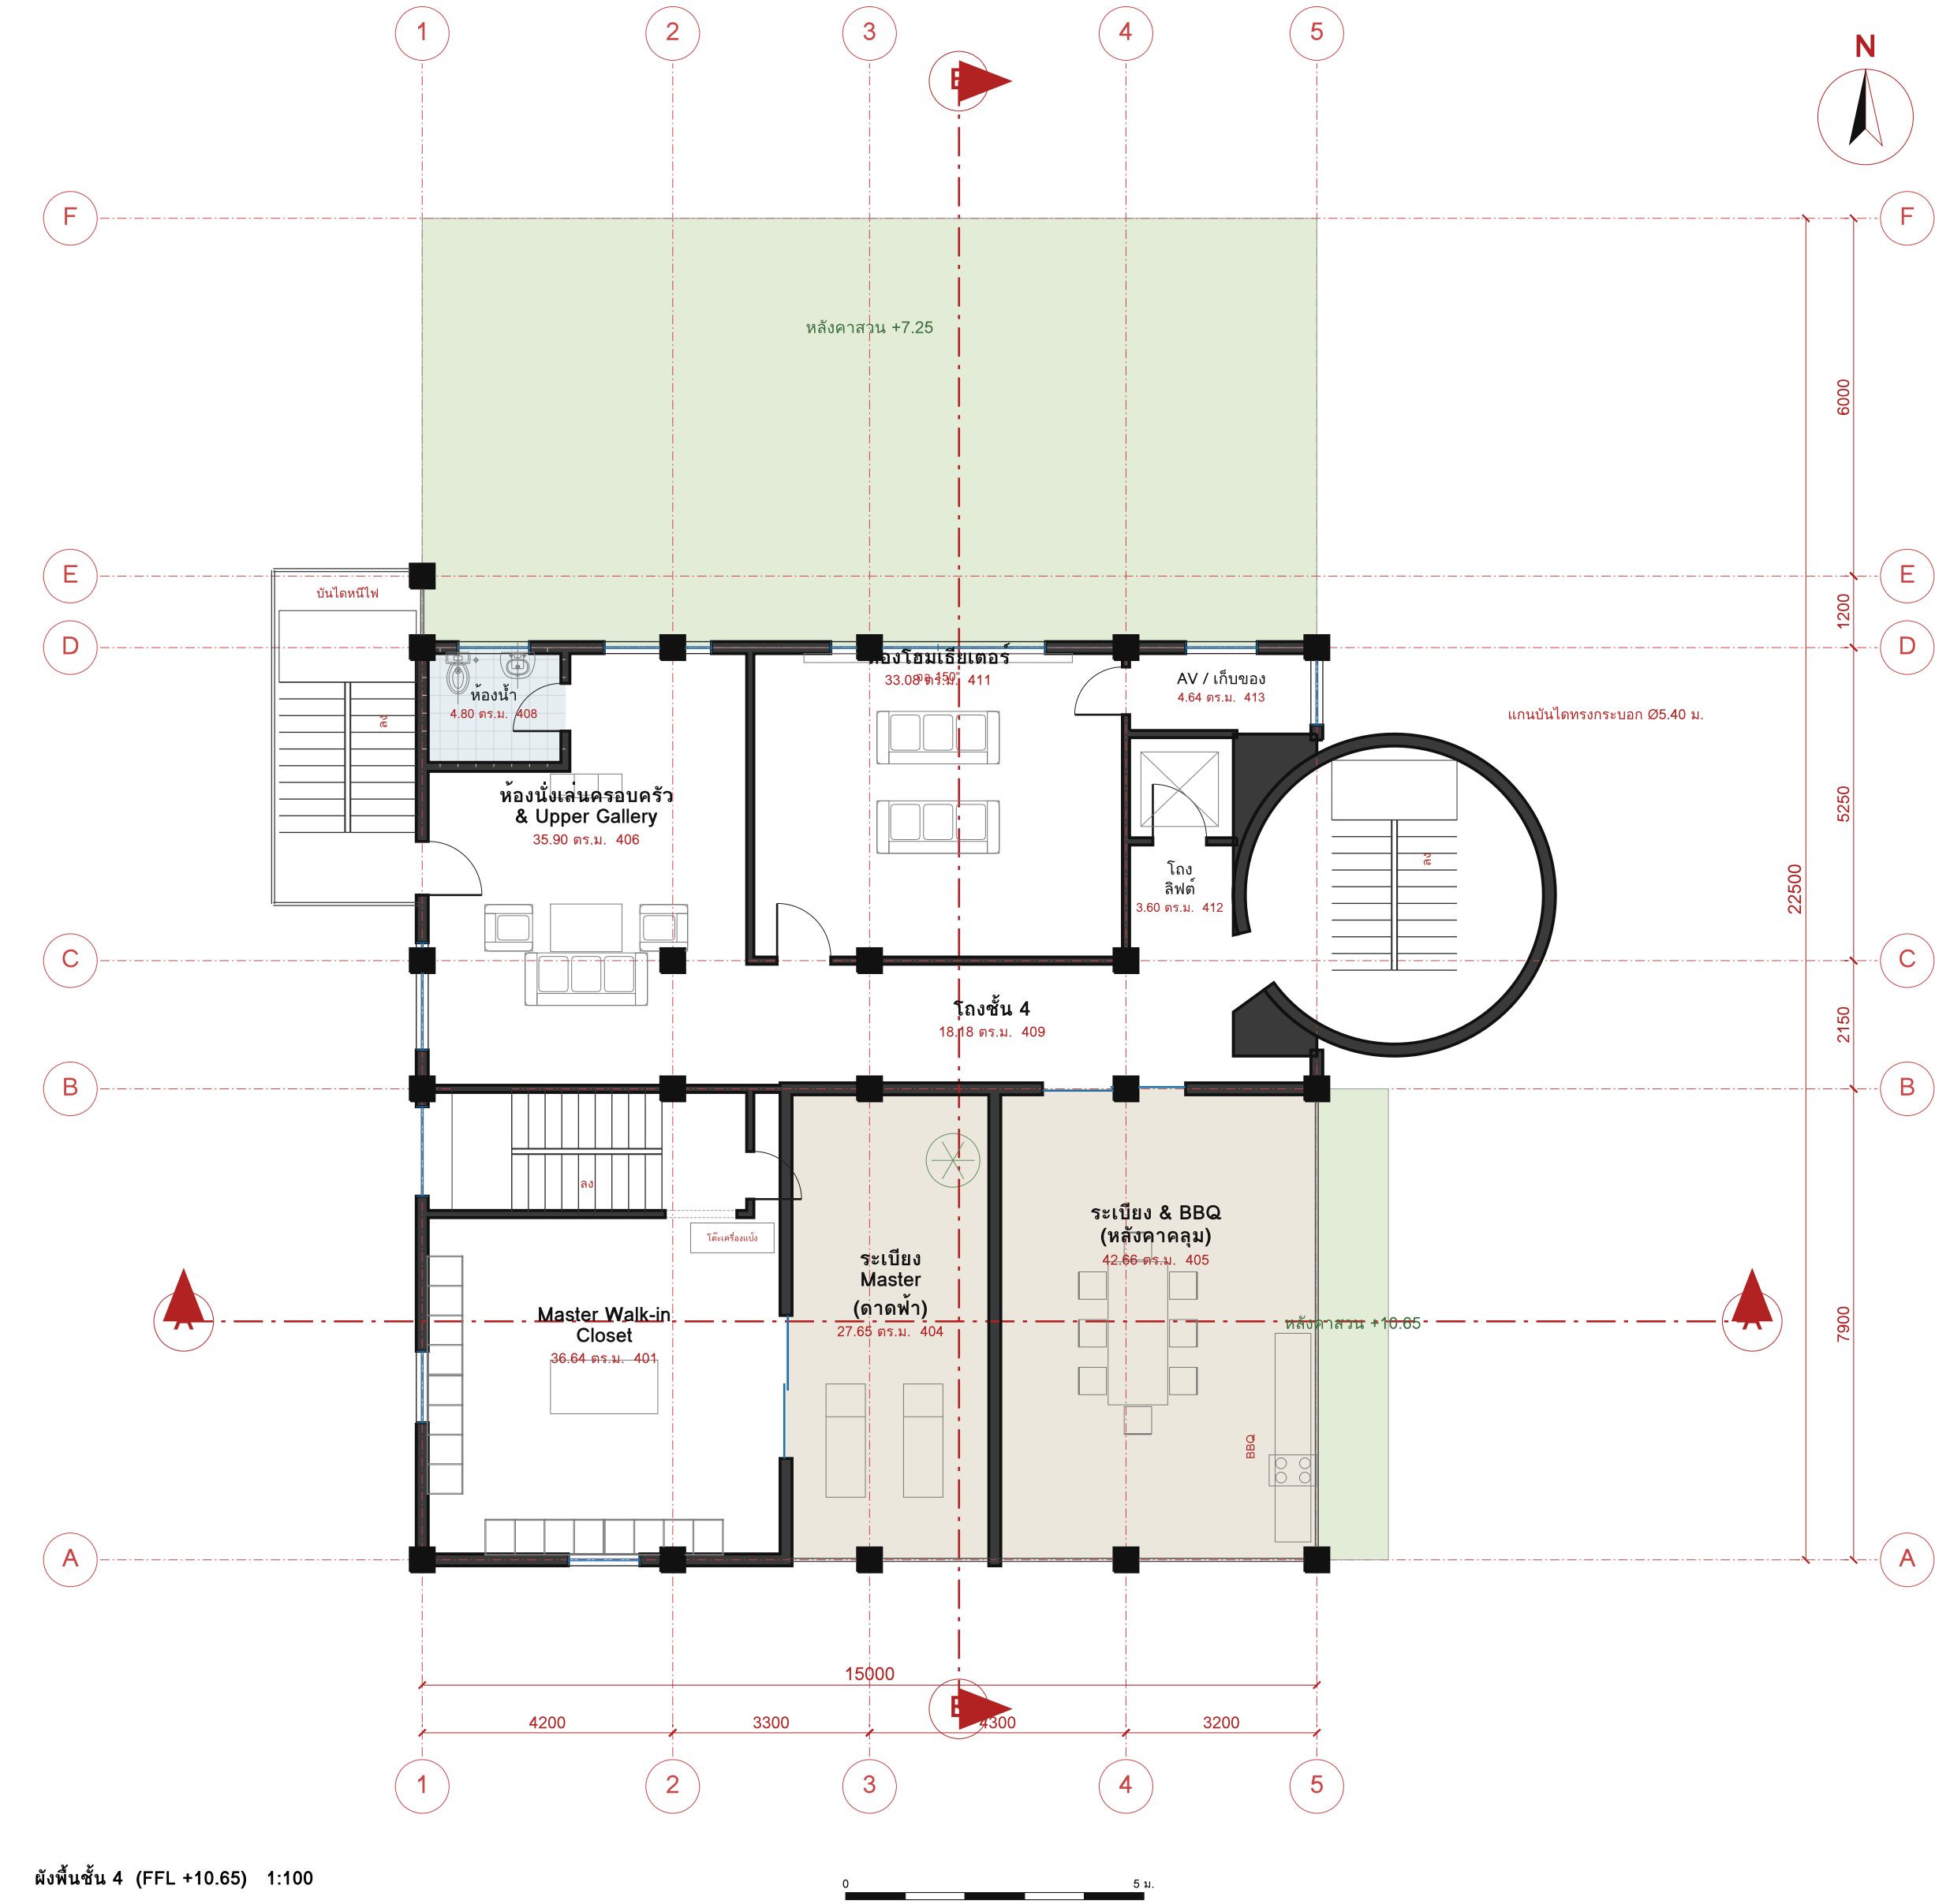

ผังพื้นชั้น 4 (FFL +10.65) 1:100

ตารางห้อง ชั้น 4

รหัส	ห้อง	ขนาด ม.	ตร.ม.	ประเภท
401	Master Walk-in Closet ชั้น 4	6.10 x 5.80	36.64	บริการ
403	บันไดส่วนตัว Master	5.50 x 2.10	11.55	บันได
404	ระเบียง Master (คาเฟ่)	3.50 x 7.90	27.65	ที่ภายนอก
405	ระเบียง & BBQ (หลังคาคลุม)	5.40 x 7.90	42.66	ที่ภายนอก
406	ห้องนั่งเล่นครอบครัว & Upper Galle	5.50 x 5.40	35.90	ห้องใช้งาน
408	ห้องนี้ชั้น 4	2.40 x 2.00	4.80	ห้องน้ำ
409	โรงชั้น 4	8.10 x 2.15	18.18	โรงรถ
411	ห้องโถงเชื่อมต่อ	6.30 x 5.25	33.08	ห้องใช้งาน
412	โรงสัฟต์ชั้น 4	1.80 x 2.00	3.60	โรงรถ
413	ห้องอุปกรณ์ AV / เก็บของ	3.20 x 1.45	4.64	บริการ
414	แกนบันไดทรงกระบอกรั	Ø 5.40	22.90	แกนบันได
415	ลิฟต์บ้าน	1.80 x 1.80	3.24	ลิฟต์
416	บันไดหนีไฟภายนอก	2.50 x 5.60	14.00	บันไดหนีไฟ

ฐานชั้น 4	ตร.ม.
พื้นที่ปิดล้อม (รวมแกน)	174.53
ที่ภายนอก	70.31
จอดรถ	0.00
รวม	244.84
บันไดหนีไฟภายนอก (ไม่รวม)	14.00

หมายเหตุ

- Master Walk-in Closet (W.I.C.) คือบันไดส่วนตัว และระเบียง Master เบื้องหน้า (pergola)
- ระเบียง & BBQ หลังคาคลุม 5.40 x 7.90 ม. จัดได้-ระบันนอก มอสร (คาเฟ่ "360°" สีจาก G-Beach)
- ห้องนั่งเล่นครอบครัว & Gallery ดีไซน์นอก หลังนั่งดูไปโรง : ห้องโถงเชื่อมต่อทิศเหนือ หน้าต่าง 3.60 ม. + ม่านทับ
- หลังคา +14.05 เทนชัน 4: แนวโซลาร์ 47 แผง = 25.65 kWp

H3A DESIGN AND BUILD

X-UNIT Architecture Lab

โครงการ

WELL-GBEACH 30x30

Executive Luxury Villa

บ้านเดี่ยว 4 ชั้น ผ่านเกณฑ์

WELL for Residential (เจดนา)

ที่ดิน 30.00 x 30.00 ม. = 225 ตร.ว.
ถนนสาธารณะทิศเหนือ (สมมติ 8.00 ม.)

แนวคิด

จาก G-Beach Residence (B+D+M):
แห่ง 15.00 x 22.50 ม. บนเสาโลย
+ แกนบันไดทรงกระบอกรั Ø5.40
+ ผนังดูโปร่งทิศระบันก

ระดับ

±0.00 ถนน * F1 +0.45 * F2 +3.85
F3 +7.25 * F4 +10.65
หลังคา +14.05 * parapet +14.65
ยอดทรงกระบอกรั +14.85

หมายเหตุ


- หน่วยเป็นมิลลิเมตร เว้นแต่ระบุ
- ระดับอ้างอิงถนนหน้าที่ดิน ±0.00
- ห้ามวัดขนาดจากแบบ ใช้ตัวเลขกำกับ
- แบบระดับ Design Development
- ต้องให้สถาปนิกและวิศวกรผู้ได้รับใบอนุญาตตรวจสอบและลงนามก่อนยื่นขออนุญาต

ชื่อแผ่น

ผังพื้นชั้น 4
(FFL +10.65)

มาตราส่วน 1:100

วันที่ 6 ต.ค. 2569 ฉบับ v1 / DD

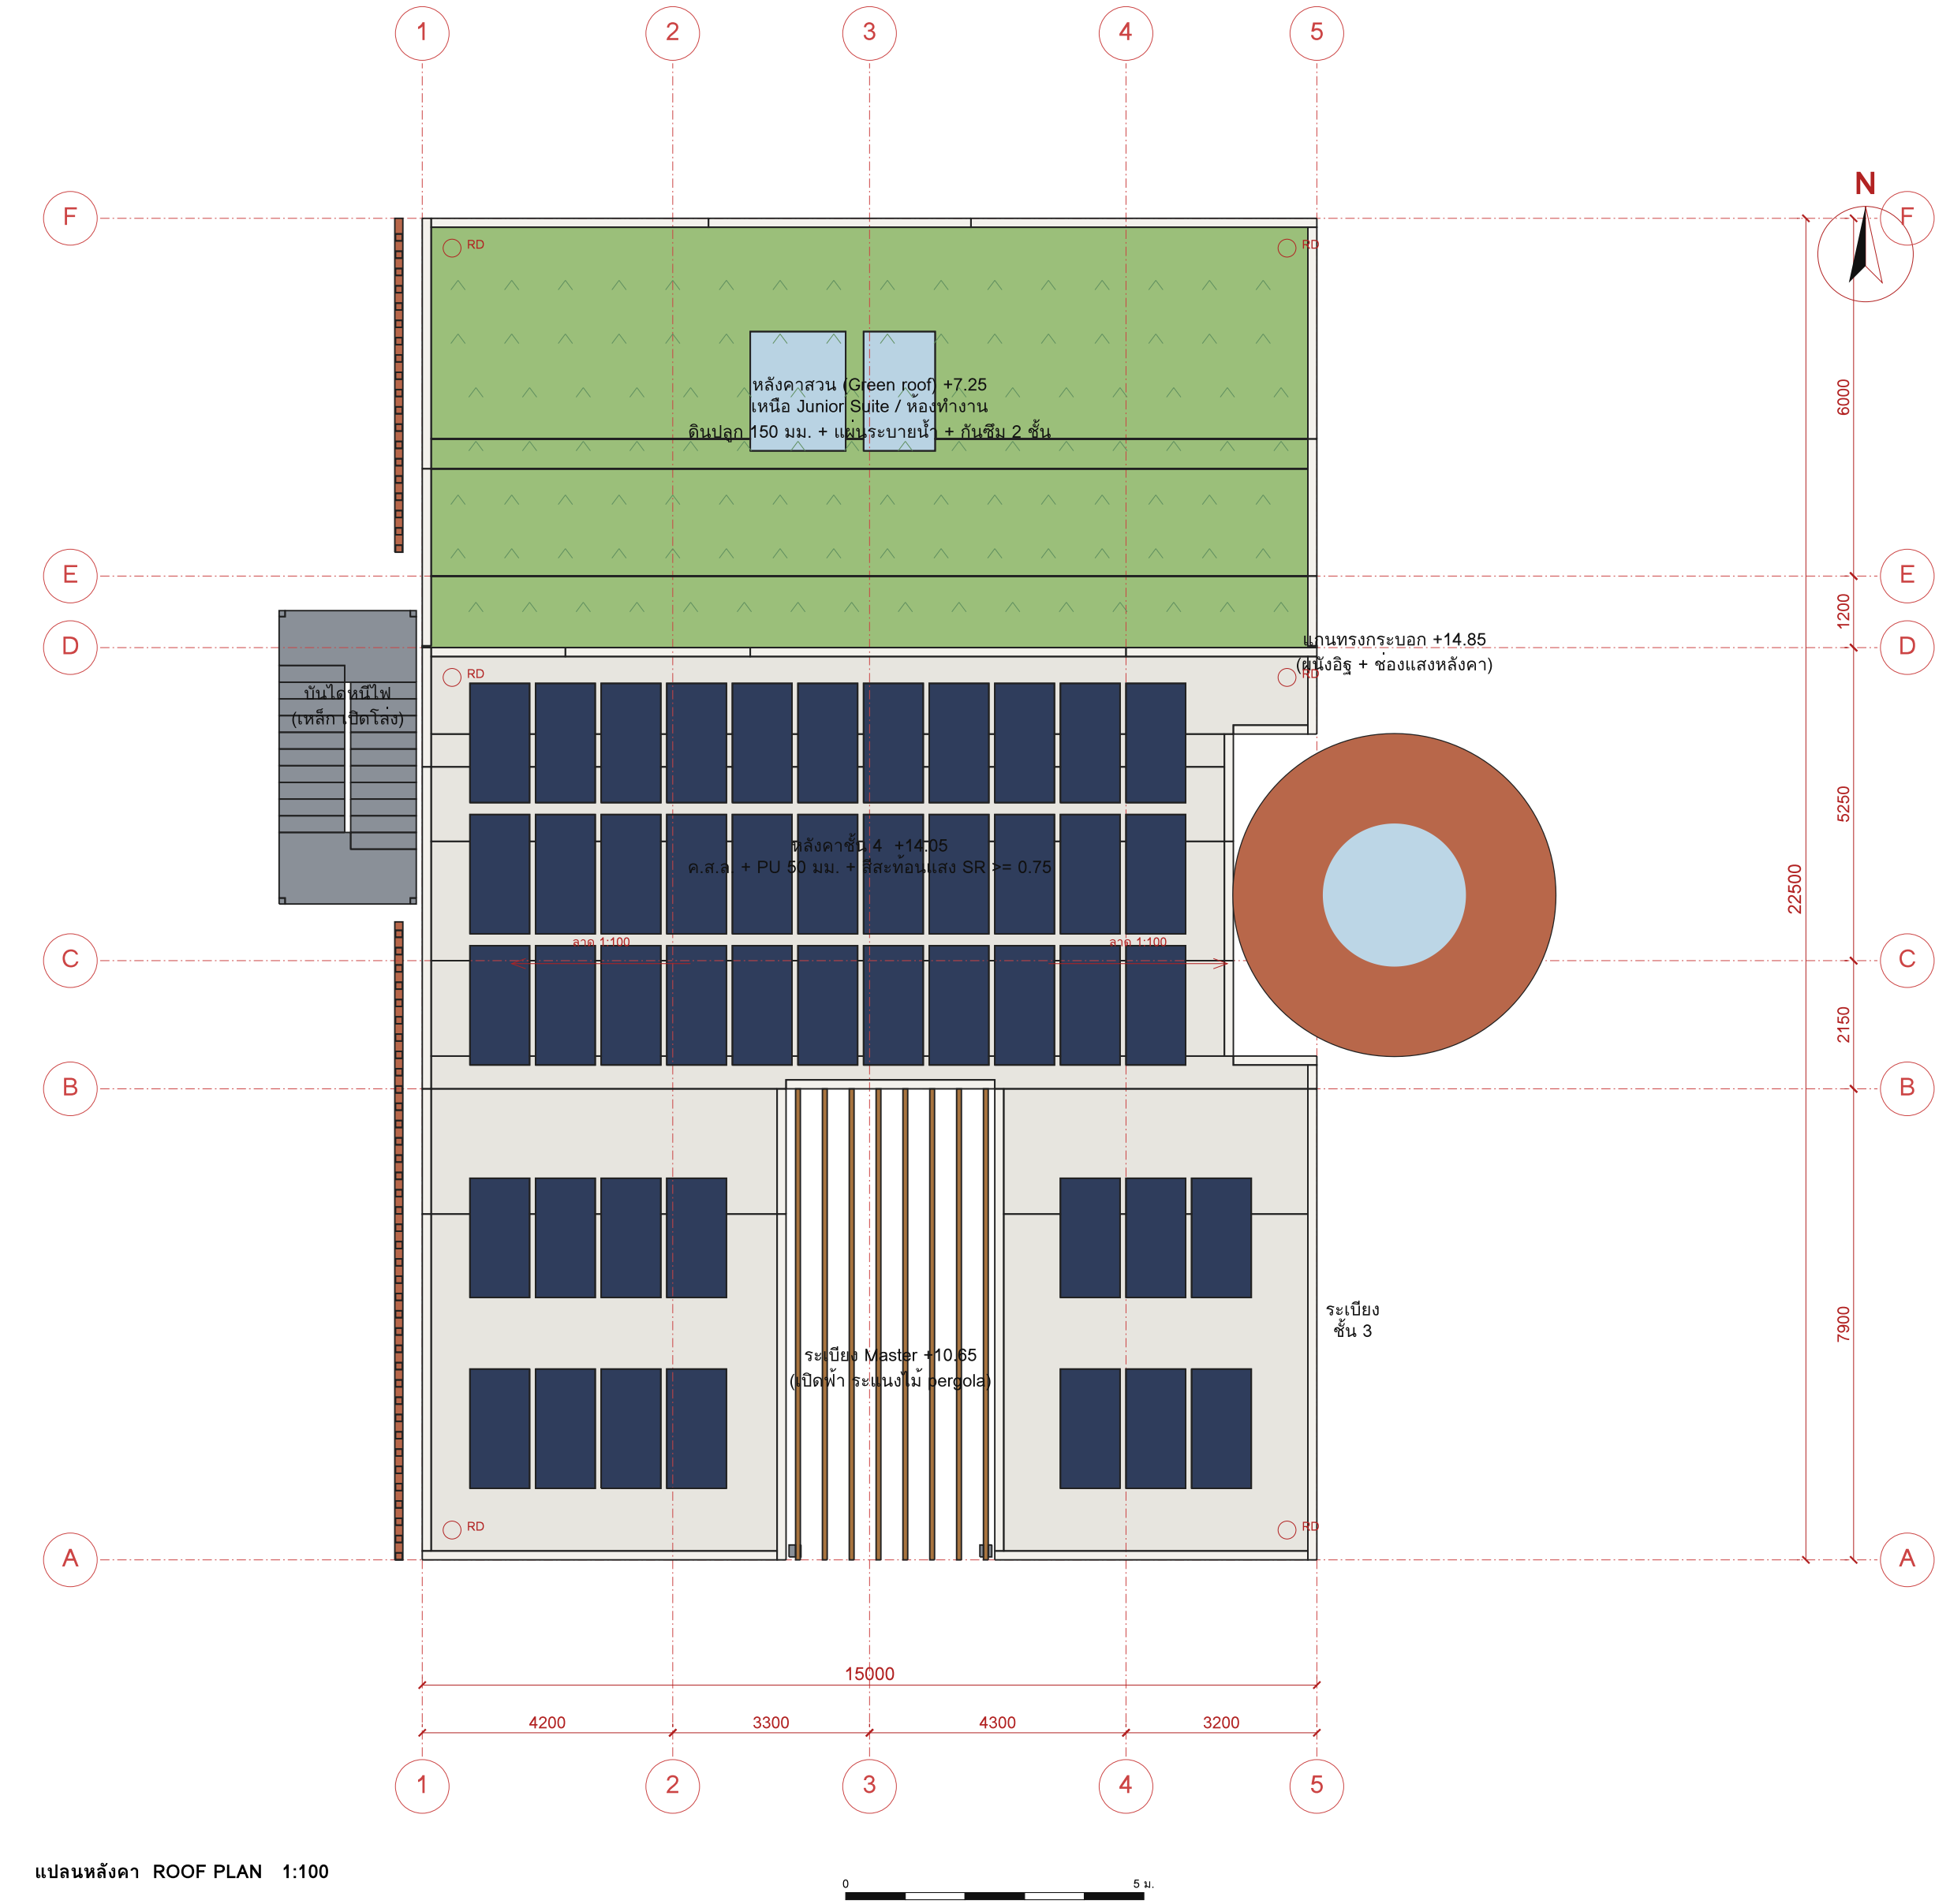

แปลนหลังคา ROOF PLAN 1:100

พื้นที่หลังคา

หลังคา	ค่า
หลังคาส่วน +7.25 (เหนือชั้น 2 คีตเหนือ)	108.00
หลังคาหลัก +14.05 (ค.ส.ล. ขาว SR)	194.29
รวม	302.29
สัดส่วนหลังคาเขียว	36%

น้ำฝน และพลังงาน

รายการ	ค่า
สมร่ายปีกรงหยา (ประมาณ)	~1,500 ลบ.ม./ปี
น้ำฝนเก็บได้ (เฉลี่ย C=0.9, ส่วน C=0.4)	327 ลบ.ม./ปี
ถังเก็บน้ำฝนใต้ดิน 2.50 x 2.50 ม.	~12 ลบ.ม. (รดน้ำ/ซักโถ)
แผงโซลาร์ 47 x 550 Wp	25.85 kWp ~ 32,300 kWh/ปี*
หลอดทรงกระบอก Ø5.30 ม.	ช่องแสงทรงจอก Ø5.30 ม.

ชั้นหลังคา

- หลังคาส่วน: ซีเมนต์ดิน + ดินปลูก 150 มม. + แผ่นโกลรอง + แผ่นระบายน้ำ 20 มม. + แผ่นกันราก + กันซึม 2 ชั้น + ค.ส.ล. ลาด 1:100
- หลังคาหลัก: สีสะท้อนแสง SR >= 0.75 + PU foam 50 มม. + กันซึม + ค.ส.ล. 200
- ระเบียง Master ชั้น 4 (เปิดฟ้า): พื้นไม้เทียมบนขาตั้ง + pergola; ระเบียง BBQ: หลังคา ค.ส.ล. ดูน
- Parapet สูง 0.60 ม.
- RD = ทุกระบายน้ำฝน ลงรางระบายน้ำ -> ถึงน้ำฝน
- * พลังงาน PV ประมาณ -1,250 kWh/kWp ปี — ต้องคำนวณจกรวมแสงทรงกระบอก/pergola

H3A DESIGN AND BUILD

X-UNIT Architecture Lab

โครงการ

WELL-GBEACH 30x30

Executive Luxury Villa
บ้านเดี่ยว 4 ชั้น ผ่านเกณฑ์
WELL for Residential (เจดนา)

ที่ดิน 30.00 x 30.00 ม. = 225 ตร.ว.
ถนนสาธารณะคี่เหนือ (สมมติ 8.00 ม.)

แนวคิด

จาก G-Beach Residence (B+D+M):
แท่ง 15.00 x 22.50 ม. บนเสาโลย
+ แกนบันไดทรงกระบอกอิฐ Ø5.40
+ ผนังอิฐโปร่งทิศตะวันตก

ระดับ

±0.00 ถนน · F1 +0.45 · F2 +3.85
F3 +7.25 · F4 +10.65
หลังคา +14.05 · parapet +14.65
ยอดทรงกระบอก +14.85

หมายเหตุ

- หน่วยเป็นมิลลิเมตร เว้นแต่ระบุ
- ระดับอ้างอิงถนนหน้าที่ดิน ±0.00
- ห้ามวัดขนาดจากแบบ ใช้ตัวเลขกำกับ
- แบบระดับ Design Development
- ต้องให้สถาปนิกและวิศวกรผู้ได้รับใบอนุญาตตรวจสอบและลงนามก่อนยื่นขออนุญาต


ชื่อแผ่น

แปลนหลังคา

มาตรฐาน 1:100

วันที่ 6 ต.ค. 2569 ฉบับ v1 / DD

รูปด้านทิศใต้ (สวน/ใต้ถุน) 1:100

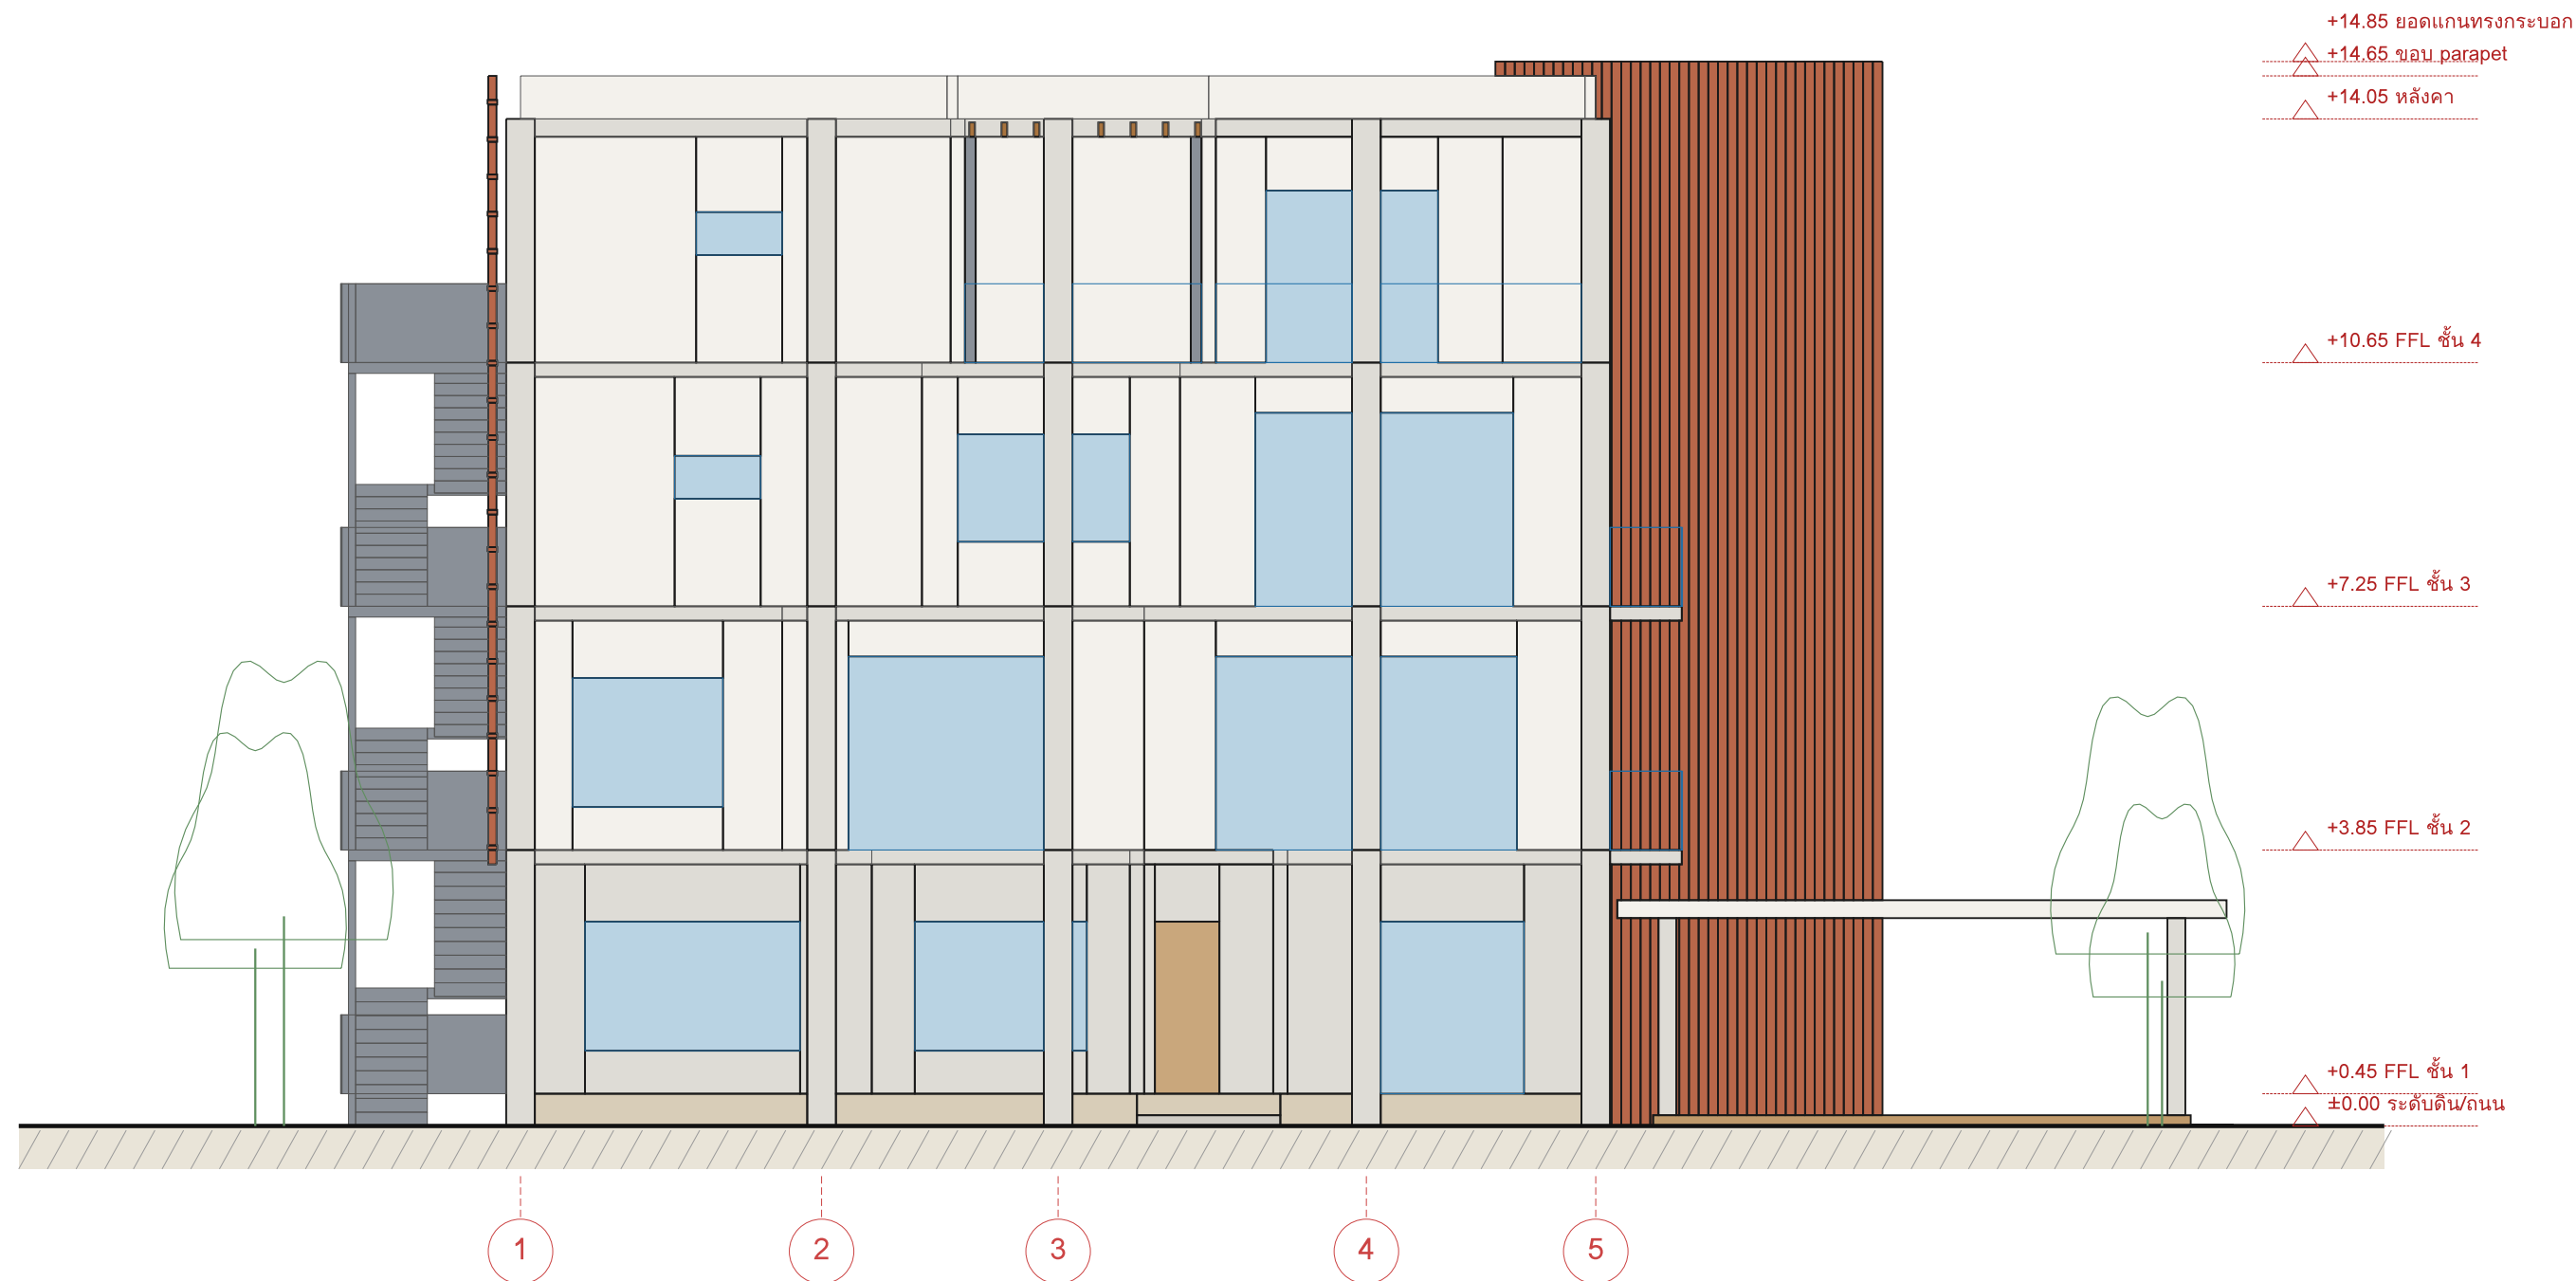

รูปด้านทิศเหนือ (ด้านถนน) 1:100



- วัสดุผิว (ระบอบแนวติด)
 - ผนังภายนอก: ฉาบเรียบสีขาว (render) บนบล็อกมวลเบา 200
 - กระจกบานนอก: อีกรูปร่างแนว สี่เหลี่ยม (brick) + ช่องแสงขอบ
 - ผนังอีกรูปร่าง: ครีมน้ำย 115 @290 + แลบนอน @520 บนโครงเหล็กกวางไนซ์
 - เหล็กฉาก ค.ส.ล. 0.40 x 0.40 ผิวฉาบกริดเปลี่ยน
 - กระจก Low-E laminated กระจกอะลูมิเนียมสีเทาเข้ม
 - ราวกันตกกระจกสูง 1.10 ม.
 - บันไดหนีไฟ: เหล็กกวางไนซ์ขาวสี ราว 1.10 ม.
 - แฉงโซลารัมบนหลังคา +14.05 (มองไม่เห็นอาคารติดกัน)

X-UNIT Architecture Lab

โครงการ

Executive Luxury Villa
บ้านเดี่ยว 4 ชั้น ผ่านเกณฑ์
WELL for Residential (เจตนา)

ที่ดิน 30.00 x 30.00 ม. = 225 ตร.ว.
ถนนสาธารณะทิศเหนือ (สมบัติ 8.00 ม.)

แนวคิด

จาก G-Beach Residence (B+D+M):
 แท่ง 15.00 x 22.50 ม. บนเสาหล่อ
 + แกนบันไดทรงกระบอกอิฐ Ø5.40
 + ผนังอิฐโปรงทิศตะวันตก

ระดับ

±0.00 ถนน · F1 +0.45 · F2 +3.85
F3 +7.25 · F4 +10.65
หลังคา +14.05 · parapet +14.65
ยอดทรงกระบอก +14.85

หมายเหตุ

- หน่วยงานเป็นนิติบุคคล เว้นแต่ระบุ
- ระดับอ้างอิงถนนหน้าที่ดิน ± 0.00
- ห้ามวัดขนาดจากแบบ ใช้ตัวเลขกำกับ
- แบบระดับ Design Development
ต้องให้สถาปนิกและวิศวกรผู้ได้รับ
ใบอนุญาตตรวจสอบและลงนาม
ก่อนยื่นขออนุญาต

ชื่อแผ่น


รูปด้านทิศใต้
+ รูปด้านทิศเหนือ

มาตราส่วน 1:100

วันที่ 6 ต.ค. 2569 ฉบับ v1 / DD

A-08

รูปด้านทิศตะวันตก (ผนังอิฐโปรง/บันไดหนีไฟ) 1:100

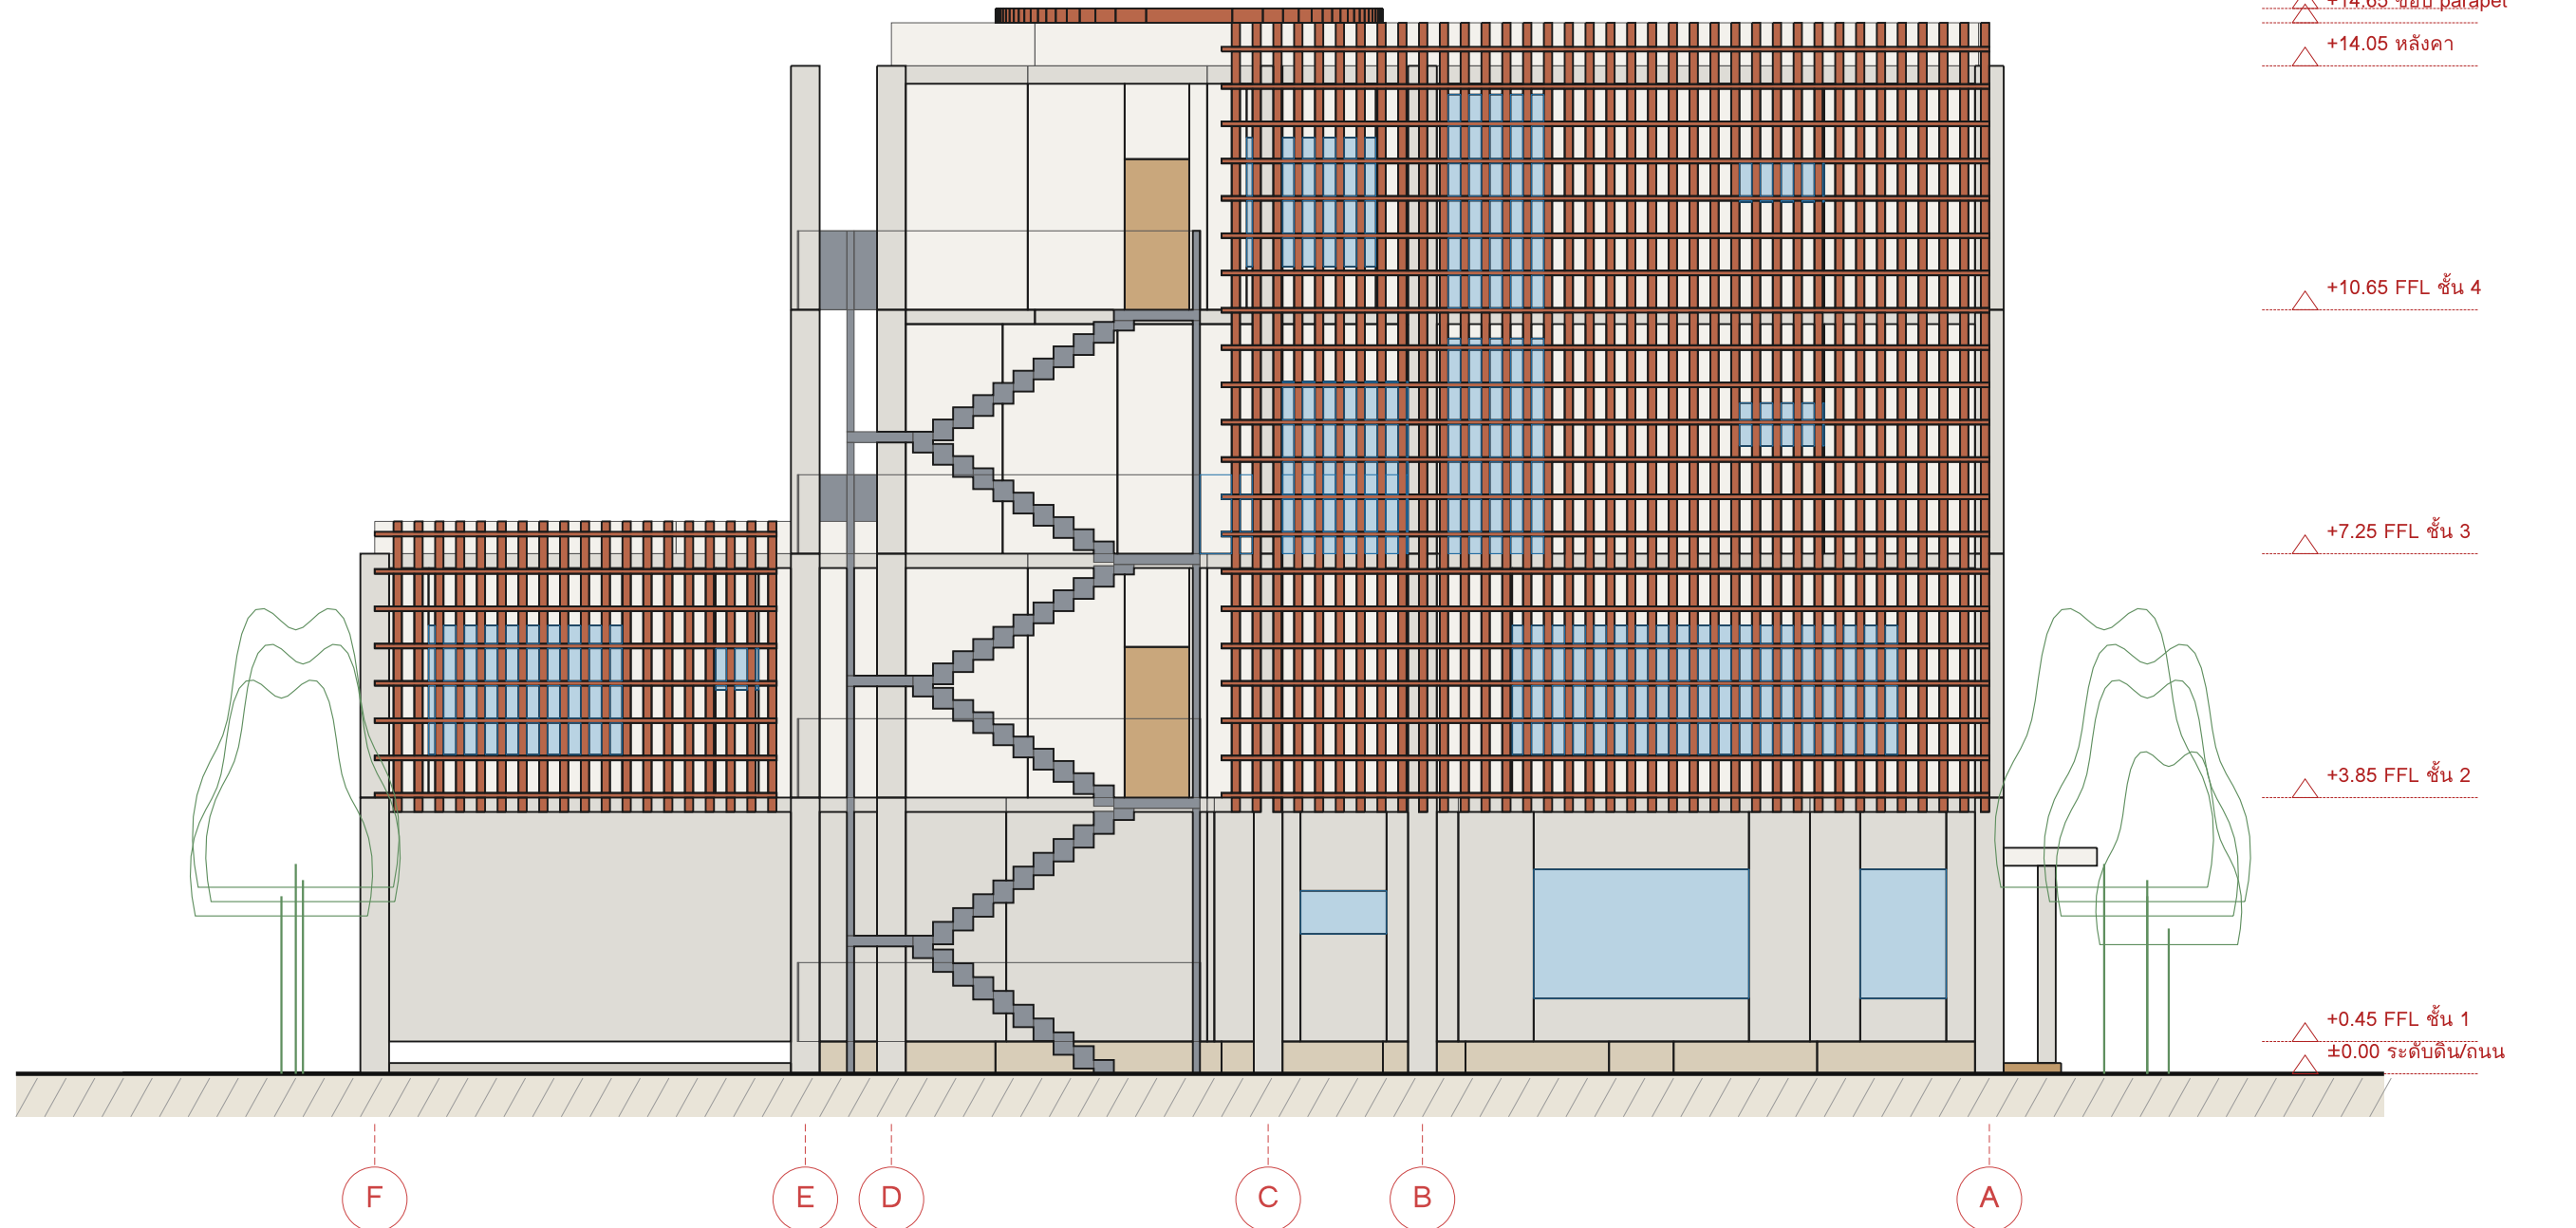

- ผนังภายนอก: ฉาบเรียบสีขาว (render) บนบล็อกมวลเบา 200
- โครงกระดูก: อิฐโชว์แนว สีส้มอิฐ (brick) + ช่องลมแยก
- ผนังอิฐโปร่ง: สกรีนอิฐ 115 @290 + แถบขนน @520 บนโครงเหล็กกลาไร้สนิม
เสาอก ค.ส.ล. 0.40 x 0.40 ครอบบนกริดเบส
- กระเบื้อง Low-E laminated กระจกอะลูมิเนียมสีฟ้าเข้ม
- ราวกันตกกระจกสูง 1.10 ม.
- ปันโดหน้าไฟ: เหล็กกลาไร้สนิม 1.10 ม.
- แสงโซลาร์บนหลังคา +14.05 (มองไปในการดับถนน)

X-UNIT Architecture Lab

โครงการ

Executive Luxury Villa
บ้านเดี่ยว 4 ชั้น ผ่านเกณฑ์
WELL for Residential (เจตนา)

ที่ดิน 30.00 x 30.00 ม. = 225 ตร.ว.
ถนนสาธารณะทิศเหนือ (สมบัติ 8.00 ม.)

แนวคิด

จาก G-Beach Residence (B+D+M):
 แท่ง 15.00 x 22.50 ม. บนเสาหล่อ
 + แกนบันไดทรงกระบอกอิฐ Ø5.40
 + ผนังอิฐโปรงหิวดะวันตก

ระดับ

±0.00 ถนน · F1 +0.45 · F2 +3.85
F3 +7.25 · F4 +10.65
หลังคา +14.05 · parapet +14.65
ยอดทรงกระบอก +14.85

หมายเหตุ

- หน่วยงานเป็นนิติบุคคล เว้นแต่ระบุ
- ระดับอ้างอิงถนนหน้าที่ดิน ± 0.00
- ห้ามวัดขนาดจากแบบ ใช้ตัวเลขกำกับ
- แบบระดับ Design Development
- ต้องให้สถาปนิกและวิศวกรผู้ได้รับใบอนุญาตตรวจสอบและลงนามก่อนยื่นขออนุญาต

ชื่อแผ่น


รูปด้านทิศตะวันออก
+ รูปด้านทิศตะวันตก

มาตราส่วน 1:100

วันที่ 6 ต.ค. 2569 ฉบับ v1 / DD



รูปตัด B-B (ตัดแนวเหนือ-ใต้ ผ่านใต้ถุน Pilotis-โถงต้อนรับสูง 2 ชั้น-โรงรถ / ห้องนั่งเล่น-ห้องทำงาน มองไปทิศตะวันออก เห็นแกนทรงกระบอก) 1:100

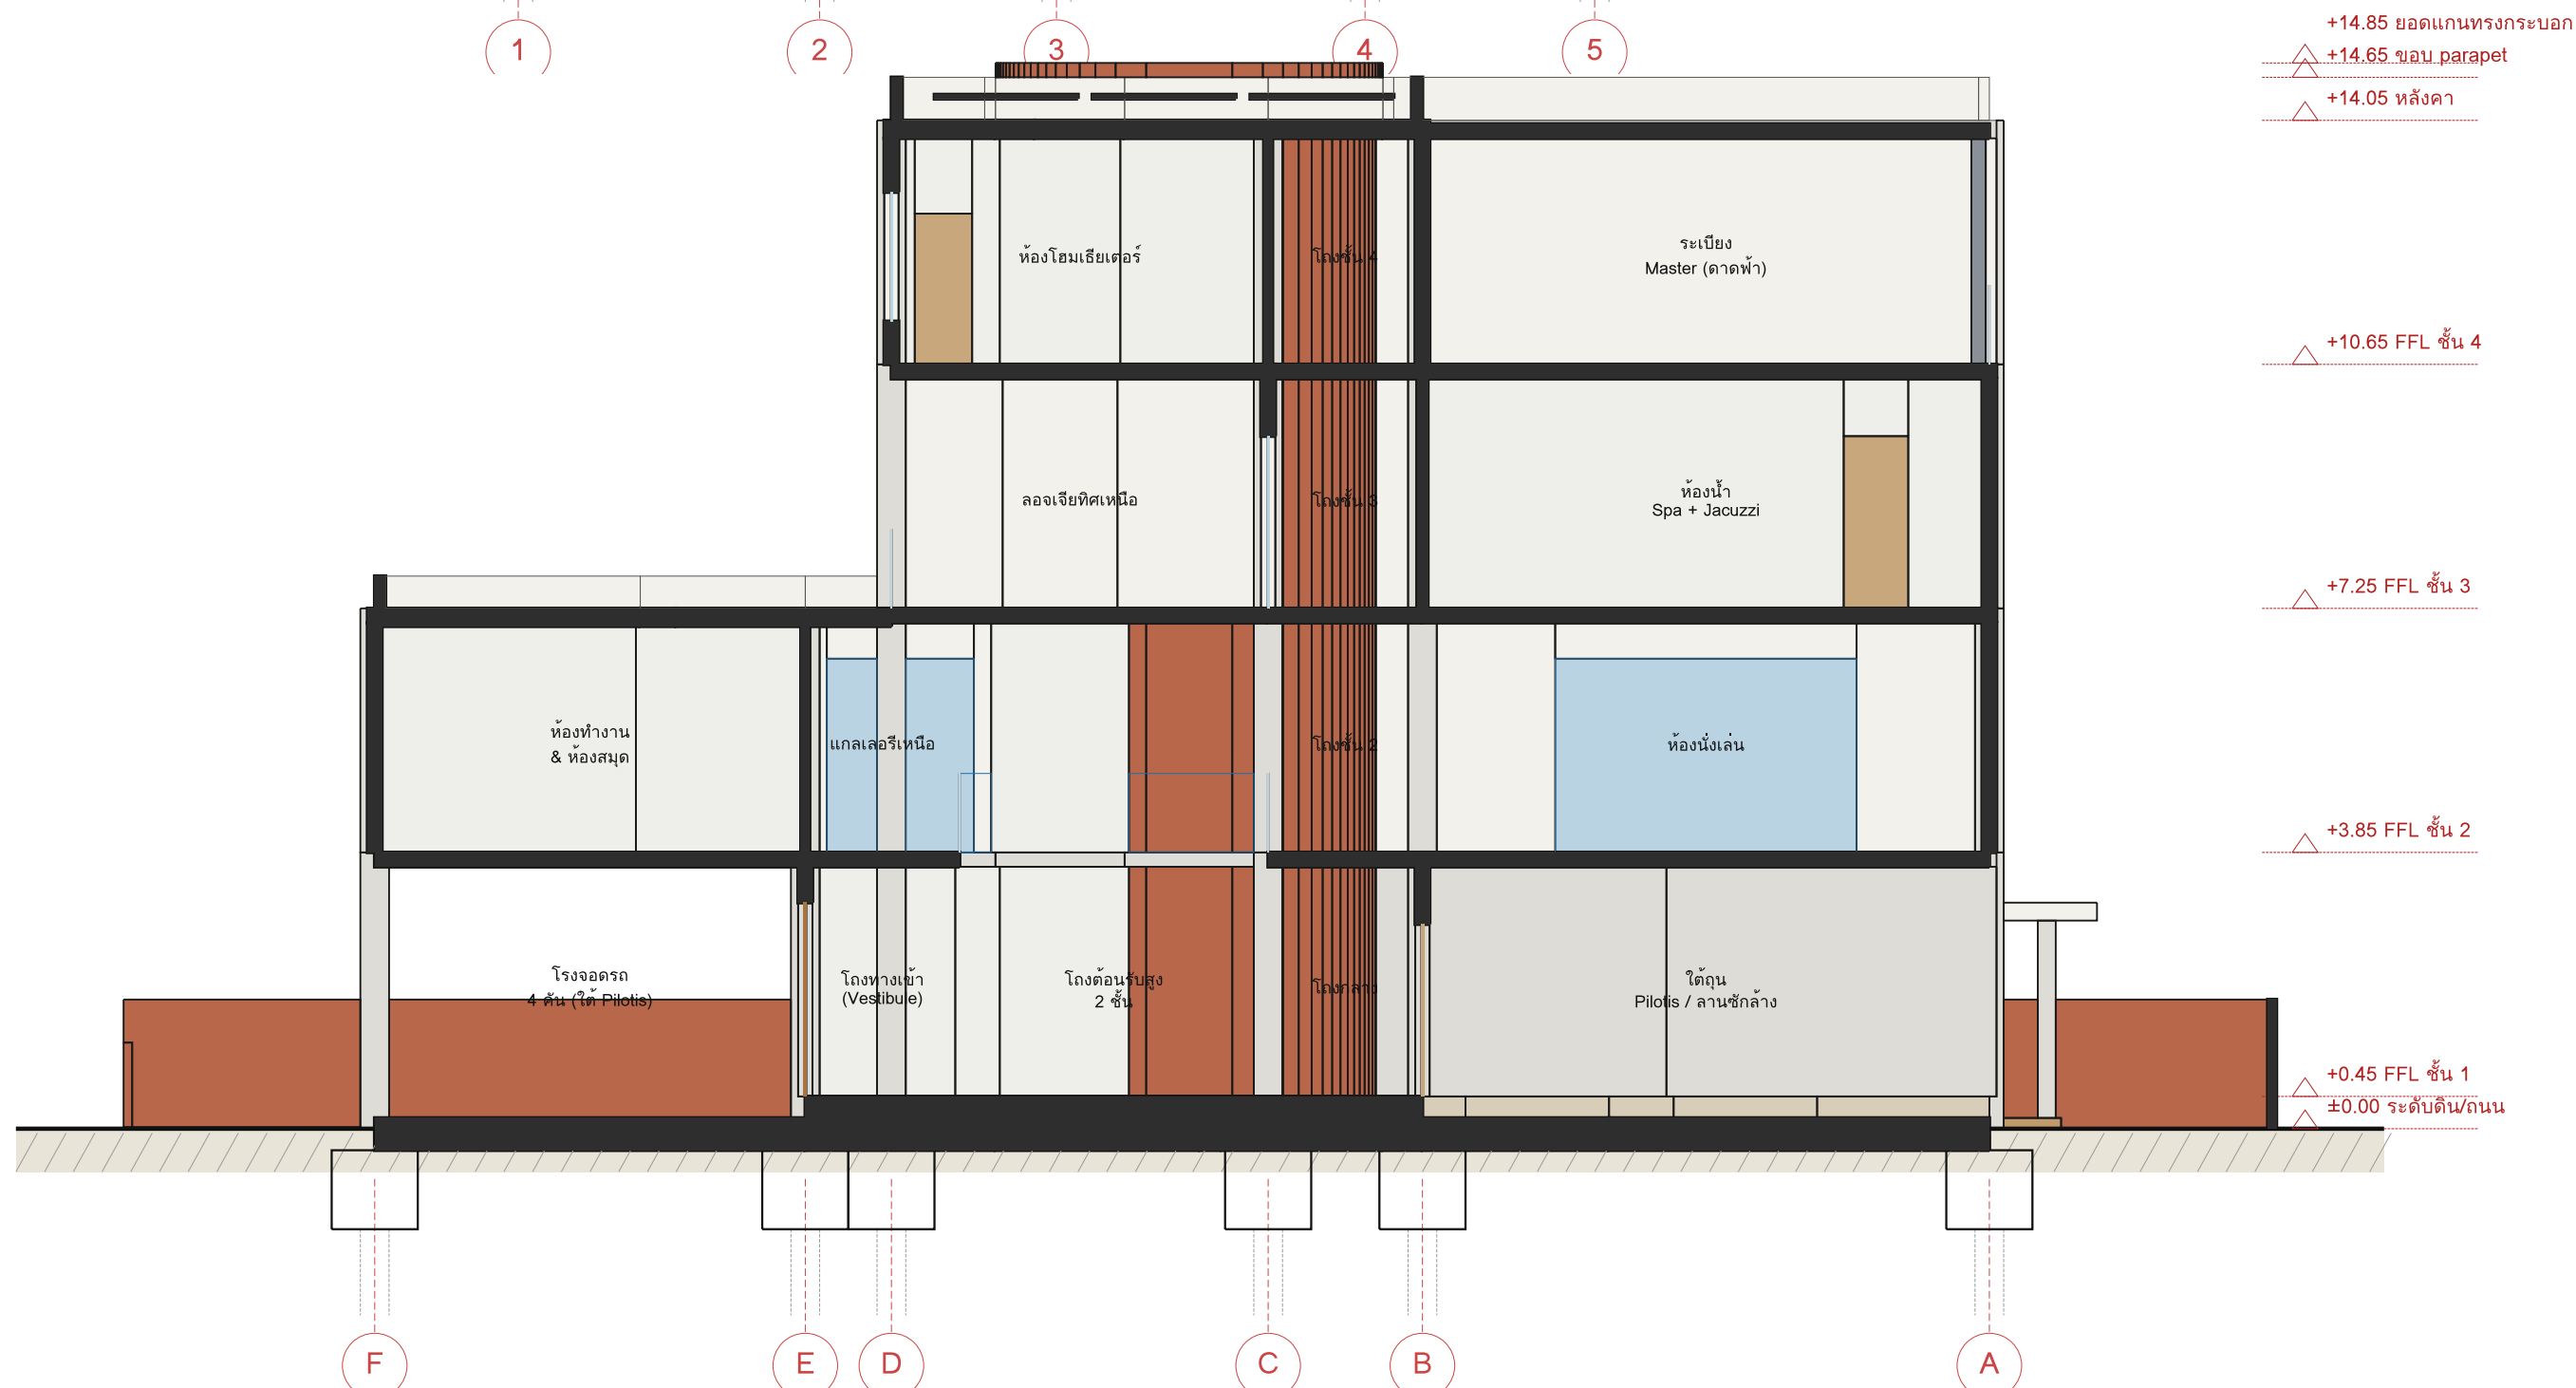

หมายเหตุรูปตัด

- พื้นถ้ำพื้น 3.40 ม. = พื้น 0.20 + ผังงานระบบ 0.40 + โปรง 2.80 ม. (ตามความสูงในโปรแกรม)
- เสาค้ำ/ฐานรากเขียนเป็นสัญลักษณ์ — ขนานลงจริงตามวิศวกรรมโครงสร้าง
- รูปตัด B-B เห็นแกนทรงกระบอกอิฐและบันไดภายในด้านหลัง
- หลังคาสวน +7.25: ดินปลูก 150 มม. น้ำหนักขึ้นน้ำ ~250-300 กก./ตร.ม.

0 5 m

WELL-GBEACH 30x30 Executive Luxury Villa - บ้านเดี่ยว 4 ชั้น "แห่งบนเสาหลอย + หงกระบอกอิฐ" (แนวคิดจาก G-Beach Residence)

ที่ดิน 30.00 x 30.00 ม. (225 ตร.ว.) - ถนน (สมมติ 8.00 ม.) ที่ดินเดิม - โปรแกรม ARCHSPACE 6 ต.ค. 2569

ตารางของเปิด (81 รายการ) — หน่วย มม. วัดจาก FFL

รหัส	ชั้น	ชนิด	กว้าง	ขอบล่าง	ขอบบน	ค่าผนัง
D01	F1	ประตูหลัก	900	0	2100	โครงสร้าง สลักบัน
D02	F1	ประตูบานเปิด	2000	0	2700	โครงสร้าง 4 ชั้น (โครงสร้างเข้า (Ve
SD01	F1	ประตูบานเลื่อนกระจก	1800	0	2400	ครัวไทย (ครัวห)
D03	F1	ประตูบานเปิดเดี่ยว	800	0	2100	ห้องนอน 2 ครัวไทย (ครัวห
SD02	F1	ประตูบานเลื่อนเดี่ยว	900	0	2100	ห้องนอนแขกผู้ ห้องนอนแขก
D04	F1	ประตูบานเปิดเดี่ยว	900	0	2100	ห้องนอนแขกผู้ ตู้เสื้อผ้า
SD03	F1	ประตูบานเลื่อนกระจก	2400	0	2400	ห้องนอนแขกผู้ ภายนอก-S
D05	F1	ประตูบานเปิดเดี่ยว	800	0	2100	ห้อง MEP / ฝ้า ทางเดินบริการ
D06	F1	ประตูบานเปิดเดี่ยว	800	0	2100	ห้องเก็บของ / คน ทางเดินบริการ
D07	F1	ประตูบานเปิดเดี่ยว	800	0	2100	ห้องส้วม โถงกลาง
D08	F1	ประตูบานเปิดเดี่ยว	900	0	2400	โถงนอน โถงกลาง
D09	F1	ประตูบานเปิดเดี่ยว	800	0	2100	ตู้เสื้อผ้าห้อง โถงกลาง
D10	F1	ประตูบานเปิดเดี่ยว	900	0	2400	ทางเดินบริการ โถงนอน
D11	F1	ประตูบานเปิดเดี่ยว	900	0	2400	ห้องนอน 1 ทางเดินบริการ
D12	F1	ประตูบานเปิดเดี่ยว	800	0	2100	ห้องนอนบัน ทางเดินบริการ
W01	F1	หน้าต่าง	3000	600	2400	ห้องนอน 2 ภายนอก-S
W02	F1	หน้าต่าง	1200	600	2400	ห้องนอน 2 ภายนอก-W
W03	F1	หน้าต่าง	3000	600	2400	ห้องนอน 1 ภายนอก-W
W04	F1	หน้าต่าง	1200	1500	2100	ห้องส้วม ภายนอก-W
W05	F1	หน้าต่าง	2400	600	2400	ครัวไทย (ครัวห)
W06	F1	หน้าต่าง	2700	600	2400	ห้องนอนแขกผู้ ภายนอก-E
W07	F1	หน้าต่าง	1200	1500	2100	ห้องนอนแขก ภายนอก-E
W08	F1	หน้าต่าง	1200	1500	2100	ห้องนอนเดี่ยว ภายนอก-E
D13	F2	ประตูหลัก	900	0	2100	โครงสร้าง 2 สลักบัน
SD04	F2	ประตูบานเลื่อนกระจก	2400	0	2400	ครัวไทย + โถง ห้องรับประทานอาหาร
D14	F2	ประตูบานเปิดเดี่ยว	900	0	2100	ครัวไทย + โถง Walk-in Pantry
D15	F2	ประตูบานเปิดเดี่ยว	800	0	2100	Walk-in Pantry & ห้องเก็บของ (ค
D16	F2	ประตูบานเปิดเดี่ยว	900	0	2100	Walk-in Pantry & อินโดนีเซีย
SD05	F2	ประตูบานเลื่อนกระจก	4200	0	2700	ห้องนอน ระเบียงหน้า
SD06	F2	ประตูบานเลื่อนกระจก	4200	0	2700	ห้องนอน ภายนอก-S
SD07	F2	ประตูบานเลื่อนกระจก	3000	0	2700	ห้องรับประทานอาหาร ภายนอก-S
D17	F2	ประตูบานเปิดเดี่ยว	800	0	2100	ตู้เสื้อผ้า Junior ห้องนอน Junior
D18	F2	ประตูบานเปิดเดี่ยว	800	0	2100	ห้องนอน Junior S ห้องนอน Junior
D19	F2	ประตูบานเปิดเดี่ยว	800	0	2100	ตู้เสื้อผ้า Junior ห้องนอน Junior
D20	F2	ประตูบานเปิดเดี่ยว	800	0	2100	ห้องนอน Junior S ห้องนอน Junior
D21	F2	ประตูบานเปิดเดี่ยว	900	0	2400	กลางแจ้ง ห้องทำงาน & ห้
D22	F2	ประตูบานเปิดเดี่ยว	800	0	2100	กลางแจ้ง ตู้เสื้อผ้า Junior
D23	F2	ประตูบานเปิดเดี่ยว	800	0	2100	ห้องนอน / ฝ้า ทางเดินบริการ (Sp
D24	F2	ประตูบานเปิดเดี่ยว	800	0	2100	ทางเดินบริการ (Sp) ห้องนอนแขก (Po
D25	F2	ประตูบานเปิดเดี่ยว	800	0	2100	ทางเดินบริการ (Sp) ตู้เสื้อผ้า Junior
W09	F2	หน้าต่าง	2100	600	2400	ครัวไทย + โถง ภายนอก-S

รหัส	ชั้น	ชนิด	กว้าง	ขอบล่าง	ขอบบน	ค่าผนัง
W10	F2	หน้าต่าง	5400	600	2400	ครัวไทย + โถง ภายนอก-W
W11	F2	ผนังกระจก	2050	0	2700	กลางแจ้งหน้า ภายนอก-E
W12	F2	หน้าต่าง	600	1500	2100	ห้องนอน Junior S ภายนอก-W
W13	F2	หน้าต่าง	3000	600	2400	ห้องนอน Junior S ภายนอก-N
W14	F2	หน้าต่าง	2700	600	2400	ห้องนอน Junior S ภายนอก-W
W15	F2	หน้าต่าง	2700	600	2400	ห้องทำงาน & ห้อง ภายนอก-N
W16	F2	หน้าต่าง	1200	1500	2100	ห้องนอน Junior S ภายนอก-E
W17	F2	หน้าต่าง	3600	600	2400	ห้องนอน Junior S ภายนอก-N
W18	F2	หน้าต่าง	2100	600	2400	ห้องนอน Junior S ภายนอก-E
D26	F3	ประตูหลัก	900	0	2100	โครงสร้าง 3 สลักบัน
D27	F3	ประตูบานเปิดเดี่ยว	900	0	2400	ห้องนอน Spa + Ja ห้องนอน Master
SD08	F3	ประตูบานเลื่อนเดี่ยว	900	0	2400	Walk-in Dressing ห้องนอน Spa +
SD09	F3	ประตูบานเลื่อนกระจก	4200	0	2700	ห้องนอน Master S ระเบียงหน้า
SD10	F3	ประตูบานเลื่อนกระจก	3600	0	2700	ห้องนอน Master S ภายนอก-S
W19	F3	หน้าต่าง	2400	900	2400	ห้องนอน Spa + Ja ภายนอก-S
SD11	F3	ประตูบานเลื่อนกระจก	1800	0	2400	โครงสร้าง 3 ระเบียงหน้า
SD12	F3	ประตูบานเลื่อนกระจก	2400	0	2400	โครงสร้าง 3 ระเบียงหน้า
D28	F3	ประตูบานเปิดเดี่ยว	900	0	2400	โครงสร้าง 3 โครงสร้าง 3
W20	F3	หน้าต่าง	1200	1500	2100	Walk-in Dressing ภายนอก-S
W21	F3	หน้าต่าง	1200	1500	2100	Walk-in Dressing ภายนอก-W
W22	F3	ผนังกระจก	1500	0	3000	อินโดนีเซีย ภายนอก-W
W23	F3	หน้าต่าง	1200	1500	2100	ห้องนอน ภายนอก-N
W24	F3	หน้าต่าง	1150	1500	2100	ห้องนอน ภายนอก-E
D29	F4	ประตูหลัก	900	0	2100	โครงสร้าง 4 สลักบัน
SD13	F4	ประตูบานเลื่อนกระจก	2400	0	2400	Master Walk-in C ระเบียง Master
SD14	F4	ประตูบานเลื่อนกระจก	2400	0	2400	ระเบียง & BBQ (ห) โครงสร้าง 4
D30	F4	ประตูบานเปิดเดี่ยว	900	0	2100	ห้องนอนแขก อินโดนีเซีย
W25	F4	หน้าต่าง	3600	600	2400	ห้องนอนแขก ภายนอก-N
D31	F4	ประตูบานเปิดเดี่ยว	800	0	2100	ห้องนอนแขก ห้องอุปกรณ์ AV
D32	F4	ประตูบานเปิดเดี่ยว	800	0	2100	ห้องนอนแขก ห้องนอน 4
D33	F4	ประตูบานเปิดเดี่ยว	800	0	2100	Master Walk-in C อินโดนีเซีย M
D34	F4	ประตูบานเปิดเดี่ยว	900	0	2400	โครงสร้าง 4 ห้องนอนแขก
W26	F4	หน้าต่าง	1200	1500	2100	Master Walk-in C ภายนอก-S
W27	F4	หน้าต่าง	1200	1500	2100	Master Walk-in C ภายนอก-W
W28	F4	ผนังกระจก	1500	0	3000	อินโดนีเซีย ภายนอก-W
W29	F4	หน้าต่าง	1800	600	2400	ห้องนอนแขก ภายนอก-W
W30	F4	หน้าต่าง	1800	600	2400	ห้องนอนแขก ภายนอก-N
W31	F4	หน้าต่าง	1200	1500	2100	ห้องนอน 4 ภายนอก-N
W32	F4	หน้าต่าง	1200	1500	2100	ห้องอุปกรณ์ AV / ภายนอก-N
W33	F4	หน้าต่าง	1150	1500	2100	ห้องอุปกรณ์ AV / ภายนอก-E

0.39 หรือ 6 ของเปิด >= 10% ของพื้นที่ห้อง

ห้อง	ของเปิดพื้นที่ห้อง	ผล
F1 ห้องนอน 2	65.6% (5.66/1.52)	ผ่าน
F1 ห้องนอน 1	45.9% (5.40/1.76)	ผ่าน
F1 ห้องนอนบัน	0.0% (0.00/6.00) -> ปิดหน้าต่าง (ข้อ 6 วรร	ผ่าน
F1 ห้องส้วม	4.4% (0.72/16.32) -> ปิดหน้าต่าง (ข้อ 6 วรร	ผ่าน
F1 ห้อง MEP / ฝ้า	0.0% (0.00/13.92) -> ปิดหน้าต่าง (ข้อ 6 วรร	ผ่าน
F1 ห้องเก็บของ / คน	0.0% (0.00/13.92) -> ปิดหน้าต่าง (ข้อ 6 วรร	ผ่าน
F1 ครัวไทย (ครัวห)	42.9% (8.64/20.14)	ผ่าน
F1 ห้องนอนแขกผู้	54.9% (10.62/19.36)	ผ่าน
F1 ตู้เสื้อผ้าห้อง	0.0% (0.00/7.70) -> ปิดหน้าต่าง (ข้อ 6 วรร	ผ่าน
F1 ห้องนอนแขก	9.4% (0.72/7.70) -> ปิดหน้าต่าง (ข้อ 6 วรร	ผ่าน
F1 ห้องเก็บเสื้อผ้า	8.5% (0.72/8.48) -> ปิดหน้าต่าง (ข้อ 6 วรร	ผ่าน
F2 ครัวไทย + โถง	48.1% (13.50/28.05)	ผ่าน
F2 ห้องรับประทานอาหาร	20.3% (8.10/39.90)	ผ่าน
F2 ห้องนอน	44.9% (22.68/50.56)	ผ่าน
F2 Walk-in Pantry & ห้อง	0.0% (0.00/11.88) -> ปิดหน้าต่าง (ข้อ 6 วรร	ผ่าน
F2 ห้องนอน / ฝ้า	0.0% (0.00/14.04) -> ปิดหน้าต่าง (ข้อ 6 วรร	ผ่าน
F2 ห้องเก็บของ (จาก Pantry)	0.0% (0.00/4.40) -> ปิดหน้าต่าง (ข้อ 6 วรร	ผ่าน
F2 ห้องนอน (Powder)	0.0% (0.00/5.20) -> ปิดหน้าต่าง (ข้อ 6 วรร	ผ่าน
F2 ห้องนอน Junior Suite 2	5.5% (0.36/6.60) -> ปิดหน้าต่าง (ข้อ 6 วรร	ผ่าน
F2 ตู้เสื้อผ้า Junior Suite 2	0.0% (0.00/7.60) -> ปิดหน้าต่าง (ข้อ 6 วรร	ผ่าน
F2 ห้องนอน Junior Suite 2	50.9% (10.26/20.16)	ผ่าน
F2 ห้องนอน & ห้อง	18.4% (4.86/26.40)	ผ่าน
F2 ตู้เสื้อผ้า Junior Suite 3	0.0% (0.00/7.59) -> ปิดหน้าต่าง (ข้อ 6 วรร	ผ่าน
F2 ห้องนอน Junior Suite 3	12.5% (0.72/5.76)	ผ่าน
F2 ห้องนอน Junior Suite 3	47.8% (10.26/21.46)	ผ่าน
F3 Walk-in Dressing (His & Hers)	4.5% (1.44/31.90) -> ปิดหน้าต่าง (ข้อ 6 วรร	ผ่าน
F3 ห้องนอน Spa + Jacuzzi	12.7% (3.60/28.44)	ผ่าน
F3 ห้องนอน Master Suite	45.2% (21.06/46.61)	ผ่าน
F3 ห้องเก็บของชั้น 3	39.4% (14.14/34)	ผ่าน
F4 Master Walk-in Closet ชั้น 4	19.7% (7.20/36.64)	ผ่าน
F4 ห้องนอนแขก & Upper Ga	18.1% (6.48/35.90)	ผ่าน
F4 ห้องนอน 4	15.0% (0.72/4.80)	ผ่าน
F4 ห้องนอนแขก	19.6% (6.48/33.08)	ผ่าน
F4 ห้องนอน AV / เก็บ	30.4% (14.14/46.64)	ผ่าน

ระนาบอากาศ >= 2 แนวหนึ่ง (เกณฑ์ภายใน สนับสนุน R-T06) / ลึก <= 4.20 ม.

ห้อง/ส่วนประจำ	ของเปิด	ลึกจากผนัง	ผล
F1 ห้องนอน 2	2 แนวหนึ่ง	2.25 ม.	ผ่าน
F1 ห้องนอน 1	1 แนวหนึ่ง -> ยาว 1 ม.	2.25 ม.	ผ่าน
F1 ครัวไทย (ครัวห)	2 แนวหนึ่ง	2.55 ม.	ผ่าน
F1 ห้องนอนแขก/ผู้	2 แนวหนึ่ง	2.15 ม.	ผ่าน
F2 ครัวไทย + โถง	2 แนวหนึ่ง	3.45 ม.	ผ่าน
F2 ห้องรับประทานอาหาร	2 แนวหนึ่ง	7.65 ม. -> ยาว 1 ม. แนว 1 ได้ 7	ผ่าน
F2 ห้องนอน	2 แนวหนึ่ง	6.25 ม. -> ยาว 1 ม. แนว 2 ด้าน	ผ่าน
F2 ห้องนอน Junior Suite 2	2 แนวหนึ่ง	4.05 ม.	ผ่าน
F2 ห้องนอน & ห้อง	1 แนวหนึ่ง -> ยาว 1 ม.	5.85 ม. -> ยาว 1 ม. แนว 1 ได้ 7	ผ่าน
F2 ห้องนอน Junior Suite 3	2 แนวหนึ่ง	3.55 ม.	ผ่าน
F3 ห้องนอน Master Suite	2 แนวหนึ่ง	5.75 ม. -> ยาว 1 ม. แนว 2 ด้าน	ผ่าน
F4 ห้องนอนแขก & Upper Ga	2 แนวหนึ่ง	5.67 ม. -> ยาว 1 ม. แนว 1 ได้ 7	ผ่าน
F4 ห้องนอนแขก & Upper Ga	2 แนวหนึ่ง	1.85 ม.	ผ่าน
F4 ห้องนอนแขก	1 แนวหนึ่ง -> ยาว 1 ม.	5.10 ม. -> ยาว 1 ม. แนว 1 ได้ 7	ผ่าน

ตารางจากเปิดของเปิด (เปิด/ยาว/ลึก) 17 รายการ: ผ่าน 17

เทียบโปรแกรม ARCHSPACE (ตร.ม.)

รายการโปรแกรม	ชั้น	โปรแกรม	ชั้นบน	แบบ	ค่า
Grand Double-Height Foyer	F1	24.00	F1	24.08	+0.08
Formal Living Room	F2	50.00	F2	50.56	+0.56
Dining Room (10-12 Seats)	F2	40.00	F2	39.90	-0.10
Powder Room	F2	6.00	F2	5.20	-0.80
Home Theater / AV Lounge	F4	36.00	F4	33.08	-2.92
Wine Cellar / Cigar Room	F2	14.00	F2	14.04	+0.04
Master Suite Bedroom	F3	48.00	F3	46.61	-1.39
Master Walk-in (His & Hers)	F3	32.00	F3	31.90	-0.10
Spa Master Bath + Jacuzzi	F3	28.00	F3	28.44	+0.44
Junior Suite 2 (bath+closet)	F2	34.00	F2	34.56	+0.56
Junior Suite 3 (bath+closet)	F2	34.00	F2	34.80	+0.80
Guest Suite (CF / elderly)	F1	30.00	F1	34.76	+4.76
Family Lounge & Upper Gallery	F4	36.00	F4	35.90	-0.10
Executive Home Office & Library	F2	26.00	F2	26.40	+0.40
Master Walk-in Closet (UL)	F4	36.00	F4	36.64	+0.64
Show Kitchen & Island Bar	F2	28.00	F2	28.05	+0.05
Heavy Thai Kitchen	F1	20.00	F1	20.14	+0.14
Walk-in Pantry & Cold Storage	F3	12.00	F2	11.88	-0.12
Laundry & Utility Room	F1	16.00	F1	16.32	+0.32
Maid Bedroom 1 & 2	F1	22.00	F1	23.28	+1.28
Maid Bathroom	F1	6.00	F1	6.00	+0.00
MEP / Electrical / Generator	F1	14.00	F1	13.92	-0.08
Covered Garage 3-4 cars	F1	85.00	F1	90.00	+5.00
Covered Veranda & BBQ	F4	45.00	F4	42.66	-2.34
Upper Master Terrace	F4	28.00	F4	27.65	-0.35
Poolside Pavilion	F1	35.00	สวน	35.25	+0.25
รวม NJA		785.00		792.02	+7.02

แบบชุด = ชั้นในแบบต่างจากโปรแกรม (Pantry ชั้น 3 -> 2 ตามที่เลือก 8 A-01 ข้อ 2)
ส่วนล่างที่เหลือ: ห้องตามรหัส 15.00 ม. ขึ้นลง 10-15% — ห้องที่ต่ำกว่าโปรแกรม 10% คูณค่า "ค่า" คูณ

H3A DESIGN AND BUILD

X-UNIT Architecture Lab

โครงการ

WELL-GBEACH 30x30

Executive Luxury Villa
บ้านเดี่ยว 4 ชั้น ผ่านเกณฑ์
WELL for Residential (เจดนา)

ที่ดิน 30.00 x 30.00 ม. = 225 ตร.ว.
ถนนสาธารณะที่ดิน (สมมติ 8.00 ม.)

แนวคิด

จาก G-Beach Residence (B+D+M):
แห่ง 15.00 x 22.50 ม. บนเสาหลอย
+ แกนบันไดทรงกระบอกอิฐ Ø5.40
+ ผนังอิฐโปร่งทิศตะวันตก

ระดับ

±0.00 ถนน · F1 +0.45 · F2 +3.85
F3 +7.25 · F4 +10.65
หลังคา +14.05 · parapet +14.65
ยอดทรงกระบอก +14.85

หมายเหตุ

- หน่วยงานเป็นผลิตภัณฑ์ เว้นแต่ระบุ
 - ระดับอ้างอิงถนนพื้นที่ ±0.00
 - ห้ามวัดขนาดจากแบบ ใช้ตัวเลขกำกับ
 - แบบระดับ Design Development
- ต้องให้สถาปนิกและวิศวกรผู้ได้รับ
ใบอนุญาตตรวจสอบและลงนาม
ก่อนยื่นขออนุญาต

ชื่อแผ่น

ตารางประตู-หน้าต่าง
+ ตารางของเปิด + เทียบโปรแกรม

มาตราส่วน: ไม่มีมาตราส่วน

วันที่ 6 ต.ค. 2569 ฉบับ v1 / DD

WELL-GBEACH 30x30 Executive Luxury Villa - บ้านเดี่ยว 4 ชั้น "แห่งบนสาละย + หอกระบอกอิฐ" (แนวคิดจาก G-Beach Residence)

ที่ดิน 30.00 x 30.00 ม. (225 ตร.ว.) · ถนน (สมมติ 8.00 ม.) ทิศเหนือ · โปรแกรม ARCHISPAC 6 ต.ค. 2569

กลยุทธ์ WELL for Residential (รหัสตาม Guidebook ก.พ. 2026)

Feature (WELL for Residential)	การตอบสนองในแบบ	สถานะ	หลักฐานที่ต้องมี
R-A01 ระบบระบายอากาศ	พัดลมดูดเฉพาะจุดครัว/ห้องน้ำ/ห้องไม่มีหน้าต่าง 15 ห้อง + ERV ห้องนอน	ระบุในแบบงานระบบ	ต้องวัด
R-A05 ลดการเผาไหม้	ครัวโซว์ชั้น 2 เต้าไฟฟ้าเหนียวน้ำ; ครัวไทยชั้น 1 แยก มีชุด + เเปด 2 ด้าน	ในแบบ	เอกสาร
R-A09 จุดชาร์จ EV	1 จุดในโรงรถใต้เสาลอย (ต่อเมื่อ 4 ช่อง)	ในแบบ	ภาพถ่าย
R-W03 น้ำที่ไม่ใช้น้ำดื่ม	ถังน้ำฝนใต้ดิน ~12 ลบ.ม. สำหรับรดน้ำ/ซักโครก	ในแบบ	แบบสุขาภิบาล
R-L01 แสงธรรมชาติ	38.8% (141.7/364.9 ตร.ม.) -> ระดับ 3	คำนวณแล้ว	ต้องตรวจแสงจ้า
R-L02 ควบคุมแสง	วงจรแยกทุกห้อง + ม่านทึบห้องนอน/เฮียเตอร์	ระบุ	แบบไฟฟ้า
R-T06 หน้าต่างเปิดได้	14/14 ห้อง	คำนวณแล้ว	นั้งลาด/ตัวล็อก
R-T07 ความร้อนภายนอก	หลังคาสวน + หลังคาขาว SR >= 0.75 + ผนังอิฐโปร่งทิศตะวันตก + ดินไม่ร้อน	ในแบบ	ค่า SR วัสดุ
R-V04 พื้นที่กิจกรรมกลางแจ้ง	สระ 3.80 x 16.00 ม. + ศาลา + ระเบียงทุกชั้น + ศาลาฟ้า	ในแบบ	-
R-V07 ออกแบบบันได	บันไดในหอกระบอก ประดูจากโถงทุกชั้น แสงจากยอด (ใช้ก่อนลิฟต์)	ในแบบ	ภาพถ่าย
R-M01 ธรรมชาติและสถานที่	ห้องหลักมองสวนสระทิศตะวันออก; วัสดุอิฐ-ไม้	ในแบบ	-
R-M04 พื้นที่ยึดเก็บ	Walk-in 2 ชั้น (Master) + ตู้ทุกห้องนอน + ห้องเก็บของทุกชั้น	ในแบบ	-
R-N01 การปรุงอาหาร	ครัว 2 ส่วน (โซว์/ไทย) + Pantry ห้องเย็นติดครัวโซว์	ในแบบ	-
R-S01 แนวกันเสียง	Master ทิศใต้ไกลถนน; Junior Suite ทิศเหนือไกลถนน -> กระຈก 2 ชั้น	ต้องระบุ STC	ทดสอบ
R-C01 ออกแบบเพื่อทุกคน	ลิฟต์บ้านทุกชั้น + ห้องแขกชั้น 1; ทางลาด 1:12 ยังต้องเพิ่ม	บางส่วน	ดู A-01 ข้อ 6
R-C06 กายพิบัติ	ยกพื้น +0.45 + บันไดหนีไฟ + เครื่องบันไฟ	ในแบบ	ระดับน้ำท่วมจริง?
R-X02 วัสดุ	สีทา VOC ต่ำ ไม้รับรอง FSC	สเปก	ใบสั่งซื้อ

สถานะ = เจตนาการออกแบบ ยังไม่ใช่คะแนนรับรอง: WELL Residence ต้องลงทะเบียน JWBI ส่งเอกสาร และตรวจวัดจริงหลังก่อสร้าง
ห้องที่ใช้พัฒนาะบาย: ห้องน้ำแม่บ้าน, ห้องซักรีด, ห้อง MEP / ไฟฟ้า, ห้องเก็บของ / คนขับรถ, ตู้เสื้อผ้าห้องแขก, ห้องน้ำห้องแขก, ห้องเก็บเสื้อผ้า, Walk-in Pantry & ห้องเย็น, ห้องโถง / ซิการ์, ห้องเก็บของ (ต่อจาก Pantry), ห้องน้ำแขก (Powder), ห้องน้ำ Junior Suite 2, ตู้เสื้อผ้า Junior Suite 2, ตู้เสื้อผ้า Junior Suite 3, Walk-in Dressing (His & Hers)

มุมมองทิศตะวันตกเฉียงเหนือ — หลังคาสวน +7.25, บันไดหนีไฟ, ผนังอิฐโปร่ง



วัสดุหลัก

หมวด	ข้อกำหนด (ระดับแนวคิด)
โครงสร้าง	ค.ส.ล. เสา 0.40x0.40 กริด 5 x 6 แนว · พื้นไร้คาน/คานแบน 0.20 · ฐานรากเสาเข็มเจาะ (รอผลเจาะดิน)
หอกระบอก	ผนัง ค.ส.ล. รับแรง + อิฐโซว์แนวกรู (แบบแสดงหนา 200 — ต้องยื่นยื่นความหนาจริง) · บันได ค.ส.ล.
ผนังอิฐโปร่ง	อิฐ 115 มม. @290 + แกบนอน @520 ยึดโครงสร้างเหล็กกลาไนซ์ ท่างผนัง 0.34-0.45 ม.
ผนังภายนอก	บล็อกมวลเบา 200 + ฉาบเรียบสีขาว · ผนังภายใน 120 / ห้องน้ำ 150
กระจก	Low-E laminated · SHGC <= 0.25 ทิศ ตก/ออก · กรอบอะลูมิเนียมสีเทาเข้ม
หลังคา	ค.ส.ล. + PU 50 + กันซึม + สี SR >= 0.75 · หลังคาสวน extensive 150 มม.
พื้น	หินขัด (ชั้น 1) · ไม้เอ็นจิเนียร์ (ชั้น 2-4) · กระเบื้องกันลื่น R11 ห้องน้ำ
ภายนอก	สระน้ำเกลือ 3.80 x 16.00 ลึก 1.40 ม. · พื้น WPC รอบสระ · บันไดหนีไฟเหล็กกลาไนซ์


สิ่งที่ต้องทำต่อ

- วิศวกรโครงสร้าง: หอกระบอก 4 ชั้น, ผนังอิฐโปร่ง (แรงลม), หลังคาสวน, เสาเข็ม
- วิศวกรงานระบบ: VRF + ERV, พัฒนาระบาย, ระบบน้ำฝน, เครื่องขึ้นไฟ, โซลาร์ 25.85 kWp
- ยืนยันกับสำนักงานเขต: บันไดหนีไฟ (ข้อ 27) สำหรับบ้านเดี่ยว 4 ชั้น, ความกว้างถนนจริง, ผังเมืองรวม
- จำลองแสง/แสงจ้า และความร้อน: ผนังอิฐโปร่งลดแสงที่ loggia/ห้องนั่งเล่นรอบครัว (การคำนวณ R-L01 ยังไม่หักเงาอิฐ)
- แบบขยาย: ทางลาด 1:12, บันไดหอกระบอก, บันไดสวนตัว, ราวกันตก, ผนังอิฐโปร่ง, สระ
- ลงทะเบียน WELL Residence และเตรียมเอกสารตามตาราง
- ประมาณราคาละเอียด (BOQ) หลังได้แบบโครงสร้าง-งานระบบ

สรุปการตรวจ

ผลตรวจทั้งหมด 112 รายการ: ผ่าน 112 / ไม่ผ่าน 0 (รายการ "ยกเว้น" มีเหตุผลกำกับ ดู A-11)
แบบระดับ design development ต้องให้สถาปนิกและวิศวกรผู้ได้รับใบอนุญาตตรวจสอบและลงนามก่อนยื่นขออนุญาต

จากมุมสวนทิศตะวันออกเฉียงเหนือ — หอกระบอกอิฐรับสระ

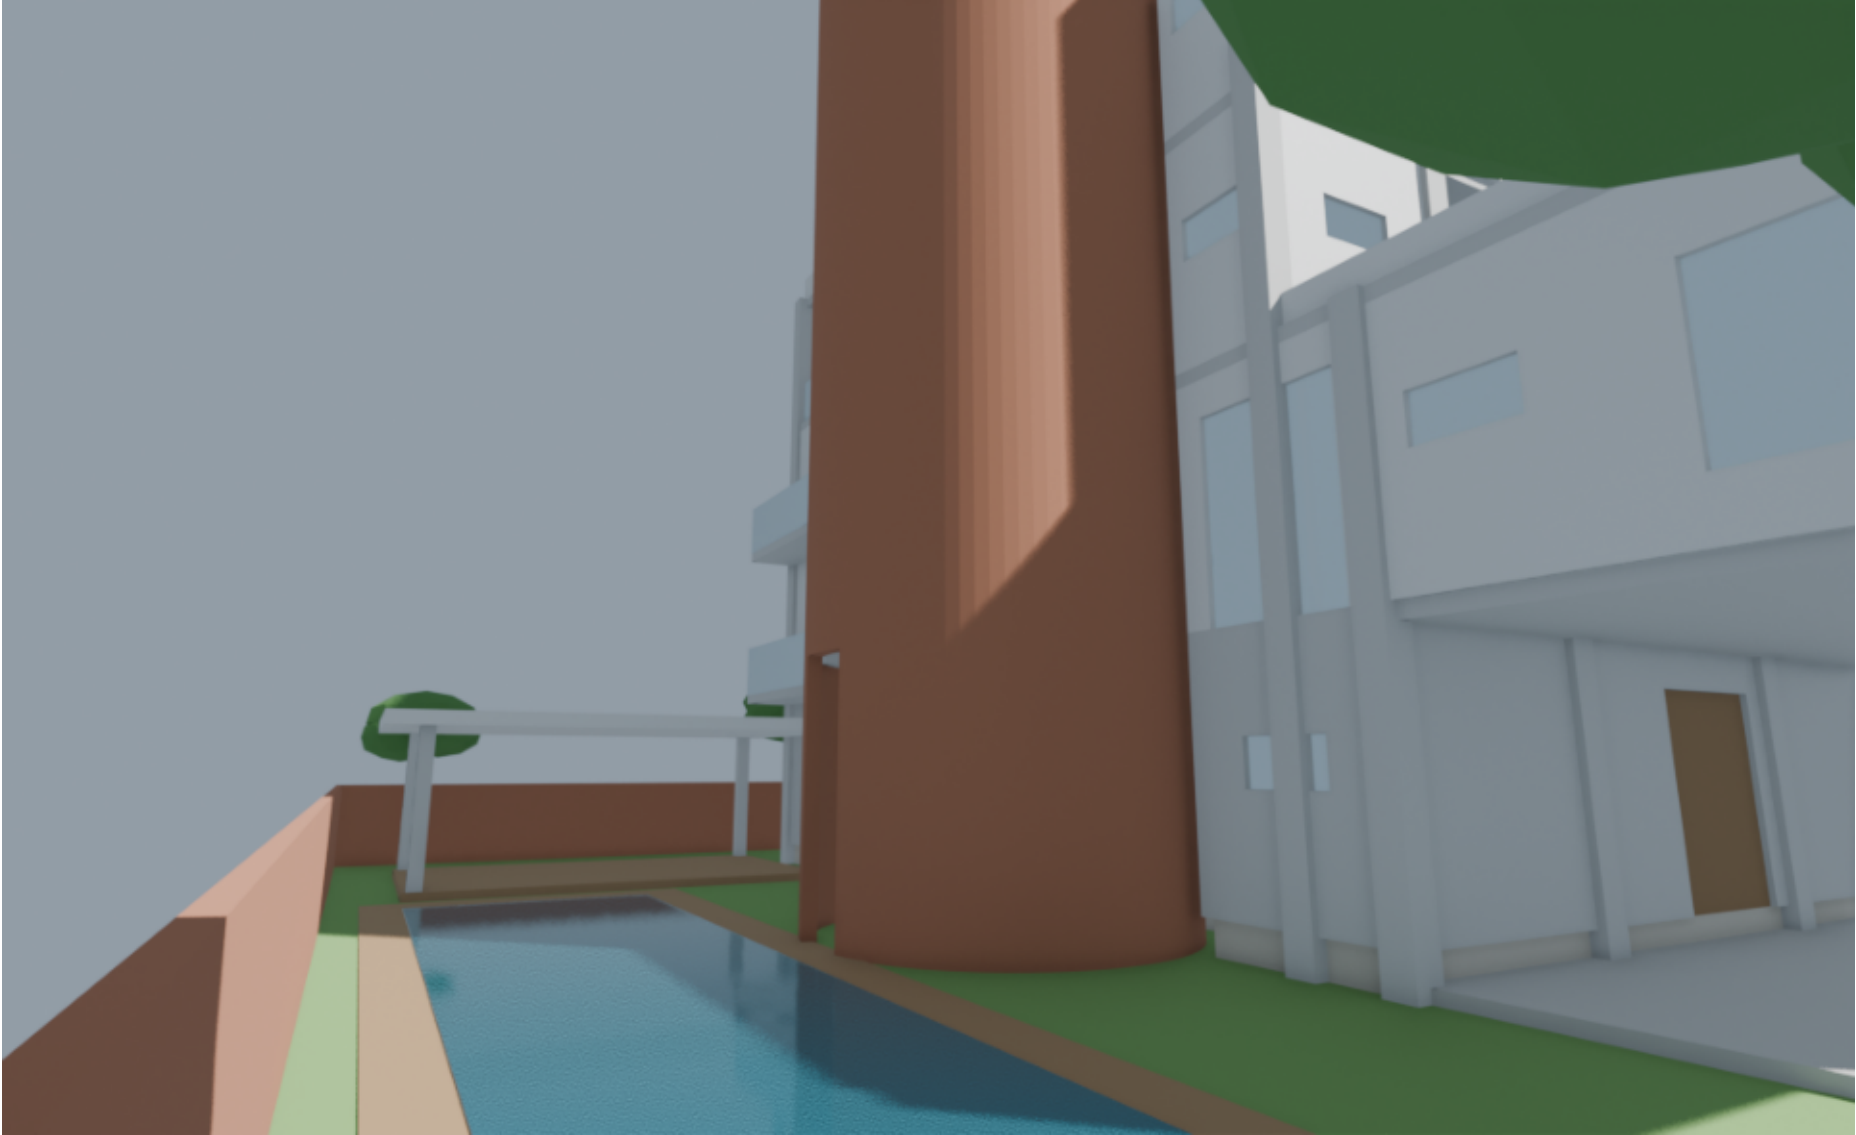

H3A DESIGN AND BUILD

X-UNIT Architecture Lab

โครงการ

WELL-GBEACH 30x30

Executive Luxury Villa
บ้านเดี่ยว 4 ชั้น ผ่านเกณฑ์
WELL for Residential (เจดนา)

ที่ดิน 30.00 x 30.00 ม. = 225 ตร.ว.
ถนนสาธารณะทิศเหนือ (สมมติ 8.00 ม.)

แนวคิด

จาก G-Beach Residence (B+D+M):
แท้ง 15.00 x 22.50 ม. บนสาละย
+ แกนบันไดหอกระบอกอิฐ Ø5.40
+ ผนังอิฐโปร่งทิศตะวันตก

ระดับ

±0.00 ถนน · F1 +0.45 · F2 +3.85
F3 +7.25 · F4 +10.65
หลังคา +14.05 · parapet +14.65
ยอดหอกระบอก +14.85

หมายเหตุ

- ผนังเป็นเอนิธลิเมตร เว้นแต่ระบุ
 - ระดับอ้างอิงถนนพื้นที่ดิน ±0.00
 - ห้ามวัดขนาดจากแบบ ใช้ตัวเลขกำกับ
 - แบบระดับ Design Development
- ต้องให้สถาปนิกและวิศวกรผู้ได้รับ
ใบอนุญาตตรวจสอบและลงนาม
ก่อนยื่นขออนุญาต

ชื่อแผ่น

WELL for Residential
+ วัสดุ + สิ่งที่ต้องทำต่อ

มาตราส่วน: ไม่มีมาตราส่วน

วันที่ 6 ค.ค. 2569 ฉบับ v1 / DD