



ภาพจากโมเดล Blender (WELL-GENWEAVE-40x40-v3-model.blend) — โมเดลมวลอาคารระดับ DD สร้างจากข้อมูลชุดเดียวกันแบบ CAD


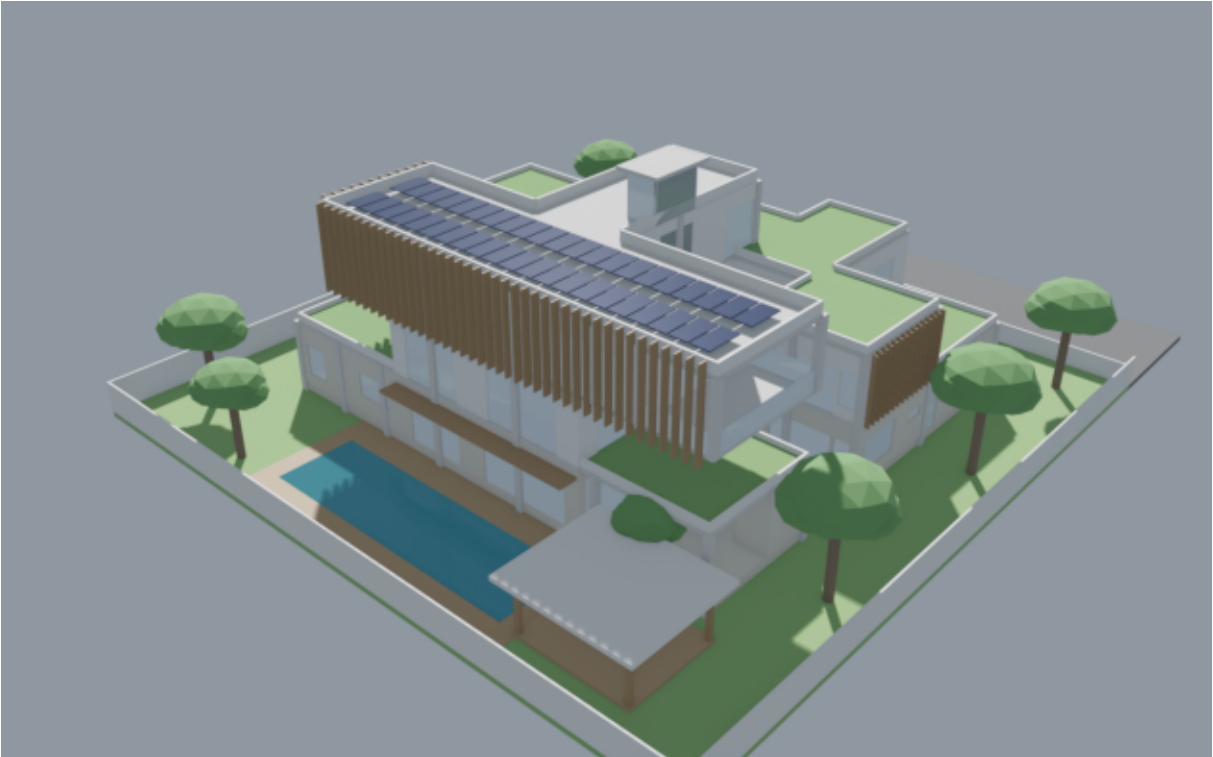


มุมมองทางอากาศ ทิศตะวันออกเฉียงใต้ — Crown bar ชั้น 3 ห่อด้วยครีปไม้ (CACTUS skin) + แผงโซลาร์ 23.1 kWp

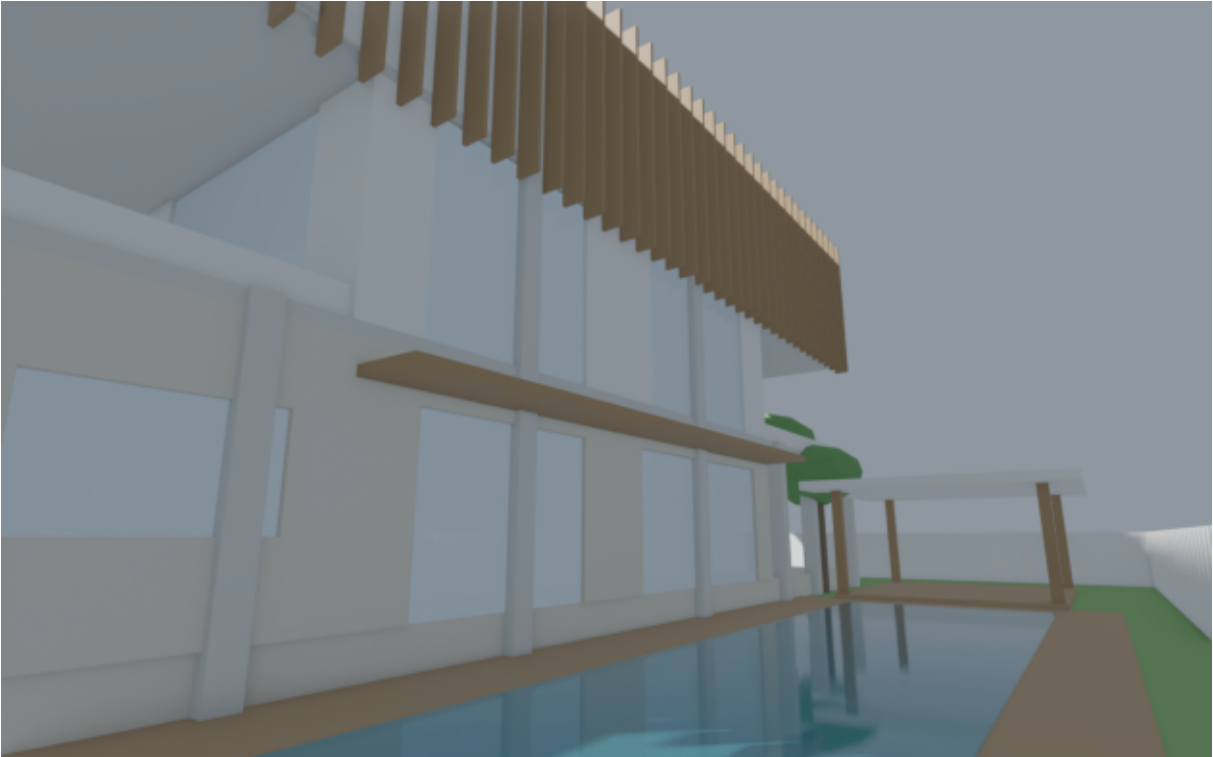

จากสวนทิศใต้ — ห้องนั่งเล่นห้องอาหารสูง 2 ชั้น กันสาดไม้ +3.50 ครีปไม้ชั้น 3

โดอะแกรม TREE -> WEAVE: ลำต้น + 4 กิ่ง รอบ 2 คอร์ต (ฝั่งชั้น 1, 1:250)

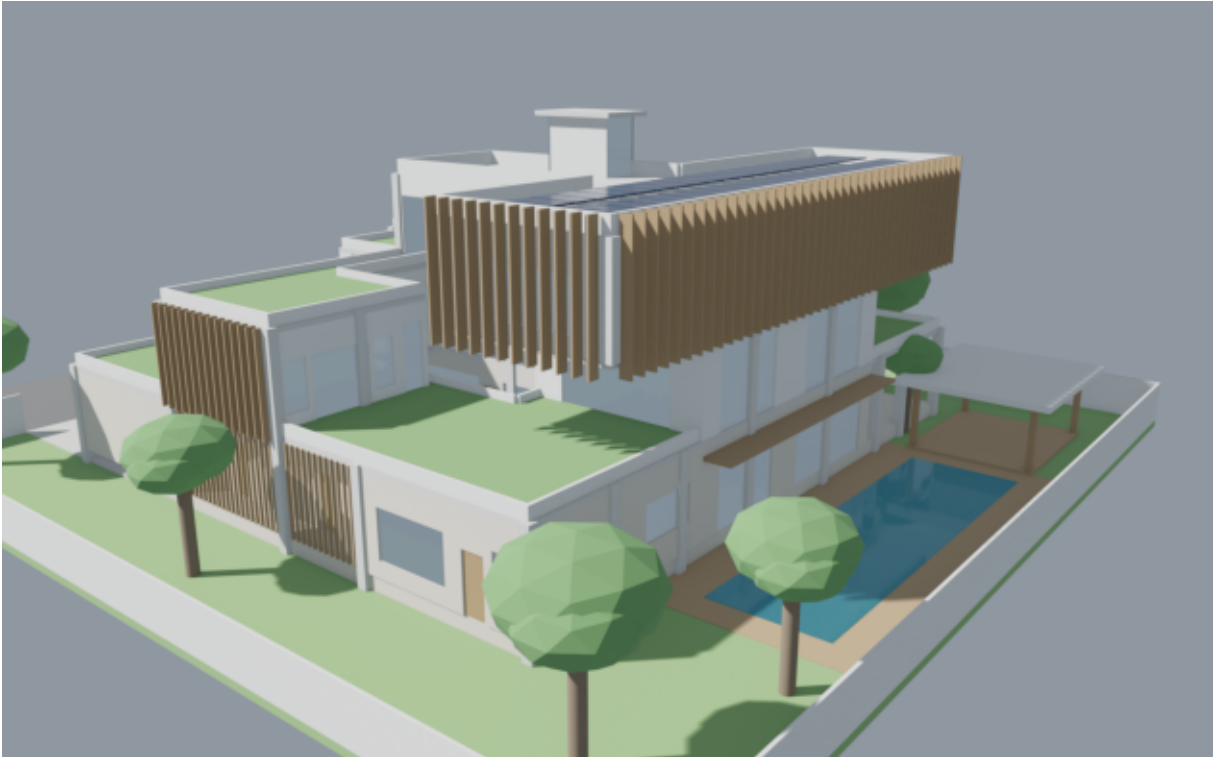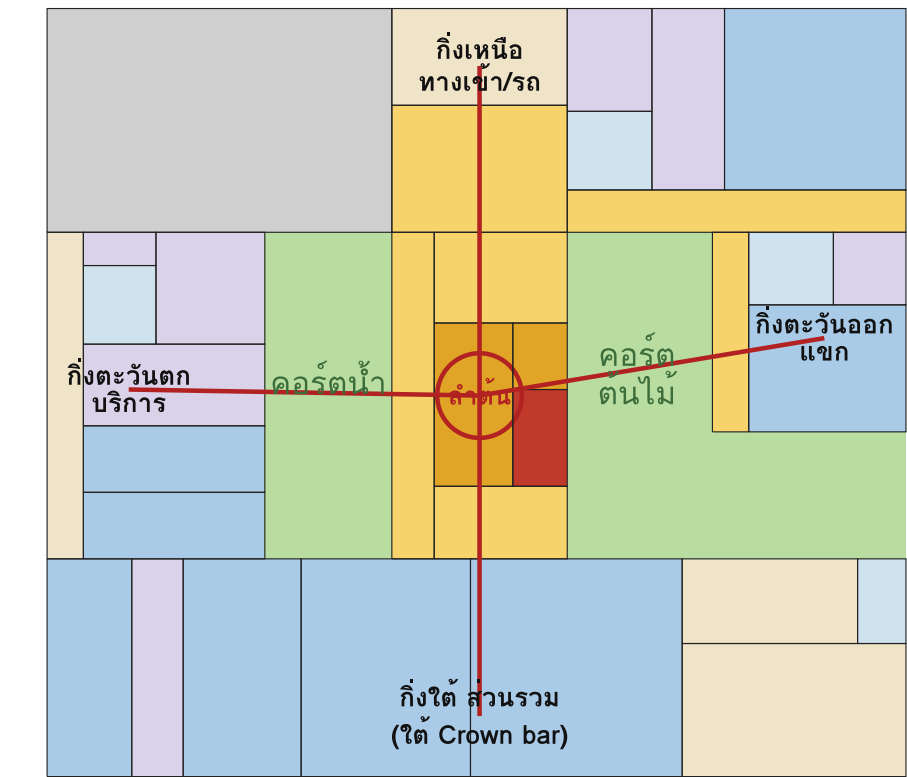


มุมมองทิศตะวันออกเฉียงใต้ — สระน้ำเกลือ ศาลาริมสระ หลังคาสวน และครีปไม้ฝั่งตะวันออก



คอร์ตต้นไม้ (ปอด Termite) — ลมเย็นจากर्मไม้เข้าสู่ห้องลมแกนลำต้น

โดอะแกรม TERMITE -> BREATH: ลมเย็นจากคอร์ต -> โถง -> ปล่องลมลำต้น -> ออก +14.00 (รูปตัด B-B, 1:250)

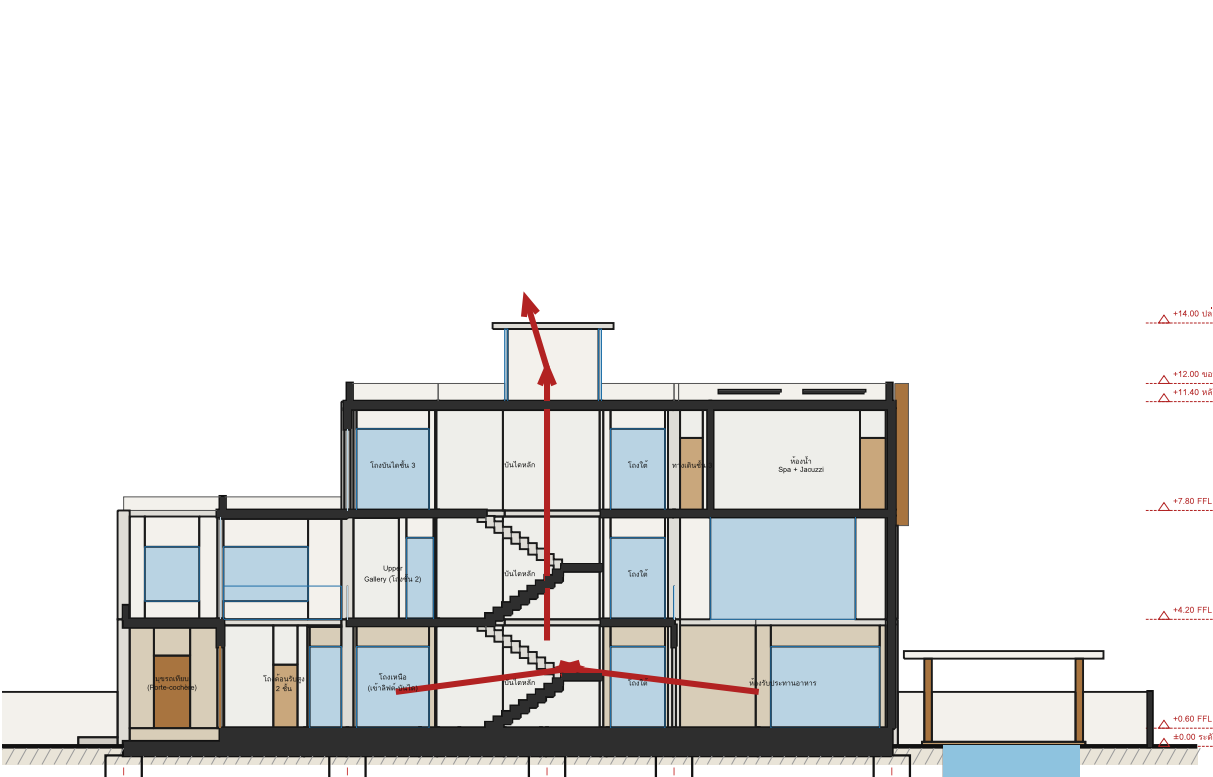

ลูกศรแดง = ทิศทางลมที่ "ดึงใจ" ตามหลัก slack effect — สีไม้ได้พิสูจน์ด้วย CFD

GENWEAVE 6 ระบบ -> องค์ประกอบในแบบ v3

ระบบชีวภาพ	สิ่งที่อยู่ในแบบ v3
01 TERMITE -> BREATH	ปล่องลมแกนลำต้น 1.80x3.20 ม. หอคู 3 ชั้นถึง +14.00 (solar chimney กรอง)
02 TREE -> WEAVE	ไม้มีทางเดินยาว: ลำต้น (ป่นโค+สฟล+ปล่อง) แยก 4 กิ่ง
03 BONE -> STRUCTURE	กริด 8 x 5 เมตร ช่วง 2.50-5.80 ม. เสา 0.40x0.40
04 CACTUS -> SKIN	ครีปไม้ 40x50 @600 ปิดได้ทั้งวันตา ของ Crown bar
05 BEETLE -> WATER	หลังคา 701 ตร.ม. ระบบหลังโซลาร์คัลน้ำ 20 ตบ.ม.
06 MANGROVE -> ECOSYSTEM	ยกพื้น +0.80 ม. จากถนน · ร่องขับน้ำ 1.00 ม. ปิดได้ทิศตะวันออก

ระบบชีวภาพ	บทบาท / สิ่งที่มีต่อผู้อยู่
01 TERMITE -> BREATH	ลมเข้าจากคอร์ตต้นไม้คอร์ตน้ำ ออกทางปล่อง (stack) — คัดพิสูจน์ด้วย CFD
02 TREE -> WEAVE	กิ่งเหนือทางเข้า/ออก ทิศตะวันตกบริการ ทิศวันออกแขก กิ่งใต้สวนรวม
03 BONE -> STRUCTURE	Crown bar ชั้น 3 วางบนแนวเสา A/B; คานถ้ำยาวโรงรถ 11.40 ม.
04 CACTUS -> SKIN	กันสาดไม้สีก 1.20 ม. ที่ +3.50 หน้าห้องนั่งเล่น-อาหาร; ผนังชั้น 1 หน้าสวนรวม
05 BEETLE -> WATER	สระน้ำเกลือ 16.0x4.5 ม. + บ่อน้ำคอร์ตน้ำ เป็นตัวลดอุณหภูมิผิวอากาศ
06 MANGROVE -> ECOSYSTEM	ตั้งระดับขับน้ำคัลน้ำหา · หลังคาสวน 460 ตร.ม. (66% ของหลังคา)

ที่มาของแนวคิด (แยกข้อเท็จจริง / การตีความ)

ข้อเท็จจริง: เอกสาร GENWEAVE ในโพเดรัซของพีจี (00-06 + Master) กำหนด 6 ระบบ และหลัก "ใช้ logic ของธรรมชาติ ไม่ copy รูปร่าง" (ข้อ 17)
ข้อเท็จจริง: README ของเอกสารระบุว่าเป็น ChatGPT Deep Research — เราไม่ได้วางตัวเลข/งานวิจัยที่อ้างในเอกสารนี้เข้า
การตีความของเรา: แปล "Central Trunk + Branching Spaces" (ข้อ 08) เป็นแกนป่นโคกลาง 5.80 ม. + 4 ถัง + สะพานระลอก 2 แห่ง
การตีความของเรา: "Crown bar" ชั้น 3 = เรือนยอดไม้ที่แปลให้สวนด้านข้าง — ไม่ใช่ข้อความในเอกสารต้นฉบับ
ไม่ได้ฉากรนของสถาปนิกรายใด และไม่ได้วางเลขระบุประสิทธิภาพที่ไม่ได้คำนวณในชุดนี้

รายงานข้อจำกัด (ตรงไปตรงมา)

- โปรแกรมซัดกับเอง: "Upper Master Terrace" ระบุชั้น 2 แต่ Master Suite อยู่ชั้น 3 -> วารหะเพียง 28.08 ตร.ม. ชั้น 3 คัดห้องนอน (ถ้าอยู่ชั้น 2 จะขาดจากห้องนอน)
- โปรแกรมให้ห้อง MEP/Generator อยู่ชั้น 2 -> ย้ายลงชั้น 1 (15.96 ตร.ม.) ติดฐานบริการ: เครื่องเย็นไฟวางลานบริการในกล่องเก็บเสียง (น้ำหนัก-น้ำเย็น-เสียง-ซ่อมบำรุง)
- ความสูงเฉลี่ยในโปรแกรม 2.80 ม. -> ใช้ตั้งแต่พื้น 3.60 ม. (ใบโรง 3.00 ม. หลังหักพื้น 0.20 + ส่วนหาระบบ 0.40) อาคารสูงถึงหลังคา 11.40 ม.
- GFA แบบ 1,077.78 ตร.ม. vs โปรแกรม 939.55 (+138.23 = +14.7%); ทางสีจริงจริง 286.16 ตร.ม. (โปรแกรมเมื่อ 89.88) จากลำต้น-สะพาน-โรงรถคอร์ต + มุขรถเทียบ 18.56 + ห้องเก็บจักรยาน 9.52 + ห้องอาบน้ำชั้นสระ 4.48 ที่ไม่มีในโปรแกรม; NUA ห้องตามโปรแกรม 770.46 vs 749.00 (+21.46).
- ห้องไม้บ้าน 2 ห้อง 13.20 ตร.ม./ห้อง (รวม +4.40) เพราะต้องกว้างคอร์ต 6.00 ม. จากฐานบริการถึงคอร์ต เพื่อให้มีช่องเปิด 2 ด้าน, ห้องไม้บ้านข้างทางฐานบริการ (หลังคาคลุม ไม่เปิดล้อม)
- โรงรถ 4 คัน กว้าง 11.40 ม. = ช่องละ 2.85 ม. (แต่สำหรับ SUV เบียดช่วง 3 คัน) และต้องใช้คานไม้ยาวระลอก 11.40 ม. (PTAเหล็ก) รับหลังคาสวน
- หาลาก 1:12 ยาว 7.20 ม. = ความชันสูงสุดพอดี: ประตูโรงรถ->โถง ตัวรถคัน 0.45 ม. ใช้ชั้นป่นโค 3 ชั้น (ผู้ใช้รถจะต้องเข้าทางมุขรถเทียบ+ทางลาด)
- ห้องสีพื้นเอปโลไม้สี 10% ใช้ฟิล์มระบาย (ล.39 ซม. 6 วรรคต่อ); ห้องบ้านแขก (Powder), ห้องโถงไม้ / ลีการ์, ห้องไม้พักผ่อน, Walk-in Pantryห้องเย็น, Walk-in Dressing (His & Hers)
- ห้องโถงเย็นเคอร์ลิค 6.00 ม. จากหน้าทาง (ฝั่งใจไม้ดี) · ห้องสะพานชั้น 3 สีก 4.05 ม. (ใกล้คอร์ต 4.20)
- คอร์ตเปิดฟ้า 2 แห่ง (124.08 ตร.ม.) ต้องมีระบายระบายน้ำตะแกรงของส้วม ต้องดึงน้ำขึ้นโคคอร์ตน้ำ
- ห้องสูง 2 ชั้น 7.20 ม. (อาหาร-นั่งเล่น 90.72 ตร.ม.) การแบ่งรัฐ: ลมธรรมชาติปล่อง Termite ช่วยได้เฉพาะช่วงอากาศเย็น ไม่แทนแอร์ในโรงรถ
- หลังคาสวน 460 ตร.ม. น้ำหนักคัลน้ำ ~300 กก./ตร.ม. ต้องสัดไม้โครงสร้าง: ครีปไม้ 119 ชิ้นลวาร์โซลูชันเดิมลายไม้เพื่อลดการบำรุงรักษา
- ไม้ทรงพื้นเมืองรวมของที่ตั้ง (FAROSR/ระยอง) — ต้องตรวจก่อนขึ้นของอนุญาต

H3A DESIGN AND BUILD

X-UNIT Architecture Lab

โครงการ

WELL-GENWEAVE 40x40 v3

Executive Luxury Villa

บ้านเดี่ยว 3 ชั้น ผ่านเกณฑ์

WELL for Residential (เจดนา)

ที่ดิน 40.00 x 40.00 ม. = 400 ตร.ว.
ถนนสาธารณะ 8.00 ม. ทิศเหนือ

แนวคิด

GENWEAVE: ลำต้น (แกนป่นโค+ปล่อง

Termite) แยกกิ่ง 4 ทิศ รอบคอร์ต 2 แห่ง

Crown bar ชั้น 3 = เรือนยอดป่นโค

ระดับ

±0.00 ถนน · F1 +0.60 · F2 +4.20

F3 +7.80 · หลังคา +11.40

parapet +12.00 · ปล่อง +14.00

หมายเหตุ

- หน่วยงานเป็นลิ้มรส เว้นแต่ระบุ
- ระดับอ้างอิงถนนหน้าที่ดิน ±0.00
- หารั้วรถขนรถจากแบบ ใช้ตัวเลขกำกับ
- แบบระดับ Design Development
- ต้องให้สถาปนิกและวิศวกรผู้ได้รับใบอนุญาตตรวจสอบและลงนามก่อนยื่นขออนุญาต

ชื่อแผ่น

แนวคิด GENWEAVE

+ โครงสร้าง + รายงานข้อจำกัด

มาตรฐาน: ไม่มีมาตรฐาน

วันที่ 1 ค.ค. 2569 ฉบับ v3 / DD

ข้อ	รายการ	คำนวณแบบ	เกณฑ์	ผล
ข้อ 20	ห้องแม่บ้าน 1	13.20 ตร.ม. (จำนวน 2.20)	>= 8.00 ตร.ม.	ผ่าน
ข้อ 20	ห้องแม่บ้าน 2	13.20 ตร.ม. (จำนวน 2.20)	>= 8.00 ตร.ม.	ผ่าน
ข้อ 20	ห้องแม่บ้านชุดีสุภาว	21.84 ตร.ม. (จำนวน 4.20)	>= 8.00 ตร.ม.	ผ่าน
ข้อ 20	ห้องนอน Junior Suite 2	22.80 ตร.ม. (จำนวน 4.20)	>= 8.00 ตร.ม.	ผ่าน
ข้อ 20	ห้องนอน Junior Suite 3	21.84 ตร.ม. (จำนวน 4.20)	>= 8.00 ตร.ม.	ผ่าน
ข้อ 20	ห้องนอน Master Suite	47.52 ตร.ม. (จำนวน 6.60)	>= 8.00 ตร.ม.	ผ่าน
ข้อ 22	ความสูงบันไดห้อง (FF 3.60 - ชั้น 0.20 - มั้วฯ)	3.00 ม.	>= 2.60 ม.	ผ่าน
ข้อ 22	ห้องสุขา 2 ชั้น (โถงอาทมาลิ้น)	6.60 ม.	>= 2.60 ม.	ผ่าน
ข้อ 23	อุกถึ	180 มม.	<= 200	ผ่าน
ข้อ 23	กานะ	280 มม.	>= 220	ผ่าน
ข้อ 23	ความกว้างบันได	1200 มม.	>= 800	ผ่าน
ข้อ 23	จานชักโครก (ฝัก)	1500 มม.	> ความกว้าง 1200	ผ่าน
ข้อ 23	จานชักโครก (ฝัก)	1580 มม.	>= 1200	ผ่าน
ข้อ 23	ชักโครกโถยู่ขวาง	1.80 ม. (10 ชั้)	<= 3.00 ม.	ผ่าน
ข้อ 23	ระบะบันไดเหล็กบันได	>= 3.22 ม.	>= 1.90 ม.	ผ่าน
ข้อ 23	2R+T	640 มม.	800-650	ผ่าน
ข้อ 33	ร็ว (นั้ดอ์บอ์บอ์)	58.5% (คณณ 664.30 ตร.ม.)	>= 30%	ผ่าน
ข้อ 33	ร็ว (นั้ดอ์บอ์บอ์) 124.08 ตร.ม.	50.7%	>= 30%	ผ่าน
ข้อ 50	ร็ว (นั้ดอ์บอ์บอ์) (นั้ดอ์บอ์บอ์) 11.40 ม.)	5.80 ม. (D05 F1 ตรั้บ) (สั้บอ์บอ์)	>= 3.00 ม.	ผ่าน
ข้อ 50	ร็ว (นั้ดอ์บอ์บอ์) (นั้ดอ์บอ์บอ์) 1.60 ม.	1.60 ม.	>= 0.50 ม.	ผ่าน
ข้อ 50	ร็ว (นั้ดอ์บอ์บอ์) (นั้ดอ์บอ์บอ์) 5.80 ม.	5.80 ม.	>= 3.00 ม. (นั้ดอ์บอ์บอ์, ส)	ผ่าน
รณนั้ดอ์บอ์บอ์	รณนั้ดอ์บอ์บอ์ (นณ 8.00 ม.)	6.00 ม.	>= 1/10 ความกว้างนณ = 0.8	ผ่าน


* ร่นแนวถนน: อาคารสูงไม่เกิน 15 ม. ถนน 6-20 ม. ใช้ 1/10 ของความกว้างถนน (ตรวจเข้ากับข้อบัญญัติท้องถิ่น/ผังเมืองรวม)

ชั้น	ปิดยอด	ตั้งภายในยอด	ยอดจริง	รวม ตร.ม.
ชั้น 1	432.60	80.32	84.36	597.28
ชั้น 2	204.20	0.00	-	204.20
ชั้น 3	213.12	28.08	-	241.20
ศาลาพักผ่อน	-	35.10	-	35.10
รวม	849.92	143.50	84.36	1077.78
โปรแกรม				939.55
ส่วนต่าง				+138.23 (+14.7%)

รายการ	ค่า
ต้นทุน	1,600.00 ตร.ม. (400 ตร.ว.)
พื้นที่อาคารดิน (รวมเสา)	664.30 ตร.ม. (41.5%)
ที่ว่าง น็อคเอาท์	58.5% (เกณฑ์ >= 30%)
ที่ว่าง ไม่บ่มลอร์ด	124.08 ตร.ม.
FAR (GFA บล็อก / พื้น)	50.7%
ความสูงอาคาร (ลิ้นชักหลัง)	0.53 : 1
	11.40 ม. (<15 ม. ไม่เป็นอาคารสูงตามกฎหมาย)

วัสดุ	สูตร (บาทต่อตร.ม.)	คำนวณหา
(ก) ดักรวยแหลมมาตรฐาน	คิดต่อผืน 849.92 x 22,000 + ปริมาณเหล็ก 143.50 x 11,000 + จอดรถ 84.36 x 8,000	20.95
(ข) ดักรวยแหลม luxury	คิดต่อผืน x 30,000 + ปริมาณเหล็ก x 15,000 + จอดรถ x 12,000	28.66
(ค) ดักรวยเดี่ยว (วัสดุเดียวกับโปรแกรม)	GFA 1077.78 x 30,000	32.33
งานเชื่อมอาคาร	สูตร 72 ตร.ม. x 35,000 + PV 23.1 kWp x 45,000 + ภูมิทัศน์บริเวณบ่อ 2.50 ล.	6.06
โปรแกรม SPACE	939.55 x 30,000 (ช่วง 24.80-35.23 ลาน)	28.19


ค่าเฉลี่ย "อยู่ในงบโหล" ขึ้นกับวิธีคิด ไม่ใช่ขึ้นกับแบบ: (ข) 28.66 ล้าน อยู่ในช่วงโปรแกรมน; (ค) 32.33 ล้าน อยู่ในช่วงแต่สูงกว่าค่ากลาง; รวมงานนอกอาคาร (ค)+6.06 = 38.39 ล้าน เกินช่วงงบ
ยังไม่รวม: ฐานราก/เสาเข็ม (ขึ้นกับผลเจาะสำรวจดิน), เฟอร์นิเจอร์ลอยตัว, ภาษี/ค่าธรรมเนียม, ค่าออกแบบ

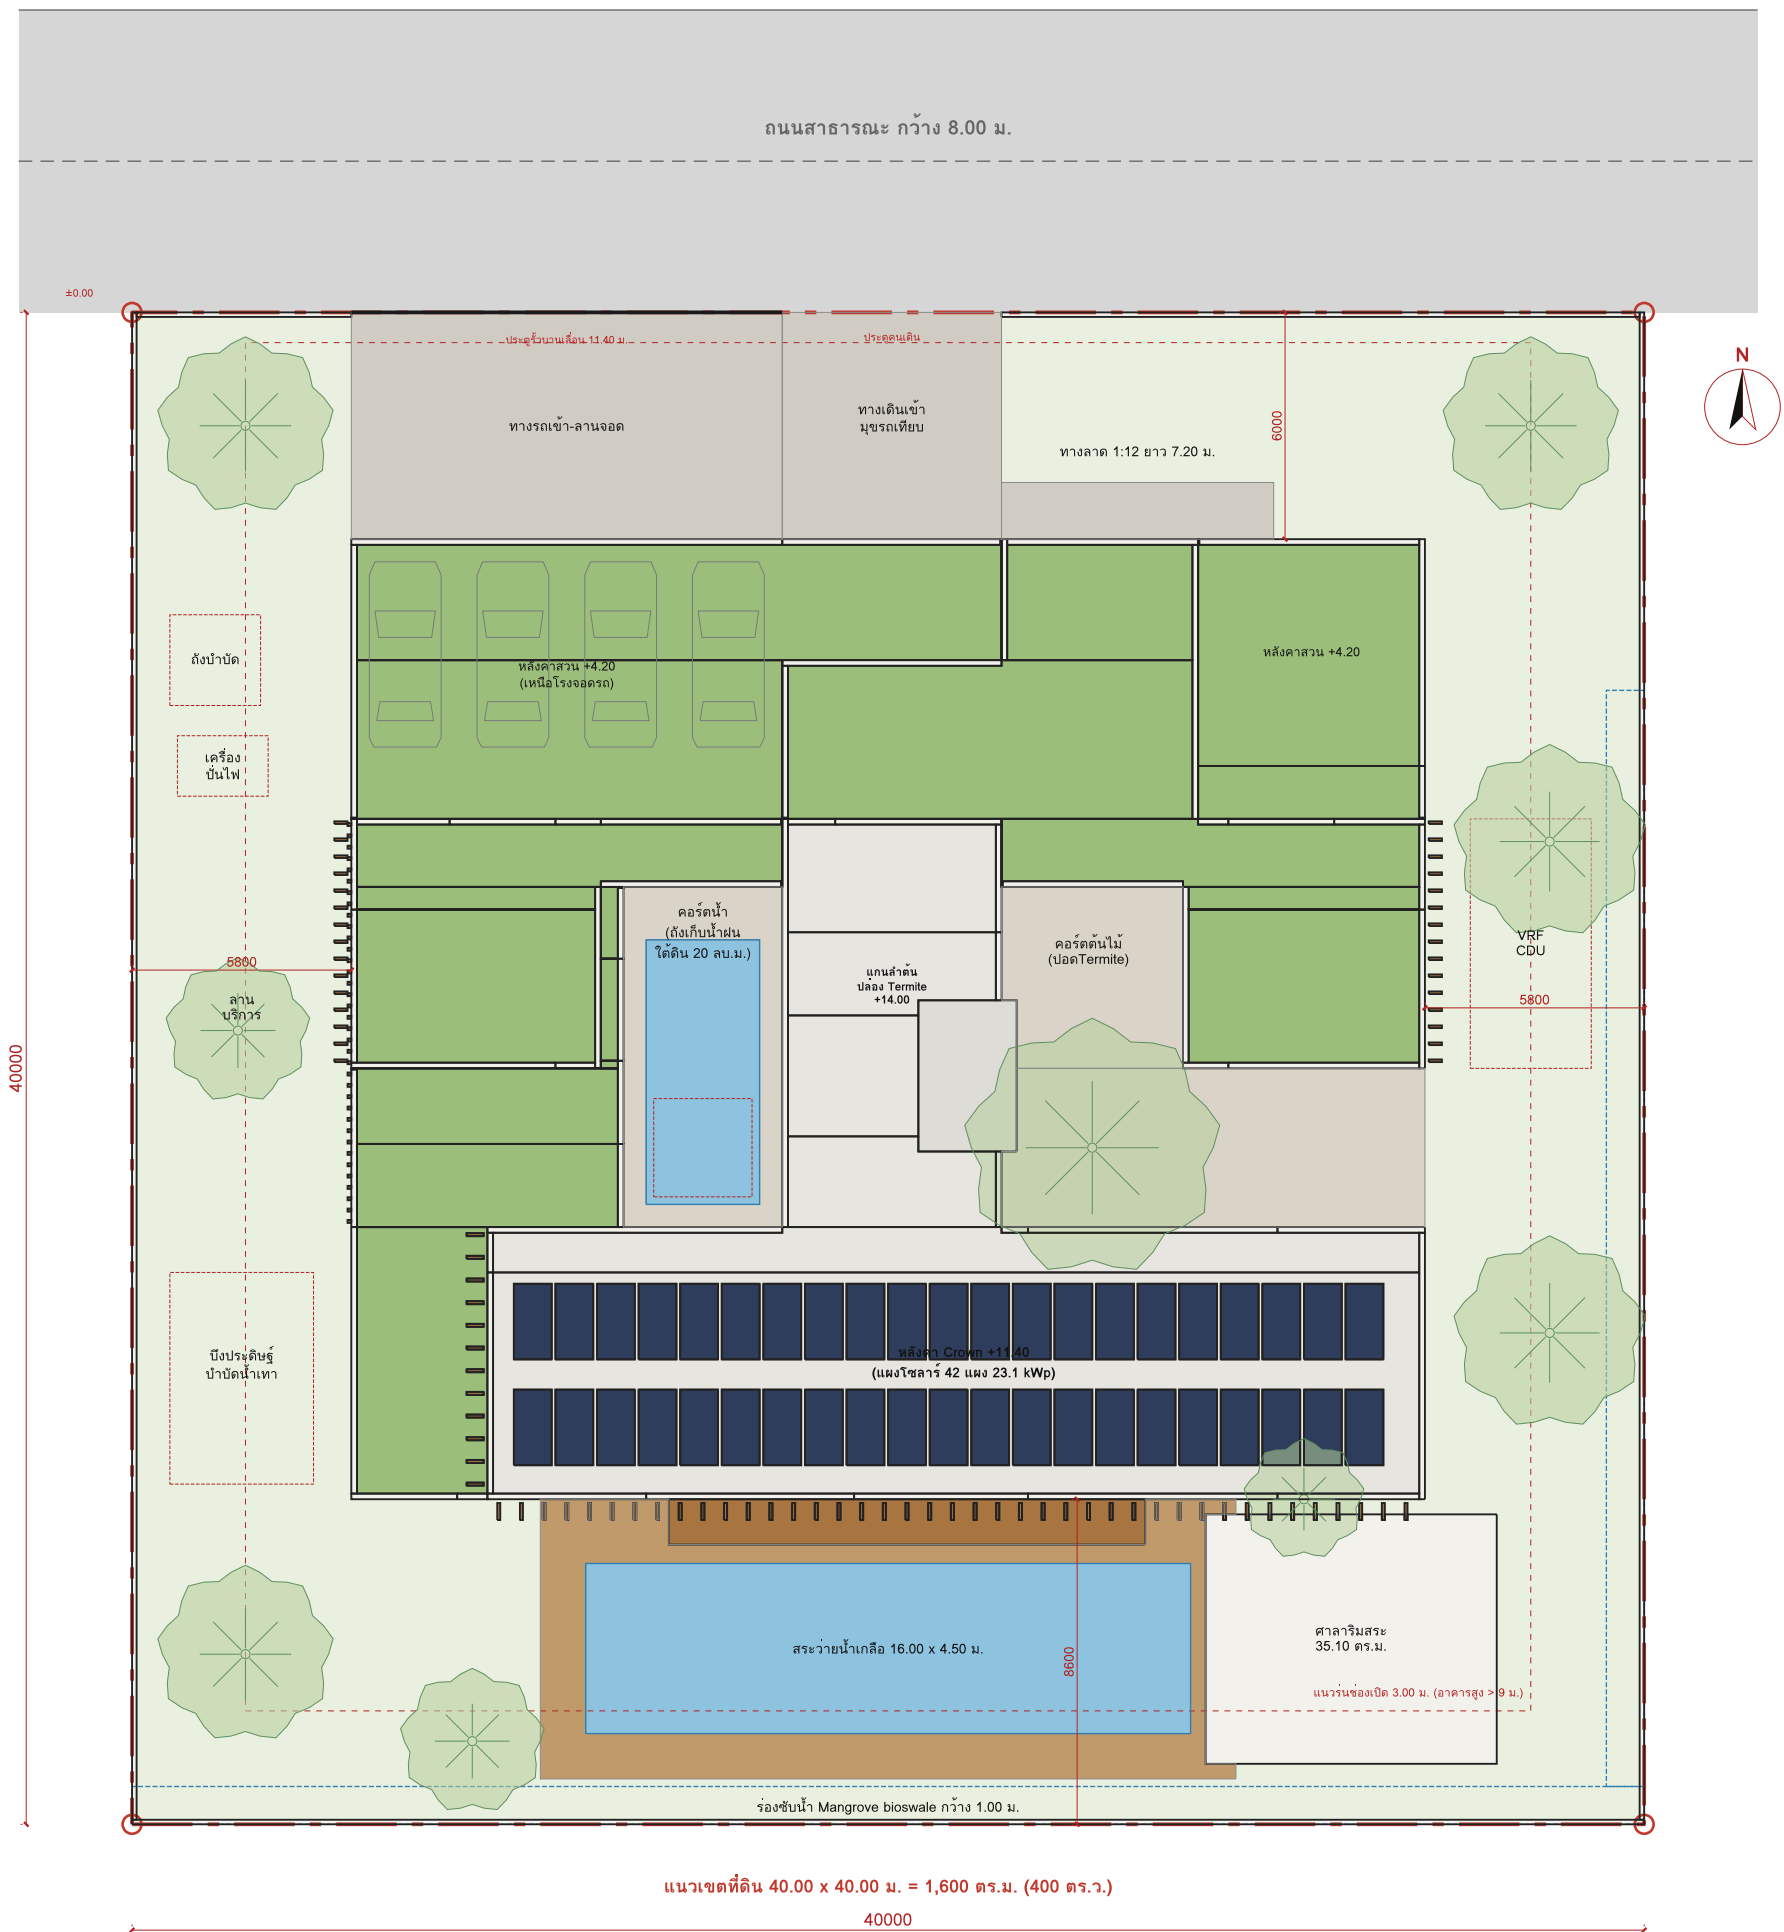

[illegible]

- หน่วยเป็นมิลลิเมตร เว้นแต่ระบุ
- ระดับอ้างอิงถนนหน้าที่ดิน ± 0.00
- ห้ามวัดขนาดจากแบบ ใช้ตัวเลขกำกับ
- แบบระดับ Design Development
ต้องให้สถาปนิกและวิศวกรผู้ได้รับ
ใบอนุญาตตรวจสอบและลงนาม
ก่อนยื่นขออนุญาต

วันที่ 1 ต.ค. 2569 ฉบับ v3 / DD

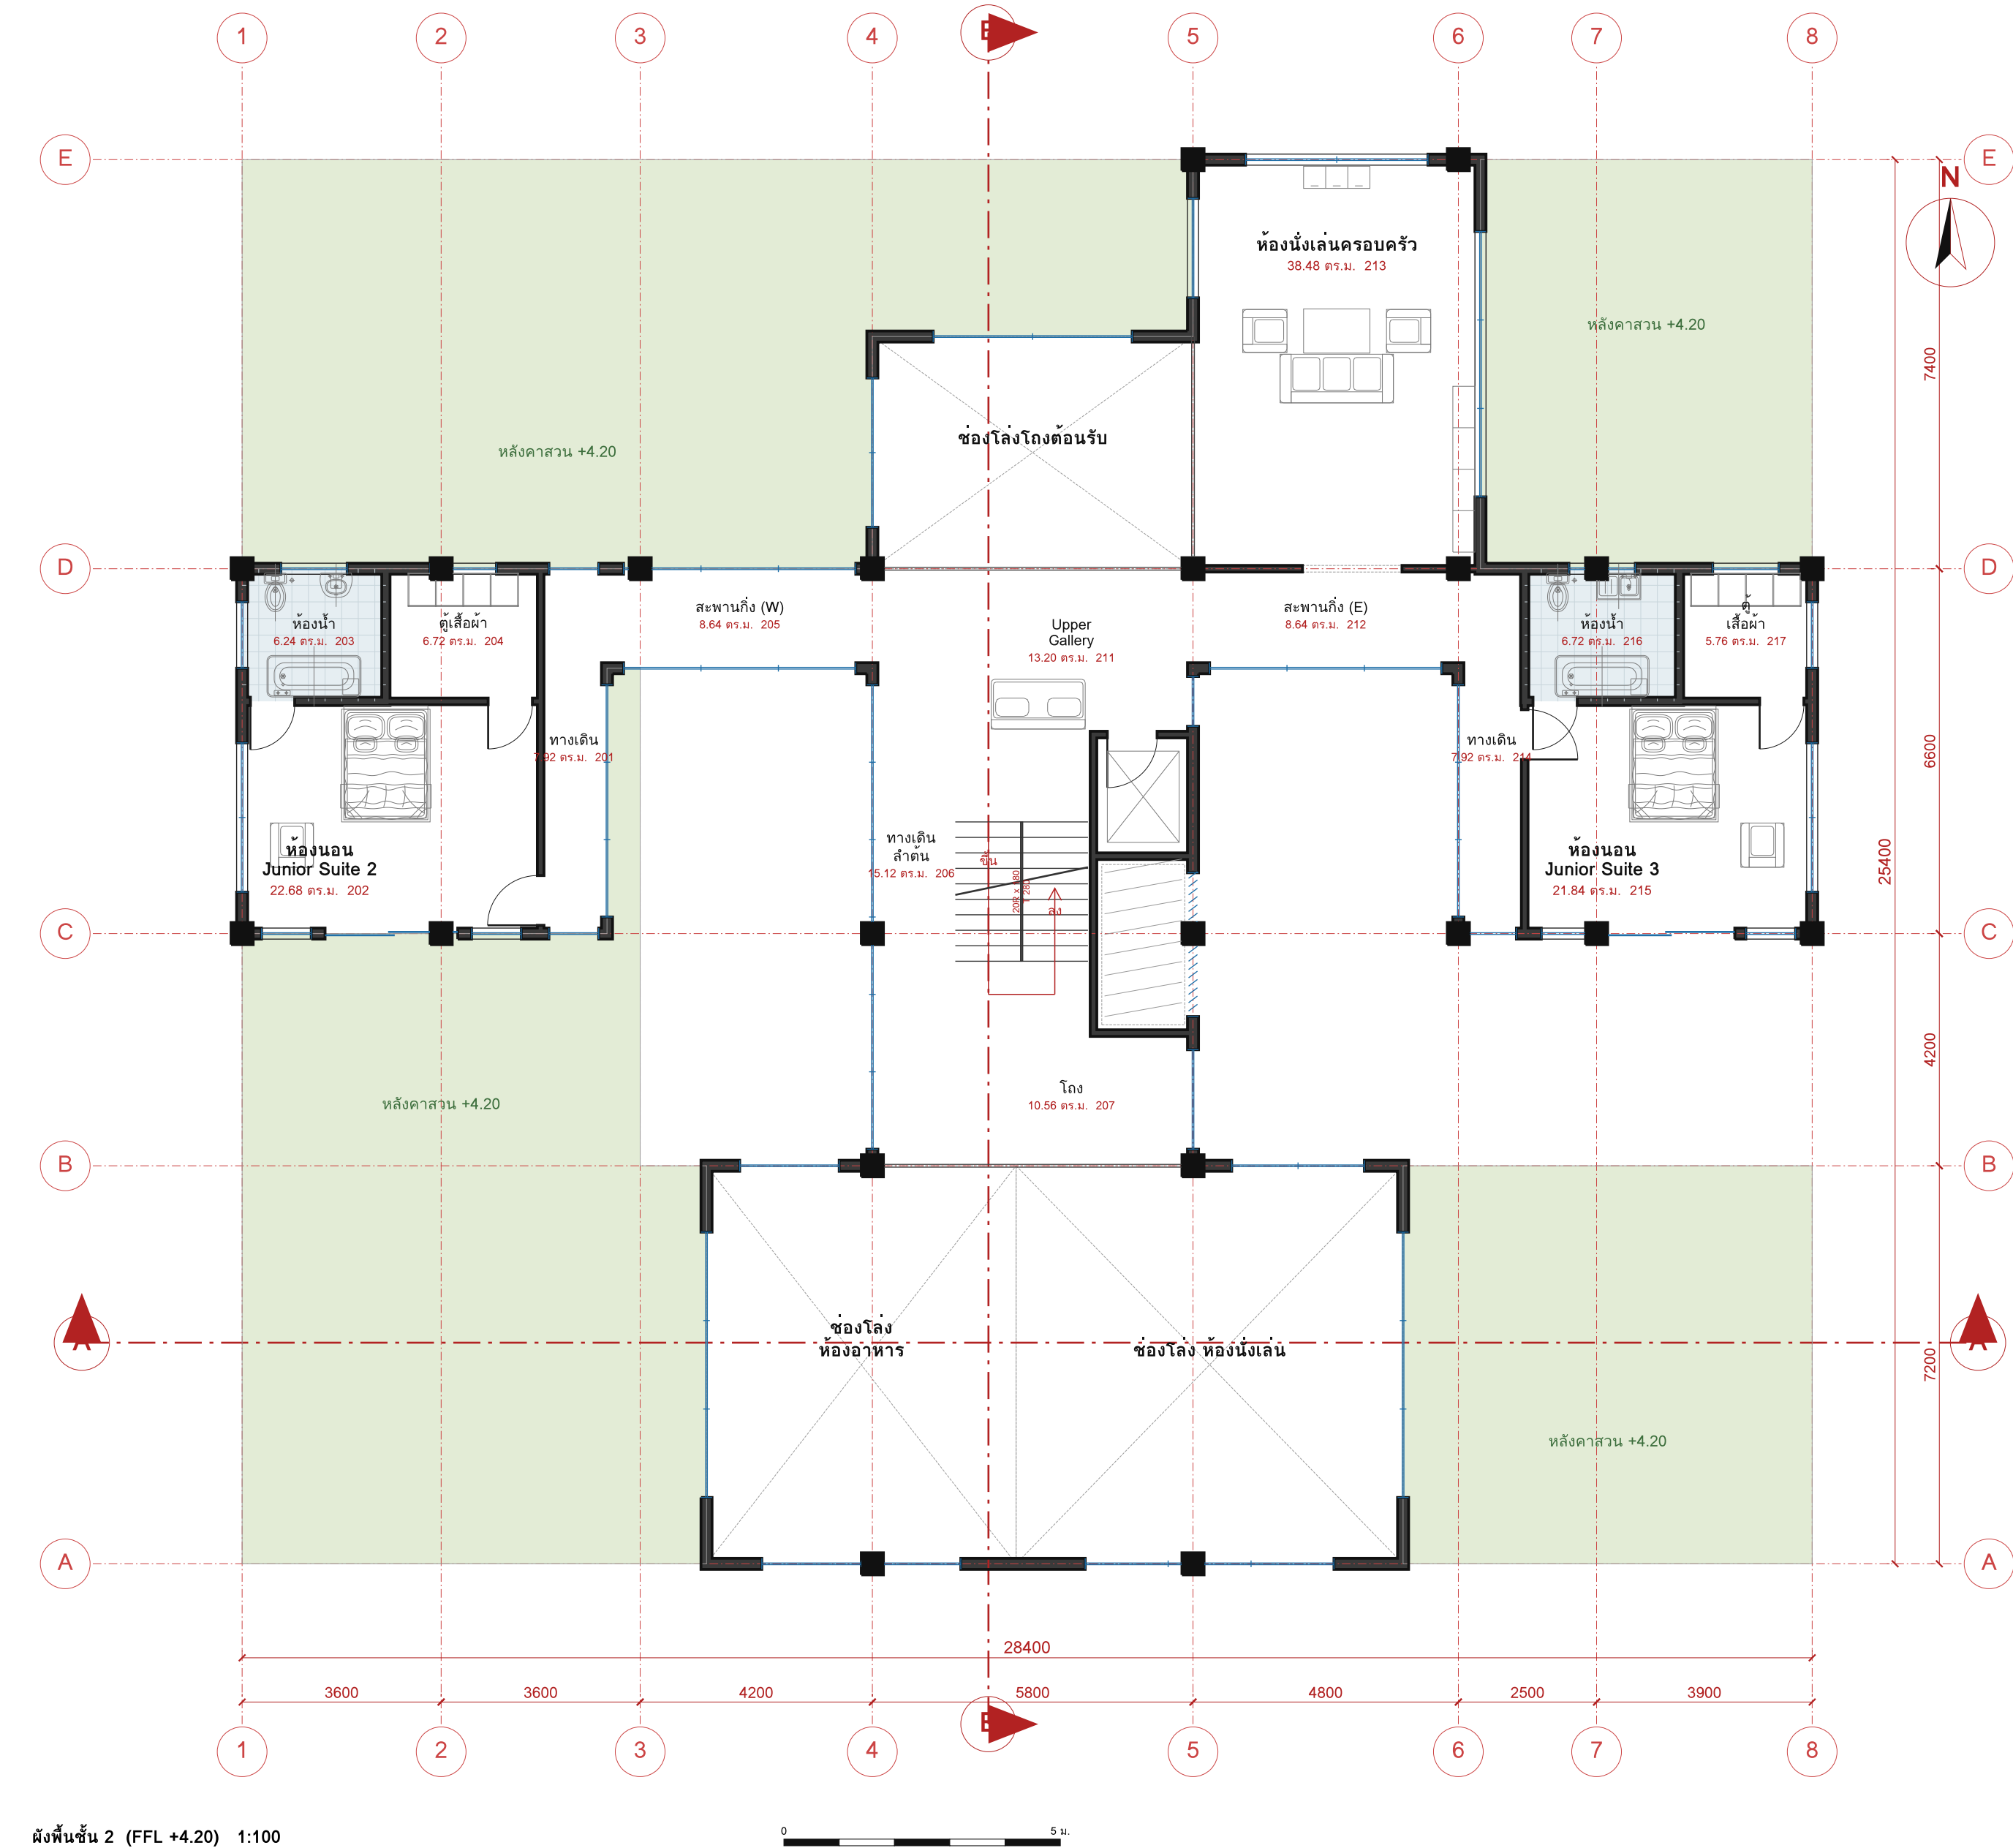

ผังพื้นชั้น 2 (FFL +4.20) 1:100

ตารางห้อง ชั้น 2

รหัส	ชื่อ	ขนาด ม.	รวม	ประเภท
201	ทางเดิน Junior Suite 2	1.20 x 6.60	7.92	สัญจร
202	ห้องนอน Junior Suite 2	5.40 x 4.20	22.68	ห้องนอน
203	ห้องน้ำ Junior Suite 2	2.60 x 2.40	6.24	ห้องน้ำ
204	ตู้เสื้อผ้า Junior Suite 2	2.80 x 2.40	6.72	บริการ
205	สะพานกิ่งตะวันตก	4.80 x 1.80	8.64	สัญจร
206	ทางเดินลำต้น (Trunk)	1.40 x 10.80	15.12	สัญจร
207	โถงใต้	4.40 x 2.40	10.56	สัญจร
208	เก็บของใต้	2.80 x 5.40	14.04	เก็บของ
209	เก็บของ Terrace	1.80 x 3.20	5.76	เก็บของ
210	รับแขกบ้าน	1.80 x 2.20	3.96	รับแขก
211	Upper Gallery (โถงชั้น 2)	4.40 x 3.00	13.20	สัญจร
212	สะพานกิ่งตะวันออก	4.80 x 1.80	8.64	สัญจร
213	ห้องนั่งเล่นครอบครัว	5.20 x 7.40	38.48	ห้องนั่งเล่น
214	ทางเดิน Junior Suite 3	1.20 x 6.60	7.92	สัญจร
215	ห้องนอน Junior Suite 3	5.20 x 4.20	21.84	ห้องนอน
216	ห้องน้ำ Junior Suite 3	2.80 x 2.40	6.72	ห้องน้ำ
217	ตู้เสื้อผ้า Junior Suite 3	2.40 x 2.40	5.76	บริการ

ส่วน	ชั้น 2	รวม
พื้นที่ใช้สอย		204.20
ที่จอดรถ		0.00
รวม		204.20

หมายเหตุ

- สะพานระหว่าง 2 แห่ง (กิ่ง W / กิ่ง E) กว้าง 1.80 ม. ข้ามคอร์ริดอร์ เชื่อม Upper Gallery /u Junior Suite
- ห้องนั่งเล่นครอบครัวเชื่อมโถงต้อนรับสู่ 2 ชั้นผ่านราวจาก 1.10 ม.
- ช่องโถงเหนือห้องอาหาร-นิตยสาร (โครงสร้าง Crown bar ชั้น 3 อยู่เหนือ)
- หลังคาส่วน +4.20 เหนือโถงใต้และโถงใต้บริการ — เชื่อมถึงเพื่อบำรุงรักษาทางช่องเปิดบนหลังคา
- ครีมนิยมนิยมนิตยสารและโถง Junior Suite ยังแตกต่างกัน

H3A DESIGN AND BUILD

X-UNIT Architecture Lab

โครงการ

WELL-GENWEAVE 40x40 v3

Executive Luxury Villa
บ้านเดี่ยว 3 ชั้น ผ่านเกณฑ์
WELL for Residential (เจดนา)

ที่ดิน 40.00 x 40.00 ม. = 400 ตร.ว.
ถนนสาธารณะ 8.00 ม. ทิศเหนือ

แนวคิด

GENWEAVE: ลำต้น (แกนบันได+ปล่อง
Termite) แดกกิ่ง 4 ทิศ รอบคอร์ริดอร์ 2 แห่ง
Crown bar ชั้น 3 = เรือนยอดกิ่งแดด

ระดับ

±0.00 ถนน · F1 +0.60 · F2 +4.20
F3 +7.80 · หลังคา +11.40
parapet +12.00 · ปล่อง +14.00

หมายเหตุ


- หน่วยงานเป็นผลิตภัณฑ์ เวนเตอร์
- ระดับอ้างอิงถนนหน้าที่ดิน ±0.00
- ห้ามวัดขนาดจากแบบ ใช้ตัวเลขกำกับ
- แบบระดับ Design Development
- ต้องให้สถาปนิกและวิศวกรผู้ได้รับ
ใบอนุญาตตรวจสอบและลงนาม
ก่อนยื่นขออนุญาต

ชื่อแผ่น

ผังพื้นชั้น 2
(FFL +4.20)

มาตราส่วน 1:100

วันที่ 1 ค.ค. 2569 ฉบับ v3 / DD

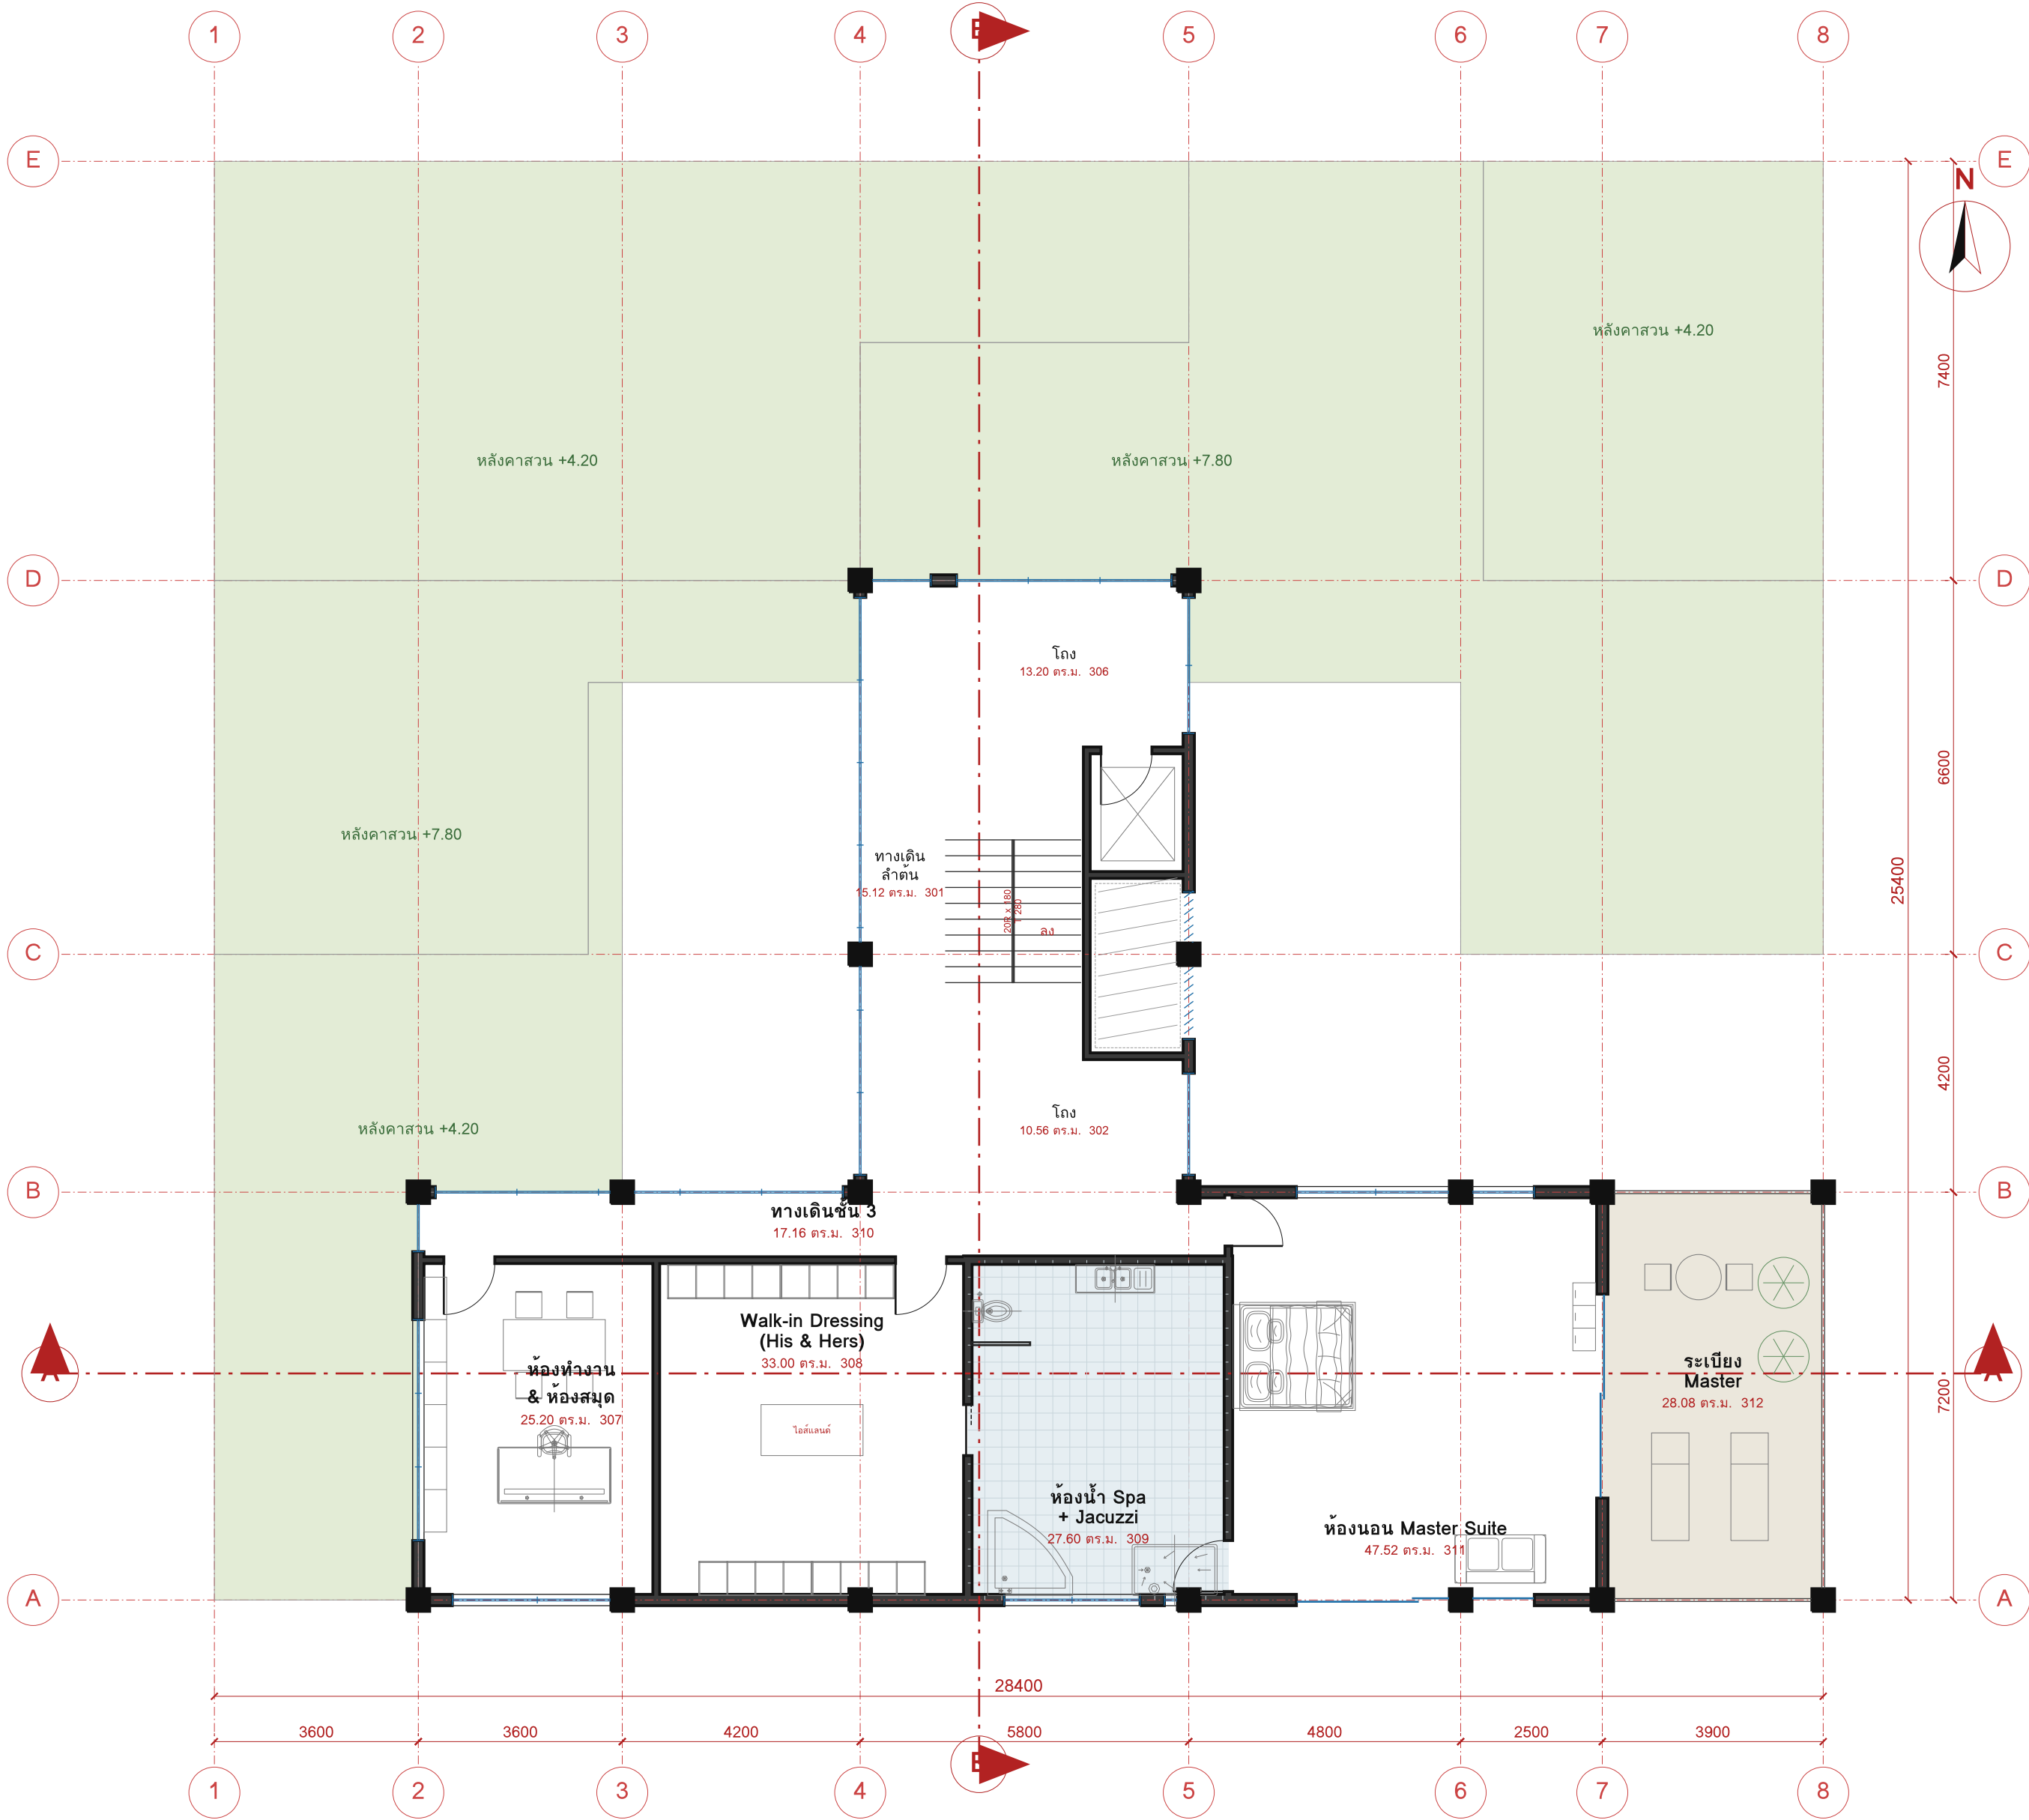

ผังพื้นชั้น 3 (FFL +7.80) 1:100

ตารางห้อง ชั้น 3

ร.บ.ค.	ห้อง	ขนาด ม.	ตร.ม.	ประเภท
301	ทางเดินลำต้น (Trunk)	1.40 x 10.80	15.12	สักรู
302	โถง	4.40 x 2.40	10.56	สักรู
303	บันไดเหล็ก	2.60 x 5.40	14.04	บันได
304	ปล่องลม Termite	1.80 x 3.20	5.76	ปล่องลม
305	ลิฟต์บ้าน	1.80 x 2.20	3.96	ลิฟต์
306	โถงบันไดชั้น 3	4.40 x 3.00	13.20	สักรู
307	ห้องทำงาน & ห้องสมุด	4.20 x 6.00	25.20	ห้องใช้งาน
308	Walk-in Dressing (His & Hers)	5.50 x 6.00	33.00	ตู้เสื้อผ้า
309	ห้องน้ำ Spa + Jacuzzi	4.80 x 6.00	27.60	ห้องน้ำ
310	ทางเดินชั้น 3	14.30 x 1.20	17.16	สักรู
311	ห้องนอน Master Suite	6.60 x 7.20	47.52	ห้องใช้งาน
312	ระเบียบ Master (หลังคาคลุม)	3.90 x 7.20	28.08	ที่ภายนอก

รวม	ตร.ม.
พื้นที่ปิดล้อม	213.12
ที่ภายนอก	28.08
จอร์ด	0.00
รวม	241.20

หมายเหตุ

- Crown bar: ห้องทำงาน-Walk-in-ห้องน้ำ Spa-ห้องนอน Master-ระเบียบ เรือสวนนอก->สวนนอก ทางเดินด้านเหนือ
- ต้นไม้ 80x450 คู่600 ทางเหนือ 100-550 มม. ด้านใต้และสวนนอกทางเหนือ (บันไดเหล็ก-บันได)
- ระเบียบ Master 28.08 ตร.ม. หลังคาคลุม (หลังคา Crown ขึ้นคลุม) ราวระลอก 3 ด้าน
- โปรแกรมระบุระเบียบ Master ชั้น 2 — บ้านชั้น 3 (ดู A-01 ข้อ 1)

H3A DESIGN AND BUILD

X-UNIT Architecture Lab

โครงการ

WELL-GENWEAVE 40x40 v3

Executive Luxury Villa

บ้านเดี่ยว 3 ชั้น ผ่านเกณฑ์

WELL for Residential (เจดุนา)

ที่ดิน 40.00 x 40.00 ม. = 400 ตร.ว.

ถนนสาธารณะ 8.00 ม. ทิศเหนือ

แนวคิด

GENWEAVE: ลำต้น (แกนบันได+ปล่อง

Termite) แยกกิ่ง 4 ทิศ รอบคอร์ริด 2 แห่ง

Crown bar ชั้น 3 = เรือนยอดกิ่งเจดุน

ระดับ

±0.00 ถนน · F1 +0.60 · F2 +4.20

F3 +7.80 · หลังคา +11.40

parapet +12.00 · ปล่อง +14.00

หมายเหตุ

- หน่วยงานเป็นผลิตภัณฑ์ เวนเตอร์
- ระดับอ้างอิงถนนหน้าที่ดิน ±0.00
- ห้ามรื้อถอนจากแบบ ใช้ตัวเลขกำกับ
- แบบระดับ Design Development
- ต้องให้สถาปนิกและวิศวกรผู้ได้รับใบอนุญาตตรวจสอบและลงนามก่อนยื่นขออนุญาต


ชื่อแผ่น

ผังพื้นชั้น 3

(FFL +7.80)

มาตราส่วน 1:100

วันที่ 1 ค.ค. 2569 ฉบับ v3 / DD

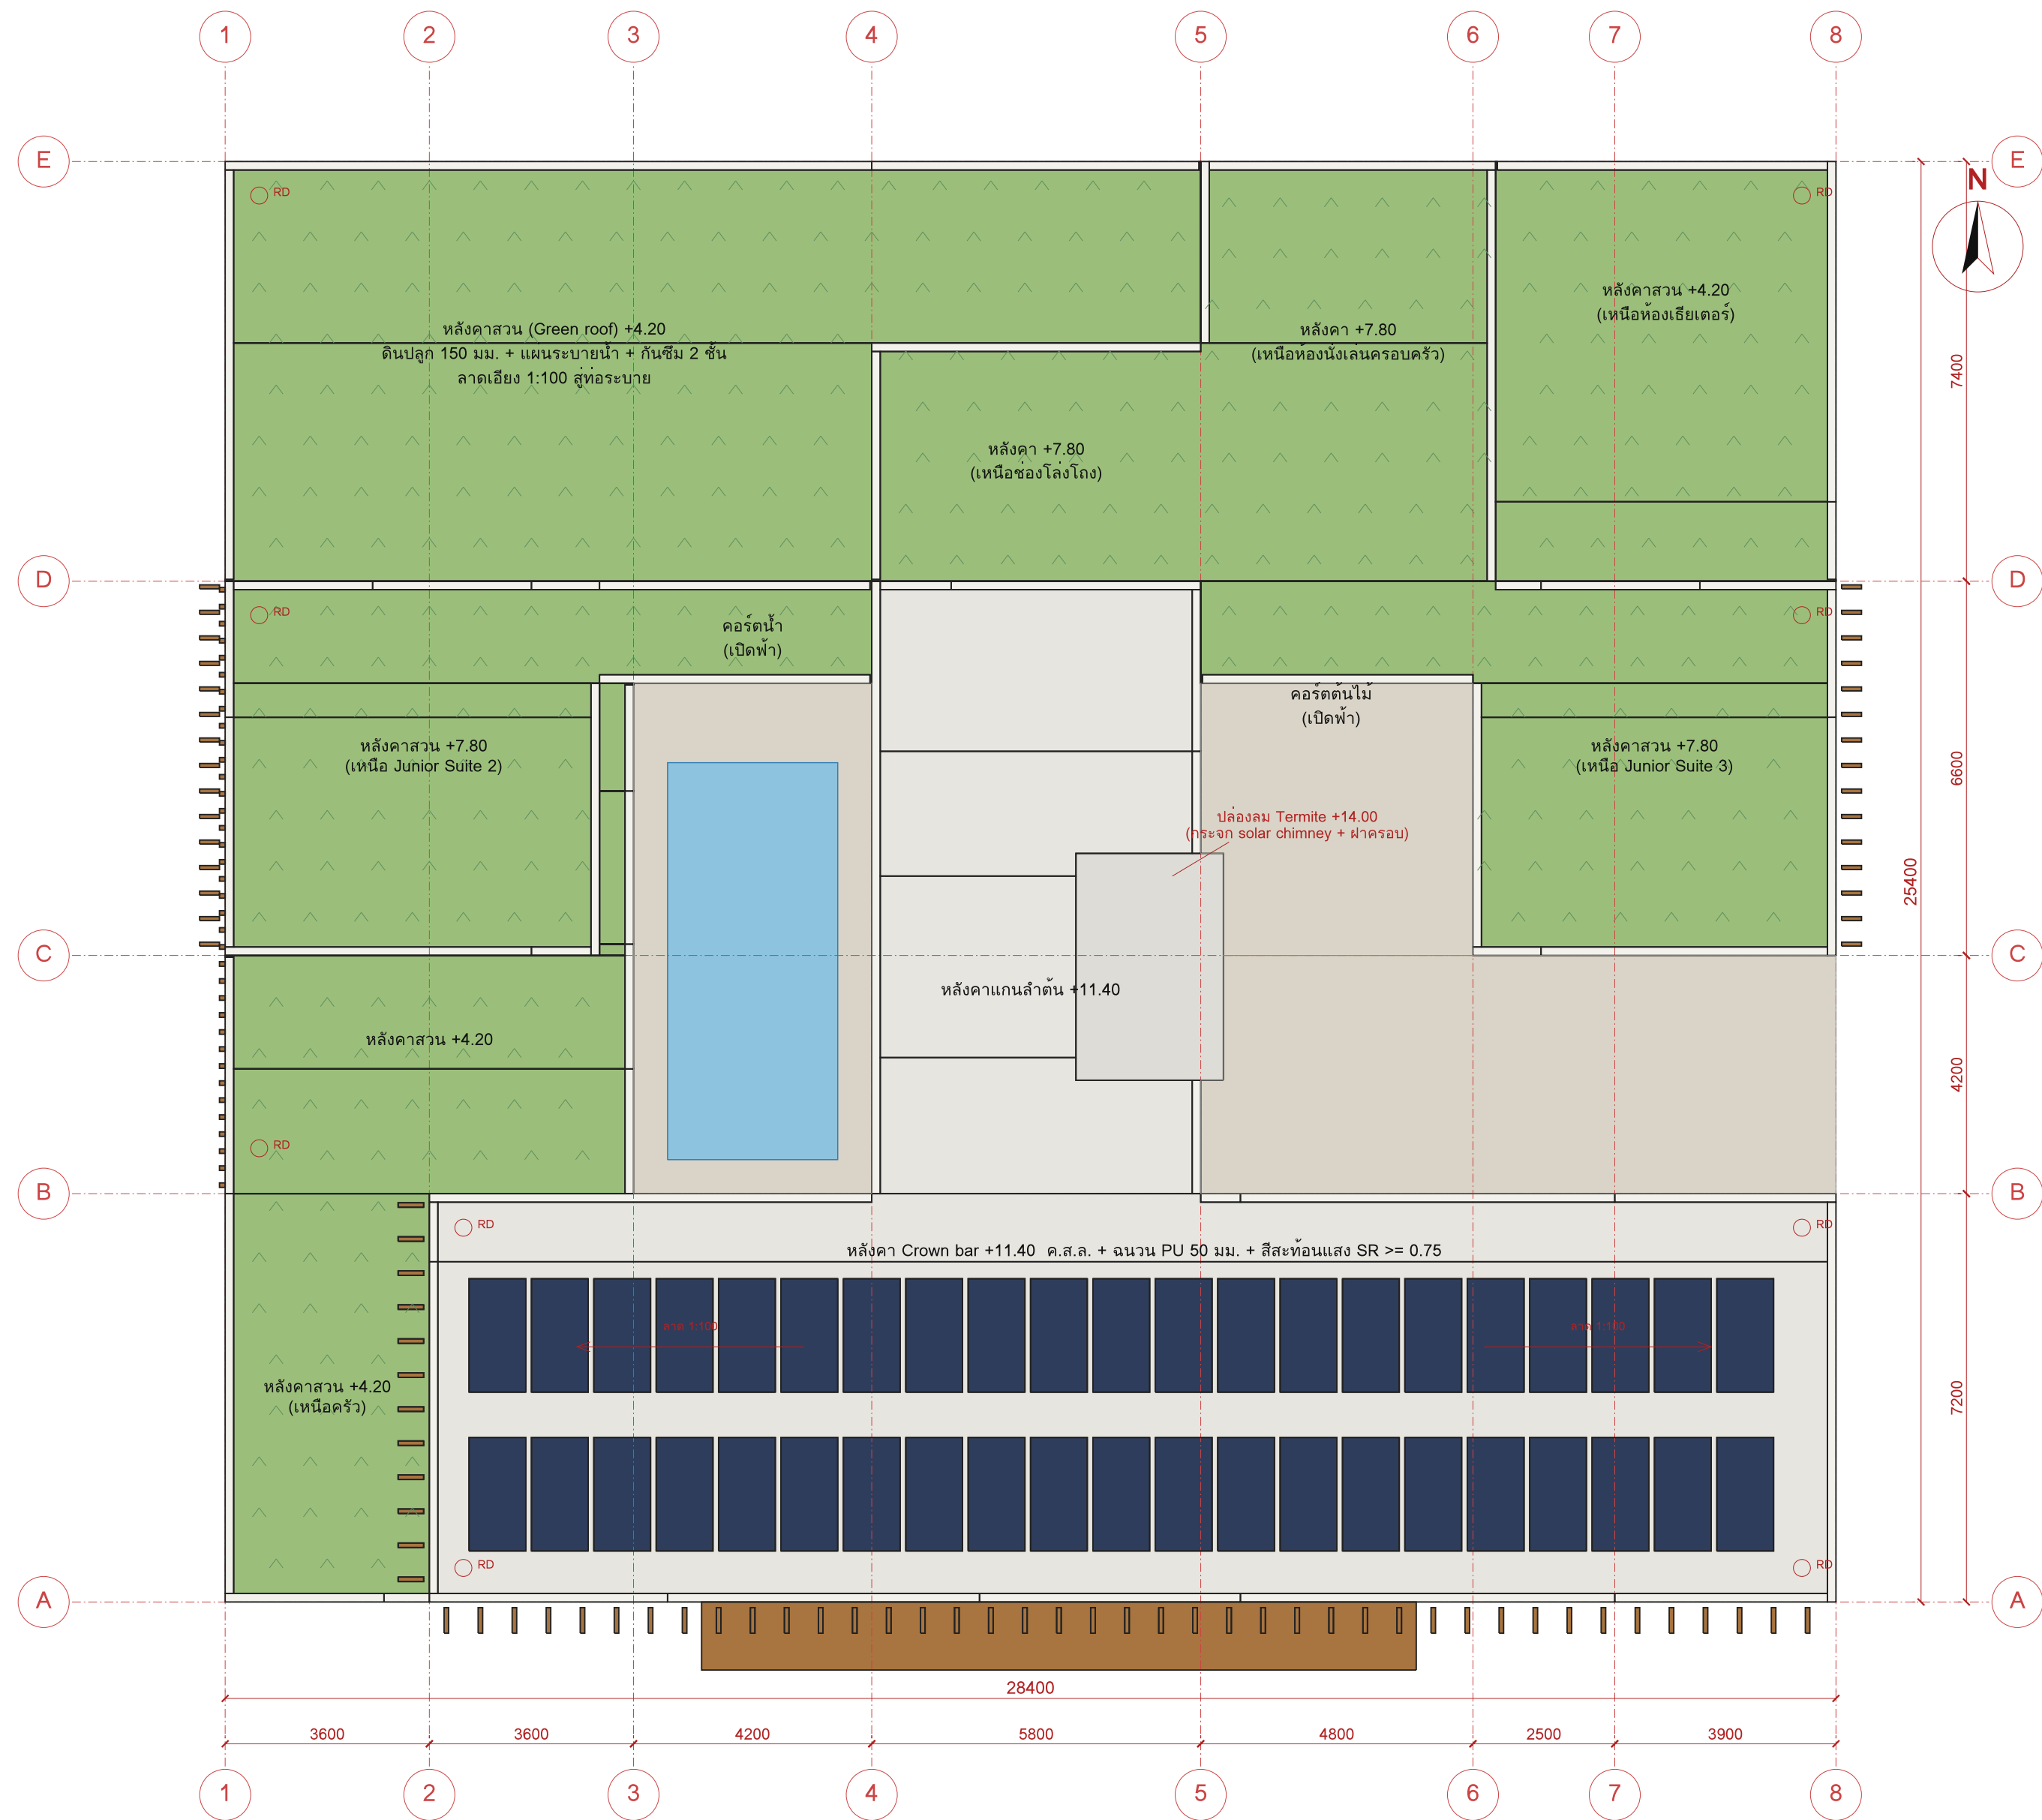

แปลนหลังคา ROOF PLAN 1:100



พื้นที่หลังคา

หลังคา	ค่า.ม.
หลังคาสวน +4.20 (เหนือชั้น 1)	294.20
หลังคาสวน +7.80 (เหนือชั้น 2)	165.92
หลังคา Crown +11.40 (ค.ส.ล. ขาว SR)	241.20
รวม	701.32
สัดส่วนหลังคาเขียว	66%

น้ำฝน (BEETLE) และพลังงาน

รายการ	ค่า
สมรภูมิการเกษตร (ปริมาณ)	~1,500 มม./ปี
น้ำฝนเก็บได้ (หลังคาเขียว C=0.9, สวน C=0.4)	602 ลบ.ม./ปี
ถังเก็บน้ำฝนอัตโนมัติ	20 ลบ.ม. (รอใช้งาน/ซักโถง)
แผงโซลาร์ 42 x 550 Wp	23.1 kWp ~ 29,000 kWh/ปี*
ปล่องลม Termite	สูง +14.00 กระจกด้านเหนือใต้

ชั้นหลังคา

- หลังคาสวน: พืชคลุมดิน + ดินปลูก 150 มม. + แผ่นใยกรอง + แผ่นระบายน้ำ 20 มม.
- + แผ่นกันรากทะลุ + กันซึม 2 ชั้น + ค.ส.ล. ลาด 1:100
- หลังคา Crown: สีสสะท้อนแสง SR >= 0.75 + PU foam 50 มม. + กันซึม + ค.ส.ล. 250
- Parapet สูง 0.60 ม. (Crown) / 0.45 ม. (หลังคาสวน)
- RD = ระบายน้ำฝนหลังคา ลรางระบายน้ำ -> ถังน้ำฝน -> ระบายน้ำ
- * พลังงาน PV ประมาณด้วย -1,250 kWh/kWp/ปี — ต้องคำนวณจริงด้วยมาจากคใบและแปลง

H3A DESIGN AND BUILD

X-UNIT Architecture Lab

โครงการ

WELL-GENWEAVE 40x40 v3

Executive Luxury Villa

บ้านเดี่ยว 3 ชั้น ผ่านเกณฑ์

WELL for Residential (เจดณา)

ที่ดิน 40.00 x 40.00 ม. = 400 ตร.ว.
ถนนสาธารณะ 8.00 ม. ทิศเหนือ

แนวคิด

GENWEAVE: ลำต้น (แกนบันได+ปล่อง Termite) แยกกิ่ง 4 ทิศ รอบคอร์ท 2 แห่ง
Crown bar ชั้น 3 = เรือนยอดกิ่งแตก

ระดับ

±0.00 ถนน · F1 +0.60 · F2 +4.20
F3 +7.80 · หลังคา +11.40
parapet +12.00 · ปล่อง +14.00

หมายเหตุ

- หน่วยงานเป็นผลิตภัณฑ์ เว้นแต่ระบุ
- ระดับอ้างอิงถนนหน้าที่ดิน ±0.00
- ห้ามวัดขนาดจากแบบ ใช้ตัวเลขกำกับ
- แบบระดับ Design Development
- ต้องให้สถาปนิกและวิศวกรผู้ได้รับใบอนุญาตตรวจสอบและลงนามก่อนยื่นขออนุญาต


ชื่อแผ่น

แปลนหลังคา


มาตรฐาน 1:100

วันที่ 1 ค.ค. 2569 ฉบับ v3 / DD

รูปด้านทิศใต้ (มองจากสวน/สระ) 1:100

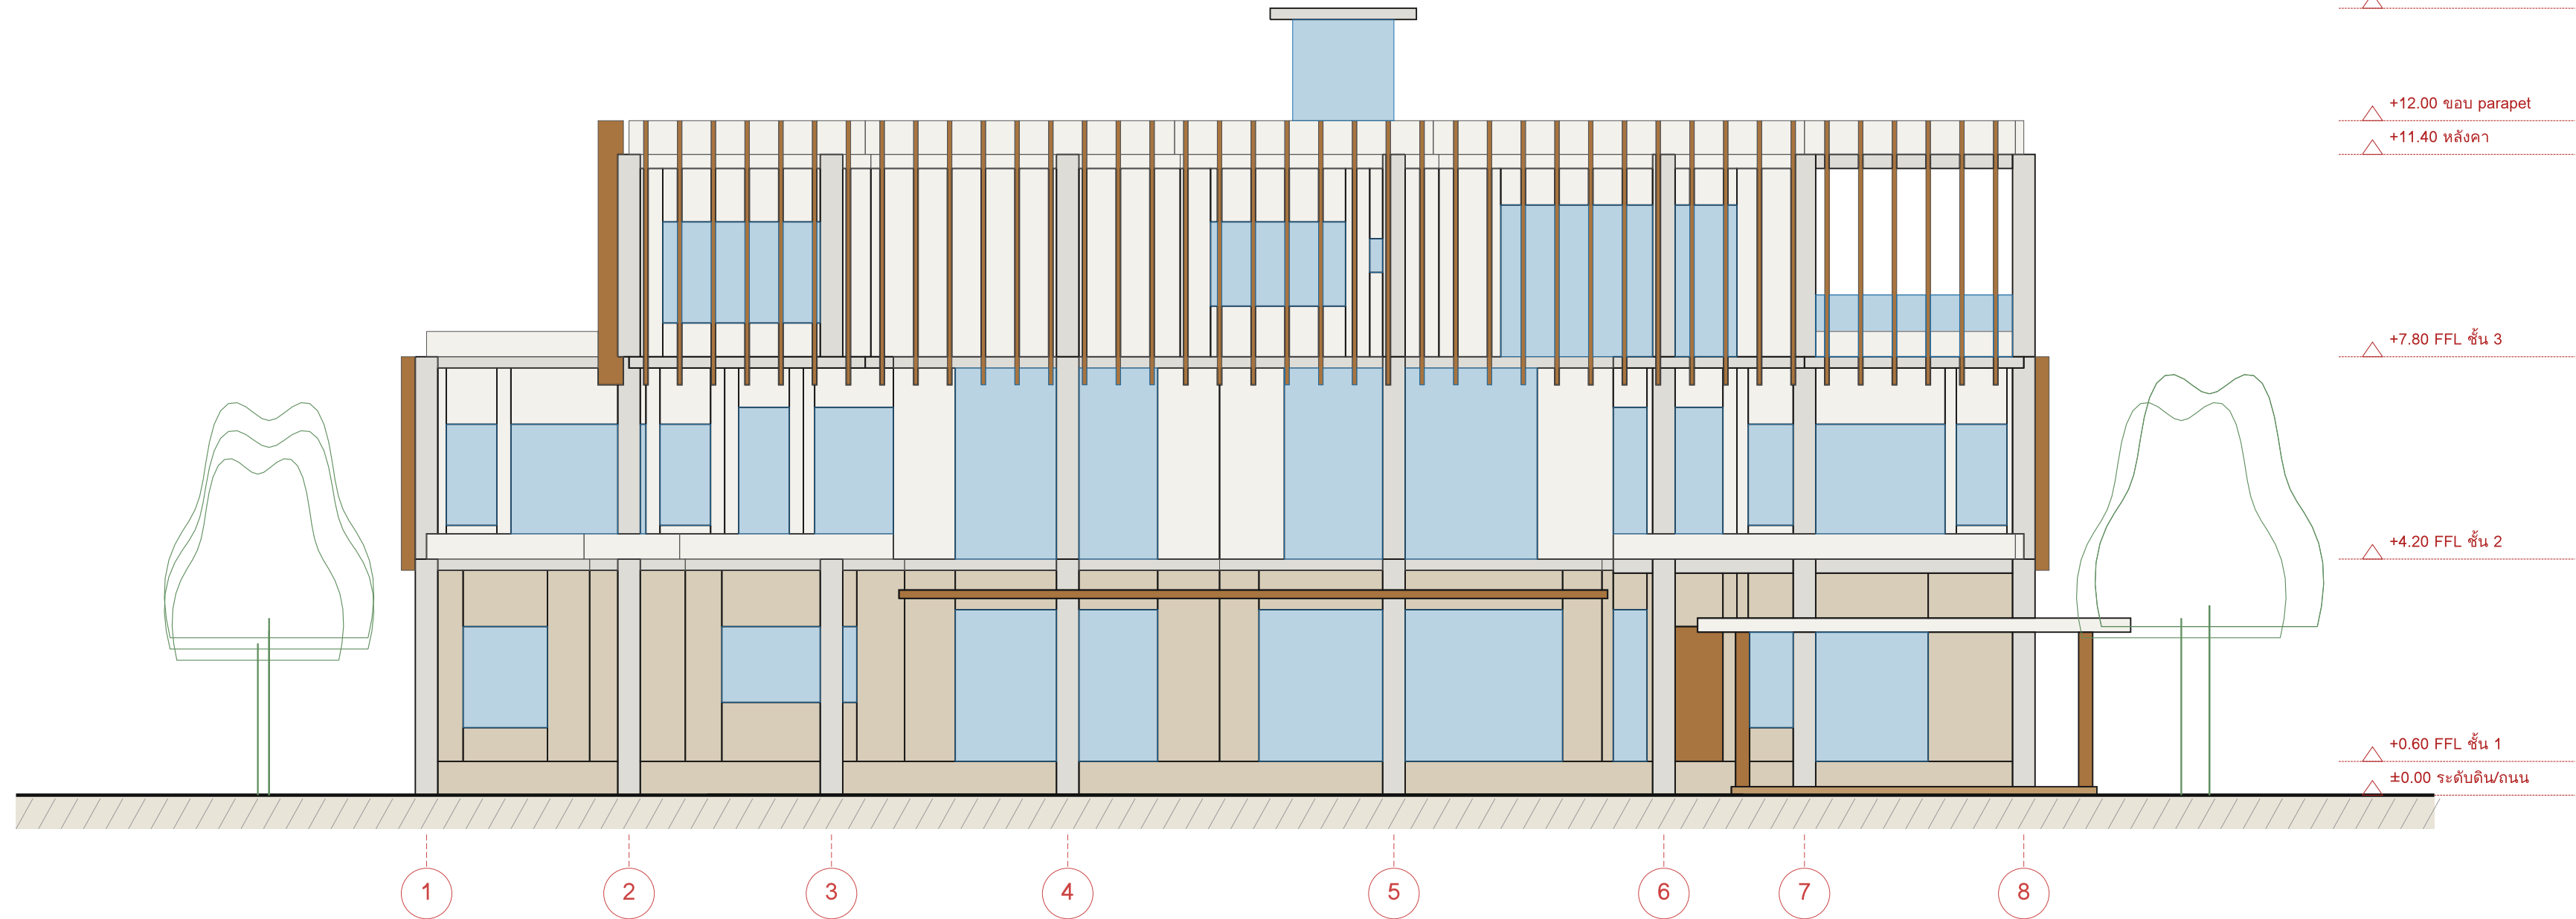

รูปด้านทิศเหนือ (ด้านถนน) 1:100

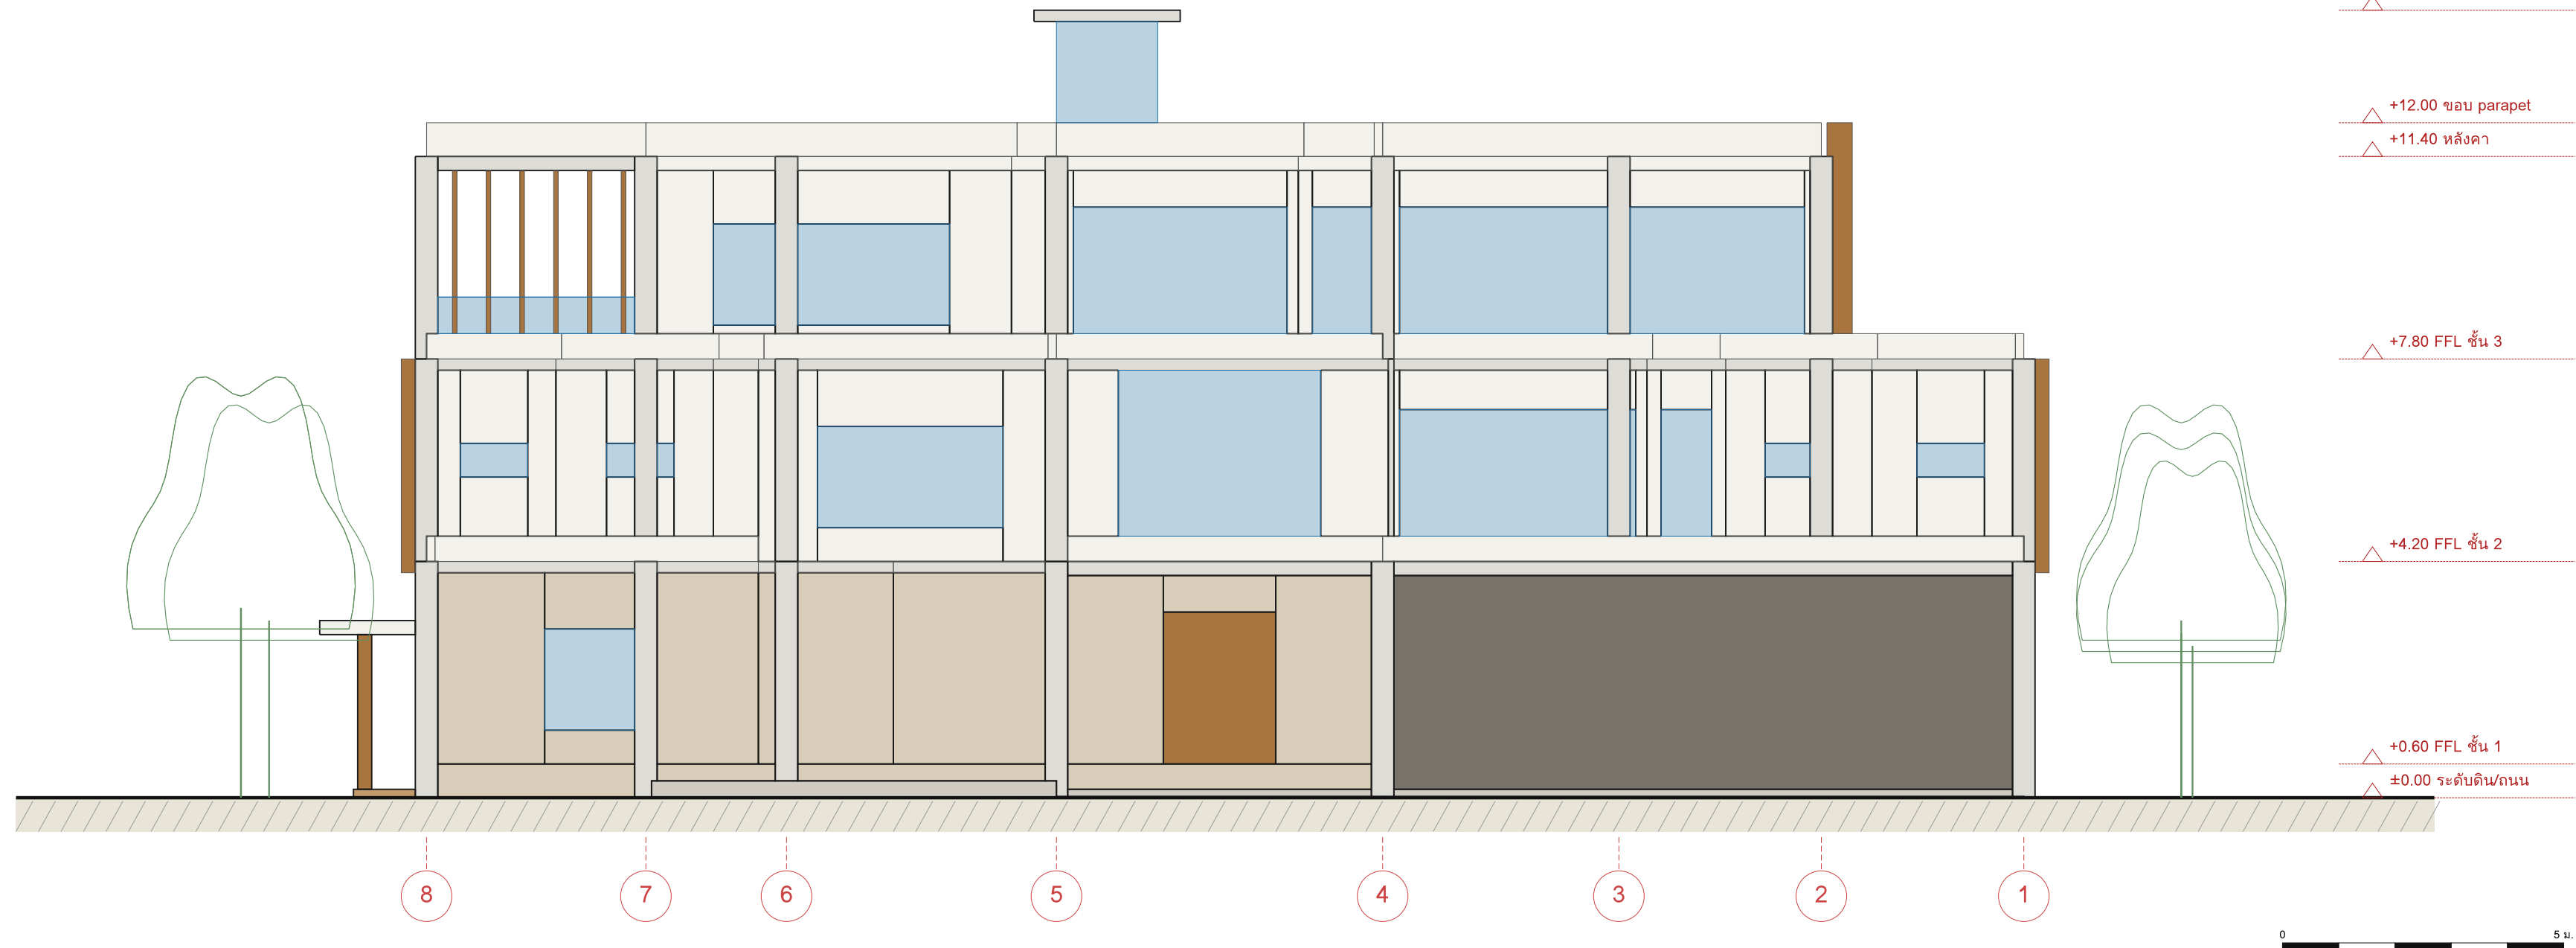

H3A DESIGN AND BUILD

X-UNIT Architecture Lab

โครงการ

WELL-GENWEAVE 40x40 v3

Executive Luxury Villa
บ้านเดี่ยว 3 ชั้น ผ่านเกณฑ์
WELL for Residential ()

ที่ดิน 40.00 x 40.00 ม. = 400 ตร.ว.
ถนนสาธารณะ 8.00 ม. หิศเหนือ

แนวคิด

GENWEAVE: ลำต้น (แกนบันได+ปล้อง Termite) แตกกิ่ง 4 ทิศ รอบคอร์ต 2 แห่ง Crown bar ชั้น 3 = เรือนยอดบังแดด

ระดับ

±0.00 ถนน · F1 +0.60 · F2 +4.20
F3 +7.80 · หลังคา +11.40
parapet +12.00 · ปล่อง +14.00

หมายเหตุ

- หน่วยเป็นมิลลิเมตร เว้นแต่ระบุ
ระดับอ้างอิงถนนหน้าที่ดิน ± 0.00
ห้ามวัดขนาดจากแบบ ใช้ตัวเลขกำกับ
แบบระดับ Design Development
ต้องให้สถาปนิกและวิศวกรผู้ได้รับ
ใบอนุญาตตรวจสอบและลงนาม
ก่อนยื่นขออนุญาต

ชื่อแผ่น

รูปด้านทิศใต้
+ รูปด้านทิศเหนือ


มาตราส่วน 1:100

วันที่ 1 ต.ค. 2569 ฉบับ v3 / DD

รูปด้านทิศตะวันออก 1:100



รูปด้านทิศตะวันตก (ลานบริการ) 1:100

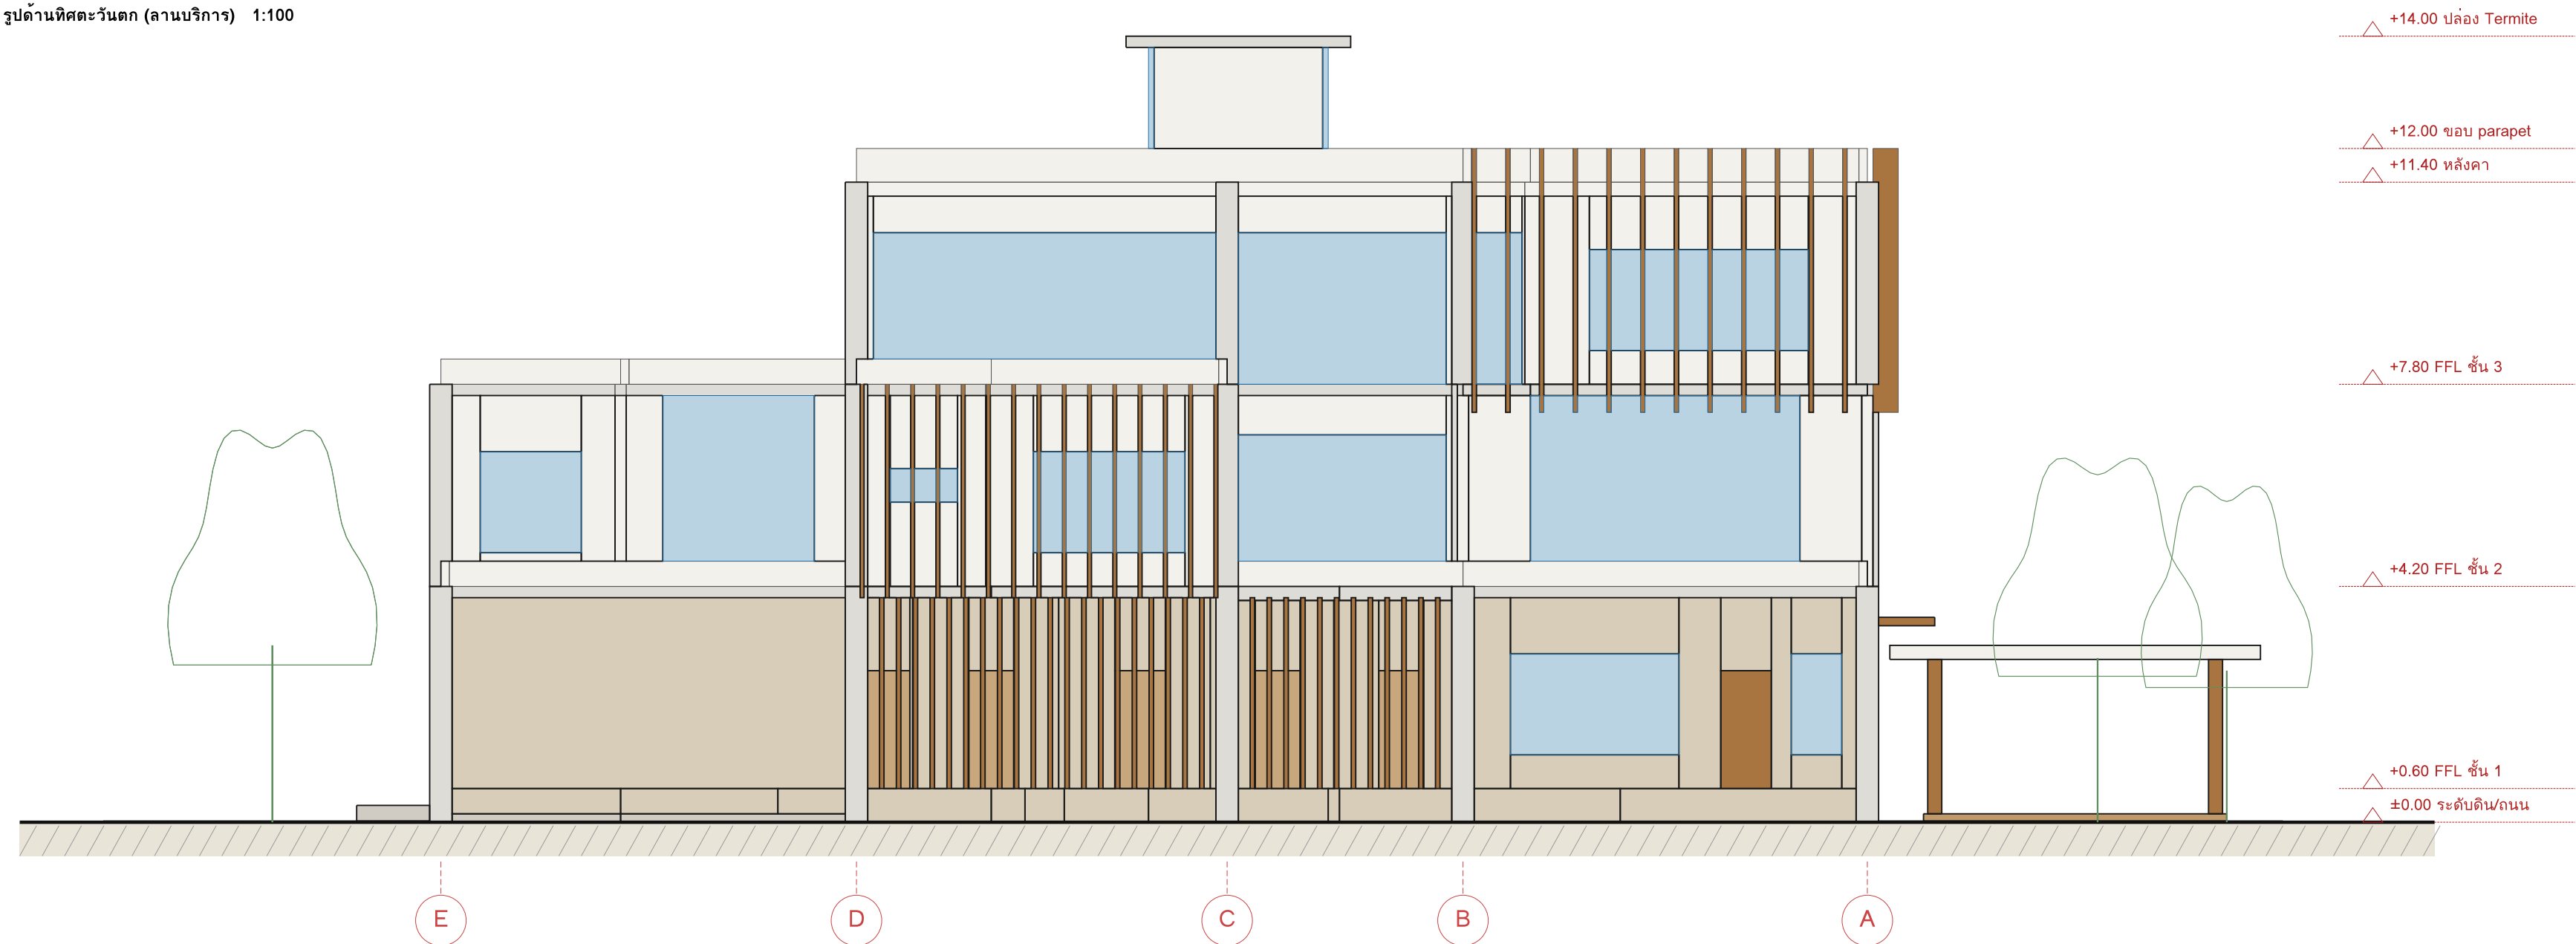

H3A DESIGN AND BUILD

X-UNIT Architecture Lab

โครงการ

WELL-GENWEAVE 40x40 v3

Executive Luxury Villa
บ้านเดี่ยว 3 ชั้น ผ่านเกณฑ์
WELL for Residential (เจดนา)

ที่ดิน 40.00 x 40.00 ม. = 400 ตร.ว.
ถนนสาธารณะ 8.00 ม. ทิศเหนือ

แนวคิด

GENWEAVE: ลำต้น (แกนบันได+ปล่อง
Termite) แยกกิ่ง 4 ทิศ รอบคอร์ท 2 แห่ง
Crown bar ชั้น 3 = เรือนยอดปิดเปิด

ระดับ

±0.00 ถนน · F1 +0.60 · F2 +4.20
F3 +7.80 · หลังคา +11.40
parapet +12.00 · ปล่อง +14.00

หมายเหตุ

- หน่วยงานศิลปกรรม เว้นแต่ระบุ
- ระดับอ้างอิงถนนหน้าที่ดิน ±0.00
- ห้ามวัดขนาดจากแบบ ใช้ตัวเลขกำกับ
- แบบระดับ Design Development
- ต้องให้สถาปนิกและวิศวกรผู้ได้รับ
ใบอนุญาตตรวจสอบและลงนาม
ก่อนยื่นขออนุญาต

ชื่อแผ่น

รูปด้านทิศตะวันออก
+ รูปด้านทิศตะวันตก

มาตราส่วน 1:100

วันที่ 1 ค.ค. 2569 ฉบับ v3 / DD

รูปตัด A-A (ตัดแนวตะวันออก-ตะวันตก ผ่านห้องครัว-ห้องอาหาร-ห้องนั่งเล่น-แถบ Crown ชั้น 3 มองไปทิศเหนือ) 1:100



รูปตัด B-B (ตัดแนวเหนือ-ใต้ ผ่านโถงต้อนรับ-บันไดหลัก-ห้องอาหาร-ห้องน้ำ Spa มองไปทิศตะวันออก) 1:100



WELL-GENWEAVE 40x40 v3

Executive Luxury Villa
บ้านเดี่ยว 3 ชั้น ผ่านเกณฑ์
WELL for Residential (เจตนา)

ที่ดิน 40.00 x 40.00 ม. = 400 ตร.ว.
ถนนสาธารณะ 8.00 ม. หิสเหนือ

GENWEAVE: ลำต้น (แกนบันได+ปล่อง Termite) ตกถึง 4 ทิศ รอบคอร์ต 2 แห่ง Crown bar ชั้น 3 = เรือนยอดบังแดด

0.00 ถนน · F1 +0.60 · F2 +4.20
 F3 +7.80 · หลังคา +11.40
 Carpet +12.00 · ปล่อง +14.00

หน่วยเป็นมิลลิเมตร เว้นแต่ระบุ
ระดับอ้างอิงบนหน้าดิน ± 0.00
ห้ามวัดขนาดจากแบบ ใช้ตัวเลขกำกับ
แบบระดับ Design Development
ต้องให้สถาปนิกและวิศวกรผู้ได้รับ
ใบอนุญาตตรวจสอบและลงนาม
ก่อนยื่นขออนุญาต

รูปตัด A-A
รูปตัด B-B

วันที่ 1 ต.ค. 2569 ฉบับ v3 / DD

WELL-GENWEAVE 40x40 v3 - GENWEAVE Executive Luxury Villa - บ้านเดี่ยว 3 ชั้น "ลำตัน + กิ่ง" (TRUNK + BRANCH)

ที่ดิน 40.00 x 40.00 ม. (400 ตร.ว.) * ถนน 8.00 ม. ทิศเหนือ * โปรแกรม ARCHSPACE 27 ก.ย. 2569

ตารางช่องเปิด (119 รายการ) — หน่วย มม. วัดจาก FFL

รหัส	ชั้น	ชนิด	กว้าง	ขอบล่าง	ขอบบน	ตำแหน่ง
D01	F1	ประตูบานเปิดคู่	2000	0	2700	โถงลิ้นชักสูง 2 ประตูเทียบ (Po
D02	F1	ประตูบานเปิดเดี่ยว	900	0	2400	โรงจอดรถ 4 คัน โถงลิ้นชักสูง
SD01	F1	ประตูบานเลื่อนกระจก	2400	0	2400	ครัวโหว่ + โถงลิ้น ห้องรับประทานผ
D03	F1	ประตูบานเปิดเดี่ยว	800	0	2100	ครัวโหว่ (ครัวหัว) Walk-in Pantry
D04	F1	ประตูบานเปิดเดี่ยว	900	0	2100	ซานบริการ/ตากผ้า ครัวโหว่ (ครัวห
D05	F1	ประตูบานเปิดเดี่ยว	900	0	2100	ครัวโหว่ (ครัวหัว) ภายนอก-W
D06	F1	ประตูบานเปิดเดี่ยว	800	0	2100	ซานบริการ/ตากผ้า ห้องนอน 1
D07	F1	ประตูบานเปิดเดี่ยว	800	0	2100	ซานบริการ/ตากผ้า ห้องนอน 2
D08	F1	ประตูบานเปิดเดี่ยว	800	0	2100	ซานบริการ/ตากผ้า ห้องนอนบน
D09	F1	ประตูบานเปิดเดี่ยว	900	0	2100	ซานบริการ/ตากผ้า ห้องซักรีด
D10	F1	ประตูบานเปิดเดี่ยว	800	0	2100	ซานบริการ/ตากผ้า ห้อง MEP / ไฟฟ
D11	F1	ประตูบานเปิดคู่	1200	0	2400	ประตูเทียบ (Port) ห้องลิ้นชัก
SD02	F1	ประตูบานเลื่อนกระจก	5400	0	2700	ห้องโถงหลักสูง ภายนอก-S
SD03	F1	ประตูบานเลื่อนกระจก	3500	0	2700	ห้องโถงหลักสูง ภายนอก-N
SD04	F1	ประตูบานเลื่อนกระจก	3600	0	2700	ห้องโถงหลักสูง ระเบียงยาวเปิด
SD05	F1	ประตูบานเลื่อนกระจก	3600	0	2700	ห้องรับประทานผ ภายนอก-S
SD06	F1	ประตูบานเลื่อนกระจก	2400	0	2700	ห้องรับประทานผ ภายนอก-N
SD07	F1	ประตูบานเลื่อนกระจก	2400	0	2400	ห้องนอนแขกใหญ่ ภายนอก-S
D12	F1	ประตูบานเปิดเดี่ยว	900	0	2400	ทางเดินห้องแขก ภายนอก-S
D13	F1	ประตูบานเปิดเดี่ยว	800	0	2100	ระเบียงยาวเปิด ห้องส้วน้ำจีนส
D14	F1	ประตูบานเปิดเดี่ยว	1000	0	2400	ทางเดินด้าน (Tr) ภายนอก-W
D15	F1	ประตูบานเปิดเดี่ยว	800	0	2100	Walk-in Pantry ครัวโหว่ + โถง
SD08	F1	ประตูบานเลื่อนเดี่ยว	900	0	2100	ห้องนอนแขกใหญ่ ห้องนั่งพักผ่อน
D16	F1	ประตูบานเปิดเดี่ยว	800	0	2100	ห้องนอนแขกใหญ่ ตู้เสื้อผ้าห้อง
W01	F1	หน้าต่าง	2400	1050	2400	ครัวโหว่ + โถงลิ้น ภายนอก-S
D17	F1	ประตูบานเปิดเดี่ยว	800	0	2100	โถงลิ้นชักสูง 2 ห้องนั่งแขก (Po
D18	F1	ประตูบานเปิดเดี่ยว	800	0	2100	ทางเดินปีกเหนือ ห้องลิ้น / ซั
D19	F1	ประตูบานเปิดเดี่ยว	900	0	2400	ทางเดินปีกเหนือ ห้องโถงเฮลิคอป
D20	F1	ประตูบานเปิดเดี่ยว	900	0	2400	ทางเดินห้องแขก ห้องนอนแขกใหญ่
D21	F1	ประตูลิ้นชัก	900	0	2400	ลิ้นชัก โถงเหนือ (เข้า
W02	F1	ผนังกระจก	4200	0	2700	ทางเดินปีกเหนือ ภายนอก-S
W03	F1	ผนังกระจก	1100	0	2700	ทางเดินปีกเหนือ ภายนอก-E
W04	F1	หน้าต่าง	1800	600	2400	ห้องโถงเฮลิคอป ภายนอก-N
W05	F1	หน้าต่าง	1800	600	2400	ห้องโถงเฮลิคอป ภายนอก-E
W06	F1	หน้าต่าง	1200	600	2400	ห้องนอน 1 ภายนอก-E
W07	F1	หน้าต่าง	1200	600	2400	ห้องนอน 2 ภายนอก-E
W08	F1	หน้าต่าง	1200	1500	2100	ห้องซักรีด ภายนอก-E
W09	F1	หน้าต่าง	1200	1500	2100	ห้อง MEP / ไฟฟ้า ภายนอก-E
W10	F1	ผนังกระจก	4400	0	2700	ทางเดินด้าน (Tr) ภายนอก-W
W11	F1	ผนังกระจก	4400	0	2700	ทางเดินด้าน (Tr) ภายนอก-W
W12	F1	ผนังกระจก	1800	0	2700	ทางเดิน ภายนอก-E
W13	F1	เกล็ดระแนงอากาศ	2600	0	3000	ปล่องลม Termite ภายนอก-E
W14	F1	ผนังกระจก	2400	0	2700	โถงเหนือ (เข้าลิ) ภายนอก-E
W15	F1	ผนังกระจก	6000	0	2700	ทางเดินห้องแขก ภายนอก-W
W16	F1	หน้าต่าง	900	600	2400	ห้องนอนแขกใหญ่ ภายนอก-S
W17	F1	หน้าต่าง	900	600	2400	ห้องนอนแขกใหญ่ ภายนอก-S
W18	F1	หน้าต่าง	2700	600	2400	ห้องนอนแขกใหญ่ ภายนอก-E
W19	F1	หน้าต่าง	1200	1500	2100	ตู้เสื้อผ้าห้อง ภายนอก-E
W20	F1	หน้าต่าง	1500	600	2400	ครัวโหว่ (ครัวหัว) ภายนอก-S
W21	F1	หน้าต่าง	900	600	2400	ครัวโหว่ (ครัวหัว) ภายนอก-W
W22	F1	หน้าต่าง	3000	600	2400	ครัวโหว่ (ครัวหัว) ภายนอก-W
W23	F1	หน้าต่าง	900	600	2400	ครัวโหว่ + โถงลิ้น ภายนอก-N
W24	F1	หน้าต่าง	600	1500	2100	ห้องส้วน้ำจีนสระ ภายนอก-N
W25	F1	หน้าต่าง	1200	1500	2100	ห้องส้วน้ำจีนสระ ภายนอก-E
D22	F2	ประตูบานเปิดเดี่ยว	800	0	2100	ห้องนอน Junior S ห้องน้ำ Junior
D23	F2	ประตูบานเปิดเดี่ยว	800	0	2100	ห้องนอน Junior S ตู้เสื้อผ้า ม
D24	F2	ประตูบานเปิดเดี่ยว	800	0	2100	ห้องนอน Junior S ห้องน้ำ Junior
D25	F2	ประตูบานเปิดเดี่ยว	800	0	2100	ห้องนอน Junior S ตู้เสื้อผ้า ม
SD09	F2	ประตูบานเลื่อนกระจก	2400	0	2400	ห้องนอน Junior S ภายนอก-S
SD10	F2	ประตูบานเลื่อนกระจก	2400	0	2400	ห้องนอน Junior S ภายนอก-S

รหัส	ชั้น	ชนิด	กว้าง	ขอบล่าง	ขอบบน	ตำแหน่ง
D26	F2	ประตูลิ้นชัก	900	0	2400	ลิ้นชักบน Upper Gallery
D27	F2	ประตูบานเปิดเดี่ยว	900	0	2400	ทางเดิน Junior S ห้องนอน Junior
D28	F2	ประตูบานเปิดเดี่ยว	900	0	2400	ทางเดิน Junior S ห้องนอน Junior
W26	F2	ผนังกระจก	900	0	2700	ทางเดิน Junior S ภายนอก-S
W27	F2	ผนังกระจก	900	0	2700	ทางเดิน Junior S ภายนอก-N
W28	F2	ผนังกระจก	4200	0	2700	ทางเดิน Junior S ภายนอก-E
W29	F2	หน้าต่าง	900	600	2400	ห้องนอน Junior S ภายนอก-S
W30	F2	หน้าต่าง	900	600	2400	ห้องนอน Junior S ภายนอก-S
W31	F2	หน้าต่าง	2700	600	2400	ห้องนอน Junior S ภายนอก-W
W32	F2	หน้าต่าง	1200	1500	2100	ห้องน้ำ Junior S ภายนอก-N
W33	F2	หน้าต่าง	1200	1500	2100	ห้องน้ำ Junior S ภายนอก-W
W34	F2	หน้าต่าง	1200	1500	2100	ตู้เสื้อผ้า มุม ภายนอก-N
W35	F2	ผนังกระจก	4200	0	2700	สะพานโถงเชื่อม ภายนอก-S
W36	F2	ผนังกระจก	4200	0	2700	สะพานโถงเชื่อม ภายนอก-N
W37	F2	ผนังกระจก	8400	0	2700	ทางเดินด้าน (Tr) ภายนอก-W
W38	F2	ผนังกระจก	1800	0	2700	โถงใต้ ภายนอก-E
W39	F2	เกล็ดระแนงอากาศ	2600	0	3000	ปล่องลม Termite ภายนอก-E
W40	F2	ผนังกระจก	900	0	2700	Upper Gallery (T) ภายนอก-E
W41	F2	ผนังกระจก	4200	0	2700	สะพานโถงเชื่อม ภายนอก-S
W42	F2	หน้าต่าง	3300	600	2400	ห้องลิ้นชักครอบ ภายนอก-N
W43	F2	หน้าต่าง	1800	600	2400	ห้องลิ้นชักครอบ ภายนอก-W
W44	F2	หน้าต่าง	4800	600	2400	ห้องลิ้นชักครอบ ภายนอก-E
W45	F2	ผนังกระจก	900	0	2700	ทางเดิน Junior S ภายนอก-S
W46	F2	ผนังกระจก	4200	0	2700	ทางเดิน Junior S ภายนอก-W
W47	F2	หน้าต่าง	900	600	2400	ห้องนอน Junior S ภายนอก-S
W48	F2	หน้าต่าง	900	600	2400	ห้องนอน Junior S ภายนอก-S
W49	F2	หน้าต่าง	2700	600	2400	ห้องนอน Junior S ภายนอก-E
W50	F2	หน้าต่าง	1200	1500	2100	ห้องน้ำ Junior S ภายนอก-N
W51	F2	หน้าต่าง	1200	1500	2100	ตู้เสื้อผ้า มุม ภายนอก-N
W52	F2	หน้าต่าง	1200	1500	2100	ตู้เสื้อผ้า มุม ภายนอก-E
W53	F2	หน้าต่าง	3600	0	3000	ช่องโถงโถงลิ้นชัก ภายนอก-N
W54	F2	หน้าต่าง	2700	0	3000	ช่องโถงโถงลิ้นชัก ภายนอก-W
W55	F2	หน้าต่าง	3600	0	3000	ช่องโถงโถงลิ้นชัก ภายนอก-N
W56	F2	หน้าต่าง	1800	0	3000	ช่องโถงโถงลิ้นชัก ภายนอก-N
W57	F2	หน้าต่าง	4800	0	3000	ช่องโถงโถงลิ้นชัก ภายนอก-W
W58	F2	หน้าต่าง	4500	0	3000	ช่องโถงโถงลิ้นชัก ภายนอก-S
W59	F2	หน้าต่าง	2400	0	3000	ช่องโถงโถงลิ้นชัก ภายนอก-N
W60	F2	หน้าต่าง	4800	0	3000	ช่องโถงโถงลิ้นชัก ภายนอก-E
SD11	F3	ประตูบานเลื่อนกระจก	3600	0	2700	ห้องนอน Master S ระเบียง Master
SD12	F3	ประตูบานเลื่อนกระจก	4200	0	2700	ห้องนอน Master S ภายนอก-S
W61	F3	หน้าต่าง	2400	900	2400	ห้องน้ำ Spa + Ja ภายนอก-S
W62	F3	หน้าต่าง	3000	600	2400	ห้องทำงาน & ห้อง ภายนอก-S
D29	F3	ประตูบานเปิดเดี่ยว	900	0	2400	ห้องน้ำ Spa + Ja ห้องนอน Master
SD13	F3	ประตูบานเปิดเดี่ยว	900	0	2400	Walk-in Dressing ห้องน้ำ Spa +
D30	F3	ประตูบานเปิดเดี่ยว	900	0	2400	Walk-in Dressing ทางเดินชั้น 3
D31	F3	ประตูบานเปิดเดี่ยว	900	0	2400	ห้องทำงาน & ห้อง ทางเดินชั้น 3
D32	F3	ประตูบานเปิดเดี่ยว	900	0	2400	ทางเดินชั้น 3 ห้องนอน Master
D33	F3	ประตูลิ้นชัก	900	0	2400	ลิ้นชักบน โถงลิ้นชักชั้น 3
W63	F3	ผนังกระจก	1100	0	2700	ทางเดินด้าน (Tr) ภายนอก-N
W64	F3	ผนังกระจก	10200	0	2700	ทางเดินด้าน (Tr) ภายนอก-W
W65	F3	ผนังกระจก	1800	0	2700	โถงใต้ ภายนอก-E
W66	F3	เกล็ดระแนงอากาศ	2600	0	3000	ปล่องลม Termite ภายนอก-E
W67	F3	ผนังกระจก	3800	0	2700	โถงลิ้นชักชั้น 3 ภายนอก-N
W68	F3	ผนังกระจก	2400	0	2700	โถงลิ้นชักชั้น 3 ภายนอก-E
W69	F3	หน้าต่าง	3900	600	2400	ห้องทำงาน & ห้อง ภายนอก-W
W70	F3	หน้าต่าง	600	1500	2100	ห้องน้ำ Spa + Ja ภายนอก-S
W71	F3	ผนังกระจก	7200	0	2700	ทางเดินชั้น 3 ภายนอก-N
W72	F3	ผนังกระจก	900	0	2700	ทางเดินชั้น 3 ภายนอก-W
W73	F3	หน้าต่าง	4200	600	2400	ห้องนอน Master S ภายนอก-N

๑.39 ข้อ 6 ช่องเปิด >= 10% ของพื้นที่ห้อง

ห้อง	ข้อมูลพื้นที่ห้อง	ผล
F1 ห้องนั่งแขก (Powder)	0.0% (0.00/7.28) -> ผิดสมรบนายอากาศ (ข้อ 6 วรร	ผ่าน
F1 ห้องเก็บจักรยาน/อุปกรณ์สวน	30.3% (2.88/9.52)	ผ่าน
F1 ห้องลิ้นชัก / ซักรีด	0.0% (0.00/14.40) -> ผิดสมรบนายอากาศ (ข้อ 6 วรร	ผ่าน
F1 ห้องโถงเฮลิคอป	18.0% (8.49/36.00)	ผ่าน
F1 ห้องนอน 1	29.1% (3.84/13.20)	ผ่าน
F1 ห้องนอน 2	29.1% (3.84/13.20)	ผ่าน
F1 ห้องซักรีด	16.1% (2.61/16.20)	ผ่าน
F1 ห้องลิ้นชักบน	26.9% (1.68/6.24)	ผ่าน
F1 ห้อง MEP / ไฟฟ้า	15.0% (2.40/15.96)	ผ่าน
F1 ห้องนอนแขกใหญ่สูง	63.5% (13.86/21.84)	ผ่าน
F1 ห้องน้ำห้องแขก	0.0% (0.00/6.72) -> ผิดสมรบนายอากาศ (ข้อ 6 วรร	ผ่าน
F1 ตู้เสื้อผ้าห้องแขก	12.5% (0.72/5.76)	ผ่าน
F1 ครัวโหว่ (ครัวหัว)	60.4% (12.18/20.16)	ผ่าน
F1 Walk-in Pantry/ห้องเย็น	0.0% (0.00/12.24) -> ผิดสมรบนายอากาศ (ข้อ 6 วรร	ผ่าน
F1 ครัวโหว่ + โถงลิ้นชัก	17.3% (4.86/28.08)	ผ่าน
F1 ห้องรับประทานอาหาร	116.1% (46.80/40.32)	ผ่าน
F1 ห้องลิ้นชักสูง 2 ชั้น	136.6% (68.85/50.40)	ผ่าน
F1 ห้องส้วน้ำจีนสระ	61.6% (2.76/4.48)	ผ่าน
F2 ห้องนอน Junior Suite 2	61.1% (13.86/22.68)	ผ่าน
F2 ห้องน้ำ Junior Suite 2	23.1% (1.44/6.24)	ผ่าน
F2 ตู้เสื้อผ้า Junior Suite 2	10.7% (0.72/6.72)	ผ่าน
F2 ห้องลิ้นชักครอบเตียง	46.3% (17.82/38.48)	ผ่าน
F2 ห้องนอน Junior Suite 3	63.5% (13.86/21.84)	ผ่าน
F2 ห้องน้ำ Junior Suite 3	10.7% (0.72/6.72)	ผ่าน
F2 ตู้เสื้อผ้า Junior Suite 3	25.0% (1.44/5.76)	ผ่าน
F3 ห้องทำงาน & ห้องสมุด	49.3% (12.42/25.20)	ผ่าน
F3 Walk-in Dressing (His & Hers)	0.0% (0.00/33.00) -> ผิดสมรบนายอากาศ (ข้อ 6 วรร	ผ่าน
F3 ห้องน้ำ Spa + Jacuzzi	14.3% (3.96/27.60)	ผ่าน
F3 ห้องนอน Master Suite	60.2% (26.62/47.52)	ผ่าน

ระบายนายอากาศข้ามห้อง >= 2 แนวหนึ่ง (เกณฑ์ภายใน สนับสนุน WELL R-T06) และความลึกห้อง <= 4.20 ม.

ห้อง/ใช้งานประจำ	ข้อมูล	ทิศทางลม/แนว	ผล
F1 ห้องโถงเฮลิคอป	2 แนวหนึ่ง	5.85 ม. (ห้องฉายภาพ ลมโถงลิ้น	ผ่าน
F1 ห้องนอน 1	2 แนวหนึ่ง	2.85 ม.	ผ่าน
F1 ห้องนอน 2	2 แนวหนึ่ง	2.85 ม.	ผ่าน
F1 ห้องนอนแขกใหญ่สูง	2 แนวหนึ่ง	4.05 ม.	ผ่าน
F1 ครัวโหว่ (ครัวหัว)	3 แนวหนึ่ง	2.55 ม.	ผ่าน
F1 ครัวโหว่ + โถงลิ้นชัก	2 แนวหนึ่ง	4.05 ม.	ผ่าน
F1 ห้องรับประทานอาหาร	3 แนวหนึ่ง	4.05 ม.	ผ่าน
F1 ห้องลิ้นชักสูง 2 ชั้น	3 แนวหนึ่ง	4.17 ม.	ผ่าน
F2 ห้องนอน Junior Suite 2	2 แนวหนึ่ง	4.05 ม.	ผ่าน
F2 ห้องลิ้นชักครอบเตียง	3 แนวหนึ่ง	2.55 ม.	ผ่าน
F2 ห้องนอน Junior Suite 3	2 แนวหนึ่ง	4.05 ม.	ผ่าน
F3 ห้องทำงาน & ห้องสมุด	2 แนวหนึ่ง	4.05 ม.	ผ่าน
F3 ห้องนอน Master Suite	3 แนวหนึ่ง	3.45 ม.	ผ่าน

ตรวจจากชนิด	ผล	
F1 ห้องอุปสมัณั ไม่พบ ไม่เว้น	ผลรวม 597.28 / ลม 597.28, พบ	ผ่าน
F1 ทุกห้องเข้าถึงได้ (กราฟประตู)	เข้าถึงได้ 0	ผ่าน
F2 ห้องอุปสมัณั ไม่พบ ไม่เว้น	ผลรวม 319.28 / ลม 319.28, พบ	ผ่าน
F2 ทุกห้องเข้าถึงได้ (กราฟประตู)	เข้าถึงได้ 0	ผ่าน
F3 ห้องอุปสมัณั ไม่พบ ไม่เว้น	ผลรวม 241.20 / ลม 241.20, พบ	ผ่าน
F3 ทุกห้องเข้าถึงได้ (กราฟประตู)	เข้าถึงได้ 0	ผ่าน
F1 ช่องเปิดคดง (ขอบบานทำผนังจริง >= 420)	พบ 0	ผ่าน
F1 ช่องเปิดบนราวบันก	พบ 0	ผ่าน
F2 ช่องเปิดคดง (ขอบบานทำผนังจริง >= 420)	พบ 0	ผ่าน
F2 ช่องเปิดบนราวบันก	พบ 0	ผ่าน
F3 ช่องเปิดคดง (ขอบบานทำผนังจริง >= 420)	พบ 0	ผ่าน
F3 ช่องเปิดบนราวบันก	พบ 0	ผ่าน

เทียบโปรแกรม ARCHSPACE (ตร.ม.)

รายการโปรแกรม	ชั้น	โปรแกรม	ชั้นบน	แบบ	ต่าง
Grand Double-Height Foyer	F1	24.00	F1	24.36	+0.36
Formal Living Room	F1	50.00	F1	50.40	+0.40
Dining Room (10-12 Seats)	F1	40.00	F1	40.32	+0.32
Powder Room	F1	6.00	F1	7.28	+1.28
Home Theater / AV Lounge	F1	36.00	F1	36.00	+0.00
Wine Cellar / Cigar Room	F1	14.00	F1	14.40	+0.40
Master Suite Bedroom	F3	48.00	F3	47.52	-0.48
Master Walk-in (His & Hers)	F3	32.00	F3	33.00	+1.00
Spa Master Bath + Jacuzzi	F3	28.00	F3	27.60	-0.40
Junior Suite 2 (bath+closet)	F2	34.00	F2	35.64	+1.64
Junior Suite 3 (bath+closet)	F2	34.00	F2	34.32	+0.32
Guest Suite (GF / elderly)	F1	30.00	F1	34.32	+4.32
Family Lounge & Upper Gallery	F2	36.00	F2	38.48	+2.48
Executive Home Office & Library	F3	26.00	F3	25.20	-0.80
Show Kitchen & Island Bar	F1	28.00	F1	28.08	+0.08
Heavy Thai Kitchen	F1	20.00	F1	20.16	+0.16
Walk-in Pantry & Cold Storage	F1	12.00	F1	12.24	+0.24
Laundry & Utility Room	F1	16.00	F1	16.20	+0.20
Maid Bedroom 1 & 2	F1	22.00	F1	26.40	+4.40
Maid Bathroom	F1	6.00	F1	6.24	+0.24
MEP / Electrical / Generator	F2	14.00	F1	15.96	+1.96
Covered Garage 3-4 cars	F1	85.00	F1	84.36	-0.64
Covered Veranda & BBQ	F1	45.00	F1	48.80	+3.80
Upper Master Terrace	F2	28.00	F3	28.08	+0.08
Poolside Pavilion	F1	35.00	สวน	35.10	+0.10
รวม NUA		749.00		770.46	+21.46

แบบสีชมพู = ชั้นในแบบต่างๆจากโปรแกรม (ดูชุดลด A-01 ข้อ 1-2)

H3A DESIGN AND BUILD


X-UNIT Architecture Lab

กลยุทธ์ WELL for Residential (รหัสตาม Guidebook ก.พ. 2026 ในไฟล์เดอ์ WELL)

Feature (WELL for Residential)	การตอบสนองในแบบ v3	สถานะ	หลักฐานที่ต้องมี
R-A01 ระบบระบายอากาศ	พัดลมดูดเฉพาะจุดครัว/ห้องน้ำทุกห้อง + ERV ห้องนอน	ระบุในแบบงานระบบ	ต้องวัด
R-A05 ลดการเผาไหม้	ครัวโซลิว์เตาไฟฟ้าเหนียวน้ำ; ครัวไทยแยกปีก มีชุด >= 510 ลบ.ม./ชม.	ในแบบ	เอกสาร
R-A09 จุดชาร์จ EV	1 จุดในโรงรถ (ต่อเมื่อ 4 ช่อง)	ในแบบ	ภาพถ่าย
R-W03 น้ำที่ไม่ใช้น้ำดื่ม	ถังน้ำฝน 20 ลบ.ม. ใต้ครัวตักน้ำ สำหรับรดน้ำ/ซักโครก	ในแบบ	แบบสุขาภิบาล
R-L01 แสงธรรมชาติ	70.2% (266.1/378.9 ตร.ม.) -> ระดับ 3	คำนวณแล้ว	ต้องตรวจแสงจ้า
R-L02 ควบคุมแสง	วงจรแยกทุกห้อง + ม่านทึบห้องนอน/เฮียเตอร์	ระบุ	แบบไฟฟ้า
R-T06 หน้าด่างเปิดได้	13/13 ห้อง	คำนวณแล้ว	มั่งลวด/ตัวล็อก
R-T07 ความร้อนภายนอก	หลังคาสวน 66% + หลังคาขาว SR >= 0.75 + ต้นไม้ร่มใหญ่ 9 ต้น	ในแบบ	ค่า SR วัสดุ
R-V04 พื้นที่กิจกรรมกลางแจ้ง	สระ 16 ม. + ศาลา + คอร์ต 2 แห่ง + สวนรอบอาคาร	ในแบบ	-
R-V07 ออกแบบบันได	บันไดสำคัญเดินฝั่งกระบอกอร์ตน้ำ เห็นจากโถง ไข่ก่อนลิฟต์	ในแบบ	ภาพถ่าย
R-M01 ธรรมชาติและสถานที่	ทุกห้องหลักเห็นคอร์ต/สวนน้ำ; วัสดุไม้-หิน	ในแบบ	-
R-M04 พื้นที่จัดเก็บ	Walk-in 33.00 + ตู้เสื้อผ้าทุกห้องนอน + ห้องเก็บ	ในแบบ	-
R-N01 การปรุงอาหาร	ครัว 2 ส่วน (โซลิว์ไทย) + Pantry ห้องเย็น	ในแบบ	-
R-S01 แนวกันเสียง	ห้องนอนหลักไกลถนน 18-25 ม.; เฮียเตอร์ผนังกันเสียง	ต้องระบุ STC	ทดสอบ
R-C01 ออกแบบเพื่อทุกคน	ทางลาด 1:12 + ลิฟต์ + ห้องนอนแยกชั้น 1	ในแบบ	ดู A-01 ข้อ 7
R-C06 ก่อพิบัติ	ยกพื้น +0.60 + ร่องซึบน้ำ + เครื่องปั๊นไฟ	ในแบบ	ระดับน้ำท่วมจริง?
R-X02 วัสดุ	สี/กาว VOC ต่ำ ไม้รับรอง FSC	สเปก	ใบสั่งซื้อ

สถานะ = เจตนาการออกแบบ ยังไม่ใช้คะแนนรับรอง WELL Residence ต้องลงทะเบียน IWB1 ส่งเอกสาร และตรวจวัดจริงหลังก่อสร้าง (อากาศ น้ำ เสียง แสง)
ไม่ได้ประเมินคะแนนรวม — ไม่อ้างว่า "ผ่าน" จนกว่าจะมีผลตรวจ

มุมมองทิศตะวันตกเฉียงเหนือ — หลังคาสวน +4.20/+7.80 และแกนลำต้น

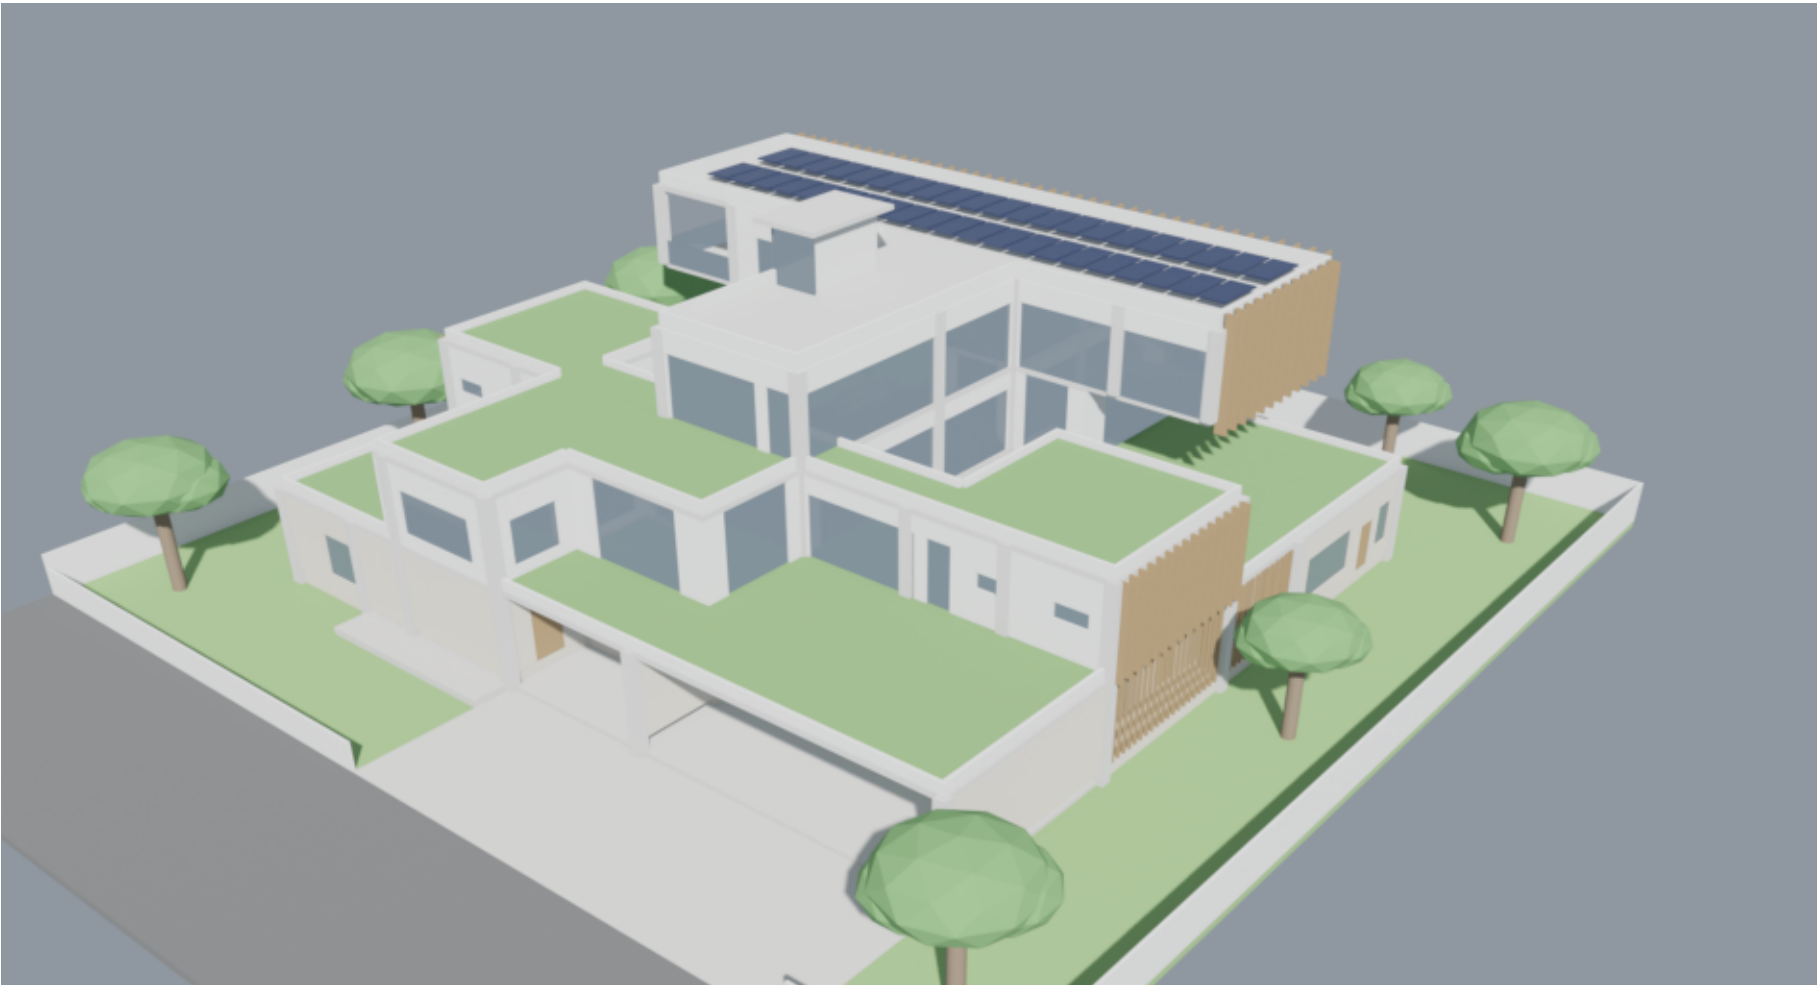

จากถนนทิศเหนือ — มุขรถเข็นและโรงรถ 4 คัน



วัสดุหลัก

หมวด	ข้อกำหนด (ระดับแนวคิด)
โครงสร้าง	ค.ส.ล. f _c ' 280 กก./ตร.ซม. เสาค 0.40x0.40 กริด 8x5 · คานถ่ายแรงโรงรถ 11.40 ม. PT/เหล็ก · ฐานรากเสาเข็มเจาะ (รพผลเจาะดิน)
ผนังภายนอก	บล็อกมวลเบา 200 มม. + ฉาบเรียบสีขาว (ชั้น 2-3) / สีนทรายกร (ชั้น 1) · ผนังภายใน 120 / ห้องน้ำ 150
กระจก	Low-E laminated 2 ชั้น · SHGC <= 0.25 ทิศ ตก/ออก, <= 0.35 ทิศใต้หลังคร์ับ · กรอบอะลูมิเนียมสีเทาเข้ม
ผิวอาคาร (CACTUS)	คريبอะลูมิเนียมลายไม้ 80x450 @600 (Crown bar) · ระแนงไม้ 80 @300 ขานบริการ · กันสาดไม้สัก 1.20 ม.
หลังคา	ค.ส.ล. + PU 50 + กันซึม + สี SR >= 0.75 · หลังคาสวนระบบ extensive 150 มม.
พื้น	หินขัดเทอร์ราซโซ (ชั้น 1) · ไม้สักจริงเอ็นจิเนียร์ (ชั้น 2-3) · กระเบื้องกันลื่น R11 ห้องน้ำ
ภายนอก	สระน้ำเกลือ 16.00x4.50 สัก 1.40 ม. · พื้นไม้เทียม WPC รอบสระ · ทางรถ ดินแกรนิตพื้นทราย

สิ่งที่ต้องทำต่อ

- วิศวกรโครงสร้าง: Crown bar เหนือห้องสูง 2 ชั้น, คานโรงรถ 11.40 ม., น้ำหนักหลังคาสวน, เสาเข็ม (ดินอ่อนกรุงเทพฯ)
- วิศวกรงานระบบ: VRF + ERV, ชุดครัวไทย, ระบบน้ำฝน/น้ำเทา, เครื่องปั๊นไฟ, โซลาร์ 23.1 kWp (ติดตั้งครับ)
- CFD + จำลองความร้อน: ยืนยันการไหลของลมผ่านปล่อง Termite และคอร์ต (ยังเป็นสมมติฐาน)
- จำลองแสงและแสงจ้า: พื้นที่กระจกสูง 70% ของพื้นที่ใช้งาน -> ต้องคุมแสงจ้า/ความร้อน
- ตรวจฝั่งเมืองรวม/ข้อบัญญัติท้องถิ่นของท้องถิ่นจริง (FAR, OSR, ระยะร่น, ความสูง)
- สำรวจระดับดิน-ระดับน้ำท่วมสูงสุด เพื่อยืนยันพื้น +0.60
- แบบขยาย: บันได, ราวกันตก, ครับ, สะพานกระชก, ห้องน้ำ Spa, ปล่องลม, สระ
- ลงทะเบียน WELL Residence และเตรียมเอกสารตามรายการด้านซ้าย
- ประมาณราคาละเอียด (BOQ) หลังได้แบบโครงสร้าง-งานระบบ

สรุปการตรวจ

ผลตรวจทั้งหมด 92 รายการ: ผ่าน 92 / ไม่ผ่าน 0
ห้องที่ใช้พัฒนาขาย (ช่องเปิด < 10%): ห้องน้ำแชก (Powder), ห้องโถงไม้ / ซักกร์, ห้องน้ำห้องแชก, Walk-in Pantry/ห้องเย็น, Walk-in Dressing (His & Hers)
แบบระดับ design development ต้องให้สถาปนิกและวิศวกรผู้ได้รับใบอนุญาตตรวจสอบและลงนามก่อนยื่นขออนุญาต

H3A DESIGN AND BUILD

X-UNIT Architecture Lab

โครงการ

WELL-GENWEAVE 40x40 v3

Executive Luxury Villa
บ้านเดี่ยว 3 ชั้น ผ่านเกณฑ์
WELL for Residential (เจดนา)

ที่ดิน 40.00 x 40.00 ม. = 400 ตร.ว.
ถนนสาธารณะ 8.00 ม. ติดเหนือ

แนวคิด

GENWEAVE: ลำต้น (แกนบันได+ปล่อง
Termite) แดกกิ่ง 4 ทิศ รอบคอร์ต 2 แห่ง
Crown bar ชั้น 3 = เรือนยอดบังแดด

ระดับ

±0.00 ถนน · F1 +0.60 · F2 +4.20
F3 +7.80 · หลังคา +11.40
parapet +12.00 · ปล่อง +14.00

หมายเหตุ

- หน่วยงานเิลกิตติมสร เว้นแต่ระบุ
- ระดับอ้างอิงถนนหน้าที่ดิน ±0.00
- ห้ามวัดขนาดจากถนน ใช้ตัวเลขกำกับ
- แบบระดับ Design Development

ต้องให้สถาปนิกและวิศวกรผู้ได้รับ
ใบอนุญาตตรวจสอบและลงนาม
ก่อนยื่นขออนุญาต

ชื่อแผ่น

WELL for Residential
+ วัสดุ + สิ่งที่ต้องทำต่อ

มาตราส่วน ไม่มาตราส่วน

วันที่ 1 ค.ค. 2569 ฉบับ v3 / DD