




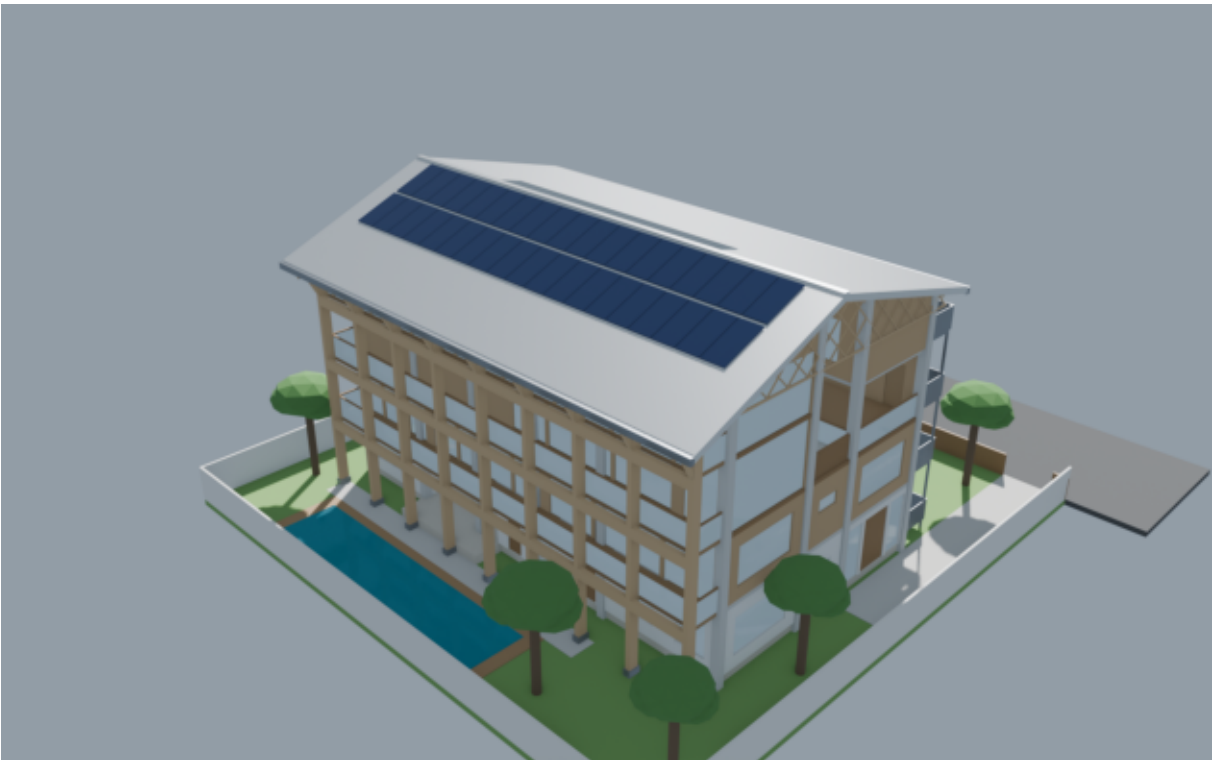


มุมมองทางอากาศ ทิศตะวันออกเฉียงใต้ — หลังคาจั่วไม้สมมาตรคลุมทั้ง 23.00 x 13.00 ม. แผงโซลาร์ลาดใต้ ช่องแสงชั้นหลังคา

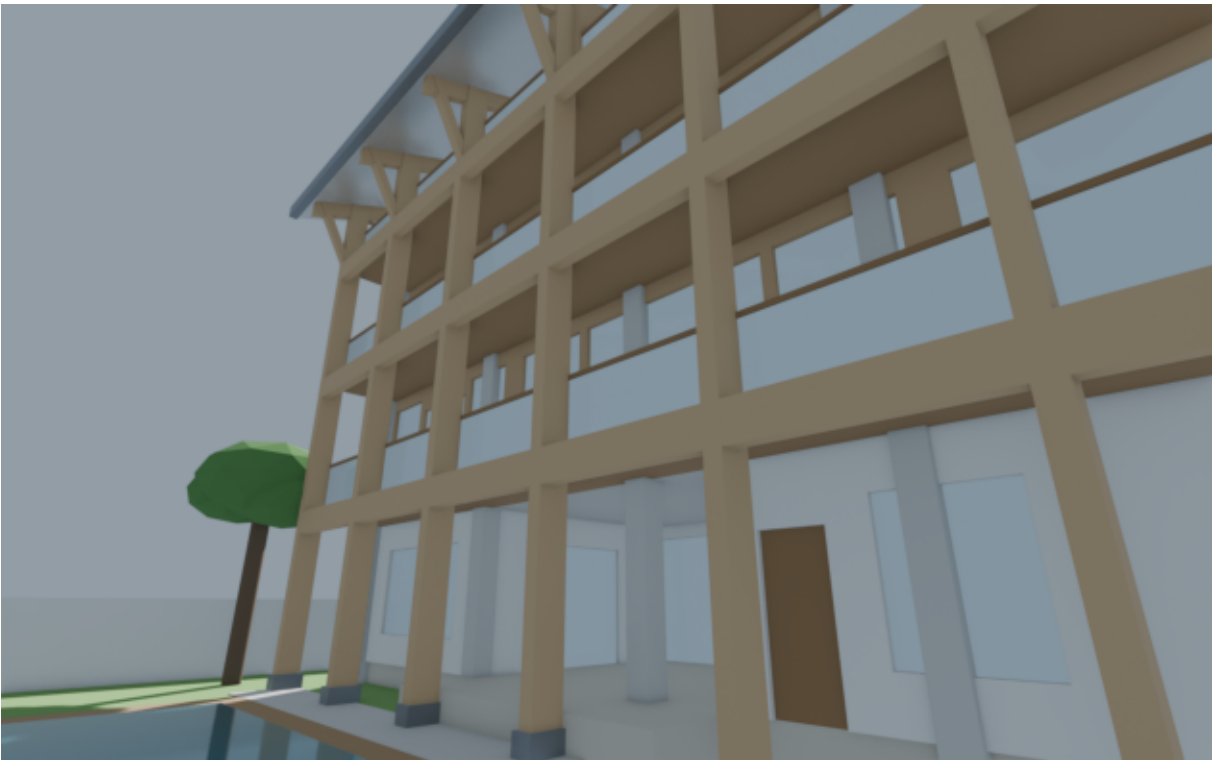


จากสวนสระทิศใต้ — เสาโครงไม้ภายนอก + ค้ำเชิงรับชายคา 3.00 ม. ระเบียงไม้ทุกชั้น ผนังกระจกเต็มบาน

โถงแรมฝั่งชั้น 1 (1:250): ทางเข้าตะวันออก -> โถงไม้ยาว -> ศาลา/สระ; เสาโครงไม้ใต้เพ็ช; แนวชายคา (เส้นประ)

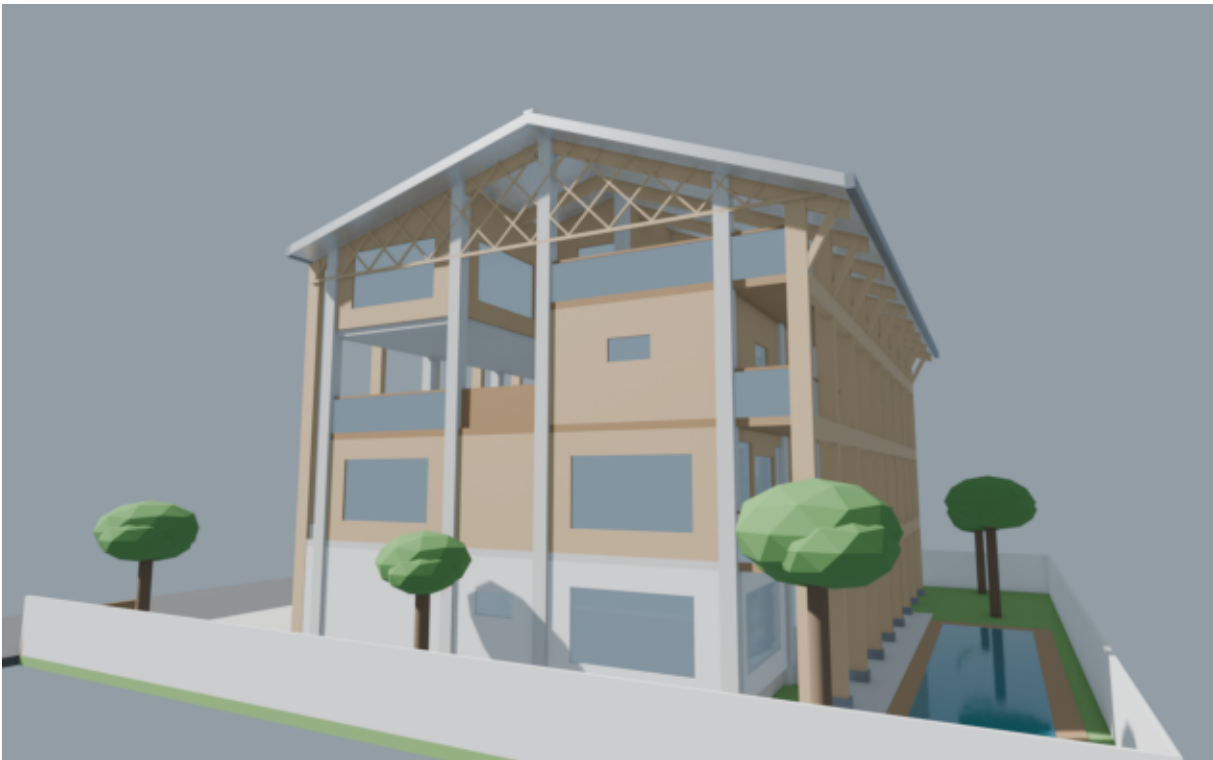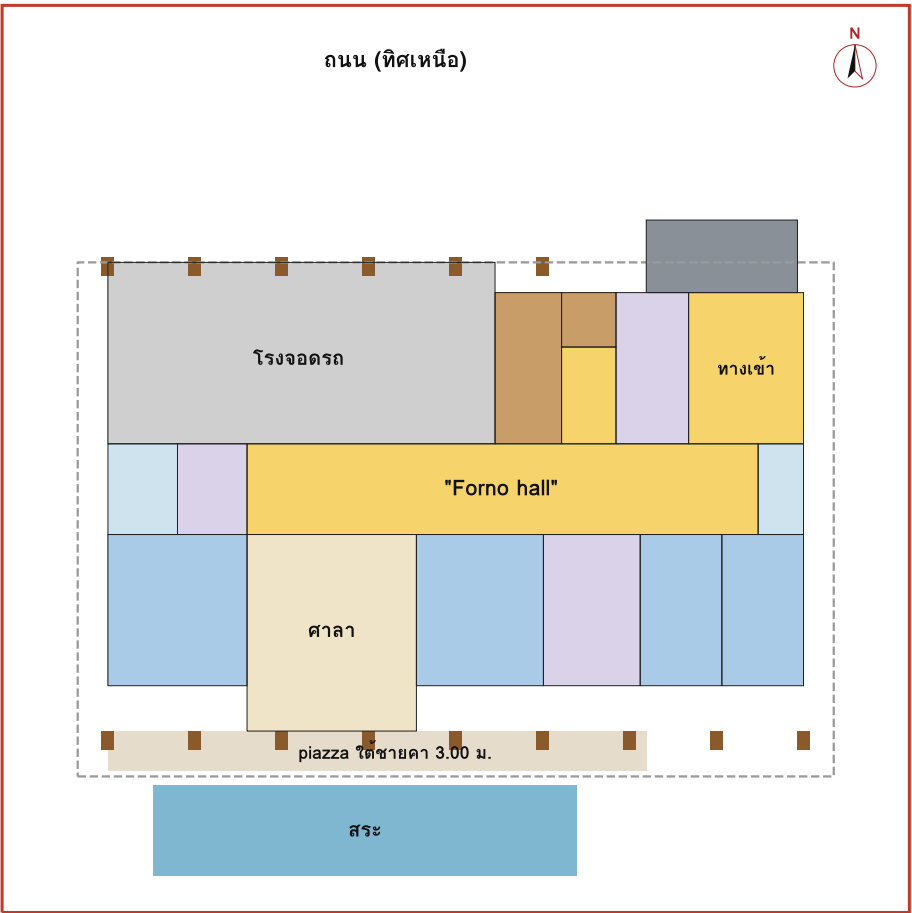


หน้าจั่วทิศตะวันตก — ระแนงไม้ทแยง คอร์ตแสงหัวท้าย และเพรชไม้ glulam ด้านใต้

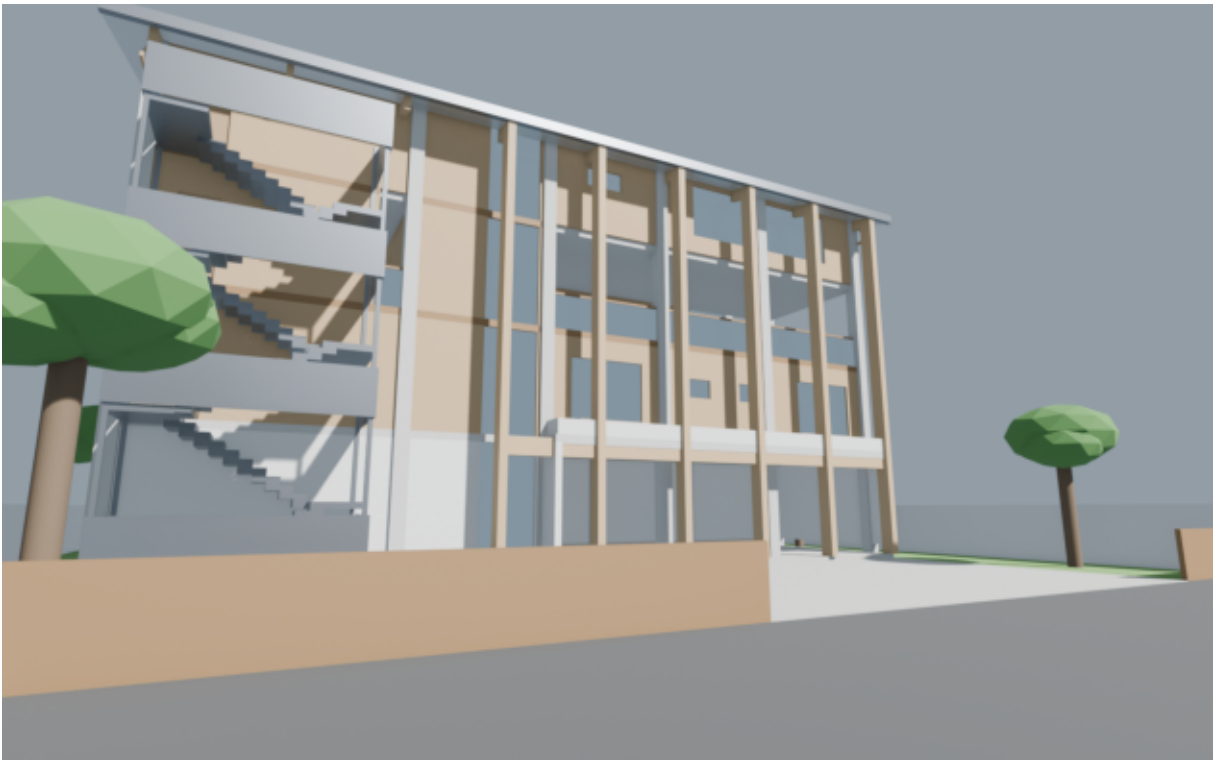

จากถนนทิศเหนือ — เสาไม้หน้าโรงจอดรถ 4 ต้น ปันโดพพีไฟเหล็ก ทางเดินเข้าบ้านทิศตะวันออก

โถงแรมรูปคัต B-B (x = 14.00, 1:250): ลมเข้าใต้ชายคา -> ห้องทิศใต้ -> โถงไม้ -> ลอยขึ้นตามช่องโถง (stack)

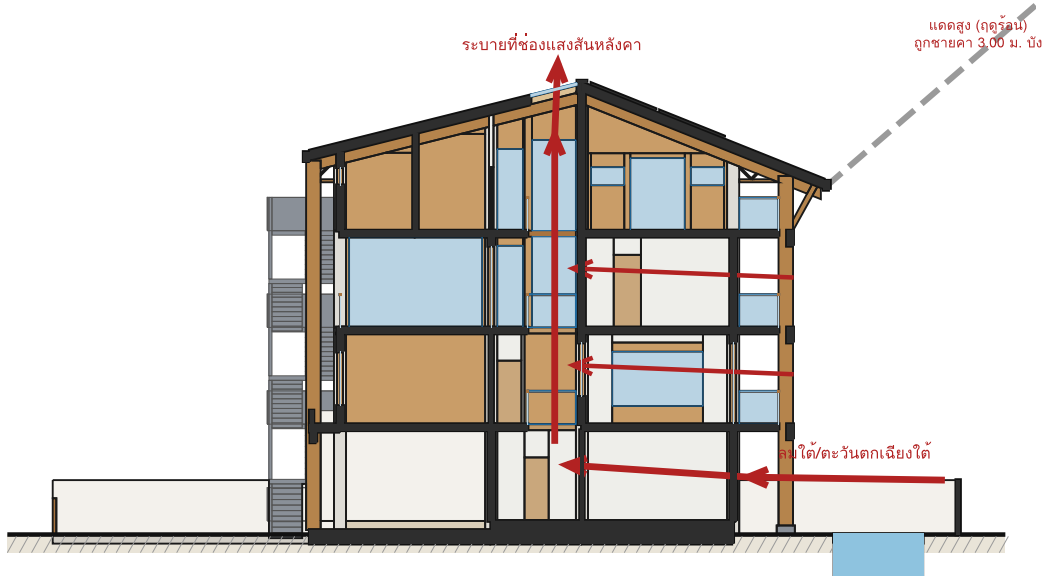

ลูกศร = เจตนารการออกแบบ (ลมปะจ้ำกรุงเพฯ ฤดูร้อน S/SW, ทิศ NE) — ยังไม่ได้พิสูจน์ด้วย CFD/การจำลองความร้อน

FORNO — ข้อเท็จจริงที่ตรงได้

หัวข้อ	ข้อเท็จจริงจากหน้า Archilizer (ข้อความ + ภาพ)
ผู้ออกแบบ	Gruppo FON Architetli
ที่ตั้ง / ปี	Treviso อิตาลี · แล้วเสร็จ 2025
ประเภท (Archilizer)	Commercial: Retail / Restaurant & Bar / Community Center — ไม่ใช่บ้านพักอาศัย
บริบท	ย่านชุมชนเมืองทิศตะวันตกเฉียงเหนือที่พัฒนาเป็นย่าน ช่างอาคาร + ลานภายนอกเปิดให้สาธารณะ ใกล้ลานจอดรถขนาดใหญ่
โครงการ	ธุรกิจแบบก่อสร้างปลีกเอกชน ได้ทุนสนับสนุนผู้ประกอบการระดับภูมิภาค · เปิด 15 ชม./วัน 7 วัน
สถาปัตยกรรม	"light wooden architecture, transparent and strongly recognizable" (ข้อความโครงการ) — เน้นคุณสมบัติของไม้
จากภาพที่เผยแพร่	โครงไม้ glulam + ค้ำเชิงรับค้ำ Y · หลังคาจั่วไม้สมมาตร ชายคายื่นลึก · ผนังกระจก · หน้าจั่วโครงไม้ทแยง · ด้านสูงเห็นผู้สวน
ไม่เผยแพร่	พื้นที่ ขนาด แบบก่อสร้าง — ทุกมิติในชุดนี้คือออกแบบใหม่

การตีความ -> แบบบ้านหลังนี้

องค์ประกอบ	การตีความของเรา (ไม่ใช่คำอธิบายของสถาปนิก)
จั่วไม้สมมาตร	หลังคาจั่วเดี่ยวคลุมทั้งหมด: ลาดใต้ 40% ชายคา 3.00 ม. คมนระเบียง/piazza · ลาดเหนือ 25% · สัน +14.95
โครงไม้ + ค้ำ Y	exoskeleton ทิศใต้ 9 เพრ @2.875 ม.: เสา glulam 240x480 + ค้ำเชิงรับปลายชายคา + คานขอบระเบียงทุกชั้น
โถงยาวเดี่ยว	"Forno hall" กว้าง 3.00 ม. ยาว 16.90 ม. โปร่ง 4 ชั้นที่ช่องแสงหลังคา มีสะพานไม้ข้ามชั้น 2-4
ความโปร่งใส	ผนังกระจกเต็มบานหลังระเบียงไม้ค้ำใต้ทุกห้องหลัก (ห้องอาหาร นั่งเล่น Master)
หน้าจั่วทแยง	ระแนงไม้ทแยงหน้าจั่วตะวันออก/ตะวันตก + คอร์ตแสงหัวท้ายชั้น 3-4
ลานสาธารณะ / เสาอบ	piazza ใต้ชายคา + ศาลาริมสระ + เสาอบหิน (forno) + ใต้ยาวในโถงกลาง
ไม้เข้ามาใช้	ไม้เป็นโครงสร้างหลัก (บ้าน 4 ชั้นใช้ ค.ส.ล.) · กระถางรอบด้าน (กระถาง/กระถางรวม)

รายงานข้อจำกัด (ตรงไปตรงมา)

- FORNO เป็นอาคารพาณิชย์ชั้นเดียว ไม่ใช่บ้าน — การแปลงเป็นบ้าน 4 ชั้นและทุกมิติเป็นการตีความของเรา
- "โครงไม้ภายนอกทุกชั้น" ไม่ใช่โครงสร้างหลัก: โครงหลัก ค.ส.ล. (อาคาร 3 ชั้นขึ้นไปต้องใช้โครงสร้างท่อน้ำ) ไม่ใช่ระเบียง/ชายคา; โครงหลังคาและแนบไม่ต้องให้วิศวกรตรวจสอบทานไฟ
- โปรแกรมชดกัน: Master ชั้น 3 แต่ Closet + Terrace ชั้น 4 -> Master duplex มีบันไดส่วนตัว; Pantry ชั้น 3 ย้ายไปชั้น 2 คัดครัว
- SFA 1200.28 vs โปรแกรม 984.70 (+21.9%); พื้นภายนอกชั้น 3 129.5 + ชั้น 4 103.5 ตร.ม. เพราะโปรแกรมชั้น 3 มีแค่ 120 ตร.ม. แต่เพ่งอาคารทุกชั้นเท่านั้น
- เล็กกว่าโปรแกรมเกิน 10%: โถงไม้ 31%, ห้องน้ำแบบบ้าน -25%, โถงคอร์ตชั้น -21% (ความสูง 2 ชั้นได้จากโถงไม้ข้างกัน), เสาคอร์ต -14%, MEP -14%, โรงรถ -10% (A-11)
- ระยะชนเกณฑ์: สันหลังคา +14.95 (ต่ำกว่า 15.00 แค่ 0.05); ชั้น 4 โปร่ง 2.60 หลังค้ำหลังชายคา; สันค้ำคานคองเป็นฐาน overhead <= 2.60 ม.
- ทางเข้าบันไดพพีไฟ ชั้น 2 ผ่านห้องทำงาน ชั้น 4 ผ่านห้องเฮลิคอป (ห้ามลืกลูปประตู) — ต้องยื่นยื่นขอ 27 กับสำนักงานเขตสำหรับบ้านเดี่ยว
- โถงโปร่ง 4 ชั้นเชื่อมทุกชั้น — ครัวไฟลานชั้นใต้: คองมีเครื่องครัวจริงครัวของระบบคานที่สั้นหลังค้ำ; ช่องเปิดโถงไม้บันเป็นช่องเปิด จ.39
- ช่องเปิดคานเดี่ยวค้ำคาน 4.20 ม. (ยกเว้นพุ่มไม้หลังค) แบบบ้าน 1 Junior Suite 3. ห้องทำงาน: ห้องนั่งเล่นคอร์ตครัว; ใช้คอร์ตระบบ 11 ห้อง (A-12)
- ไม้ภายนอกในโถงอากาศหรือชั้น: คอร์ตค้ำน้ำชายคาปลาย/เขี้ยว เคลือบกัน UV ฐานเคลือบพื้นคาน 0.30 ม. และประตูทุก 2-3 ปี; คอร์ตเปิดหัวท้ายรับฝนสาค คองมีท่อระบายของคานคอง
- ความกว้างถนนเดิมค 8.00 ม.; ทางลาดโรงรถ +0.15 -> +0.45 ยังไม่เขียน; ไม่ทราบหลังฝั่งรวม/ข้อบัญญัติท้องถิ่น — ต้องตรวจก่อนยื่น

แหล่งข้อมูลอ้างอิง FORNO

· archilizer.com/projects/forno-1 (ลิงก์ที่ผู้ใช้นิยาม) — อ่านข้อความโครงการและรูปภาพเมื่อ 6 ค.ศ. 2569

ไม่ได้รับแบบจริงของโครงการ — ไม่มีขนาดพื้นที่ของงานต้นแบบ

H3A DESIGN AND BUILD

X-UNIT Architecture Lab

โครงการ

WELL-FORNO 30x30

Executive Luxury Villa

บ้านเดี่ยว 4 ชั้น ผ่านเกณฑ์

WELL for Residential (เจคนา)

ที่ดิน 30.00 x 30.00 ม. = 225 ตร.ว.

ถนนสาธารณะทิศเหนือ (สมมติ 8.00 ม.)

แนวคิด

ตีความจาก FORNO (Gruppo FON):

โครงไม้ glulam ภายนอกทุกชั้น + ค้ำเชิง

+ หลังคาจั่วไม้สมมาตร ชายคาใต้ 3.00

+ โถงไม้ "Forno hall" โปร่ง 4 ชั้น

ระดับ

±0.00 ถนน · F1 +0.45 · F2 +3.65

F3 +6.85 · F4 +10.05

หลังคาที่แนวผนัง +12.95

สันหลังคา +14.95

หมายเหตุ

· หน่วยงานเป็นลิขสิทธิ์ เว้นแต่ระบุ

· ระดับอ้างอิงถนนพื้นที่ดิน ±0.00

· ห้ามวัดขนาดจากแบบ ใช้ตัวเลขกำกับ

· แบบระดับ Design Development

ต้องให้สถาปนิกและวิศวกรผู้ได้รับ

ใบอนุญาตตรวจสอบและลงนาม

ก่อนยื่นขออนุญาต


ชื่อแผ่น

แนวคิด FORNO -> บ้านโครงไม้

+ รายงานข้อจำกัด

มาตราส่วน: ไม่มีมาตราส่วน

วันที่ 6 ค.ศ. 2569 ฉบับ v1 / DD

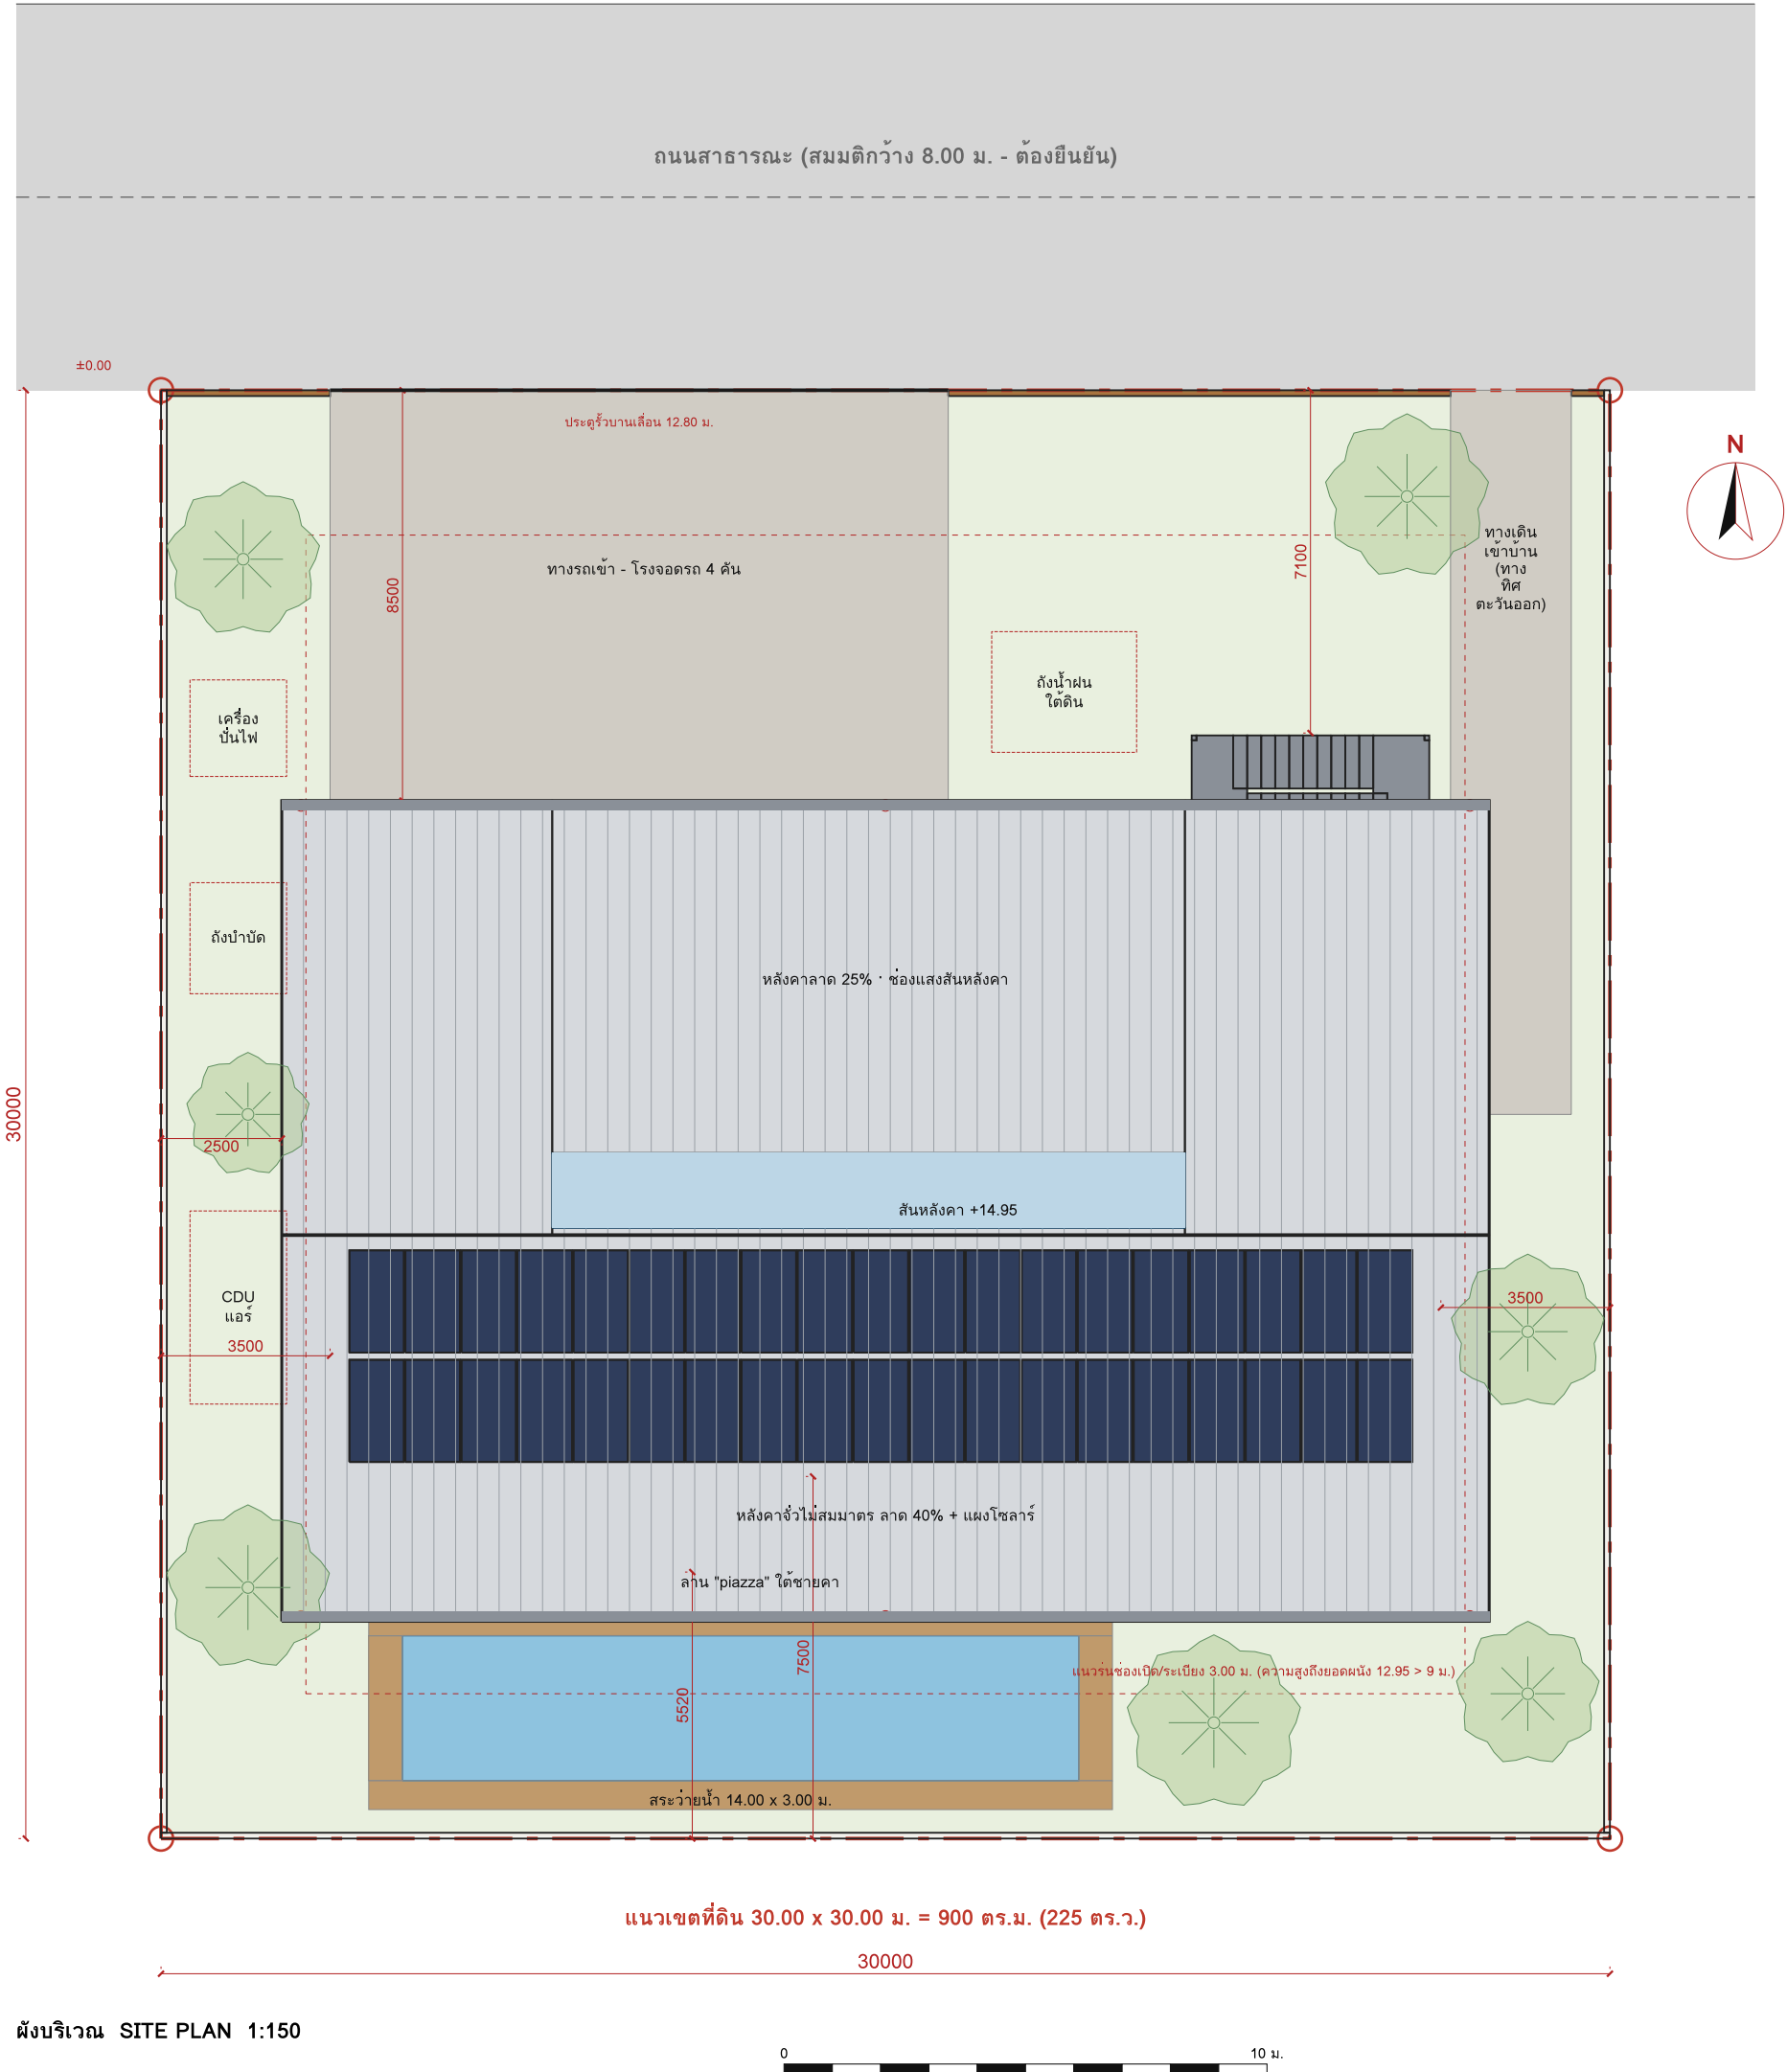

ตารางกฎกระทรวง ฉบับที่ 55 (2543) และระยะร่น

ชั้น	รายการ	ค่าในแบบ	เกณฑ์	ผล
ชั้น 20	ห้องนอนแยก/ห้องอาบ	23.00 ตร.ม. (ด้านแคบ 4.60)	>= 8.00 ตร.ม.	ผ่าน
ชั้น 20	ห้องนอนบ้าน 1	13.50 ตร.ม. (ด้านแคบ 2.70)	>= 8.00 ตร.ม.	ผ่าน
ชั้น 20	ห้องนอนบ้าน 2	13.50 ตร.ม. (ด้านแคบ 2.70)	>= 8.00 ตร.ม.	ผ่าน
ชั้น 20	ห้องนอน Junior Suite 2	20.00 ตร.ม. (ด้านแคบ 4.00)	>= 8.00 ตร.ม.	ผ่าน
ชั้น 20	ห้องนอน Junior Suite 3	20.00 ตร.ม. (ด้านแคบ 4.00)	>= 8.00 ตร.ม.	ผ่าน
ชั้น 20	ห้องนอน Master Suite	48.00 ตร.ม. (ด้านแคบ 5.00)	>= 8.00 ตร.ม.	ผ่าน
ชั้น 22	ความสูงโปร่งห้อง ชั้น 1-3 (FF 3.20 - พื้น 0.20	2.80 ม.	>= 2.60 ม.	ผ่าน
ชั้น 22	ชั้น 4 โถงหลังคาลาด: ห้องนั่งเล่นครอบครัว & Up	2.60 / 3.85 ม.	>= 2.60 ม.	ผ่าน
ชั้น 22	ชั้น 4 โถงหลังคาลาด: ห้องโถงเชื่อมต่อ (ด้านนอก)	2.60 / 3.85 ม.	>= 2.60 ม.	ผ่าน
ชั้น 22	ชั้น 4 Walk-in Closet (ห้องเก็บของเสื้อผ้า)	2.60 / 4.60 ม.	>= 2.60 ม.	ผ่าน
ชั้น 22	โถงไม้ "Forno hall" (โปร่ง 4 ชั้น ถึงช่องแสง)	14.20 ม.	>= 2.60 ม.	ผ่าน
ชั้น 23	บันไดหลัก (โถงไม้): ลูกตั้ง (สูงสุด) / ลูกนอน	160.0 / 290 มม.	<= 200 / >= 220	ผ่าน
ชั้น 23	บันไดหลัก (โถงไม้): ขานหลัก (ลึก)	1000 มม.	<= 800	ผ่าน
ชั้น 23	บันไดส่วนหัว Master ชั้น 3-4: ลูกตั้ง (สูงสุด)	160.0 / 290 มม.	<= 200 / >= 220	ผ่าน
ชั้น 23	บันไดส่วนหัว Master ชั้น 3-4: ความกว้าง	1000 มม.	>= 800	ผ่าน
ชั้น 23	บันไดส่วนหัว Master ชั้น 3-4: ขานหลัก (ลึก)	1000 มม.	>= ความกว้าง 1000	ผ่าน
ชั้น 23	บันไดหลักในภายนอก: ลูกตั้ง (สูงสุด) / ลูกนอน	182.5 / 290 มม.	<= 200 / >= 220	ผ่าน
ชั้น 23	บันไดหลักในภายนอก: ความกว้าง	1100 มม.	>= 800	ผ่าน
ชั้น 23	บันไดหลักในภายนอก: ขานหลัก (ลึก)	1150 มม.	>= ความกว้าง 1100	ผ่าน
ชั้น 23	ขอบบันไดสูงต่อข้าง	1.60 ม. (10 ชั้น)	<= 3.00 ม.	ผ่าน
ชั้น 23	ระยะโปร่งเหนือชั้นบันได	>= 2.84 ม.	>= 1.90 ม.	ผ่าน
ชั้น 23	2R+T	610 มม.	600-650	ผ่าน
ชั้น 27	อาคาร 4 ชั้น: มีบันไดหนีไฟไม่ใช้แนวตั้ง	บันไดเหล็กภายนอก กว้าง 1.10 ม. ชั้นปร	5 / กว้าง >= 0.80 / ชั้น <	ผ่าน
ชั้น 27	ทางเข้าบันไดหนีไฟทุกชั้น	ชั้น 2: ห้องส่งงาน, ชั้น 3: คลองขยะ	มีทางเข้าทุกชั้น	ผ่าน
ชั้น 33	ที่ว่าง (นับต่อพื้นที่อาคาร)	52.0% (คลุมดิน 432.00 ตร.ม.)	>= 30%	ผ่าน
ชั้น 33	ที่ว่าง (นับต่อพื้นที่อาคาร)	52.0%	>= 30%	ผ่าน
ชั้น 50	ช่องเปิดลิ้นชักชุดลิ้น (อาคารสูง 12.95 ม.)	3.50 ม. (D02 F1 โถงคั่นบัน (ทางเข้า)	>= 3.00 ม.	ผ่าน
ชั้น 50	ระเบียง/ช่องเปิดบันไดหนีไฟ ลิ้นชักชุด	3.50 ม.	>= 3.00 ม.	ผ่าน
ชั้น 50	ชายคา/เสาโครงไม้/เสา ลิ้นชักชุด	2.50 ม.	>= 0.50 ม.	ผ่าน
ชั้น 50	ผนังอาคารลิ้นชักชุด (ชายคาหลัง)	3.50 ม.	>= 3.00 ม. (มีช่องเปิด, ฐ	ผ่าน
บันไดภายนอก	อาคาร/ชายคา (โถงรถ) ถึงเขตทาง (ถนนสมมติ 8.00 ม	8.50 ม.	>= 1/10 ความกว้างถนน = 0.8	ผ่าน

* จำนวนถนน: อาคารสูงไม่เกิน 15 ม. ถนนกว้าง 6-20 ม. รัน 1/10 ของความกว้างถนน (ความกว้างถนนเป็นค่าสมมติ — ควรใช้กับข้อบัญญัติท้องถิ่น)

พื้นที่อาคาร (คิดถึงแนวศูนย์กลางผนัง)

ชั้น	ปิดล้อม*	กึ่งภายนอก	จอดรถ	บันไดหนีไฟ	รวม ตร.ม.
ชั้น 1	207.00	36.40	76.80	12.00	320.20
ชั้น 2	278.66	34.50	-	12.00	313.16
ชั้น 3	153.96	129.50	-	12.00	283.46
ชั้น 4	179.96	103.50	-	12.00	283.46
รวม	619.58	303.90	76.80	48.00	1200.28
ส่วนกลาง					+215.58 (+21.9%)

* ไม่นับช่องโถงโถงไม้ - ส่วนใต้ชายคาชั้น 1 = ศาลาพักผ่อนบันไดภายนอก (กึ่งภายนอก) - บันไดหนีไฟไม้

ที่ว่างและการใช้ที่ดิน

รายการ	ค่า
พื้นที่ดิน	900.00 ตร.ม. (225 ตร.ว.)
พื้นที่อาคารคลุมดิน (รวมชายคาบันไดหนีไฟ)	432.00 ตร.ม. (48.0%)
ที่ว่าง	52.0% (เกณฑ์ >= 30%)
FAR (GFA ปิดล้อม / ที่ดิน)	0.91 : 1
ความสูงอาคาร	ยอดหนึ่งชั้นบนสุด 12.95 (33'10"หลังคาจั่ว) / ส่วนหลังคา 14.95 ม. (< 15.00)
ที่ดินยื่นเข้าตามโปรแกรม	113 ตร.ว. — ที่ดินจริง 225 ตร.ว.

ประมาณราคาค่าก่อสร้าง (ระดับแนวคิด)

วัสดุ	สูตร (บาท/ตร.ม.)	คำนวณ
(ก) อัตราแยกมาตรฐาน	ปิดล้อม 819.58 x 22.000 + กึ่งภายนอก 303.90 x 11.000 + จอดรถ 76.80 x 8.000	21.99
(ข) อัตราแยก luxury	ปิดล้อม x 30.000 + กึ่งภายนอก x 15.000 + จอดรถ x 12.000	30.07
(ค) อัตราเดี่ยว (ใช้เดียวกับโปรแกรม)	GFA 1200.28 x 30.000	36.01
งานสถาปัตย์	สร= 42.0 ตร.ม. x 35.000 + PV 20.00 kWh x 45.000 + ภูมิทัศน์ทั่วไป 1.80 + ลิฟท์ 0.90 + บันไดหนีไฟ 1.20 + โครงไม้หลังคา glulam 2.50 a.	8.81
โปรแกรม ARCHSPACE	984.70 x 30.000 (ช่วง 26.00-36.93 ล้าน)	29.54

อัตราแยก vs อัตราเดี่ยว: (ก) 21.99 ล้าน ค่าว่างโปรแกรม: (ข) 30.07 ล้าน อยู่ในช่วง 26.00-36.93; (ค) 36.01 ล้าน และขอบบนของช่วง เพราะ GFA มากกว่าโปรแกรม 21.9%

รวมรวมแยกอาคาร: (ข)+8.81 = 38.88 ล้าน · (ค)+8.81 = 44.82 ล้าน (ใช้ช่วงบนของโปรแกรม)

ยังไม่รวม: เสาเข็มฐานราก (จะแยกเจดีย์), เฟอร์นิเจอร์ลอยตัว, ภาษีค่าธรรมเนียม, ค่าออกแบบ

H3A DESIGN AND BUILD

X-UNIT Architecture Lab

โครงการ

WELL-FORNO 30x30

Executive Luxury Villa

บ้านเดี่ยว 4 ชั้น ผ่านเกณฑ์

WELL for Residential (เจดีย์)

ที่ดิน 30.00 x 30.00 ม. = 225 ตร.ว.

ถนนสาธารณะติดเหนือ (สมมติ 8.00 ม.)

แนวคิด

ตีความจาก FORNO (Gruppo FON):

โครงไม้ glulam ภายนอกทุกชั้น + ค้ำเชิง

+ หลังคาจั่วไม้สมมาตร ชายคาใต้ 3.00

+ โถงไม้ "Forno hall" โปร่ง 4 ชั้น

ระดับ

±0.00 ถนน · F1 +0.45 · F2 +3.65

F3 +6.85 · F4 +10.05

หลังคาที่แนวหนึ่ง +12.95

พื้นหลังคา +14.95

หมายเหตุ

· หน่วยงานเป็นผลิตภัณฑ์ เว้นแต่ระบุ

· ระดับอ้างอิงถนนพื้นที่ดิน ±0.00

· ห้ามวัดขนาดจากแบบ ใช้ตัวเลขกำกับ

· งบประมาณ Design Development

ต้องให้สถาปนิกและวิศวกรผู้ได้รับ

ใบอนุญาตตรวจสอบและลงนาม

ก่อนยื่นขออนุญาต


ชื่อแผ่น

ผังบริเวณ + ตารางกฎหมาย

+ ประมาณราคา

มาตราส่วน 1:150

วันที่ 6 ค.ด. 2569 ฉบับ v1 / DD

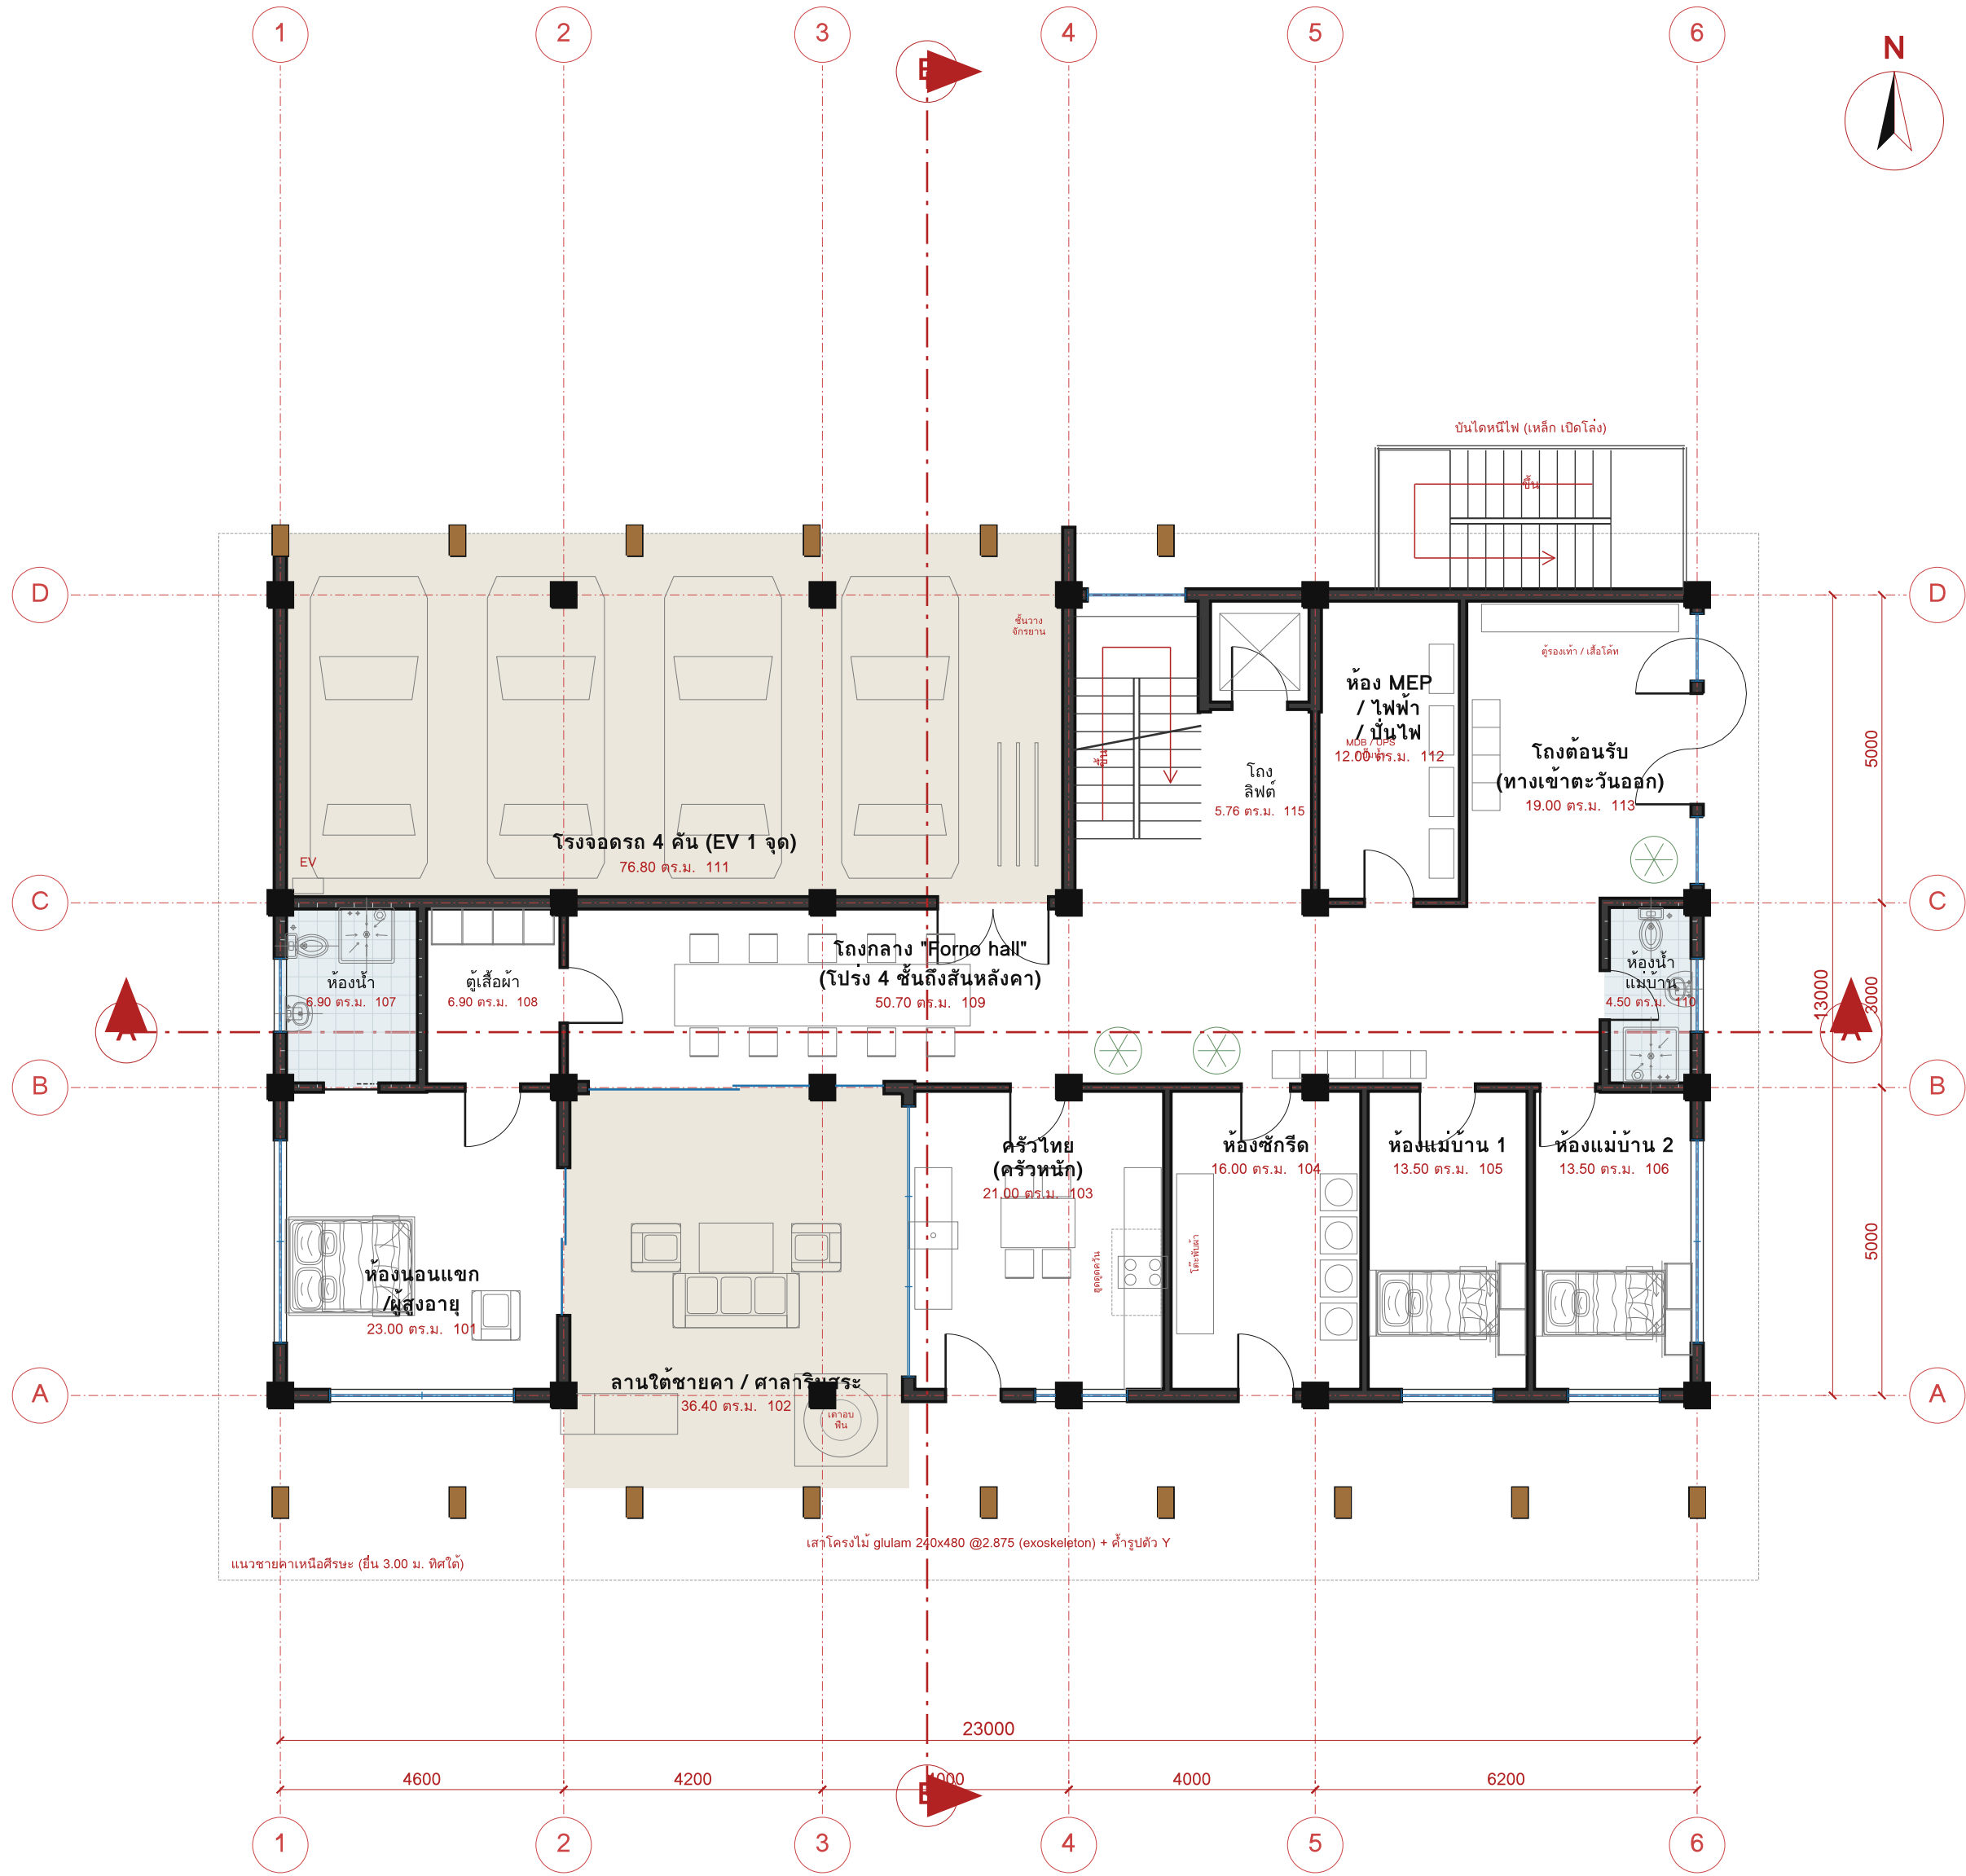

ผังพื้นชั้น 1 (FFL +0.45) 1:100

ตารางห้อง ชั้น 1

รหัส	ห้อง	ขนาด ม.	ตร.ม.	ประเภท
101	ห้องนอนแขก/ผู้สูงอายุ	4.60 x 5.00	23.00	ห้องใช้งาน
102	ลานใต้ชายคา / ศาลาริมนสระ	5.60 x 6.50	36.40	ที่ภายนอก
103	ครัวไทย (ครัวหลัก)	4.20 x 5.00	21.00	ห้องใช้งาน
104	ห้องซักรีด	3.20 x 5.00	16.00	บริการ
105	ห้องนอน 1	2.70 x 5.00	13.50	ห้องใช้งาน
106	ห้องนอน 2	2.30 x 3.00	6.90	ห้องใช้งาน
107	ห้องน้ำ	2.30 x 3.00	6.90	ห้องน้ำ
108	ตู้เสื้อผ้าห้องแขก	2.30 x 3.00	6.90	บริการ
109	โถงกลาง "Forno hall"	16.90 x 3.00	50.70	สโตน
110	โรงจอดรถ 4 คัน	1.50 x 3.00	4.50	ที่จอดรถ
111	โรงจอดรถ 4 คัน	12.80 x 6.00	76.80	จอดรถ
112	ห้อง MEP / ไฟฟ้า / เครื่องปรับอากาศ	2.40 x 5.00	12.00	บริการ
113	โถงต้อนรับ (ทางเข้าทิศตะวันออก)	3.80 x 5.00	19.00	สโตน
114	บันไดหลัก (โถงไม่)	2.20 x 5.00	11.00	บันได
115	โถงลิฟต์	1.80 x 3.20	5.76	สโตน
116	ลิฟต์บ้าน	1.80 x 1.80	3.24	ลิฟต์
117	บันไดหนีไฟภายนอก	5.00 x 2.40	12.00	บันไดหนีไฟ

ส่วนชั้น 1	ตร.ม.
พื้นที่อาคาร	207.00
ที่ภายนอก	36.40
จอดรถ	76.80
รวม	320.20
บันไดหนีไฟภายนอก (ไม่รวม)	12.00

หมายเหตุ

- ทางเข้าหลักทิศตะวันออก (ทางเดินจากถนนข้างรั้ว) -> โถงต้อนรับ -> โถงกลาง "Forno hall" กว้าง 3.00 ม. ไปยังห้องและพื้นที่กลางแจ้ง
- โถงกลางเปิดกว้าง 4.80 ม. ศาลาริมนสระ (piazza ใต้ชายคา) — โต๊ะยาว + เคาบหิน (forno) ตามแนวคิดแบบ
- โรงจอดรถ 4 คัน ด้านหน้าเปิด เสาไม้ glulam @2.875 ม. เป็นช่องจอด (ช่องว่างระหว่างเสา 2.64 ม.) ประตูอัตโนมัติ โถงกลาง: ทางลาด 1:12 ต้องเพิ่ม
- ห้องนอนแขก (ผู้สูงอายุ) มุมตะวันตกเฉียงใต้ เข้าทางตู้เสื้อผ้า เปิดสู่ศาลา · ครัวไทยมีประตูบริการที่ติด
- จุดชาร์จรถไฟฟ้า (EV) 1 จุดในโรงรถ (WELL R-A09) · เสาไม้หัดได้ตั้งบนฐานหลัสูง 0.30 ม.

H3A DESIGN AND BUILD

X-UNIT Architecture Lab

โครงการ

WELL-FORNO 30x30

Executive Luxury Villa

บ้านเดี่ยว 4 ชั้น ผ่านเกณฑ์

WELL for Residential (เจดนา)

ที่ดิน 30.00 x 30.00 ม. = 225 ตร.ว.
ถนนสาธารณะติดเหนือ (สมมติ 8.00 ม.)

แนวคิด

ตีความจาก FORNO (Gruppo FON):
โครงไม้ glulam ภายนอกทุกชั้น + ค้ำเชิง
+ หลังคาจั่วไม่สมมาตร ชายคาใต้ 3.00
+ โถงไม้ "Forno hall" โปร่ง 4 ชั้น

ระดับ

±0.00 ถนน · F1 +0.45 · F2 +3.65
F3 +6.85 · F4 +10.05
หลังคาที่แนวหนึ่ง +12.95
สันหลังคา +14.95

หมายเหตุ


- หน่วยเป็นมิลลิเมตร เว้นแต่ระบุ
- ระดับอ้างอิงถนนที่ ±0.00
- ห้ามวัดขนาดจากแบบ ใช้ตัวเลขกำกับ
- แบบระดับ Design Development
- ต้องให้สถาปนิกและวิศวกรผู้ได้รับใบอนุญาตตรวจสอบและลงนามก่อนยื่นขออนุญาต

ชื่อแผ่น

ผังพื้นชั้น 1
(FFL +0.45)

มาตราส่วน 1:100

วันที่ 6 ค.ศ. 2569 ฉบับ v1 / DD

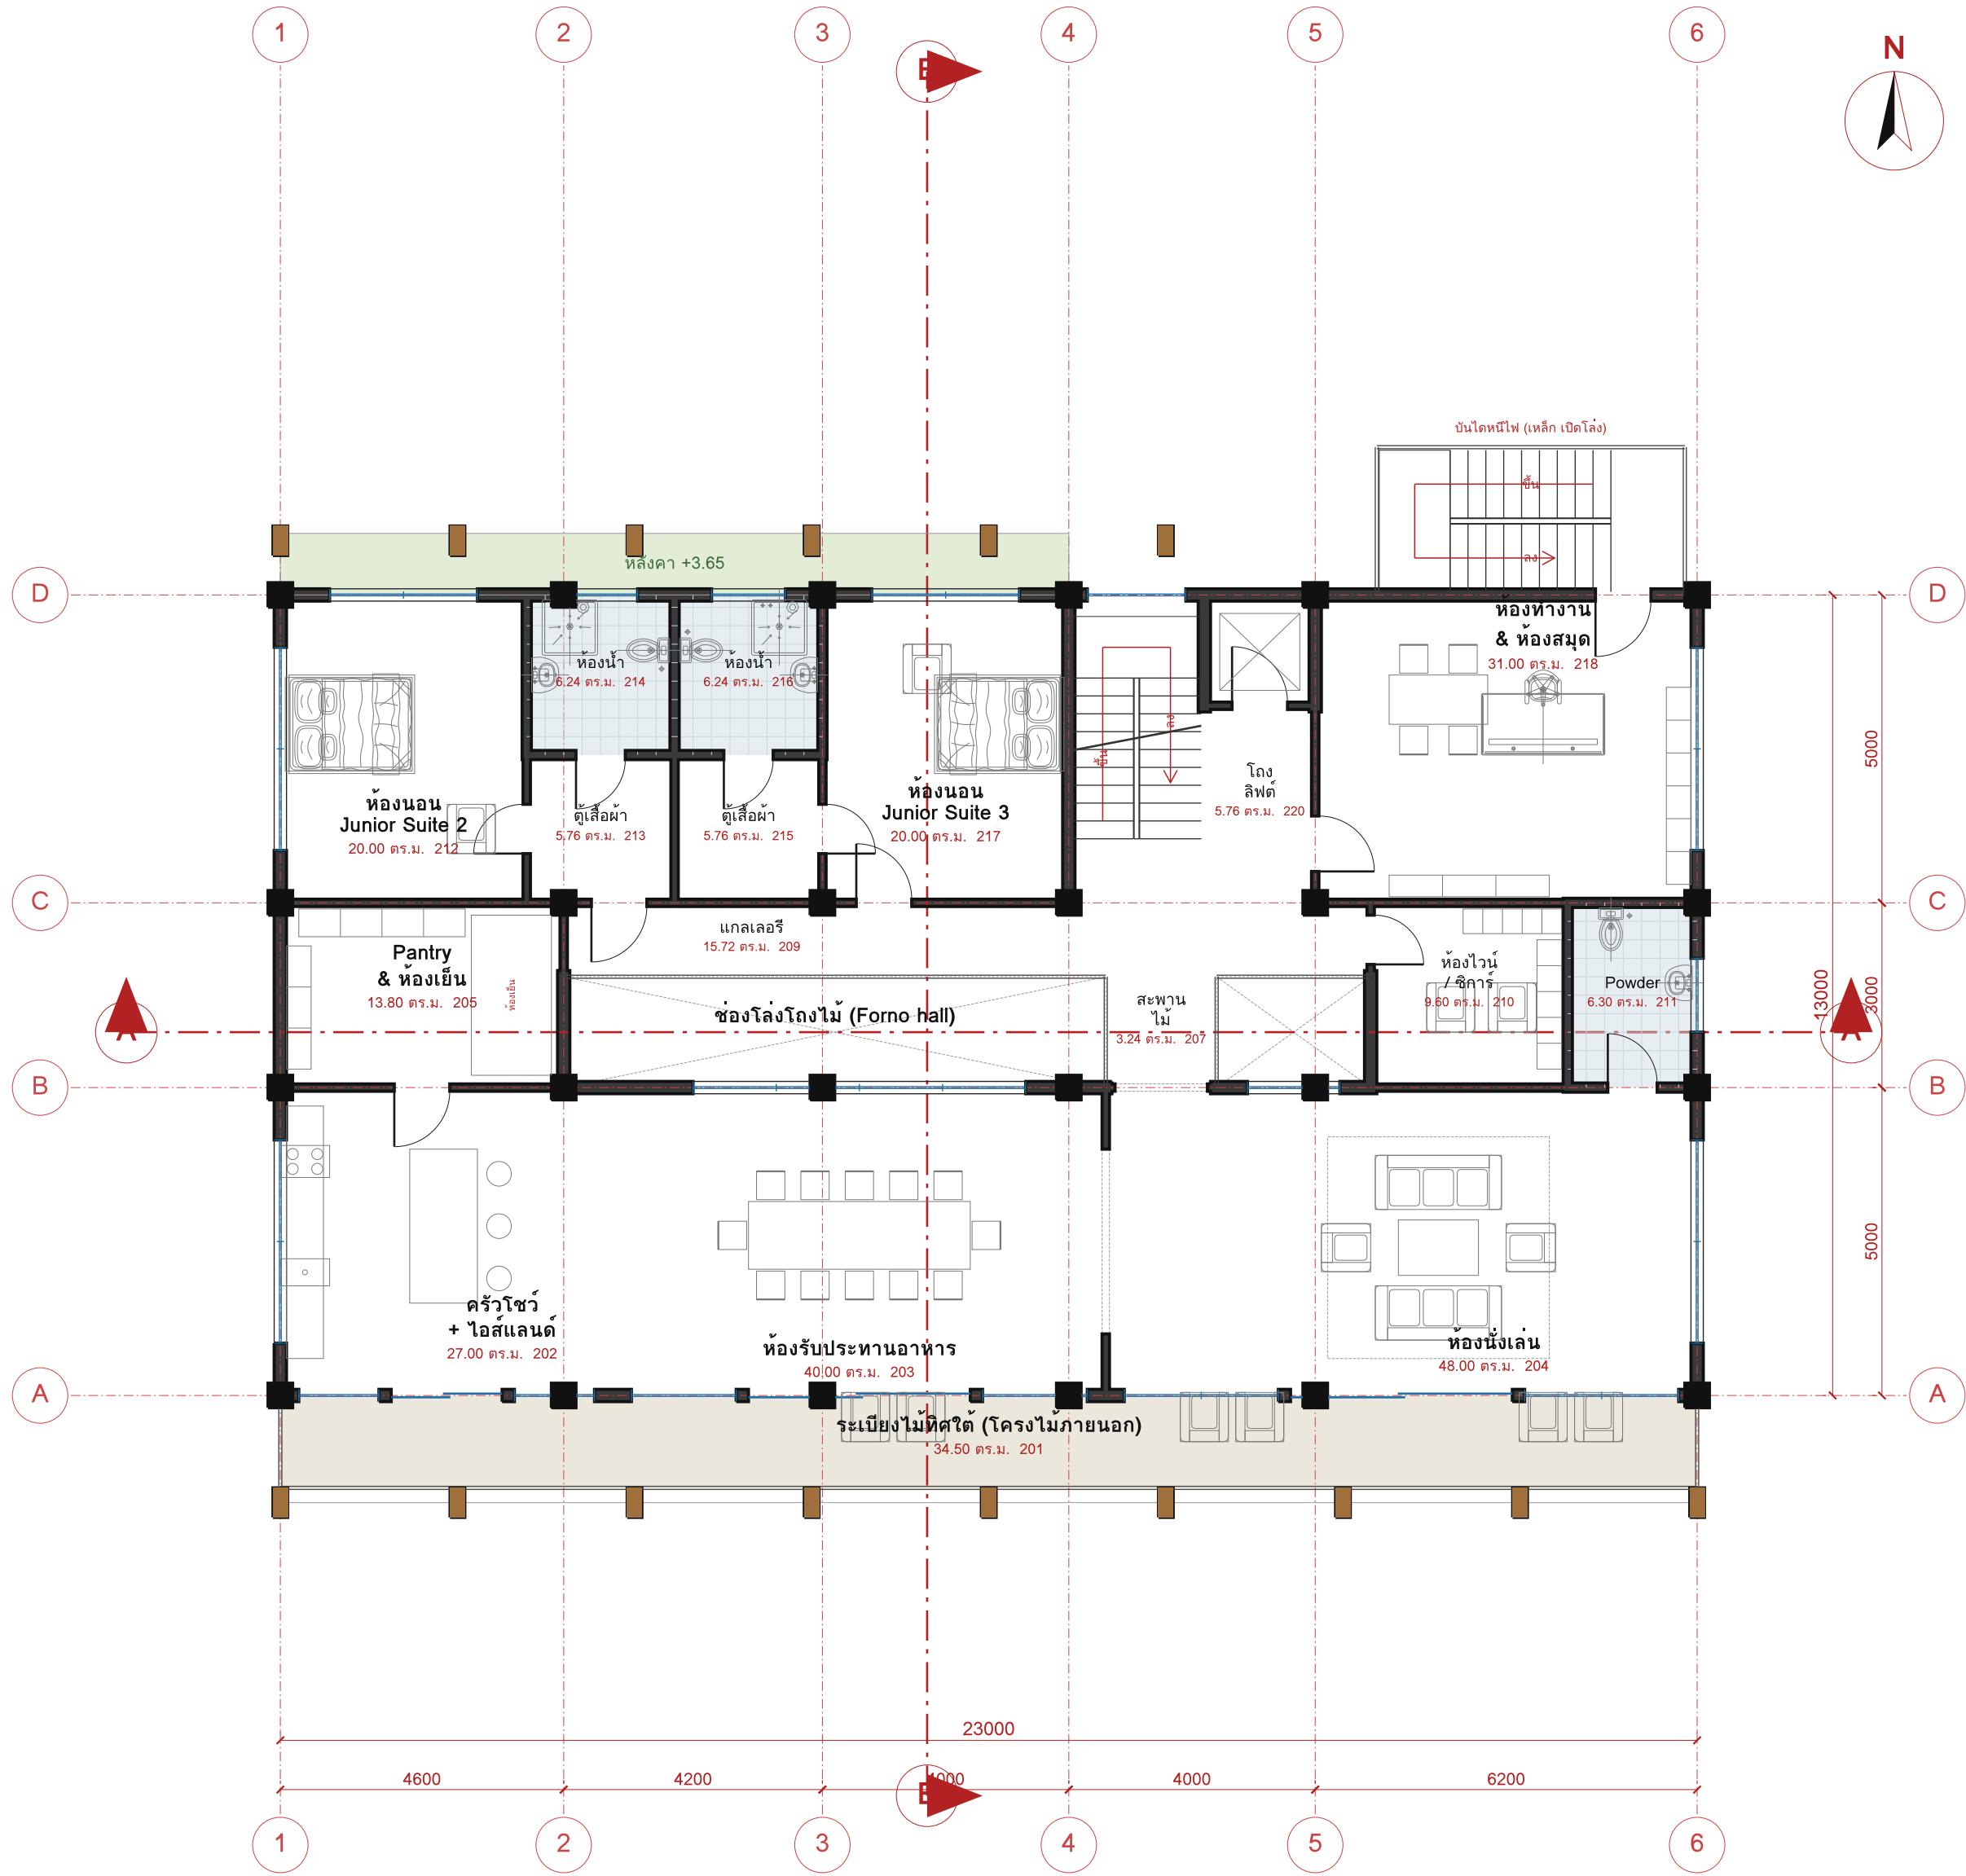

ผังพื้นชั้น 2 (FFL +3.65) 1:100



ตารางห้อง ชั้น 2

รหัส	ห้อง	ขนาด ม.	ตร.ม.	ประเภท
201	ระเบียงไม้ทิศใต้ ชั้น 2	23.00 x 1.50	34.50	ที่ภายนอก
202	ครัวโชว์ + ไอส์แลนด์	5.40 x 5.00	27.00	ห้องใช้งาน
203	ห้องรับประทานอาหาร	8.00 x 5.00	40.00	ห้องใช้งาน
204	ห้องนั่งเล่น	9.60 x 5.00	48.00	ห้องใช้งาน
205	Walk-in Pantry & ห้องเย็น	4.60 x 3.00	13.80	บริการ
206	ช่องโถงโถงไม้ ชั้น 2	8.80 x 1.80	20.34	ช่องโถง
207	สะพานไม้ ชั้น 2	1.80 x 1.80	3.24	สัญจร
209	ทางเดินจากเฉลย ชั้น 2	13.10 x 1.20	15.72	สัญจร
210	ห้องโถง / ซักรีด	3.20 x 3.00	9.60	บริการ
211	ห้องน้ำเช็ก (Powder)	2.10 x 3.00	6.30	ห้องน้ำแยก
212	ห้องนอน Junior Suite 2	4.00 x 5.00	20.00	ห้องใช้งาน
213	ตู้เสื้อผ้า Junior Suite 2	2.40 x 2.40	5.76	บริการ
214	ห้องน้ำ Junior Suite 2	2.40 x 2.60	6.24	ห้องน้ำแยก
215	ตู้เสื้อผ้า Junior Suite 3	2.40 x 2.40	5.76	บริการ
216	ห้องนอน Junior Suite 3	2.40 x 2.60	6.24	ห้องน้ำแยก
217	ห้องนอน Junior Suite 3	4.00 x 5.00	20.00	ห้องใช้งาน
218	ห้องทำงาน & ห้องสมุด	6.20 x 5.00	31.00	ห้องใช้งาน
219	บันไดหลัก (โถงไม้)	2.20 x 5.00	11.00	บันได
220	โถงลิฟต์ ชั้น 2	1.80 x 3.20	5.76	สัญจร
221	ลิฟต์บ้าน	1.80 x 1.80	3.24	ลิฟต์
222	บันไดหนีไฟภายนอก	5.00 x 2.40	12.00	บันไดหนีไฟ

รายละเอียด	ตร.ม.
พื้นที่อาคาร	278.66
ที่ภายนอก	34.50
เฉลย	0.00
รวม	313.16
บันไดหนีไฟภายนอก (ไม่รวม)	12.00

หมายเหตุ

- ส่วนรวมทิศใต้: ครัวโชว์ -> ห้องอาหาร 12 ที่นั่ง -> ห้องนั่งเล่น ผนังกระจกเต็มบานออกกระเบื้องไม้ยาว 23.00 ม.
- สะพานไม้ข้ามโถงไม้จากเฉลย (หน้าบันได) สู่ห้องนั่งเล่น, ห้องอาหาร/ห้องนั่งเล่นหน้าค้ำภายในมอของโถง
- Pantry ย้ายจากชั้น 3 (โปรแกรม) มาติดครัวโชว์ · ห้องโถง/ซักรีดไม่มีหน้าต่าง (ตั้งใจ) เข้าจากเฉลย
- Junior Suite 2 เข้าผ่านตู้เสื้อผ้า (walk-through); Junior Suite 3 เข้าจากเฉลย · ห้องทำงานมีทางออกบันไดหนีไฟ

H3A DESIGN AND BUILD

X-UNIT Architecture Lab

โครงการ

WELL-FORNO 30x30

Executive Luxury Villa

บ้านเดี่ยว 4 ชั้น ผ่านเกณฑ์

WELL for Residential (เจดนา)

ที่ดิน 30.00 x 30.00 ม. = 225 ตร.ว.
ถนนสาธารณะทิศเหนือ (สมมติ 8.00 ม.)

แนวคิด

ตีความจาก FORNO (Gruppo FON):
โครงไม้ glulam ภายนอกทุกชั้น + ค้ำเชิง
+ หลังคาจั่วไม้สมมาตร ชายคาใต้ 3.00
+ โถงไม้ "Forno hall" โปร่ง 4 ชั้น

ระดับ

±0.00 ถนน · F1 +0.45 · F2 +3.65
F3 +6.85 · F4 +10.05
หลังคาที่แนวหนึ่ง +12.95
สันหลังคา +14.95

หมายเหตุ


- หน่วยงานเป็นผลิตภัณฑ์ เว้นแต่ระบุ
- ระดับอ้างอิงถนนหน้าที่ดิน ±0.00
- ห้ามวัดขนาดจากแบบ ใช้ตัวเลขกำกับ
- แบบระดับ Design Development
- ต้องให้สถาปนิกและวิศวกรผู้ได้รับใบอนุญาตตรวจสอบและลงนามก่อนยื่นขออนุญาต

ชื่อแผ่น

ผังพื้นชั้น 2
(FFL +3.65)

มาตราส่วน 1:100

วันที่ 6 ค.ศ. 2569 ฉบับ v1 / DD

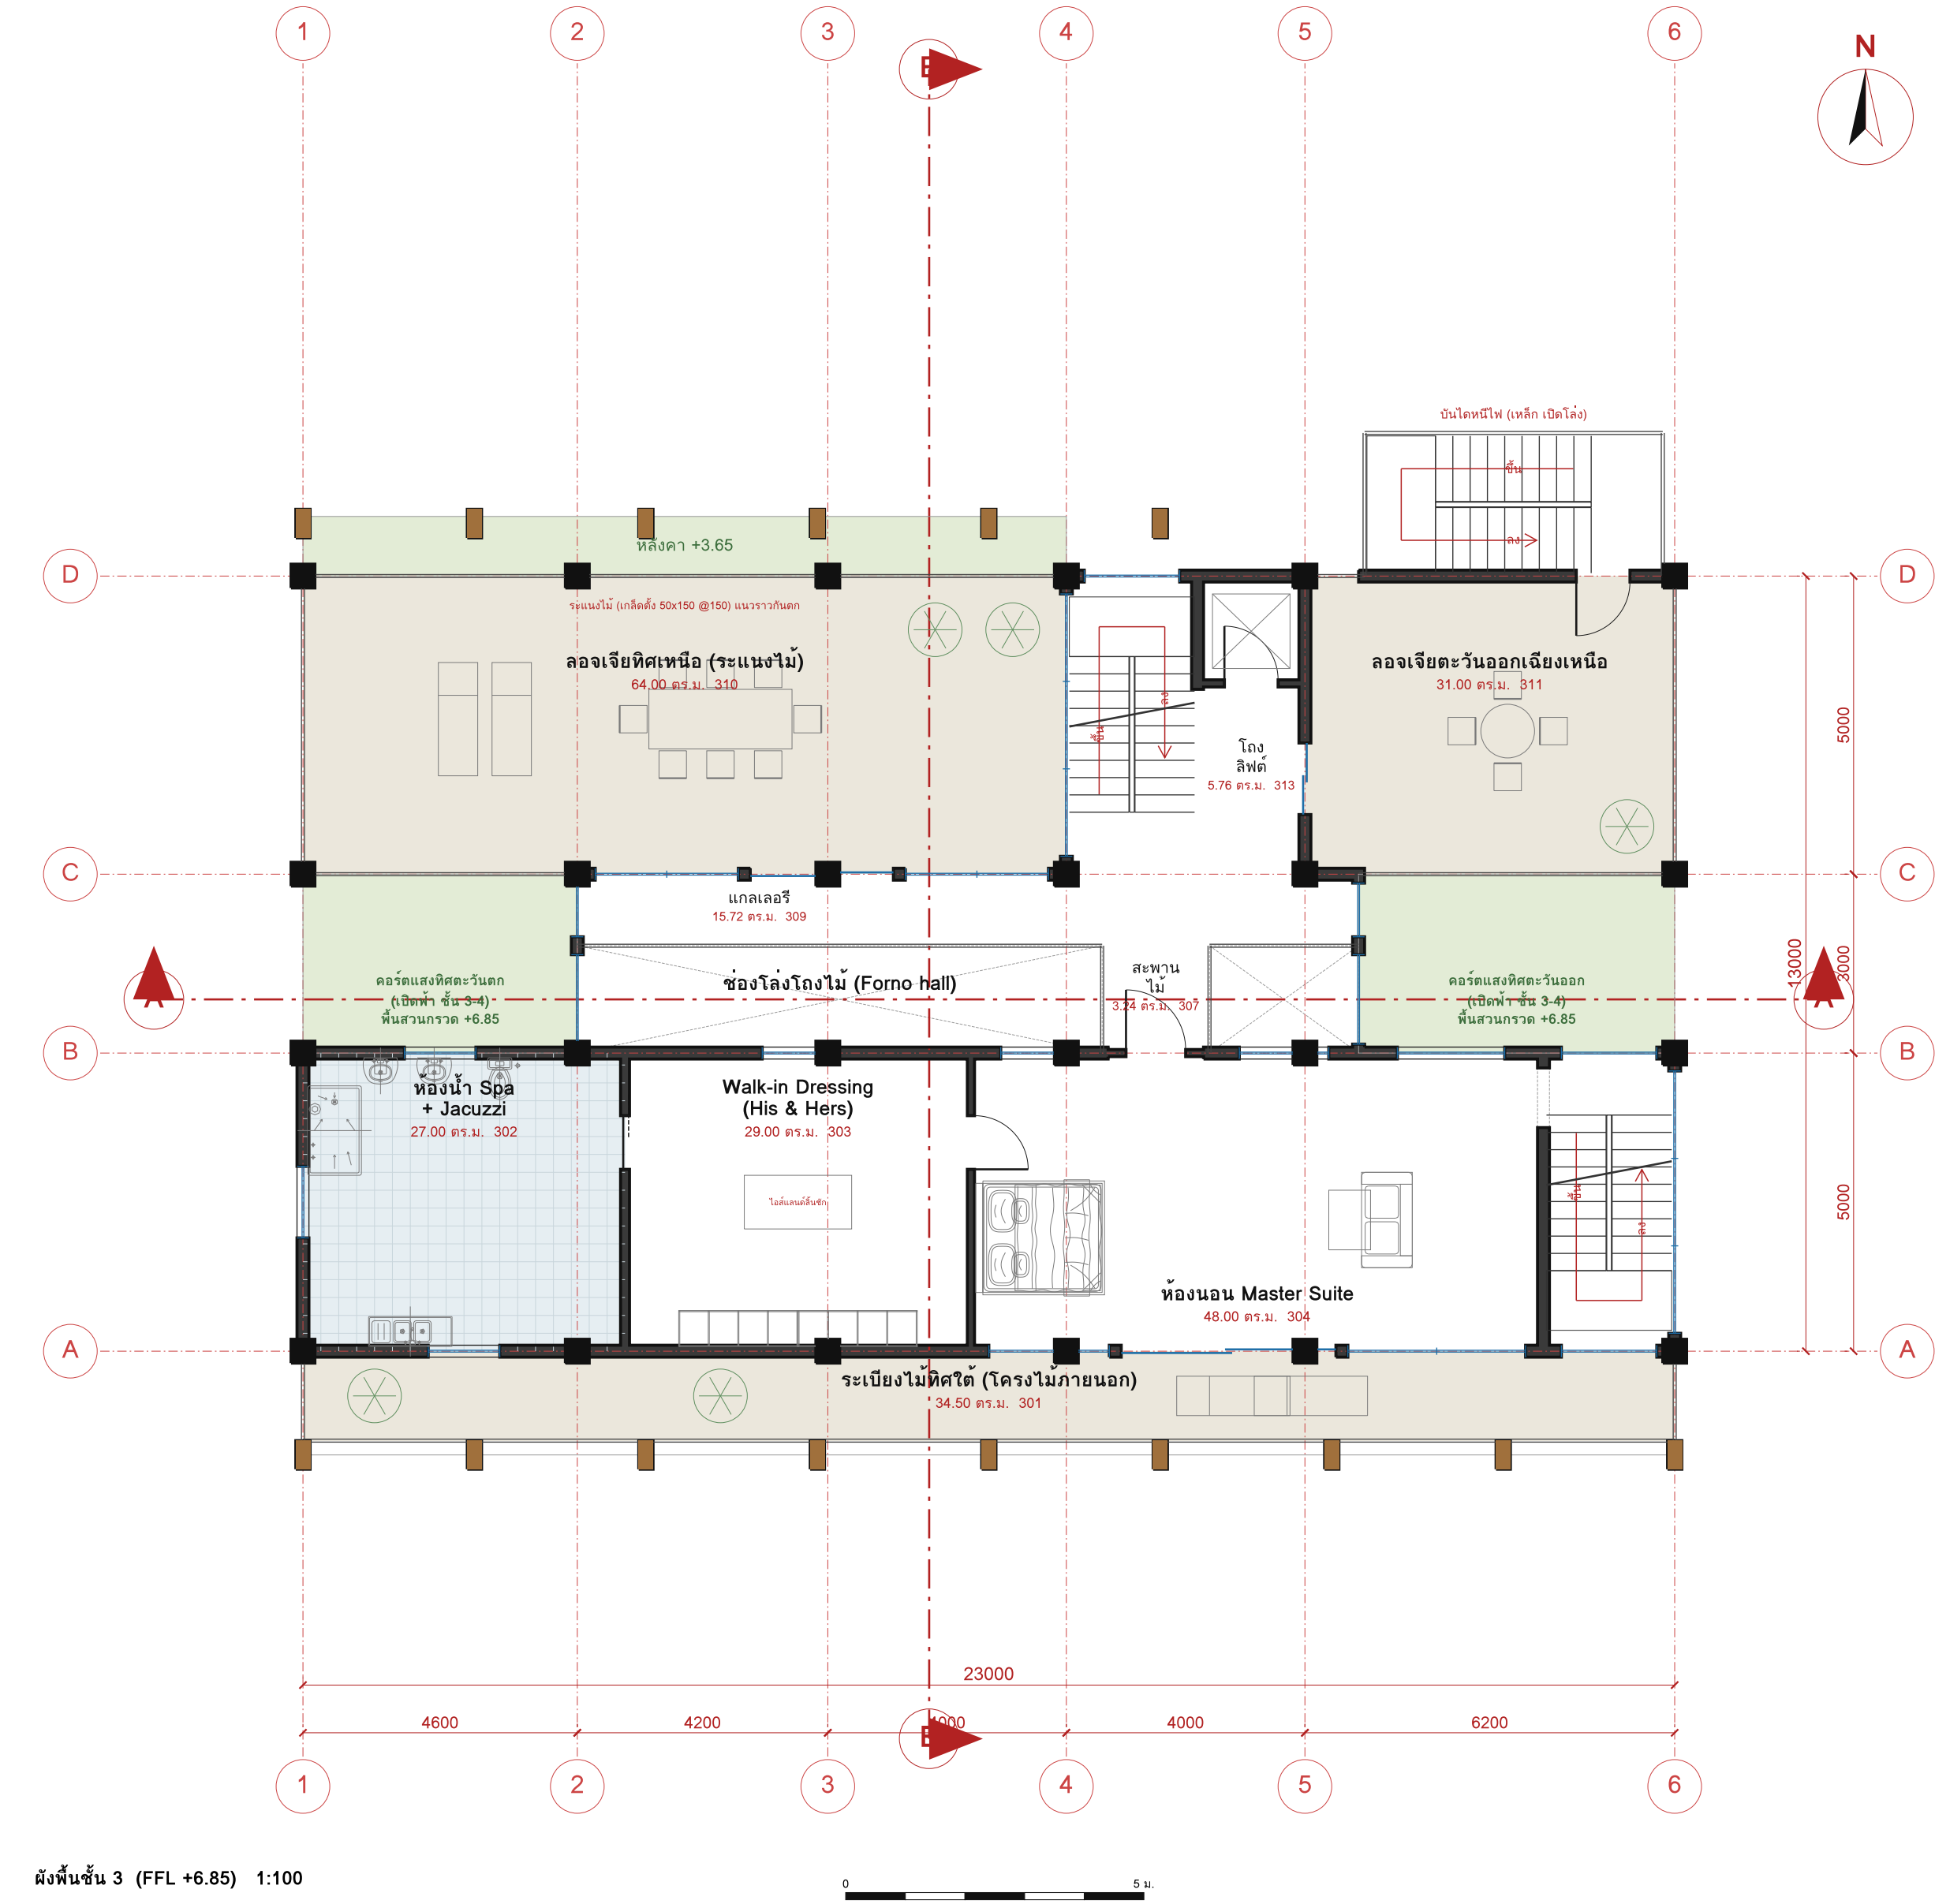

ผังพื้นชั้น 3 (FFL +6.85) 1:100

ตารางห้อง ชั้น 3

รหัส	ห้อง	ขนาด ม.	ตร.ม.	ประเภท
301	ระเบียงไม้ทิศใต้ ชั้น 3	23.00 x 1.50	34.50	ที่ภายนอก
302	ห้องน้ำ Spa + Jacuzzi	5.40 x 5.00	27.00	ห้องน้ำ
303	Walk-in Dressing (His & Hers)	5.80 x 5.00	29.00	บริการ
304	ห้องนอน Master Suite	9.60 x 5.00	48.00	ห้องใช้งาน
305	บันไดส่วนครัว Master	2.20 x 5.00	11.00	บันได
306	ช่องโถงโถงไม้ ชั้น 3	8.80 x 1.90	20.34	ช่องโถง
307	สะพานไม้ ชั้น 3	1.80 x 1.80	3.24	สัญจร
309	ทางเดินภายนอก ชั้น 3	13.10 x 1.20	15.72	สัญจร
310	ห้องนั่งเล่น (รวมไม้)	12.80 x 5.00	64.00	ที่ภายนอก
311	ห้องรับประทานอาหาร (รวมไม้)	6.20 x 5.00	31.00	ที่ภายนอก
312	บันไดหลัก (โถงไม้)	2.20 x 5.00	11.00	บันได
313	โถงลิฟต์ ชั้น 3	1.80 x 3.20	5.76	สัญจร
314	ลิฟต์บ้าน	1.80 x 1.80	3.24	ลิฟต์
315	บันไดหนีไฟภายนอก	5.00 x 2.40	12.00	บันไดหนีไฟ

รายการ	ตร.ม.
พื้นที่ปิดล้อม	153.96
ที่ภายนอก	129.50
จอดรถ	0.00
รวม	283.46
บันไดหนีไฟภายนอก (ไม่รวม)	12.00

หมายเหตุ

- ชั้น Master: สะพานไม้ -> ห้องนอน Master -> Walk-in -> ห้องน้ำ Spa: บันไดส่วนครัวภายนอกชั้น 4 (Master duplex)
- ระเบียงไม้ทิศใต้ชั้น 3 เป็นของ Master : ห้องนั่งเล่น 12.80 x 5.00 ม. ราวระแนงไม้ (ส่วนกันโปรแกรน -> ลานรอบครัวกับภายนอก)
- คอร์ริดอร์หัวท้าย (ที่ถูกรวบหลังอาคารชั้น 2) เปิดด้านสกัดได้หลังคา ฝ้าแสงสว่างโถงไม้ทางผนังกระจก
- ทางหนีไฟชั้น 3: แกะโลว์ -> โถงลิฟต์ -> ห้องนั่งเล่นภายนอกชั้นเหนือ -> บันไดหนีไฟ

H3A DESIGN AND BUILD

X-UNIT Architecture Lab

โครงการ

WELL-FORNO 30x30

Executive Luxury Villa
บ้านเดี่ยว 4 ชั้น ผ่านเกณฑ์
WELL for Residential (เจดนา)

ที่ดิน 30.00 x 30.00 ม. = 225 ตร.ว.
ถนนสาธารณะที่ดินเนื้อที่ (สมมติ 8.00 ม.)

แนวคิด

ตีความจาก FORNO (Gruppo FON):
โครงสร้าง ไม้ กล้าม ภายนอกทุกชั้น + ค้ำเชิง
+ หลังคาจั่วไม้สมมาตร ชายคาใต้ 3.00
+ โถงไม้ "Forno hall" โปร่ง 4 ชั้น

ระดับ

±0.00 ถนน · F1 +0.45 · F2 +3.65
F3 +6.85 · F4 +10.05
หลังคาชั้นแนวสูง +12.95
สันหลังคา +14.95

หมายเหตุ


- หน่วยเป็นมิลลิเมตร เว้นแต่ระบุ
- ระดับอ้างอิงถนนที่ถนน ±0.00
- ห้ามวัดขนาดจากแบบ ใช้ตัวเลขกำกับ
- แบบระดับ Design Development
- ต้องให้สถาปนิกและวิศวกรผู้ได้รับใบอนุญาตตรวจสอบและลงนามก่อนยื่นขออนุญาต

ชื่อแผ่น

ผังพื้นชั้น 3
(FFL +6.85)

มาตราส่วน 1:100

วันที่ 6 ค.ด. 2569 ฉบับ v1 / DD

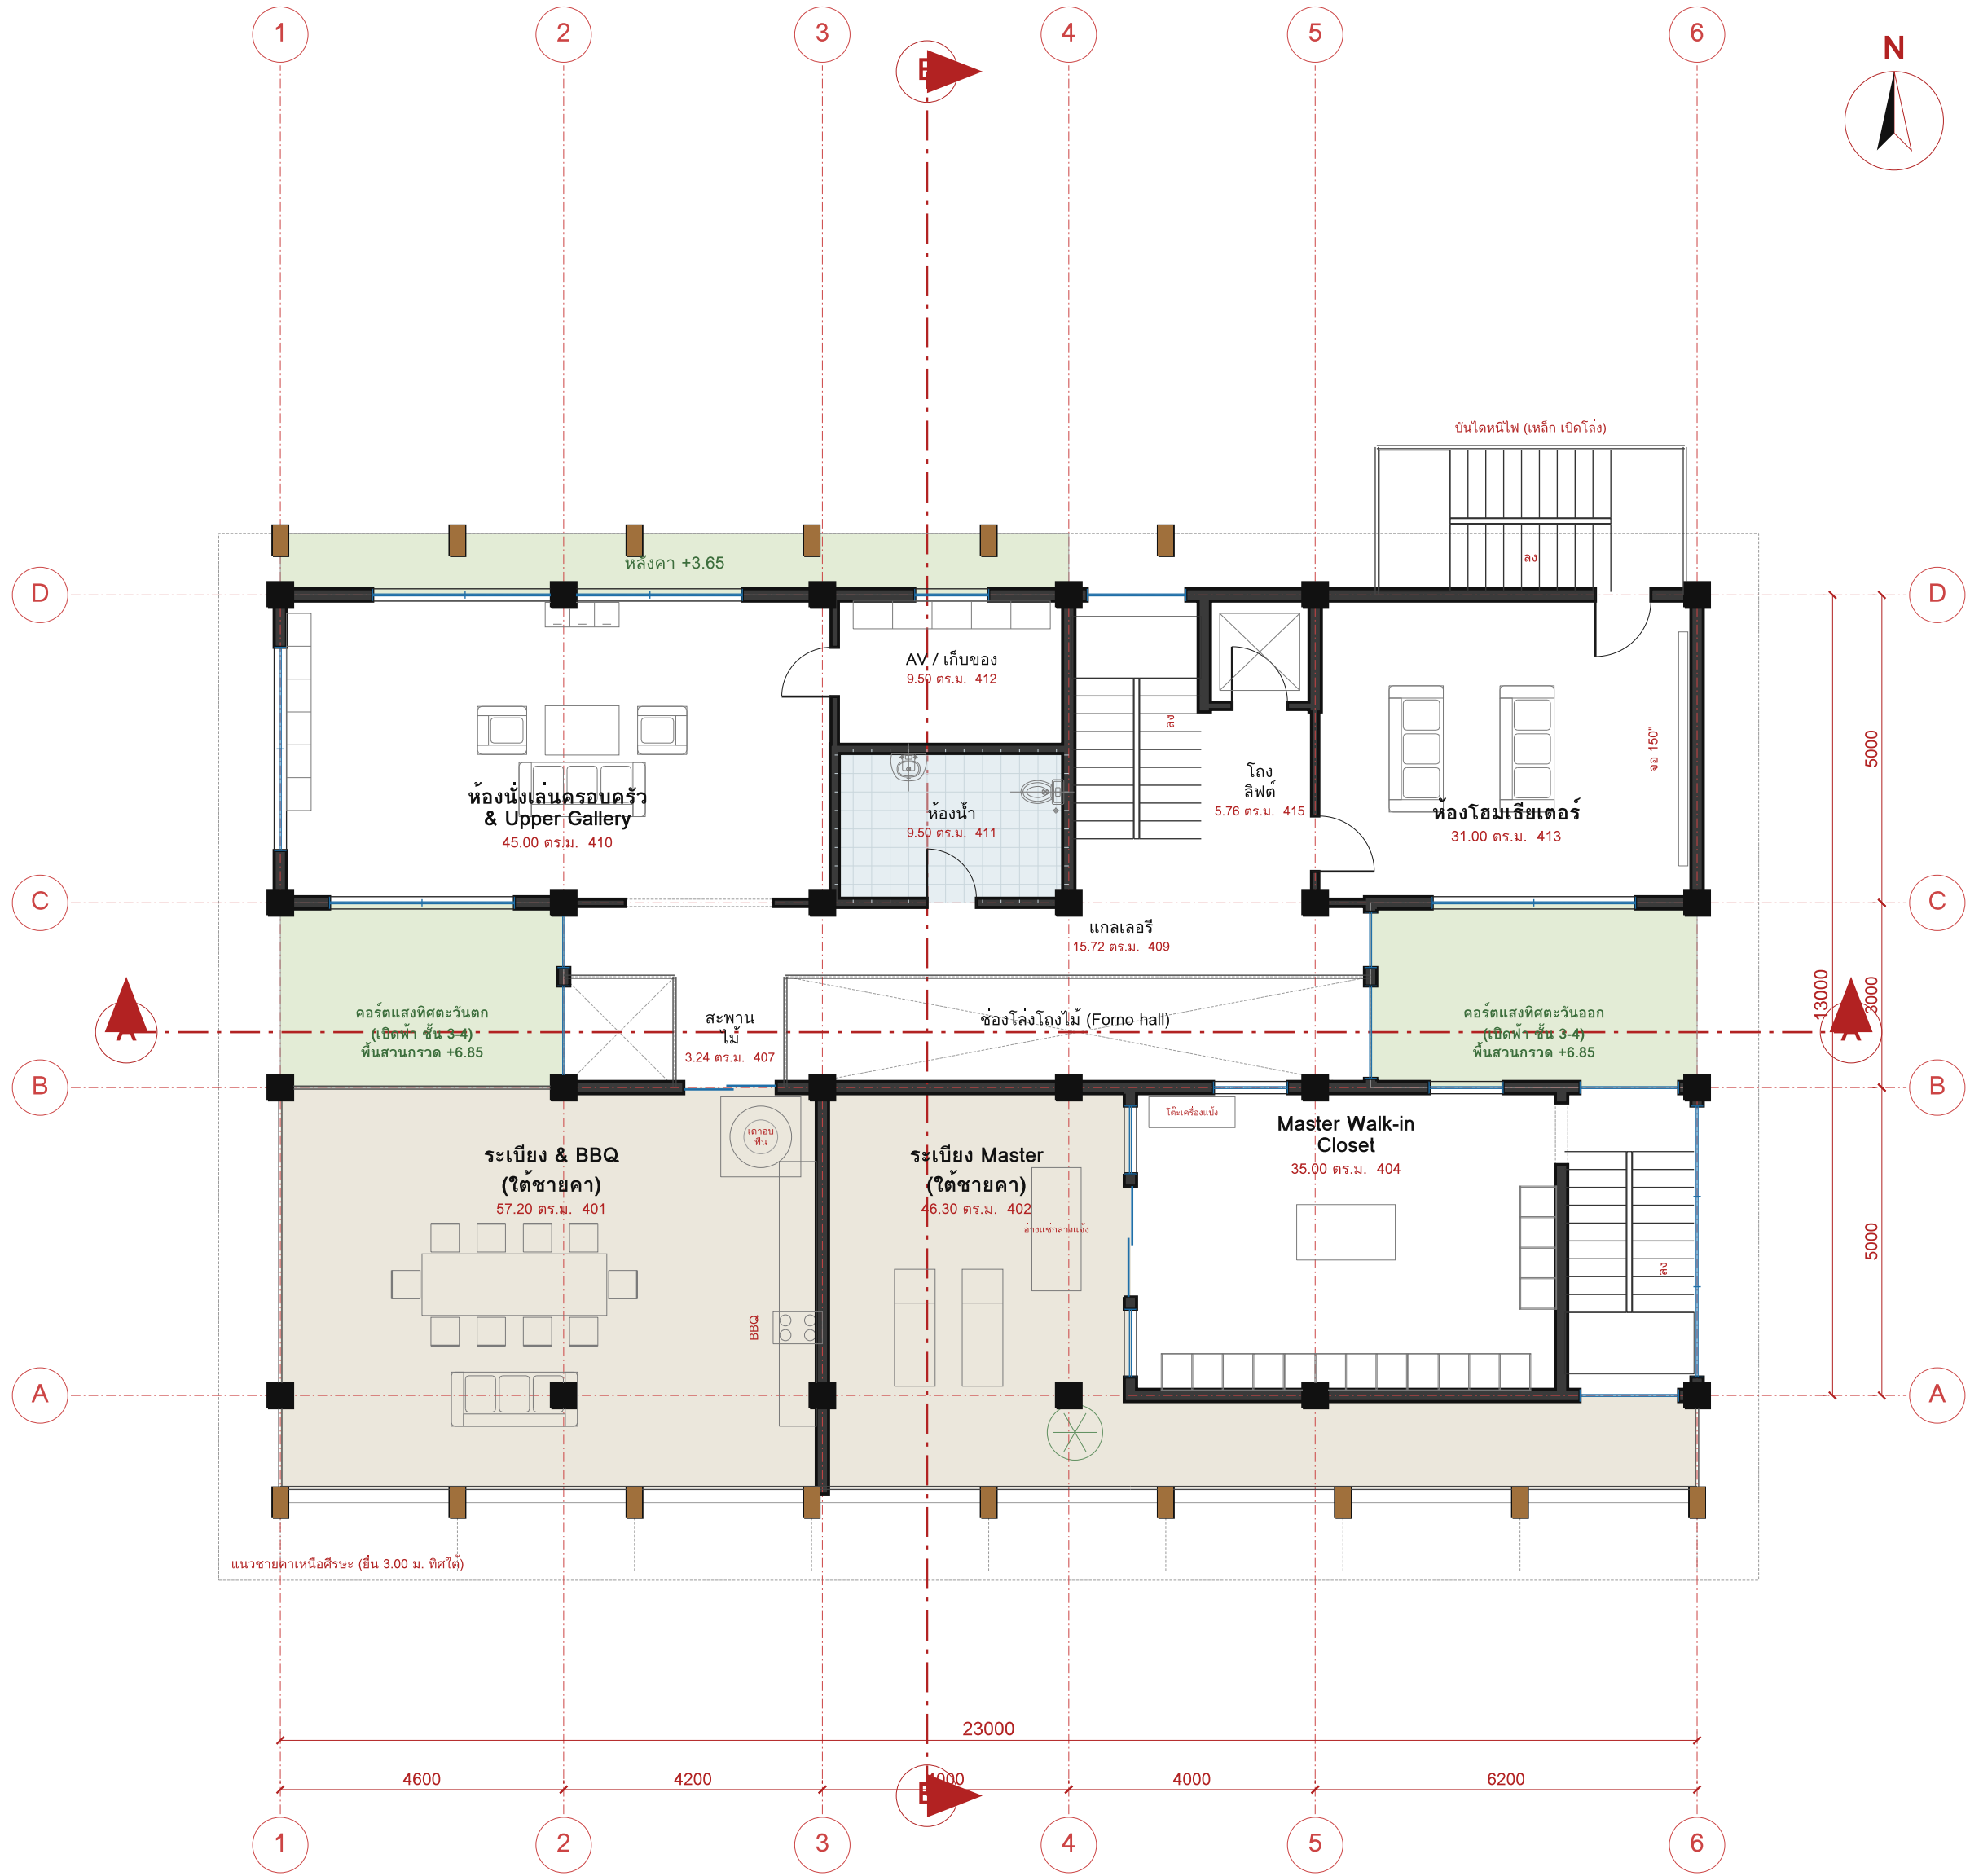

ผังพื้นชั้น 4 (FFL +10.05) 1:100



ตารางห้อง ชั้น 4

รหัส	ห้อง	ขนาด ม.	ตร.ม.	ประเภท
401	ระเบียง & BBQ (ใต้ชายคา)	8.80 x 6.50	57.20	กึ่งภายนอก
402	ระเบียง Master (ใต้ชายคา)	5.00 x 6.50	46.30	กึ่งภายนอก
404	Master Walk-in Closet ชั้น 4	7.00 x 5.00	35.00	บริการ
405	บันไดส่วนตัว Master	2.20 x 5.00	11.00	บันได
406	ช่องโถงโถงไม้ ชั้น 4	1.80 x 1.90	20.34	ช่องโถง
407	สะพานไม้ ชั้น 4	1.80 x 1.90	3.24	สัญจร
409	ทางเดินแกลเลอรี ชั้น 4	13.10 x 1.20	15.72	สัญจร
410	ห้องนั่งเล่นเครื่องครัว & Upper Galle	9.00 x 5.00	45.00	ห้องใช้งาน
411	ห้องนี้ชั้น 4	3.80 x 2.50	9.50	ห้องโถงเปิด
412	ห้องอุปกรณ์ AV / เก็บของ	3.80 x 2.50	9.50	บริการ
413	ห้องโอมะฮิเตอร์	6.20 x 5.00	31.00	ห้องใช้งาน
414	บันไดหลัก (โถงไม้)	2.20 x 5.00	11.00	บันได
415	โถงลิฟต์ ชั้น 4	1.80 x 3.20	5.76	สัญจร
416	ลิฟต์บ้าน	1.80 x 1.90	3.24	ลิฟต์
417	บันไดหนีไฟภายนอก	5.00 x 2.40	12.00	บันไดหนีไฟ

ฐานชั้น 4	ตร.ม.
พื้นที่ปิดล้อม	179.96
กึ่งภายนอก	103.50
จอดรถ	0.00
รวม	283.46
บันไดหนีไฟภายนอก (ไม่รวม)	12.00

หมายเหตุ

- โถงลิฟต์อาคาร: โปร่ง 2.60 ม. ที่นั่งชายคา สูงขึ้นถึง 4.60 ม. ที่ชั้น: ไม้ glulam เปิดโชว์ทุกเฟรม
- ระเบียง & BBQ (อาคารและชานบ้าน) เข้าจากสะพานไม้ชั้น 4: ผนังกระจกระเบียง Master · ระเบียง Master + ถ้ำเข้า Closet
- ห้องนั่งเล่นเครื่องครัวเปิด 2.40 ม. สูงแกลเลอรี (Upper Gallery) · ห้องโอมะฮิเตอร์มีทางออกบันไดหนีไฟ (หันลิ้น)
- หลังคาอาคารได้: แสงโซลาร์ 38 แสง = 20.90 kWp

H3A DESIGN AND BUILD

X-UNIT Architecture Lab

โครงการ

WELL-FORNO 30x30

Executive Luxury Villa

บ้านเดี่ยว 4 ชั้น ผ่านเกณฑ์

WELL for Residential (เจดนา)

ที่ดิน 30.00 x 30.00 ม. = 225 ตร.ว.
ถนนสาธารณะติดเหนือ (สมมติ 8.00 ม.)

แนวคิด

ตีความจาก FORNO (Gruppo FON):

โครงสร้างไม้ glulam ภายนอกทุกชั้น + ค้ำเชิง
+ หลังคาจั่วไม้สมมาตร ชายคาได้ 3.00
+ โถงไม้ "Forno hall" โปร่ง 4 ชั้น

ระดับ

±0.00 ถนน · F1 +0.45 · F2 +3.65
F3 +6.85 · F4 +10.05
หลังคาที่แนวนี้ +12.95
สันหลังคา +14.95

หมายเหตุ


- หน่วยงานเป็นผลิตภัณฑ์ เวนเตอร์
- ระดับอ้างอิงถนนที่ชั้น ±0.00
- ห้ามวัดขนาดจากแบบ ใช้ตัวเลขกำกับ
- แบบระดับ Design Development
- ต้องให้สถาปนิกและวิศวกรผู้ได้รับใบอนุญาตตรวจสอบและลงนามก่อนยื่นขออนุญาต

ชื่อแผ่น

ผังพื้นชั้น 4
(FFL +10.05)

มาตราส่วน 1:100

วันที่ 6 ค.ศ. 2569 ฉบับ v1 / DD

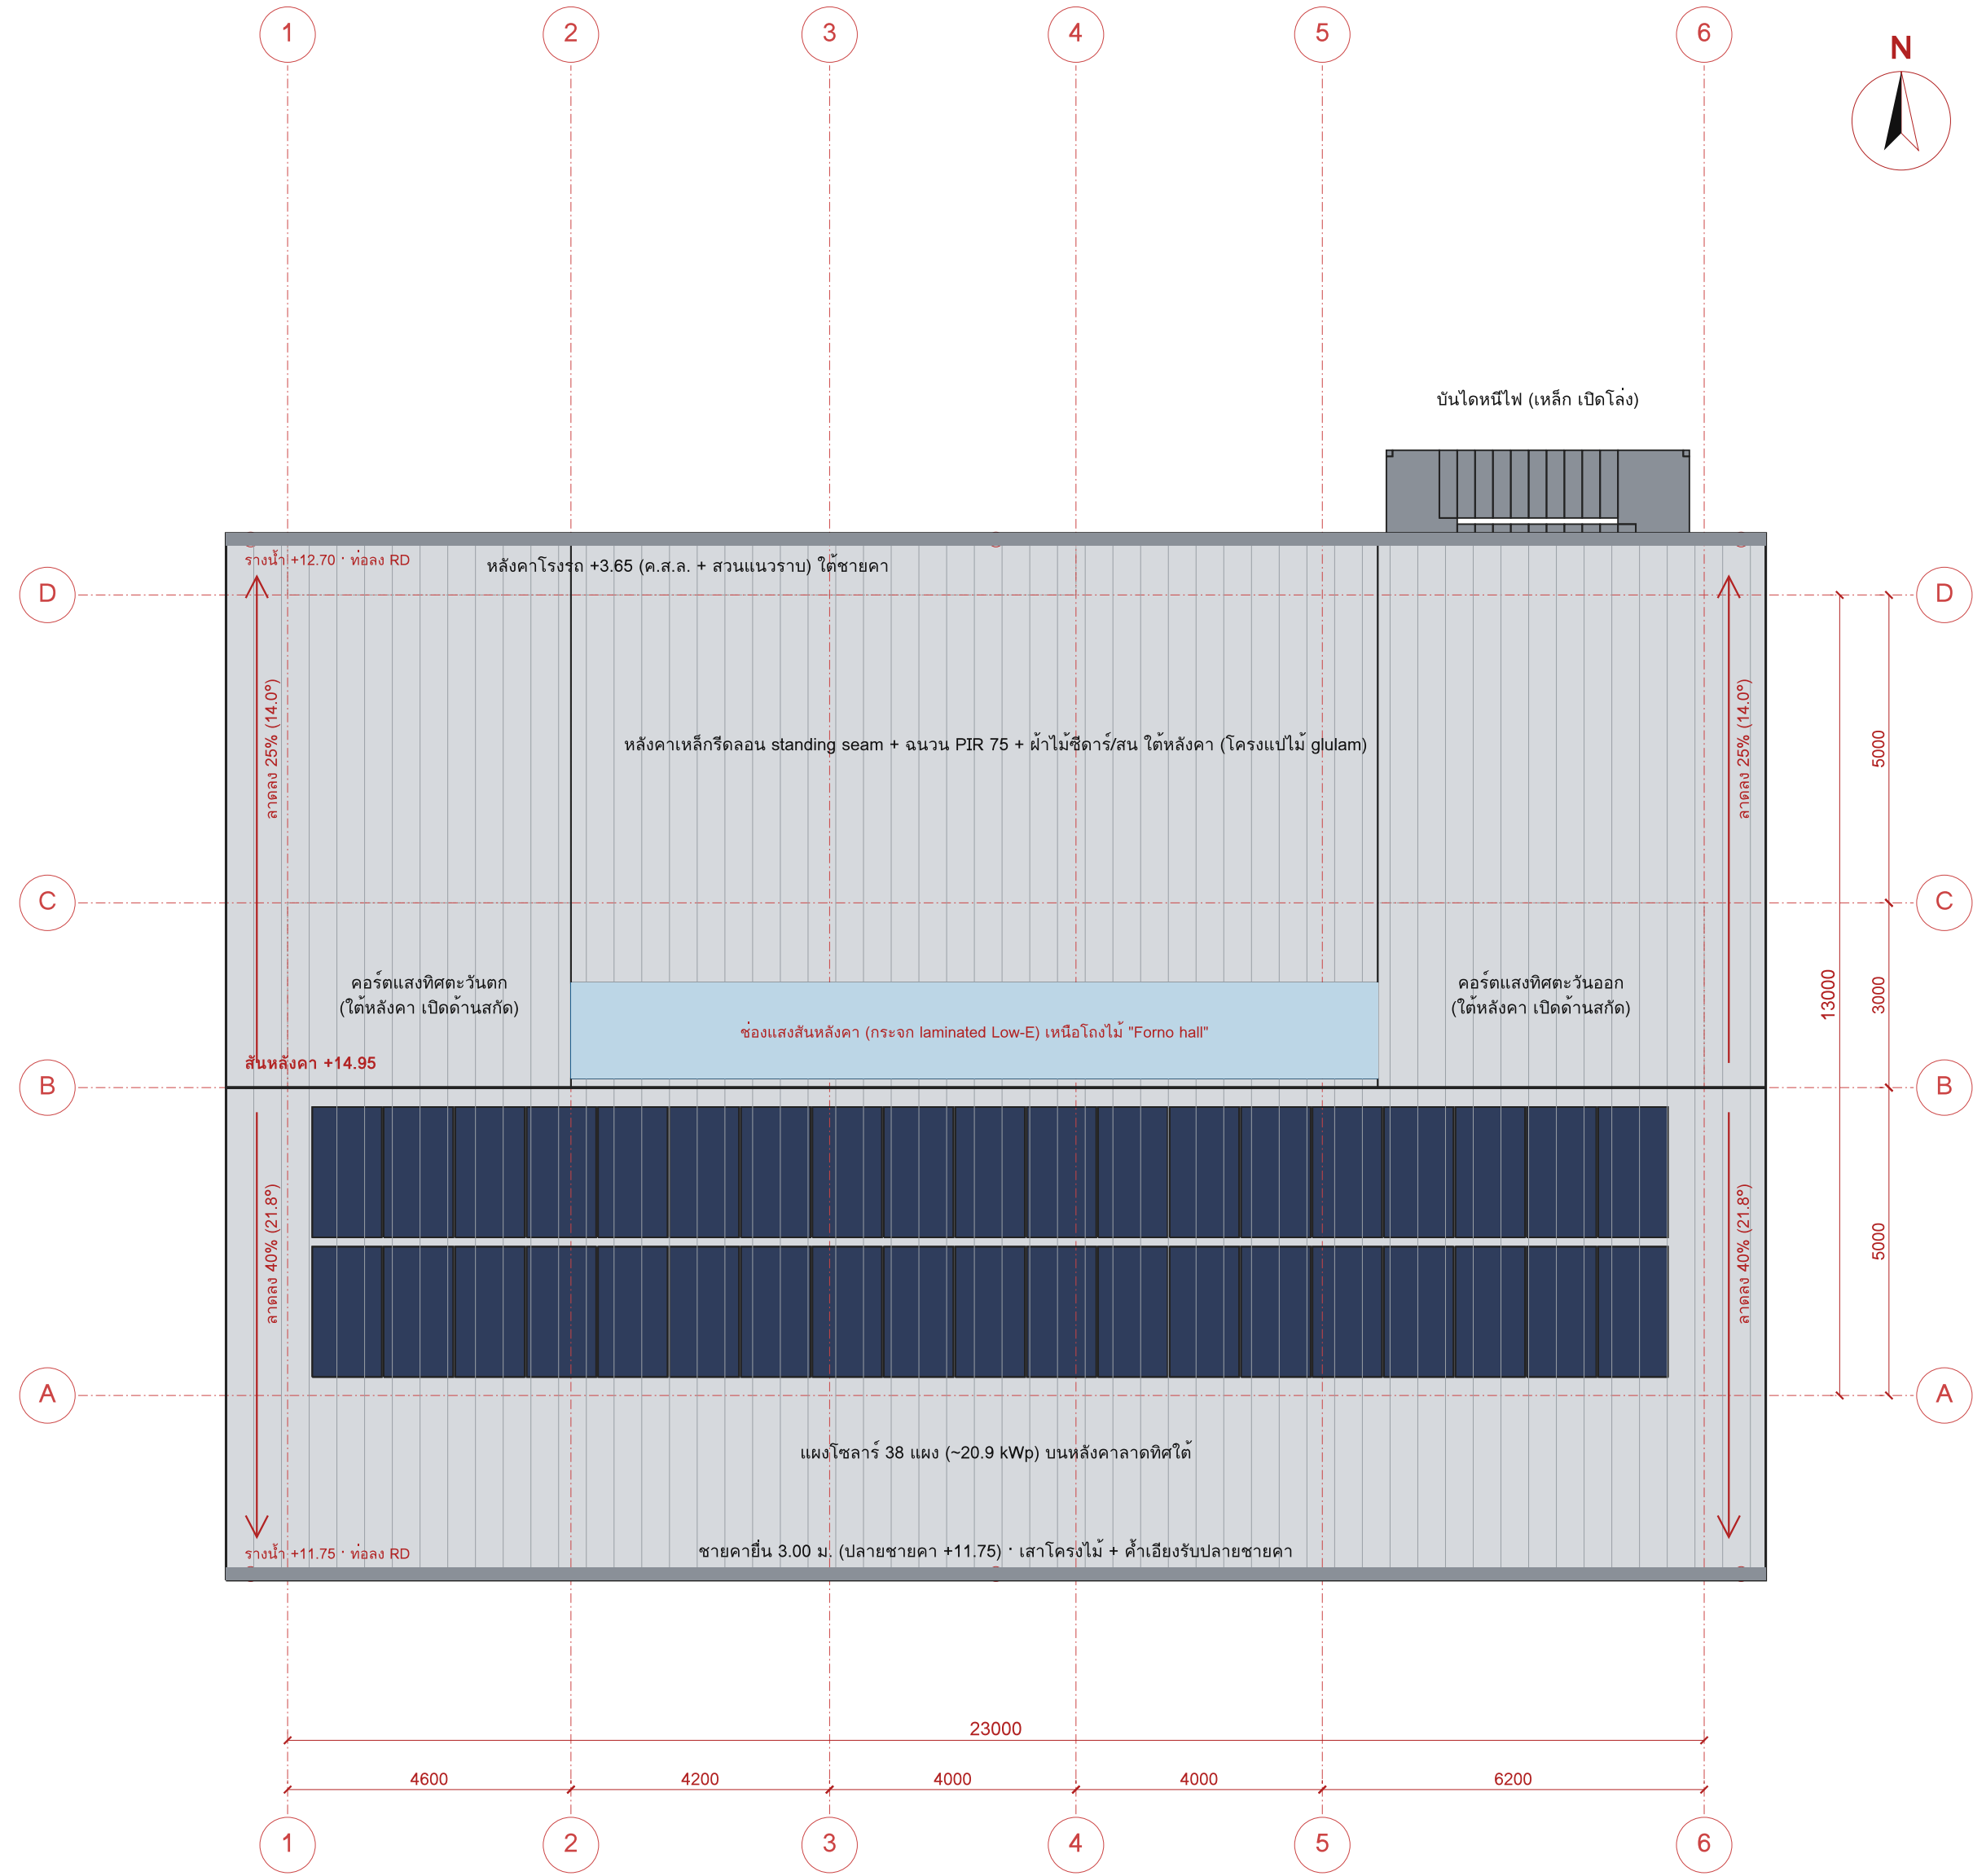

แปลนหลังคา ROOF PLAN 1:100



พื้นที่หลังคา

หลังคา	ค.ร.ม.
หลังคาจั่ว (แบบ รวมชายคา) 25.00 x 17.00 ม.	425.00
- แผงโซลาร์บนลาดใต้	97.90
- ช่องแสงสันหลังคา 13.10 x 1.55 ม.	20.30
หลังคาโรงรถ +3.65 (ใต้ชายคา)	12.80
พื้นคอร์ตแสง +6.85 (กรวด ใต้หลังคา)	29.70

บ้านหลังคา และระดับ

รายการ	ค่า
ระยะจากโครงสร้าง (ประมาณ)	~1,500 มม./ปี
น้ำฝนจากหลังคาจั่ว (C=0.9)	574 ลบ.ม./ปี
ถังเก็บน้ำฝนใต้ดิน 3.00 x 2.50 ม.	~12 ลบ.ม. (รับน้ำซัดโครก)
แผงโซลาร์ 38 x 550 Wp	20.90 kWp ~ 26,100 kWh/ปี*
ความลาด ใต้ / เหนือ	40% (21.8°) / 25% (14.0°)
ระดับ สัน / แนวผนัง / ปลายชายคาใต้ / เหนือ	+14.95 / +12.95 / +11.75 / +12.70

ชั้นหลังคา

- หลังคาจั่ว: เหล็กรีดลอน standing seam เคลือบสีลอน (SR >= 0.75 — ต้องกินยาปลูก) + ฉนวน PIR 75 มม. + แผ่นกันชื้น + ไม้ระแนงรอบรับ + ไม้ปู glulam
- ฝ้าใต้หลังคา: ไม้สนซีดาร์ เคลือบสีไฟ (ต้องทาสีตามหน้าไฟ) · ฝ้าไม้ 180 x 400 ทุกเฟรม @2,875 ม. เปิดโชว์
- ช่องแสงสันหลังคา: กรอบ laminated Low-E ลาดตามหลังคา ผนังเป็นโครงข่ายอากาศ/ฉนวนใต้ไม้ดี (เจตนา stack effect)
- รายนํ้าฝนที่กลิ้งลงปลายชายคาก็จะลงด้าน -> ท่อลง RD ตามลาดไม้ -> รวบรวมอาคาร -> ถังน้ำฝน
- ปลายชายคาใต้ดิน 3.00 ม. รับน้ำสาดเข้าจากสายท่อฝน (สไลด์แรงลมยก ต้องให้วิศวกรตรวจ)
- หลังคา PV ประมาณ ~1,250 kWh/kWp/ปี ที่ความเอียง 21.8° ขึ้นได้ — ต้องคำนวณเชิงวิศวกรรมหลังคา

H3A DESIGN AND BUILD

X-UNIT Architecture Lab

โครงการ

WELL-FORNO 30x30

Executive Luxury Villa
บ้านเดี่ยว 4 ชั้น ผ่านเกณฑ์
WELL for Residential (เจตนา)

ที่ดิน 30.00 x 30.00 ม. = 225 ตร.ว.
ถนนสาธารณะทิศเหนือ (สมบัติ 8.00 ม.)

แนวคิด

ตีความจาก FORNO (Gruppo FON):
โครงไม้ glulam ภายนอกทุกชั้น + ค้ำแข็ง
+ หลังคาจั่วไม้สมมาตร ชายคาใต้ 3.00
+ โถงไม้ "Forno hall" โปร่ง 4 ชั้น

ระดับ

±0.00 ถนน · F1 +0.45 · F2 +3.65
F3 +6.85 · F4 +10.05
หลังคาที่แนวผนัง +12.95
สันหลังคา +14.95

หมายเหตุ

- หน่วยงานเป็นผลิตภัณฑ์ เว้นแต่ระบุ
- ระดับอ้างอิงถนนหน้าที่ดิน ±0.00
- ห้ามวัดขนาดจากแบบ ใช้ตัวเลขกำกับ
- แบบระดับ Design Development
- ต้องให้สถาปนิกและวิศวกรผู้ได้รับใบอนุญาตตรวจสอบและลงนามก่อนยื่นขออนุญาต

ชื่อแผ่น

แปลนหลังคา

มาตราส่วน 1:100

วันที่ 6 ค.ศ. 2569 ฉบับ v1 / DD

รูปด้านทิศเหนือ (ถนน — เสาไม้หน้าโรงรถ / บ้านไดโนไฟ) 1:100



• โครงสร้างภายในคือ: glulam (สนทนูปรับน้ำหนัก) ถัดหน้า + เติบอบกับ UV กระจกเหล็กทึบเห็น 0.30 m.
 • ชั้น 1: ผังงานภายใน (lime render) • ชั้น 2-4: ผนัง ค.ส.ล.กลึง + ไม้ทึบยาวครึ่ง (ใช้ตรงหน้าอาคารหลักทั้ง) !
 • หลังคา: กระจกกลึงอน standing screen สีส้ม + เติบอบสีขาวทึบ + ช่องแสงชั้นหลังคา
 • หน้าจั่ว: เติบอบไม้ขอบ 60 x 80 @1.20 m. (ไม้เนื้อแข็ง +120%) • ช่องแสงหน้าจั่วขาวราว 1.10 m.
 • กระดาน Low-E laminated กรอบอะลูมิเนียมสีบรอนซ์ • ราวกระดาน 1.10 m. + ผึงกับ
 • ปีนีโตนีไฟ: เติบอบกล้วยไม้ขาวสี ราว 1.10 m.

X-UNIT Architecture Lab

โครงการ

Executive Luxury Villa
บ้านเดี่ยว 4 ชั้น ผ่านเกณฑ์
WELL for Residential (เจตนา)

ที่ดิน 30.00 x 30.00 ม. = 225 ตร.ว.
ถนนสาธารณะทิศเหนือ (สมบัติ 8.00 ม.)

แนวคิด

ตีความจาก FORNO (Gruppo FON):
 โครงไม้ glulam ภายนอกทุกชั้น + ค้ำเอียง
 + หลังคาจั่วไม้สนมาตร ชายคาใต้ 3.00
 + โถงไม้ "Forno hall" โปรง 4 ชั้น

ระดับ

± 0.00 ถนน $\cdot F_1 + 0.45 \cdot F_2 + 3.65$
 $F_3 + 6.85 \cdot F_4 + 10.05$
 หลังคาที่แนวม้ง $+12.95$
 สันหลังคา $+14.95$

หมายเหตุ

- หน่วยงานเป็นลิขสิทธิ์ เวนแต่ละระบุ
- ระดับอ้างอิงถนนหน้าที่ดิน ± 0.00
- ห้ามรื้อขนาดจากแบบ ใช้ตัวเลขกำกับ
- แบบระดับ Design Development
ต้องให้สถาปนิกและวิศวกรผู้ได้รับ
ใบอนุญาตตรวจสอบและลงนาม
ก่อนยื่นขออนุญาต

ชื่อแผ่น


รูปด้านทิศใต้
+ รูปด้านทิศเหนือ

มาตราส่วน 1:100


วันที่ 6 ต.ค. 2569 ฉบับ v1 / DD

A-08

รูปด้านทิศตะวันออก (หน้าจั่วไม้สมมาตร — ทางเข้า) 1:100

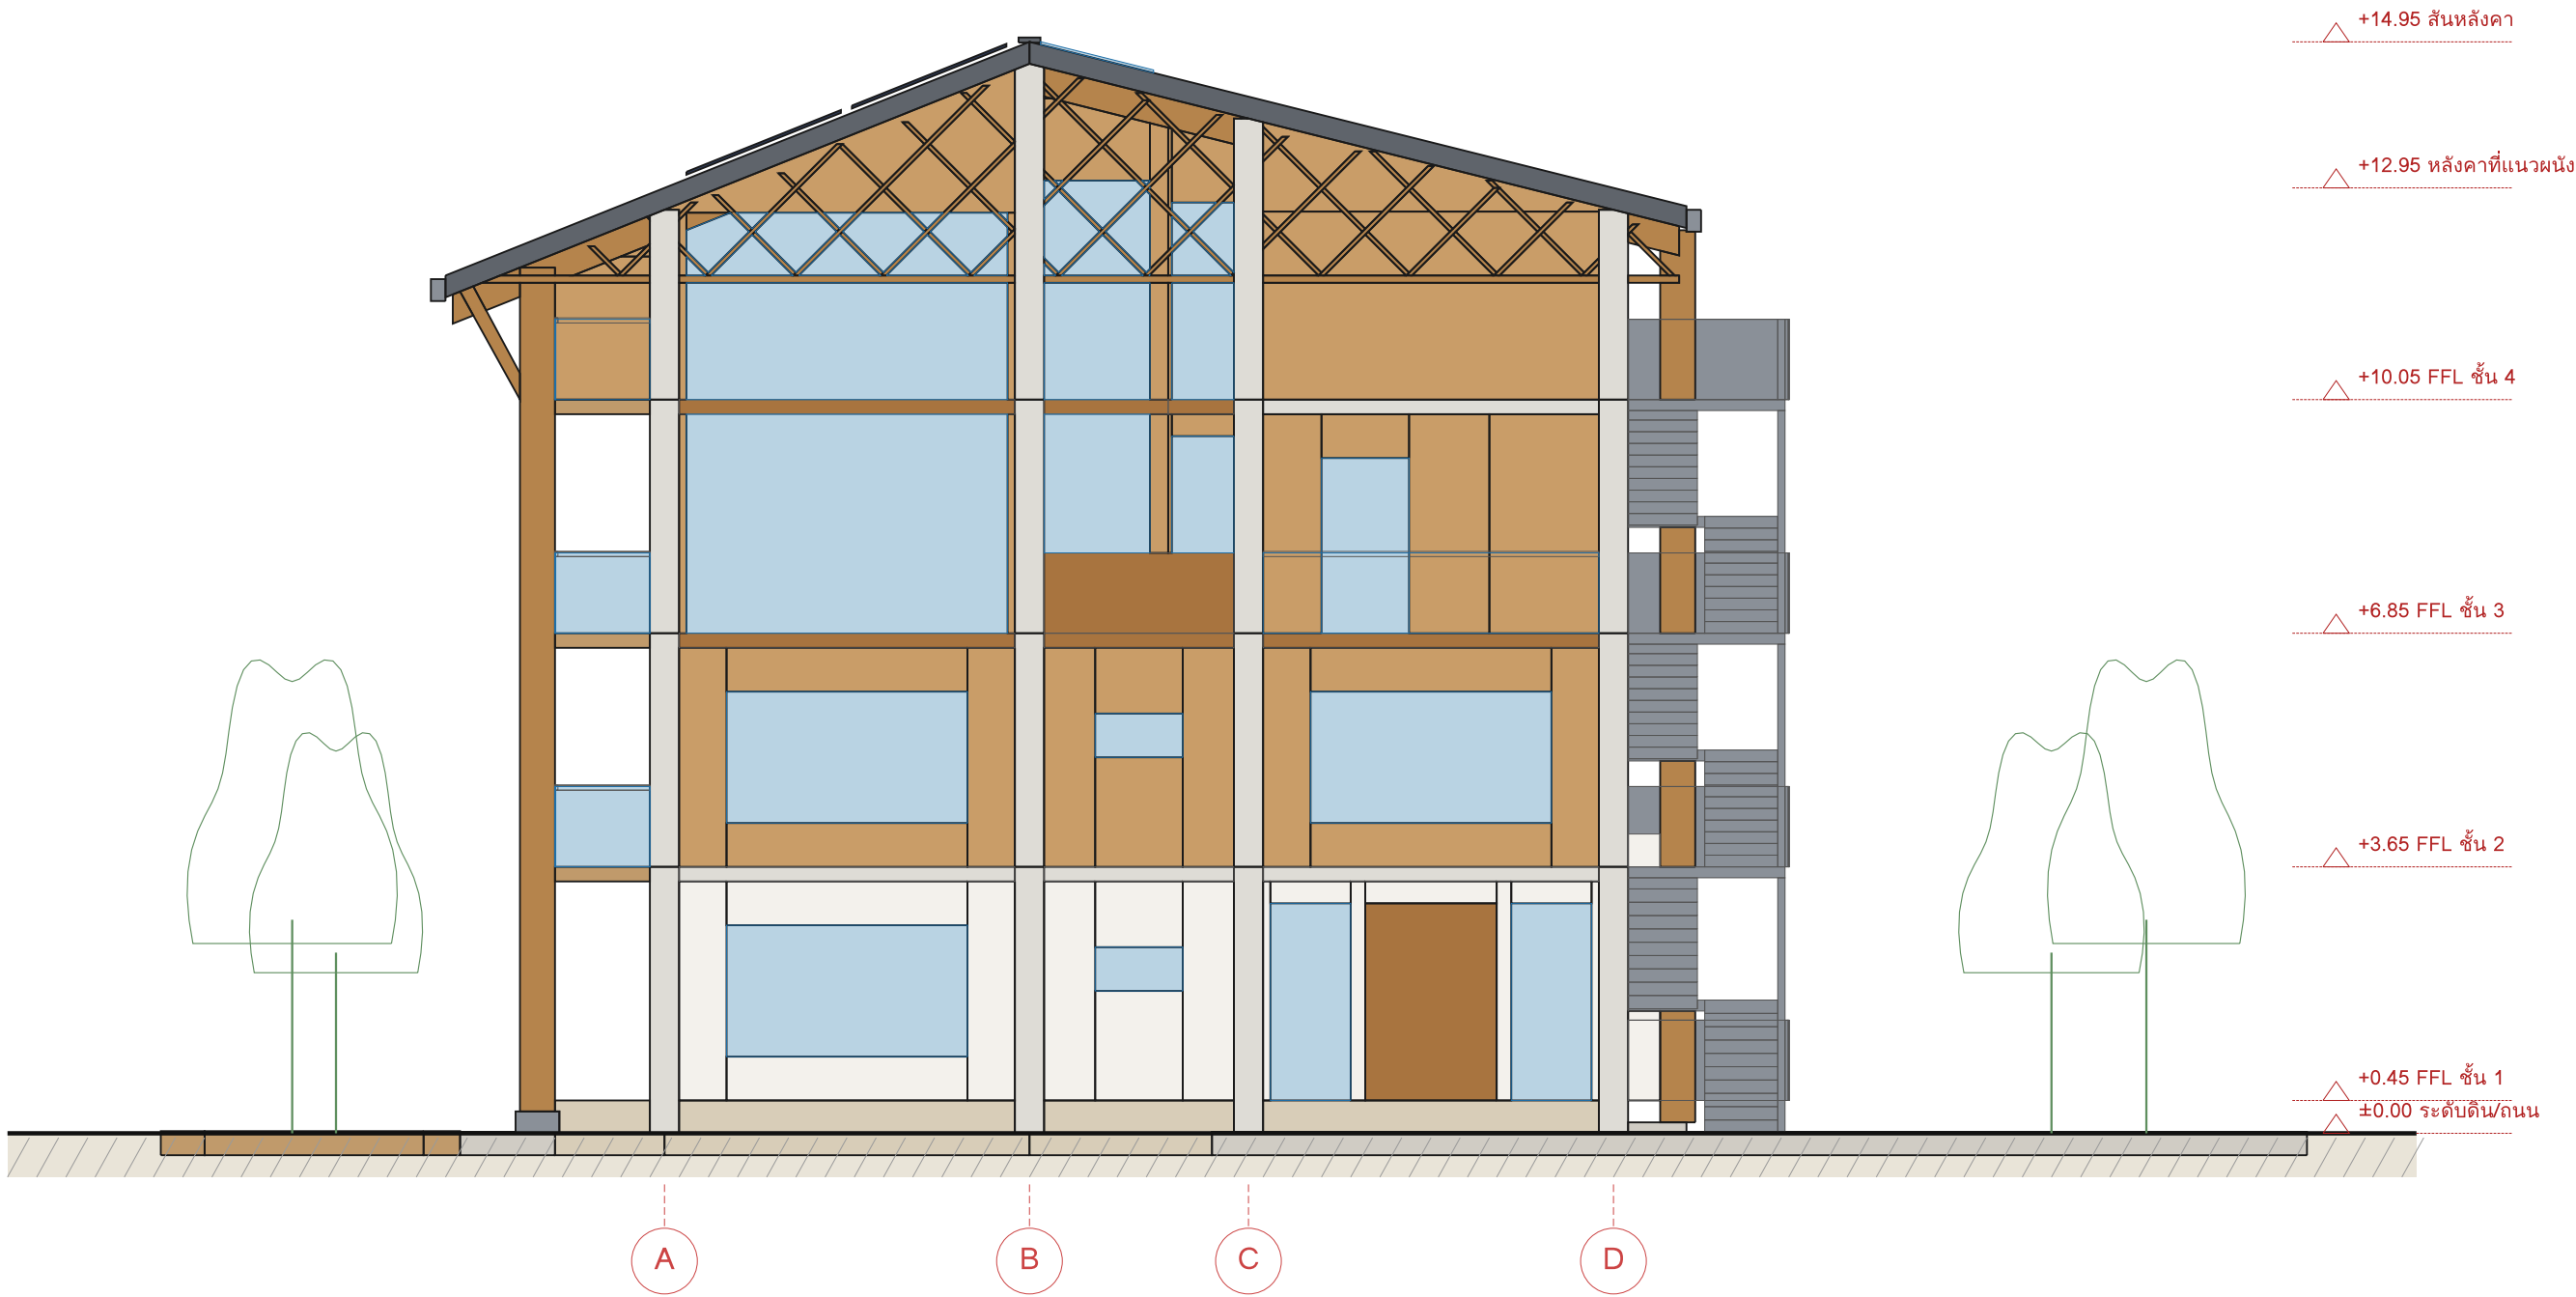

รูปด้านทิศตะวันตก (หน้าจั่ว + ระแนงไม้ทแยง) 1:100

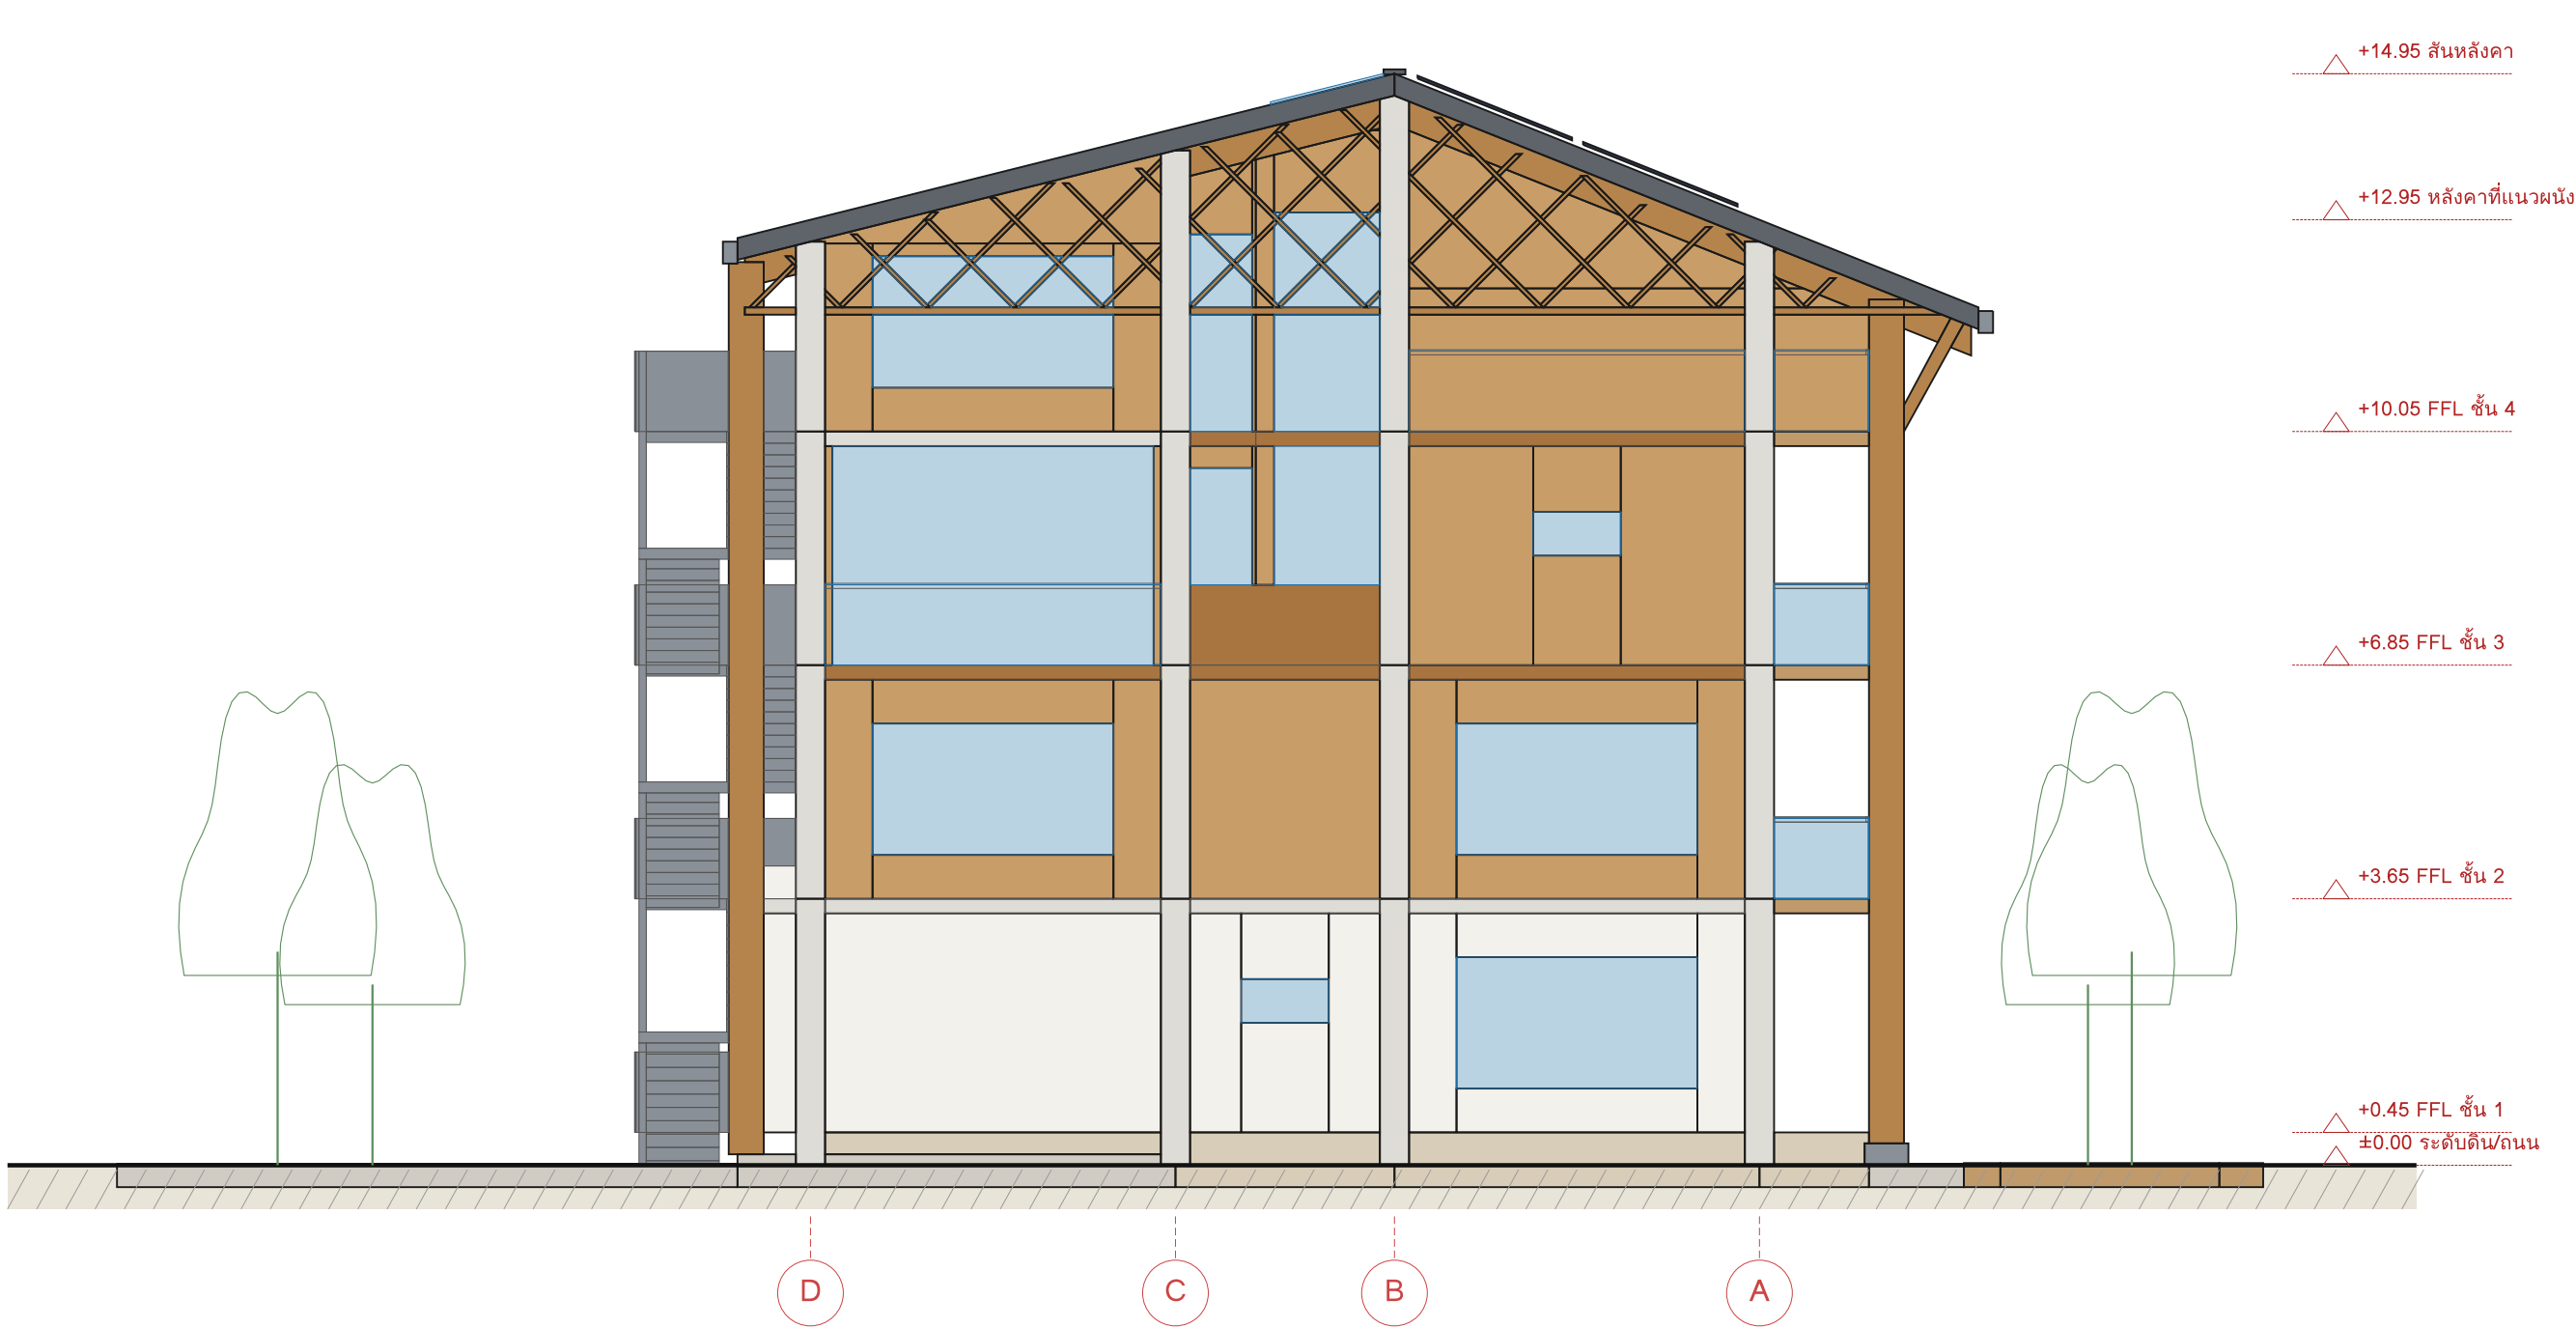

วัสดุผิว (ระดับแนวคิด)

- โครงไม้ภายนอก: glulam (สนูป/โรน/ไม้ท่อน) ใต้ฝ้า + เคลือบกัน UV ฐานเหล็กยกพื้น 0.30 ม.
- ชั้น 1: ผนังปูนฉาบขาว (lime render) · ชั้น 2-4: ผนัง ค.ส.ล./บล็อก + ไม้กรุแนวตั้ง (มีช่องระบายอากาศหลังไม้)
- หลังคา: เหล็กโครงสร้าง standing seam สีฉ่อน + แฉงโซลาร์ลวด + ช่องแสงสันหลังคา
- หน้าจั่ว: ระแนงไม้ทแยง 60 x 80 @1.20 ม. (เหนือระดับ +12.00) · โครงสร้างหลังคาทำด้วยไม้ 1.10 ม.
- กระเบื้อง Low-E laminated กรอบอะลูมิเนียมสีบรอนซ์ · ราวกระเบื้อง 1.10 ม. + ผิวยิปซี
- ประตูหน้าต่าง: เหล็กทึบในซีกทาสี ราว 1.10 ม.



H3A DESIGN AND BUILD

X-UNIT Architecture Lab

โครงการ

WELL-FORNO 30x30

Executive Luxury Villa

บ้านเดี่ยว 4 ชั้น ผ่านเกณฑ์

WELL for Residential (เจดนา)

ที่ดิน 30.00 x 30.00 ม. = 225 ตร.ว.

ถนนสาธารณะติดเหนือ (สมมติ 8.00 ม.)

แนวคิด

ตีความจาก FORNO (Gruppo FON):

โครงไม้ glulam ภายนอกทุกชั้น + ค้ำแข็ง

+ หลังคาจั่วไม้สมมาตร ชายคาโด่ 3.00

+ โถงไม้ "Forno hall" โปร่ง 4 ชั้น

ระดับ

±0.00 ถนน · F1 +0.45 · F2 +3.65

F3 +6.85 · F4 +10.05

หลังคาที่แนวผนัง +12.95

สันหลังคา +14.95

หมายเหตุ

· ผนังเป็นลิมิตเรเตอร์ เว้นแต่ระบุ

· ระดับอ้างอิงถนนหน้าที่ดิน ±0.00

· ห้ามวัดขนาดจากแบบ ใช้ตัวเลขกำกับ

· แบบระดับ Design Development

ต้องให้สถาปนิกและวิศวกรผู้ได้รับ

ใบอนุญาตตรวจชอบและลงนาม

ก่อนยื่นขออนุญาต


ชื่อแผ่น

รูปด้านทิศตะวันออก


+ รูปด้านทิศตะวันตก

มาตราส่วน 1:100

วันที่ 6 ค.ศ. 2569 ฉบับ v1 / DD

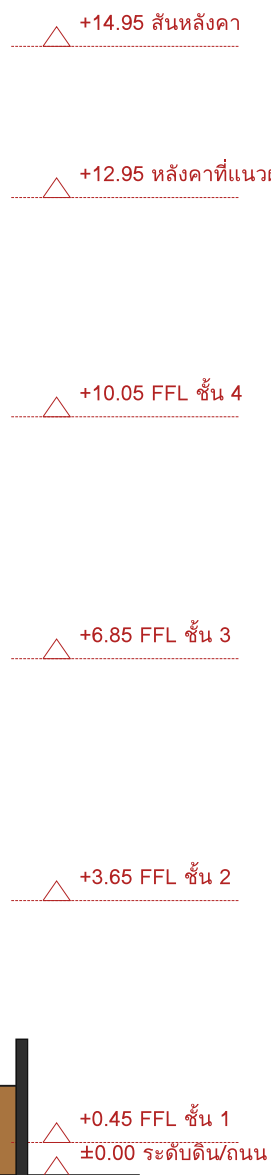

รูปตัด B-B (ตัดแนวเหนือ-ใต้ ผ่านสระ-โครงไม้ภายนอก-ครัวไทย / ห้องอาหาร / Walk-in / ระเบียง Master-ช่องลิ้ง-แกลเลอรี-โรงรถ / ห้องนอน / ลอดเจีย / ห้องน้ำ มองไปทิศตะวันออก) 1:100

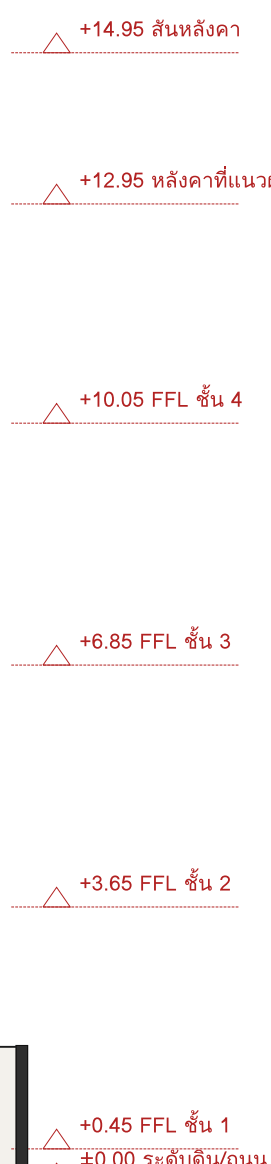

หมายเหตุสรุปปิด

- พื้นที่ตั้ง 3.20 ม. = พื้น 0.20 + มั่ว/งานรอบบ 0.20 + โปร่ง 2.80 ม. (ส่วน 1+3)
- ชั้น 4 โชว์ห้องคาลาอา: โปร่ง 2.60 ม. พื้นผิวขนาดบวกริ 4.60 ม. พื้น (แต่ไม่เปิดโชว์)
- ปูปิด A-A คัดตัวอย่างบ้านใกล้มี (โชว์ห้อง + สะพานไม้ + คลองส่งน้ำท้าย) - ปูปิด B-B คัดขวางเห็นห้องคาลาอาในสนามราบ + ดำเนิน และประตู
- สะพานเชื่อมเขื่อนเป็นลักษณะนี้ - ขนาบสองด้านยาวกริดตรง

X-UNIT Architecture Lab

โครงการ

WELL-FORNO 30x30

Executive Luxury Villa
บ้านเดี่ยว 4 ชั้น ผ่านเกณฑ์
WELL for Residential (เจตนา)

ที่ดิน 30.00 x 30.00 ม. = 225 ตร.ว.
ถนนสาธารณะทิศเหนือ (สมบัติ 8.00 ม.)

แนวคิด

ตีความจาก FORNO (Gruppo FON):
 โครงไม้ glulam ภายนอกทุกชั้น + ค้ำเหล็ก
 + หลังคาจั่วไม้สนมาตร ชายคาใต้ 3.00
 + โถงไม้ "Forno hall" โปรง 4 ชั้น

ระดับ

± 0.00 ถนน $\cdot F_1 + 0.45 \cdot F_2 + 3.65$
 $F_3 + 6.85 \cdot F_4 + 10.05$
 หลังคาที่แนวนม $+12.95$
 สันหลังคา $+14.95$

หมายเหตุ

- หน่วยเป็นมิลลิเมตร เว้นแต่ระบุ
- ระดับอ้างอิงถนนหน้าที่ดิน ± 0.00
- ห้ามวัดขนาดจากแบบ ใช้ตัวเลขกำกับ
- แบบระดับ Design Development
ต้องให้สถาปนิกและวิศวกรผู้ได้รับ
ใบอนุญาตตรวจสอบและลงนาม
ก่อนยื่นขออนุญาต

ชื่อแผ่น

รูปตัด A-A
+ รูปตัด B-B

มาตราส่วน 1:100

วันที่ 6 ต.ค. 2569 ฉบับ v1 / DD

WELL-FORNO 30x30 · Executive Luxury Villa · บ้านเดี่ยว 4 ชั้น โครโมกายเนก + หลังคาจั่วไม้สมมาตร + โถงไม้ปาร์จ 4 ชั้น (แนวคิดจาก FORNO / Gruppo FON Architeti)

ที่ดิน 30.00 x 30.00 ม. (225 ตร.ว.) · ถนน (สมมติ 8.00 ม.) ที่ดินเดิม · โปรแกรม ARCHSPACE 6 ค.ศ. 2569

ตารางของเปิด (113 รายการ) — หน่วย มม. วัดจาก FFL

รหัส	ชั้น	ชนิด	กว้าง	ขอบล่าง	ขอบบน	คำพ้อง
D01	F1	ประตูหลัก	900	0	2100	โถงหลัก ลิฟต์บ้าน
D02	F1	ประตูบานเปิด	1800	0	2700	โถงต้อนรับ (ทาง ภายนอก-E
SD01	F1	ประตูบานเลื่อนกระจก	4800	0	2700	ลานใต้ชายคา / ทาง โถงกลาง "Fomo
D03	F1	ประตูบานเปิด	1800	0	2400	โถงกลาง "Fomo h ไรรอลา 4 ชั้น
D04	F1	ประตูบานเปิดเดี่ยว	900	0	2100	ตู้เสื้อผ้าห้อง โถงกลาง "Fomo
D05	F1	ประตูบานเปิดเดี่ยว	900	0	2100	ห้องนอนแขกผู้ ตู้เสื้อผ้า
SD02	F1	ประตูบานเลื่อนเดี่ยว	900	0	2100	ห้องนอนแขกผู้ ห้องน้ำห้องแขก
SD03	F1	ประตูบานเลื่อนกระจก	2400	0	2400	ห้องนอนแขกผู้ ลานใต้ชายคา /
D06	F1	ประตูบานเปิดเดี่ยว	900	0	2100	ครัวไทย (ครัวฟ ภายนอก-S
D07	F1	ประตูบานเปิดเดี่ยว	900	0	2100	ห้องสัฟ ภายนอก-S
D08	F1	ประตูบานเปิดเดี่ยว	900	0	2400	ครัวไทย (ครัวฟ โถงกลาง "Fomo
D09	F1	ประตูบานเปิดเดี่ยว	800	0	2100	ห้องสัฟ โถงกลาง "Fomo
D10	F1	ประตูบานเปิดเดี่ยว	900	0	2400	ห้องนอน 1 โถงกลาง "Fomo
D11	F1	ประตูบานเปิดเดี่ยว	900	0	2400	ห้องนอน 2 โถงกลาง "Fomo
D12	F1	ประตูบานเปิดเดี่ยว	800	0	2100	โถงกลาง "Fomo h ห้อง MEP / ใท
D13	F1	ประตูบานเปิดเดี่ยว	800	0	2100	โถงกลาง "Fomo h ห้องน้ำบน
W01	F1	ผนังกระจก	4400	0	2700	ลานใต้ชายคา / ทาง ครัวไทย (ครัวฟ
W02	F1	หน้าต่าง	3000	600	2400	ห้องนอนแขกผู้ ภายนอก-S
W03	F1	หน้าต่าง	3300	600	2400	ห้องนอนแขกผู้ ภายนอก-W
W04	F1	หน้าต่าง	1500	600	2400	ครัวไทย (ครัวฟ ภายนอก-S
W05	F1	หน้าต่าง	1500	600	2400	ห้องนอน 1 ภายนอก-S
W06	F1	หน้าต่าง	1500	600	2400	ห้องนอน 2 ภายนอก-S
W07	F1	หน้าต่าง	3300	600	2400	ห้องนอน 2 ภายนอก-E
W08	F1	หน้าต่าง	1200	1500	2100	ห้องน้ำห้องแขก ภายนอก-W
W09	F1	หน้าต่าง	1200	1500	2100	ห้องน้ำบน ภายนอก-E
W10	F1	ผนังกระจก	1100	0	2700	โถงต้อนรับ (ทาง ภายนอก-E
W11	F1	ผนังกระจก	1100	0	2700	โถงต้อนรับ (ทาง ภายนอก-E
W12	F1	ผนังกระจก	1600	0	3000	บันไดหลัก (โถงใ ภายนอก-N
D14	F2	ประตูหลัก	900	0	2100	โถงหลัก ชั้น 2 ลิฟต์บ้าน
D15	F2	ประตูบานเปิดเดี่ยว	900	0	2100	ครัวไทย + โถง Walk-in Pantry
D16	F2	ประตูบานเปิดเดี่ยว	900	0	2400	ทางเดินแขกผู้ ตู้เสื้อผ้า ัน
D17	F2	ประตูบานเปิดเดี่ยว	800	0	2100	ห้องนอน Junior S ตู้เสื้อผ้า ัน
D18	F2	ประตูบานเปิดเดี่ยว	800	0	2100	ตู้เสื้อผ้า Jun ห้องน้ำ Junior
D19	F2	ประตูบานเปิดเดี่ยว	800	0	2100	ตู้เสื้อผ้า Jun ห้องนอน Junior
D20	F2	ประตูบานเปิดเดี่ยว	800	0	2100	ตู้เสื้อผ้า Jun ห้องน้ำ Junior
D21	F2	ประตูบานเปิดเดี่ยว	800	0	2100	ห้องนอน & ห้อง ห้องน้ำแขก (Po
SD04	F2	ประตูบานเลื่อนกระจก	3600	0	2700	ระเบียงไม้หัด ห้องนอน
SD05	F2	ประตูบานเลื่อนกระจก	3600	0	2700	ระเบียงไม้หัด ห้องรับประทานอาหาร
SD06	F2	ประตูบานเลื่อนกระจก	1800	0	2400	ระเบียงไม้หัด ครัวไทย + โส
D22	F2	ประตูบานเปิดเดี่ยว	900	0	2100	ห้องทำงาน & ห้อง บันไดใฟ้ากาย
D23	F2	ประตูบานเปิดเดี่ยว	900	0	2400	ทางเดินแขกผู้ ห้องนอน Junior
D24	F2	ประตูบานเปิดเดี่ยว	800	0	2100	ทางเดินแขกผู้ ห้องน้ำ / ชัก
D25	F2	ประตูบานเปิดเดี่ยว	900	0	2400	ห้องทำงาน & ห้อง โถงหลัก ชั้น
W13	F2	ผนังกระจก	1300	0	2700	ระเบียงไม้หัด ครัวไทย + โส
W14	F2	ผนังกระจก	1300	0	2700	ระเบียงไม้หัด ครัวไทย + โส
W15	F2	ผนังกระจก	1700	0	2700	ระเบียงไม้หัด ห้องรับประทานอาหาร
W16	F2	ผนังกระจก	1700	0	2700	ระเบียงไม้หัด ห้องรับประทานอาหาร
W17	F2	ผนังกระจก	2500	0	2700	ระเบียงไม้หัด ห้องนอน
W18	F2	ผนังกระจก	2500	0	2700	ระเบียงไม้หัด ห้องนอน
W19	F2	หน้าต่าง	5400	900	2700	ห้องรับประทานอาหาร ห้องน้ำโถงใ
W20	F2	หน้าต่าง	1500	900	2700	ห้องนอน ห้องน้ำโถงใ
W21	F2	หน้าต่าง	3300	600	2400	ครัวไทย + โถง ภายนอก-W
W22	F2	หน้าต่าง	3300	600	2400	ห้องนอน ภายนอก-E
W23	F2	หน้าต่าง	1200	1500	2100	ห้องน้ำแขก (Pow ภายนอก-E
W24	F2	หน้าต่าง	2400	600	2400	ห้องนอน Junior S ภายนอก-N
W25	F2	หน้าต่าง	3300	600	2400	ห้องนอน Junior S ภายนอก-W
W26	F2	หน้าต่าง	1200	1500	2100	ห้องน้ำ Junior S ภายนอก-N

รหัส	ชั้น	ชนิด	กว้าง	ขอบล่าง	ขอบบน	คำพ้อง
W27	F2	หน้าต่าง	1200	1500	2100	ห้องน้ำ Junior S ภายนอก-N
W28	F2	หน้าต่าง	2400	600	2400	ห้องนอน Junior S ภายนอก-N
W29	F2	หน้าต่าง	3300	600	2400	ห้องทำงาน & ห้อง ภายนอก-E
W30	F2	ผนังกระจก	1600	0	3000	บันไดหลัก (โถงใ ภายนอก-N
D26	F3	ประตูหลัก	900	0	2100	โถงหลัก ชั้น 3 ลิฟต์บ้าน
D27	F3	ประตูบานเปิดเดี่ยว	1000	0	2400	ห้องนอน Master S สะพานไม้ ชั้น
D28	F3	ประตูบานเปิดเดี่ยว	900	0	2400	Walk-in Dressing ห้องนอน Master
SD07	F3	ประตูบานเลื่อนเดี่ยว	900	0	2400	ห้องน้ำ Spa + Ja Walk-in Dressi
SD08	F3	ประตูบานเลื่อนกระจก	3600	0	2700	ระเบียงไม้หัด ห้องนอน Master
SD09	F3	ประตูบานเลื่อนกระจก	2400	0	2400	ทางเดินแขกผู้ ลอเจียคันท
SD10	F3	ประตูบานเลื่อนกระจก	1200	0	2400	ลอเจียคันท โถงหลัก ชั้น
D29	F3	ประตูบานเปิดเดี่ยว	900	0	2100	ลอเจียคันท บันไดใฟ้ากาย
W31	F3	หน้าต่าง	1200	1500	2100	ระเบียงไม้หัด ห้องน้ำ Spa +
W32	F3	ผนังกระจก	2020	0	2700	ระเบียงไม้หัด ห้องนอน Master
W33	F3	ผนังกระจก	2380	0	2700	ระเบียงไม้หัด ห้องนอน Master
W34	F3	ผนังกระจก	1600	0	3000	ระเบียงไม้หัด บันไดส่วนหัว M
W35	F3	หน้าต่าง	1200	1500	2100	Walk-in Dressing ห้องน้ำโถงใ
W36	F3	หน้าต่าง	1200	900	2700	ห้องนอน Master S ห้องน้ำโถงใ
W37	F3	หน้าต่าง	1500	900	2700	ห้องนอน Master S ห้องน้ำโถงใ
W38	F3	ผนังกระจก	2400	0	2700	ทางเดินแขกผู้ ลอเจียคันท
W39	F3	ผนังกระจก	2400	0	2700	ทางเดินแขกผู้ ลอเจียคันท
W40	F3	ผนังกระจก	4400	0	3000	ลอเจียคันท บันไดหลัก (โถ
W41	F3	หน้าต่าง	1200	1500	2100	ห้องน้ำ Spa + Ja ภายนอก-N
W42	F3	หน้าต่าง	1200	1500	2100	ห้องน้ำ Spa + Ja ภายนอก-W
W43	F3	หน้าต่าง	1800	600	2400	ห้องนอน Master S ภายนอก-W
W44	F3	ผนังกระจก	1600	0	3000	บันไดส่วนหัว Mas ภายนอก-N
W45	F3	ผนังกระจก	4400	0	3000	บันไดส่วนหัว Mas ภายนอก-E
W46	F3	ผนังกระจก	1500	0	3000	ห้องน้ำโถงใ ทุ ภายนอก-W
W47	F3	ผนังกระจก	1500	0	3000	ห้องน้ำโถงใ ทุ ภายนอก-E
W48	F3	ผนังกระจก	900	0	2700	ทางเดินแขกผู้ ภายนอก-W
W49	F3	ผนังกระจก	900	0	2700	ทางเดินแขกผู้ ภายนอก-E
W50	F3	ผนังกระจก	1600	0	3000	บันไดหลัก (โถงใ ภายนอก-N
D30	F4	ประตูหลัก	900	0	2100	โถงหลัก ชั้น 4 ลิฟต์บ้าน
SD11	F4	ประตูบานเลื่อนกระจก	1500	0	2700	ระเบียง & BBQ (สะพานไม้ ชั้น
SD12	F4	ประตูบานเลื่อนกระจก	1800	0	2400	ระเบียง Master (Master Walk-in
D31	F4	ประตูบานเปิดเดี่ยว	800	0	2100	ห้องนอนครอบครัว ห้องอุปกรณ์ AV
D32	F4	ประตูบานเปิดเดี่ยว	900	0	2100	ห้องนอนเดี่ยว บันไดใฟ้ากาย
D33	F4	ประตูบานเปิดเดี่ยว	800	0	2100	ทางเดินแขกผู้ ห้องน้ำชั้น 4
D34	F4	ประตูบานเปิดเดี่ยว	900	0	2400	ห้องนอนเดี่ยว โถงหลัก ชั้น
W51	F4	หน้าต่าง	1100	1500	2100	ระเบียง Master (Master Walk-in
W52	F4	หน้าต่าง	1100	1500	2100	ระเบียง Master (Master Walk-in
W53	F4	ผนังกระจก	1600	0	3000	ระเบียง Master (บันไดส่วนหัว M
W54	F4	หน้าต่าง	1200	1500	2100	Master Walk-in C ห้องน้ำโถงใ
W55	F4	หน้าต่าง	1200	1500	2100	Master Walk-in C ภายนอก-N
W56	F4	ผนังกระจก	1600	0	3000	บันไดส่วนหัว Mas ภายนอก-N
W57	F4	ผนังกระจก	4400	0	3000	บันไดส่วนหัว Mas ภายนอก-E
W58	F4	ผนังกระจก	1500	0	3000	ห้องน้ำโถงใ ทุ ภายนอก-W
W59	F4	ผนังกระจก	1500	0	3000	ห้องน้ำโถงใ ทุ ภายนอก-E
W60	F4	ผนังกระจก	900	0	2700	ทางเดินแขกผู้ ภายนอก-W
W61	F4	ผนังกระจก	900	0	2700	ทางเดินแขกผู้ ภายนอก-E
W62	F4	หน้าต่าง	3000	600	2400	ห้องนอนครอบครัว ภายนอก-S
W63	F4	หน้าต่าง	6000	600	2400	ห้องนอนครอบครัว ภายนอก-N
W64	F4	หน้าต่าง	3300	600	2400	ห้องนอนครอบครัว ภายนอก-W
W65	F4	หน้าต่าง	1200	1500	2100	ห้องอุปกรณ์ AV / ภายนอก-N
W66	F4	หน้าต่าง	3300	600	2400	ห้องนอนเดี่ยว ภายนอก-S
W67	F4	ผนังกระจก	1600	0	3000	บันไดหลัก (โถงใ ภายนอก-N

๑.39 ข้อ 6 ของเปิด >= 10% ของพื้นที่ห้อง

ห้อง	ข้อเปิดพื้นที่ห้อง	ผล
F1 ห้องนอนแขกผู้	74.3% (17.10/23.00)	ผ่าน
F1 ครัวไทย (ครัวฟ)	72.1% (15.15/21.00)	ผ่าน
F1 ห้องสัฟ	3.5% (0.57/16.00) -> พัดลมระบายอากาศ (ข้อ 6 วรร	ผ่าน
F1 ห้องน้ำบน	20.0% (2.70/13.50)	ผ่าน
F1 ห้องน้ำบน 2	64.0% (8.64/13.50)	ผ่าน
F1 ห้องน้ำห้องแขก	19.4% (0.72/6.90)	ผ่าน
F1 ตู้เสื้อผ้าห้องแขก	0.0% (0.00/6.90) -> พัดลมระบายอากาศ (ข้อ 6 วรร	ผ่าน
F1 ห้องน้ำบน	16.0% (0.72/4.50)	ผ่าน
F1 ห้อง MEP / ใฟ้า / เคื่องอื่น	0.0% (0.00/12.00) -> พัดลมระบายอากาศ (ข้อ 6 วรร	ผ่าน
F2 ครัวไทย + โถงคันท	64.0% (17.28/27.00)	ผ่าน
F2 ห้องรับประทานอาหาร	47.2% (18.90/40.00)	ผ่าน
F2 ห้องนอน	60.7% (29.16/48.00)	ผ่าน
F2 Walk-in Pantry & ห้องอื่น	0.0% (0.00/13.80) -> พัดลมระบายอากาศ (ข้อ 6 วรร	ผ่าน
F2 ห้องครัว / ชัก	0.0% (0.00/9.60) -> พัดลมระบายอากาศ (ข้อ 6 วรร	ผ่าน
F2 ห้องน้ำแขก (Powder)	11.4% (0.72/6.30)	ผ่าน
F2 ห้องนอน Junior Suite 2	51.3% (10.26/20.00)	ผ่าน
F2 ตู้เสื้อผ้า Junior Suite 2	0.0% (0.00/5.76) -> พัดลมระบายอากาศ (ข้อ 6 วรร	ผ่าน
F2 ห้องน้ำ Junior Suite 2	11.5% (0.72/6.24)	ผ่าน
F2 ตู้เสื้อผ้า Junior Suite 3	0.0% (0.00/5.76) -> พัดลมระบายอากาศ (ข้อ 6 วรร	ผ่าน
F2 ห้องน้ำ Junior Suite 3	11.5% (0.72/6.24)	ผ่าน
F2 ห้องนอน Junior Suite 3	21.6% (4.32/20.00)	ผ่าน
F2 ห้องทำงาน & ห้องสุม	19.2% (5.94/31.00)	ผ่าน
F3 ห้องน้ำ Spa + Jacuzzi	8.0% (2.16/27.00) -> พัดลมระบายอากาศ (ข้อ 6 วรร	ผ่าน
F3 Walk-in Dressing (His & Hers)	0.0% (0.00/29.00) -> พัดลมระบายอากาศ (ข้อ 6 วรร	ผ่าน
F3 ห้องนอน Master Suite	55.1% (26.46/48.00)	ผ่าน
F4 Master Walk-in Closet ชั้น 4	18.2% (6.36/35.00)	ผ่าน
F4 ห้องนอนครอบครัว & Upper Ga	49.2% (22.14/45.00)	ผ่าน
F4 ห้องน้ำชั้น 4	0.0% (0.00/9.50) -> พัดลมระบายอากาศ (ข้อ 6 วรร	ผ่าน
F4 ห้องอุปกรณ์ AV / เก็บของ	7.6% (0.72/9.50) -> พัดลมระบายอากาศ (ข้อ 6 วรร	ผ่าน
F4 ห้องนอนเดี่ยว	19.2% (5.94/31.00)	ผ่าน

ระบายอากาศ >= 2 แนวหนึ่ง (เกณฑ์ภายใน สทปนสน R-T06) / ลึก <= 4.20 ม.

หน่วยคำนวณระบาย	ข้อเปิด	ลึกจากผนังนอก	ผล
F1 ห้องนอนแขกผู้	3 แนวหนึ่ง	2.25 ม.	ผ่าน
F1 ครัวไทย (ครัวฟ)	2 แนวหนึ่ง	4.05 ม.	ผ่าน
F1 ห้องน้ำบน 1	1 แนวหนึ่ง -> ยกเว้น 1	4.95 ม. -> ยกเว้น ห้องเปิด	ผ่าน
F1 ห้องน้ำบน 2	2 แนวหนึ่ง	2.55 ม.	ผ่าน
F2 ครัวไทย + โถงคันท	2 แนวหนึ่ง	2.77 ม.	ผ่าน
F2 ห้องรับประทานอาหาร	2 แนวหนึ่ง	2.45 ม.	ผ่าน
F2 ห้องนอน	2 แนวหนึ่ง	2.85 ม.	ผ่าน
F2 ห้องนอน Junior Suite 2	2 แนวหนึ่ง	3.75 ม.	ผ่าน
F2 ห้องนอน Junior Suite 3	1 แนวหนึ่ง -> ยกเว้น 1	4.85 ม. -> ยกเว้น เปิดด้านท	ผ่าน
F2 ห้องทำงาน & ห้องสุม	2 แนวหนึ่ง	4.85 ม. -> ยกเว้น หน้าต่างค	ผ่าน
F3 ห้องนอน Master Suite	2 แนวหนึ่ง	2.55 ม.	ผ่าน
F4 ห้องนอนครอบครัว & Upper Ga	3 แนวหนึ่ง	4.27 ม. -> ยกเว้น เปิด 3 ด้าน	ผ่าน
F4 ห้องนอนเดี่ยว	2 แนวหนึ่ง	2.85 ม.	ผ่าน

ตรวจรายละเอียดของเปิด (โดยทั่วไปรวมทุก) 18 รายการ: ผ่าน 18

เทียบโปรแกรม ARCHSPACE (ตร.ม.)

รายการโปรแกรม	ชั้น	โปรแกรม	ชั้นบน	แบบ	ค่า
Grand Double-Height Foyer	F1	24.00	F1	19.00	-5.00
Formal Living Room	F2	50.00	F2	48.00	-2.00
Dining Room (10-12 Seats)	F2	40.00	F2	40.00	+0.00
Powder Room	F2	6.00	F2	6.30	+0.30
Home Theater / AV Lounge	F4	36.00	F4	31.00	-5.00
Wine Cellar / Cigar Room	F2	14.00	F2	9.60	-4.40
Master Suite Bedroom	F3	48.00	F3	48.00	+0.00
Master Walk-in (His & Hers)	F3	32.00	F3	29.00	-3.00
Spa Master Bath + Jacuzzi	F3	28.00	F3	27.00	-1.00
Junior Suite 2 (bath+closet)	F2	34.00	F2	32.00	-2.00
Junior Suite 3 (bath+closet)	F2	34.00	F2	32.00	-2.00
Guest Suite (CF / elderly)	F1	30.00	F1	36.80	+6.80
Family Lounge & Upper Gallery	F4	36.00	F4	45.00	+9.00
Executive Home Office & Library	F2	26.00	F2	31.00	+5.00
Master Walk-in Closet (UL)	F4	36.00	F4	35.00	-1.00
Show Kitchen & Island Bar	F2	28.00	F2	27.00	-1.00
Heavy Thai Kitchen	F1	20.00	F1	21.00	+1.00
Walk-in Pantry & Cold Storage	F3	12.00	F2	13.80	+1.80
Laundry & Utility Room	F1	16.00	F1	16.00	+0.00
Maid Bedroom 1 & 2	F1	22.00	F1	27.00	+5.00
Maid Bathroom	F1	6.00	F1	4.50	-1.50
MEP / Electrical / Generator	F1	14.00	F1	12.00	-2.00
Covered Garage 3-4 cars	F1	85.00	F1	76.80	-8.20
Covered Veranda & BBQ	F4	45.00	F4	57.20	+12.20
Upper Master Terrace	F4	28.00	F4	46.30	+18.30
Poolside Pavilion	F1	35.00	F1	36.40	+1.40
รวม NJA		785.00		807.70	+22.70

แบบรูป = ขึ้นในแบบต่างๆโปรแกรม (Pantry ชั้น 3 -> 2 ถู A-01 ข้อ 3) · ศาลาริมสระ = ลานใต้ชายคาชั้น 1
ห้องใช้ตามเงื่อนไขพื้นที่ว่าง 13.00 ม. (5.00 | 3.00 | 5.00) — ห้องใช้สำหรับโปรแกรมอื่น 10% ของค่า "ค่า" คิดลบ

H3A DESIGN AND BUILD

X-UNIT Architecture Lab

โครงการ

WELL-FORNO 30x30

Executive Luxury Villa

บ้านเดี่ยว 4 ชั้น ผ่านเกณฑ์
WELL for Residential (เจดนา)

ที่ดิน 30.00 x 30.00 ม. = 225 ตร.ว.
ถนนสาธารณะติดหน้า (สมมติ 8.00 ม.)

แนวคิด

ตีความจาก FORNO (Gruppo FON):
โครโม กล้าม ภายนอกทุกชั้น + คำเสียง
+ หลังคาจั่วไม้สมมาตร ชายคาใต้ 3.00
+ โถงไม้ "Forno hall" ปาร์จ 4 ชั้น

ระดับ

±0.00 ถนน · F1 +0.45 · F2 +3.65
F3 +6.85 · F4 +10.05
หลังคาที่แนวหนึ่ง +12.95
สิ้นหลังคา +14.95

หมายเหตุ

· หน่วยเป็นมิลลิเมตร เว้นแต่ระบุ
· ระดับอ้างอิงถนนหน้าที่ดิน ±0.00
· ห้ามวัดขนาดจากขอบ ใช้ตัวเลขกำกับ
· แบบระดับ Design Development
ต้องให้สถาปนิกและวิศวกรผู้ได้รับ
ใบอนุญาตตรวจสอบและลงนาม
ก่อนยื่นขออนุญาต

WELL-FORNO 30x30 · Executive Luxury Villa · บ้านเดี่ยว 4 ชั้น โครงไม้ภายนอก + หลังคาจั่วไม้สมมาตร + โถงไม้โปร่ง 4 ชั้น (แนวคิดจาก FORNO / Gruppo FON Architeti)


ที่ดิน 30.00 x 30.00 ม. (225 ตร.ว.) · ถนน (สมมติ 8.00 ม.) ทิศเหนือ · โปรแกรม ARCHISPACE 6 ต.ค. 2569

กลยุทธ์ WELL for Residential (รหัสตาม Guidebook ก.พ. 2026)


Feature (WELL for Residential)	การตอบสนองในแบบ	สถานะ	หลักฐานที่ต้องมี
R-A01 ระบบระบายอากาศ	พัดลมดูดเฉพาะจุดครัว/ห้องน้ำห้องไม่มีหน้าต่าง 11 ห้อง + ERV ห้องนอน	ระบุในแบบงานระบบ	ต้องวัด
R-A05 ลดการเผาไหม้	ครัวโซว์ชั้น 2 เตาไฟฟ้าเหนี่ยวนำ; ครัวไทยเตาอบหินอยู่ชั้น 1 แยก มีชุด เตาอบอยู่นอกอาคาร	ในแบบ	เอกสาร
R-A09 จุดชาร์จ EV	1 จุดในโรงจอดรถ (ช่องเมื่อ 4 ช่อง)	ในแบบ	ภาพถ่าย
R-W03 น้ำที่ไม่ใช่ น้ำดื่ม	ถังน้ำฝนใต้ดิน ~12 ลบ.ม. จากหลังคาจั่ว สำหรับรดน้ำ/ซักโครก	ในแบบ	แบบสุขาภิบาล
R-L01 แสงธรรมชาติ	48.1% (183.4/381.0 ตร.ม.) -> ระดับ 3 (ไม่นับกระจกคู่โถง)	คำนวณแล้ว	ต้องตรวจแสงจ้า
R-L02 ควบคุมแสง	วงจแยกทุกห้อง + ม่านพับห้องนอน/เฮียเตอร์ · ซายดาโต้ 3.00 ม. ลดแสงจ้า	ระบุ	แบบไฟฟ้า
R-T06 หน้าต่างเปิดได้	13/13 ห้อง	คำนวณแล้ว	มุงลาด/ตัวล็อก
R-T07 ความร้อนภายนอก	ซายดาโต้ 3.00 ม. + ระเบียงไม้บังแดด + หลังคาสีอ่อน + PV 23% ของหลังคา + ดันไม้ร่ม	ในแบบ	ค่า SR วัสดุ
R-V04 พื้นที่กิจกรรมกลางแจ้ง	สระ 14.00 x 3.00 ม. + piazza/ศาลา + ระเบียงไม้ทุกชั้น + ล่องเจีย + BBQ	ในแบบ	-
R-V07 ออกแบบบันได	บันไดหลักไม้เปิดโล่งสู่โถงไม้/เกลเลอรี ผนังกระจกทิศเหนือ อยู่หน้าลิฟต์ทุกชั้น	ในแบบ	ภาพถ่าย
R-M01 ธรรมชาติและสถานที่	โครงไม้ glulam เปิดโชว์ภายใน-ภายนอก + มงสวนสระทุกชั้น + เคาบหิน (Forno)	ในแบบ	-
R-M04 พื้นที่จัดเก็บ	Walk-in 2 ชั้น (Master) + ตู้ทุกห้องนอน + Pantry + ห้อง AV/เก็บของ	ในแบบ	-
R-N01 การปรุงอาหาร	ครัว 2 ส่วน (โซว์/ไทย) + Pantry ห้องเย็นติดครัวโซว์ + โต๊ะยาวในโถงกลาง	ในแบบ	-
R-S01 แนวกันเสียง	โถงโปร่ง 4 ชั้นส่งเสียงข้ามชั้น -> ฝ้าไม้ชั้นเสียง + ประตูดห้องนอนกันเสียง	ต้องระบุ STC	ทดสอบ
R-C01 ออกแบบเพื่อทุกคน	ลิฟต์บ้านทุกชั้น + ห้องแขกชั้น 1; ทางลาด 1:12 ยังต้องเพิ่ม	บางส่วน	ดู A-01 ข้อ 11
R-C06 กายพิบัตื	ยกพื้น +0.45 + บันไดหนีไฟ + เครื่องปั่นไฟ + ตรวจจับควันในโถงโปร่ง	ในแบบ	ระดับน้ำท่วมจริง?
R-X02 วัสดุ	ไม้รับรอง FSC/PEFC กาวไร้ฟอร์มาลดีไฮด์ สี/เคลือบ VOC ต่ำ	สเปก	ใบสั่งซื้อ

สถานะ = เจตนาการออกแบบ ยังไม่ใช่คะแนนรับรอง: WELL Residence ต้องลงทะเบียน JWBI ส่งเอกสาร และตรวจวัดจริงหลังก่อสร้าง
ห้องที่ใช้พัฒนาะบาย: ห้องซักрид, ตู้เสื้อผ้าห้องแขก, ห้อง MEP / ไฟฟ้า / เครื่องปั่นไฟ, Walk-in Pantry & ห้องเย็น, ห้องโถงไม้ / ซัการ, ตู้เสื้อผ้า Junior Suite 2, ตู้เสื้อผ้า Junior Suite 3, ห้องน้ำ Spa + Jacuzzi, Walk-in Dressing (His & Hers), ห้องน้ำชั้น 4, ห้องอุปกรณ์ AV / เก็บของ

มุมมองทิศตะวันตกเฉียงเหนือ — หน้าจั่วระแนงไม้ ลาดหลังคาทิศเหนือ เสาไม้หน้าโรงรถ

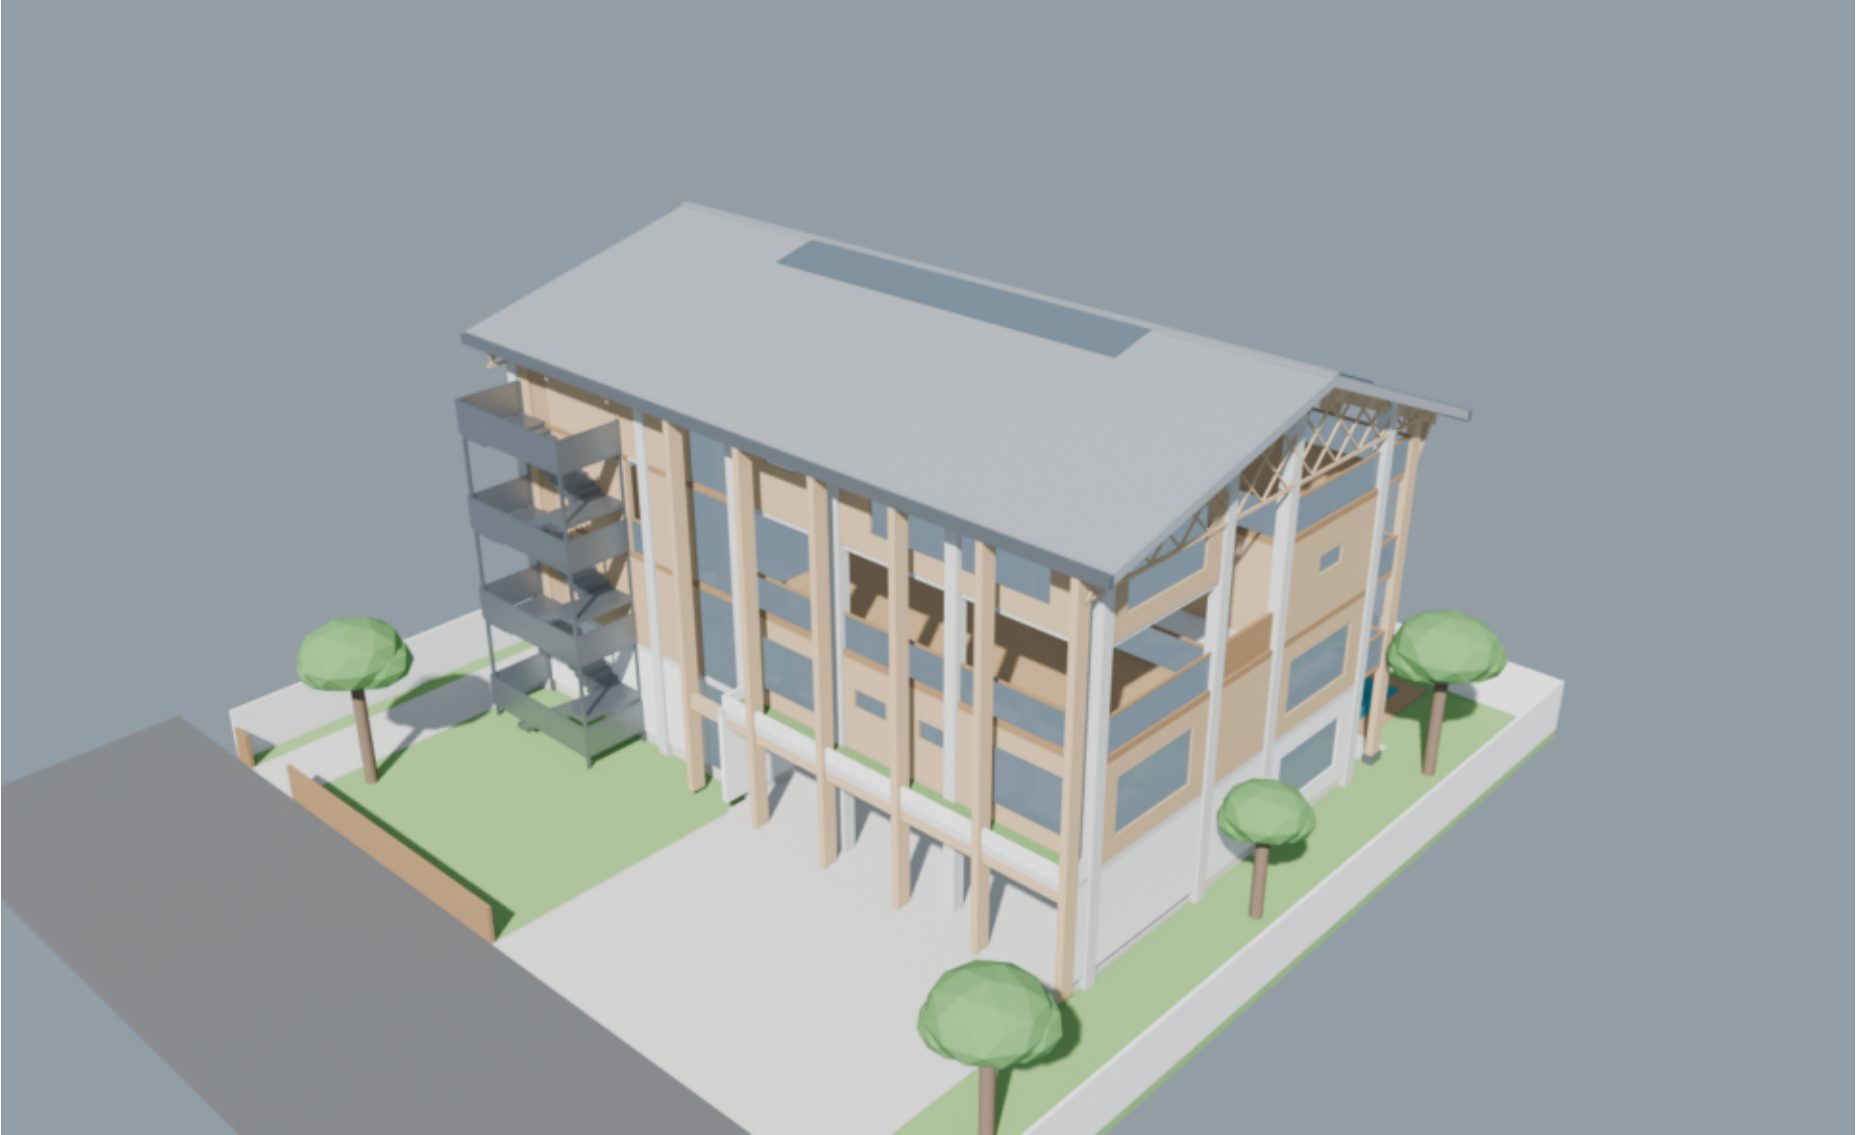

จากสวนทิศใต้ — เฟรมไม้ glulam ดำเอียงรับซายดา ระเบียงไม้ ผนังกระจก

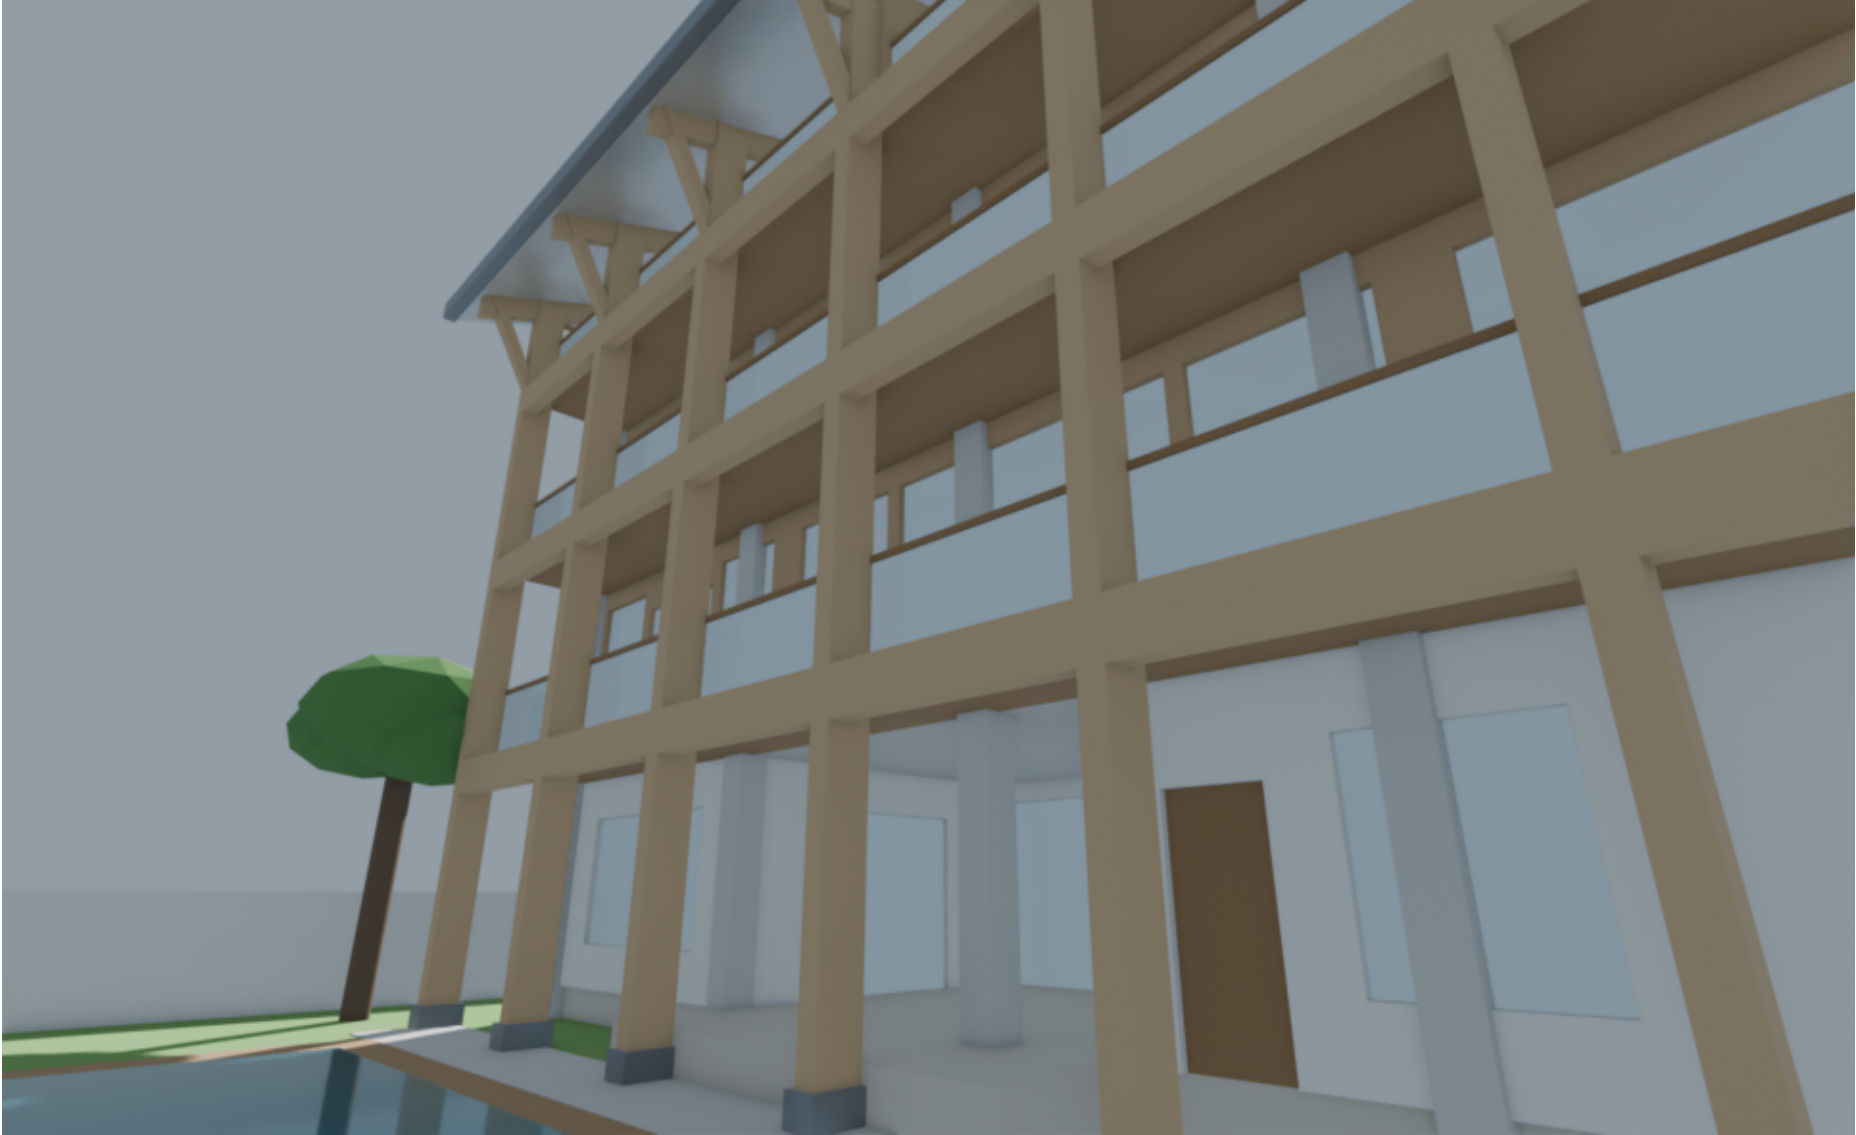

วัสดุหลัก

หมวด	ข้อกำหนด (ระดับแนวคิด)
โครงสร้างหลัก	ค.ส.ล. เสา 0.40x0.40 กริด 6 x 4 แนว · พื้นดานแบน 0.20 · ผนังรอบบันได/ลิฟต์ ค.ส.ล. · เสาเอ็นเจาะ (รอผลเจาะดิน)
โครงไม้ภายนอก	glulam เสา 240x480 @2.875 + ค้ำเอียง + คานขอบระเียง · ตัวยึดสแตนเลส · ฐานเหล็กสูง 0.30 ม. · ไม้ใช้โครงสร้างหลัก
หลังคา	แป้ไม้ glulam 160x400 ทุกเฟรม + standing seam สีอ่อน + PJR 75 + ฝ้าไม้ · ช่องแสงสันหลังคา laminated Low-E
ผนังภายนอก	ชั้น 1 ปูนฉาบขาว · ชั้น 2-4 บล็อกมวลเบา 200 + ไม้กรุแนวตั้งบนโครงสร้าง · ผนังภายใน 120 / ห้องน้ำ 150
ระเียง / สะพาน	พื้น ค.ส.ล. ยื่น 1.50 ม. ปูไม้ทึบเคลดผ่น · สะพานข้ามโถงโครงสร้าง+พื้นไม้ · ราวระเียง 1.10 ม.
กระจก	Low-E laminated · SHGC <= 0.25 ทิศตะวันออก/ตะวันตก · กระจกคู่โถงเป็นกระจกนิรภัย
พื้น	หินขัด/คอนกรีตขัดมัน (ชั้น 1 โถง/ศาลา) · ไม้เอ็นจิเนียร์ (ชั้น 2-4) · กระเบื้องกันสั่น R11
ภายนอก	สระน้ำเกลือ 14.00 x 3.00 สัก 1.40 ม. · ลาน piazza หินแกรนิต · เคาบหิน · บันไดหนีไฟเหล็กกล้าในซั

สิ่งที่ต้องทำต่อ

- วิศวกรโครงสร้าง: โครง ค.ส.ล. + ซายดายื่น 3.00 ม. (แรงลมยก) + จุดต่อไม้-คอนกรีต + อัตราหนไฟโครงสร้างหลังคาไม้ + เสาเอ็น
- วิศวกรงานระบบ: VRF + ERV, ระบายควันโถงโปร่ง 4 ชั้น, พัดลมระบาย, น้ำฝน, ปั้ไฟฟ้า, โซลาร์ 20.90 kWp
- ยืนยันกับสำนักงานเขต: ข้อ 27 บันไดหนีไฟบ้านเดี่ยว 4 ชั้น, การวัดความสูงหลังคาจั่ว, ความกว้างถนน, ผังเมืองรวม
- จำลอง CFD/ความร้อน: stack effect ในโถงไม้ (ยังเป็นสมมติฐาน); จำลองแสง/แสงจ้าห้องหลัก
- แบบขยาย: จุดต่อเสาไม้/ค้ำ, รางน้ำ, ช่องแสงสันหลังคา, สะพานไม้, หน้าจั่วระแนง, บันไดส่วนหัว, ทางลาด 1:12, เคาบหิน
- เลือกลิฟต์บ้านรุ่น overhead <= 2.60 ม. และหลุมลิฟต์ · แผนบำรุงรักษาไม้ภายนอก
- ลงทะเบียน WELL Residence · ประมาณราคาละเอียด (BOQ) หลังได้แบบโครงสร้าง-งานระบบ

สรุปการตรวจ

ผลตรวจทั้งหมด 111 รายการ: ผ่าน 111 / ไม่ผ่าน 0 (รายการ "ยกเว้น" มีเหตุผลกำกับ ดู A-11)
แบบระดับ design development ต้องให้สถาปนิกและวิศวกรผู้ได้รับใบอนุญาตตรวจสอบและลงนามก่อนยื่นขออนุญาต

H3A DESIGN AND BUILD

X-UNIT Architecture Lab

โครงการ

WELL-FORNO 30x30

Executive Luxury Villa
บ้านเดี่ยว 4 ชั้น ผ่านเกณฑ์
WELL for Residential (เจดนา)

ที่ดิน 30.00 x 30.00 ม. = 225 ตร.ว.
ถนนสาธารณะทิศเหนือ (สมมติ 8.00 ม.)

แนวคิด

ตีความจาก FORNO (Gruppo FON):
โครงไม้ glulam ภายนอกทุกชั้น + ค้ำเอียง
+ หลังคาจั่วไม้สมมาตร ซายดาโต้ 3.00
+ โถงไม้ "Forno hall" โปร่ง 4 ชั้น

ระดับ

±0.00 ถนน · F1 +0.45 · F2 +3.65
F3 +6.85 · F4 +10.05
หลังคาที่แนวหนึ่ง +12.95
สันหลังคา +14.95

หมายเหตุ

- หนึ่งเป็นผลิตภัณฑ์ เว้นแต่ระบุ
- ระดับอ้างอิงถนนพื้นที่ดิน ±0.00
- ห้ามวัดขนาดจากแบบ ใช้ตัวเลขกำกับ
- แบบระดับ Design Development

ต้องให้สถาปนิกและวิศวกรผู้ได้รับ
ใบอนุญาตตรวจสอบและลงนาม
ก่อนยื่นขออนุญาต

ชื่อแผ่น

WELL for Residential
+ วัสดุ + สิ่งที่ต้องทำต่อ

มาตราส่วน: ไม่มีมาตราส่วน
วันที่ 6 ค.ค. 2569 ฉบับ v1 / DD