




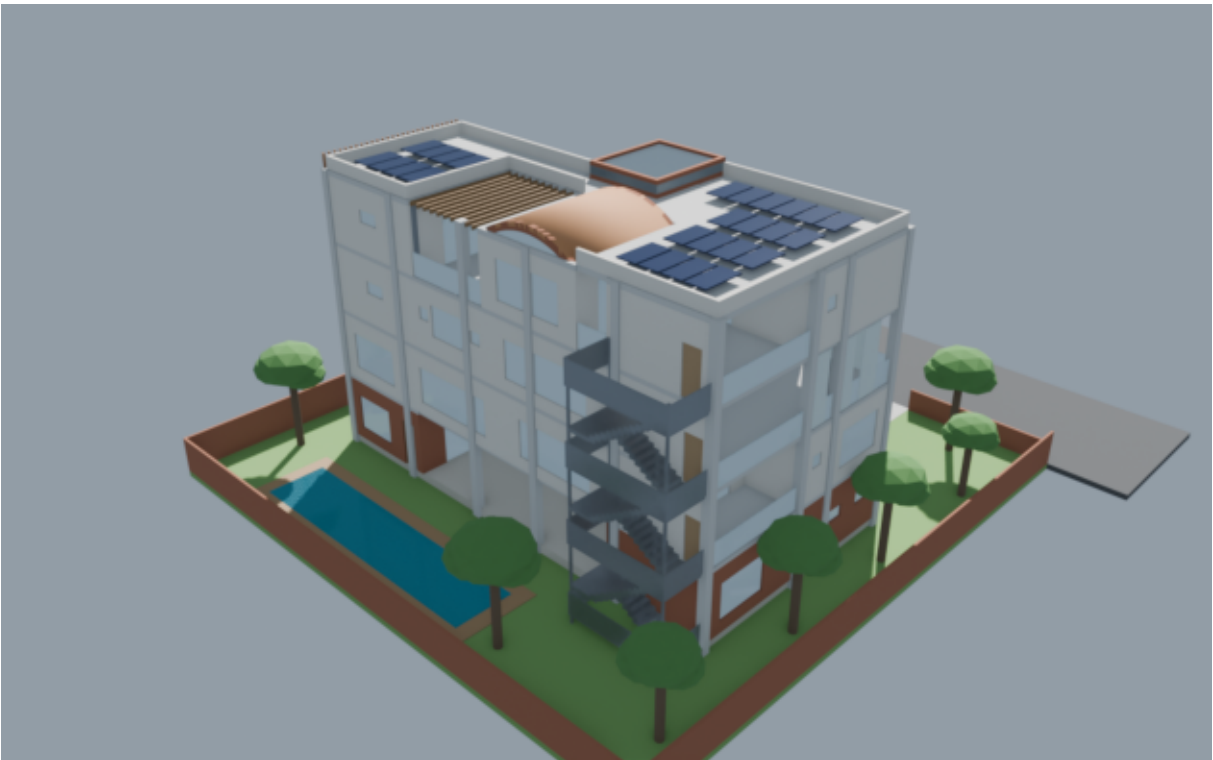


มุมมองทางอากาศ ทิศตะวันออกเฉียงใต้ — แท่งอาคาร 23.00 x 12.00 ม. หลังคาโค้งดินเผา ปล่องอิฐ และบันไดหนีไฟเหล็ก

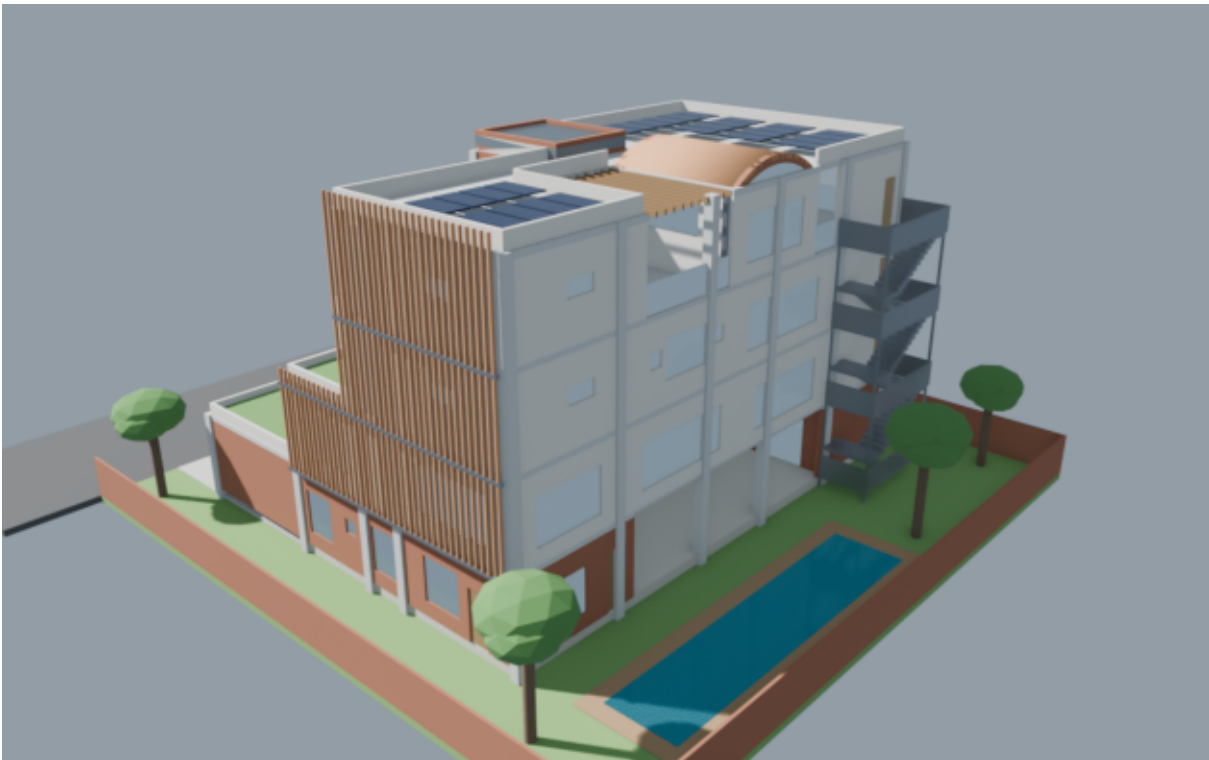

มุมมองทิศตะวันตกเฉียงใต้ — คริบดินเผาทิศตะวันตก (ปีงแดดบ่าง) ฐานอิฐชั้น 1 สระ 14.00 x 3.00 ม.

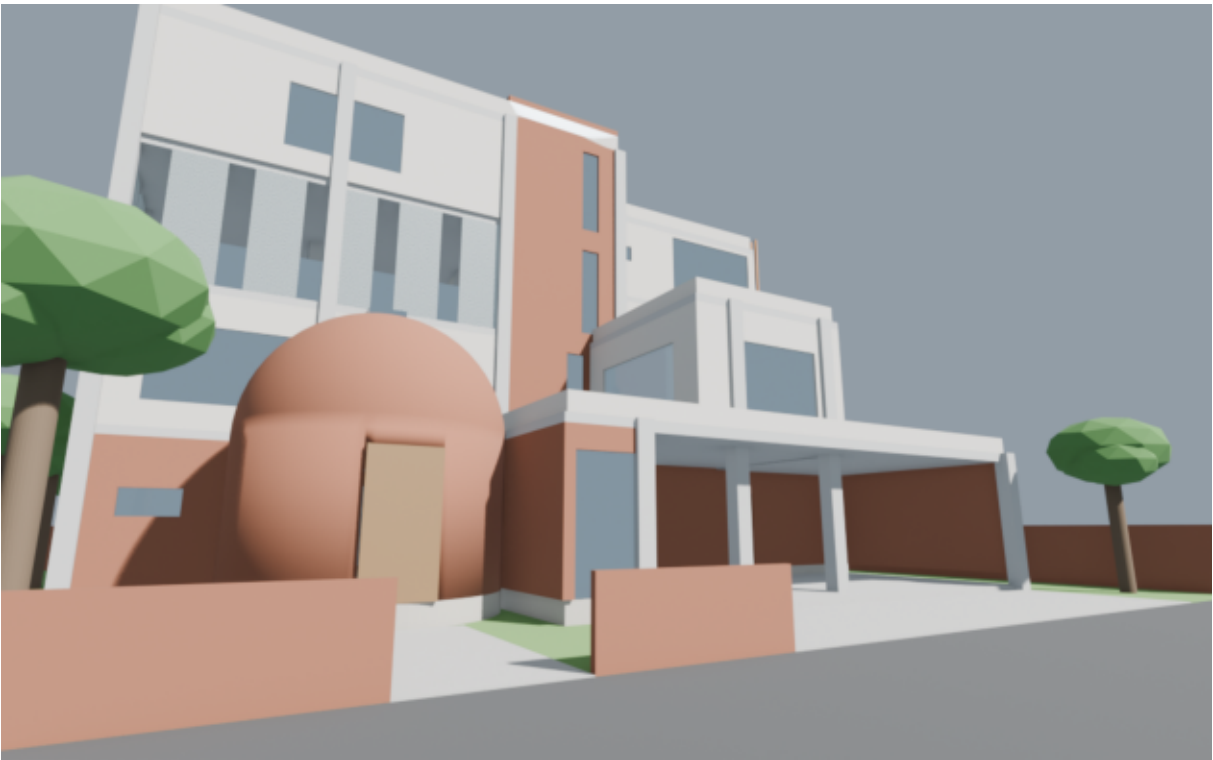


จากถนนทิศเหนือ — โดมอิฐ "เตาเผา" เป็นทางเข้าหลัก ข้างโรงจอดรถ 4 คัน และห้องทำงานบนหลังคาสวน

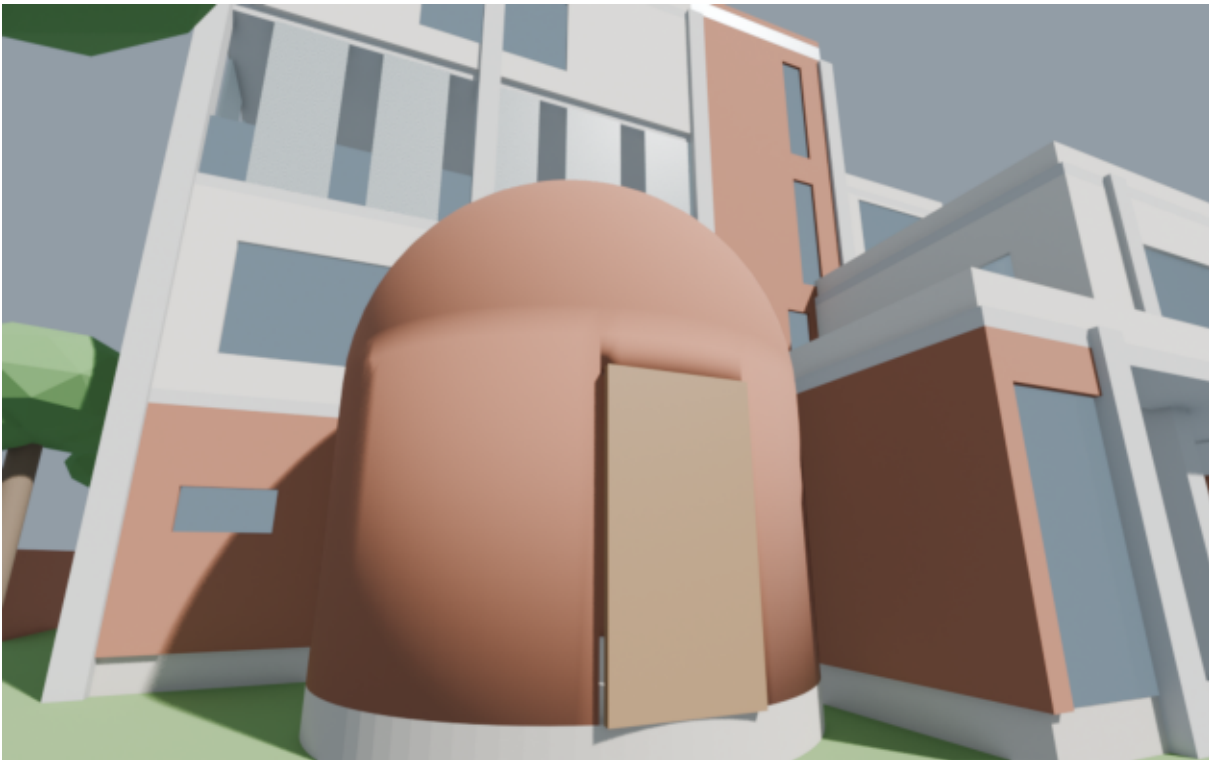


ทางเข้าโดมอิฐ Ø5.60 ม. ยอด +6.25 ช่องแสง oculus ด้านบน ปล่องอิฐด้านหลัง

โตะแกรมผังชั้น 1 (1:250): โดมเตาเผา -> โถง -> ปล่องอิฐ; ทางลมเหนือ-ใต้; ลานใต้ถุนเปิดสู่สวนสระ

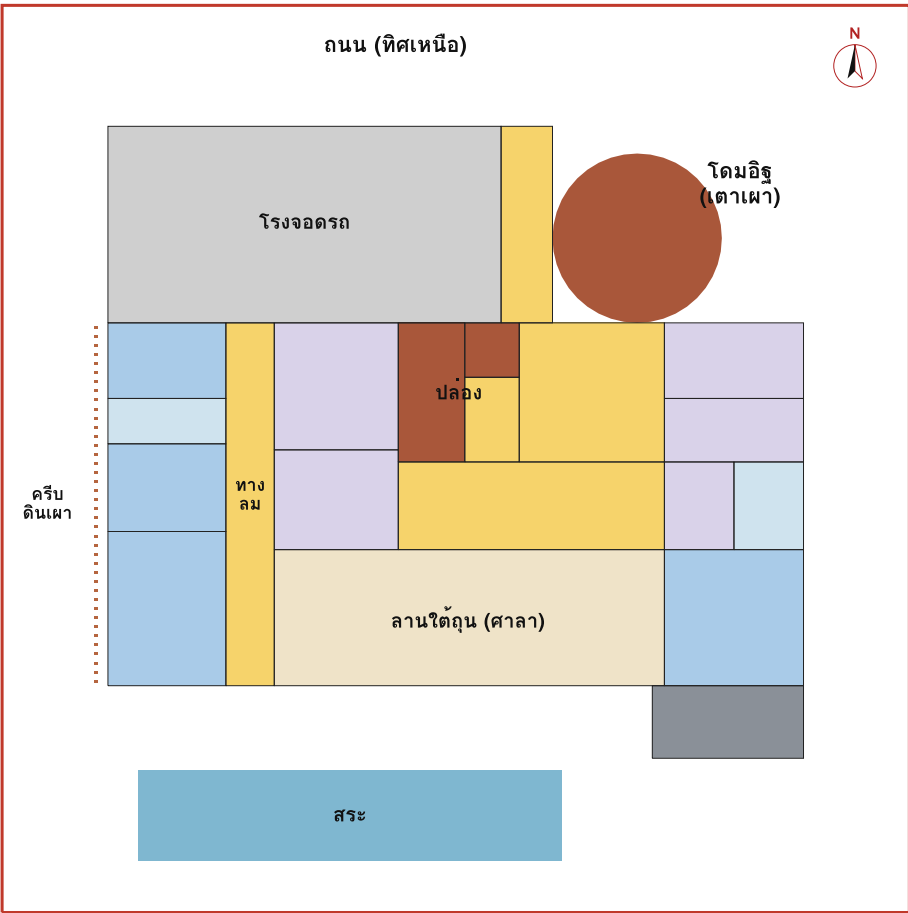

โตะแกรมรูปตัดผ่านปล่องอิฐ (x = 14.20, 1:250): ลมเข้าลานใต้ถุน -> โถง -> ลอยขึ้นตามปล่อง (stack)

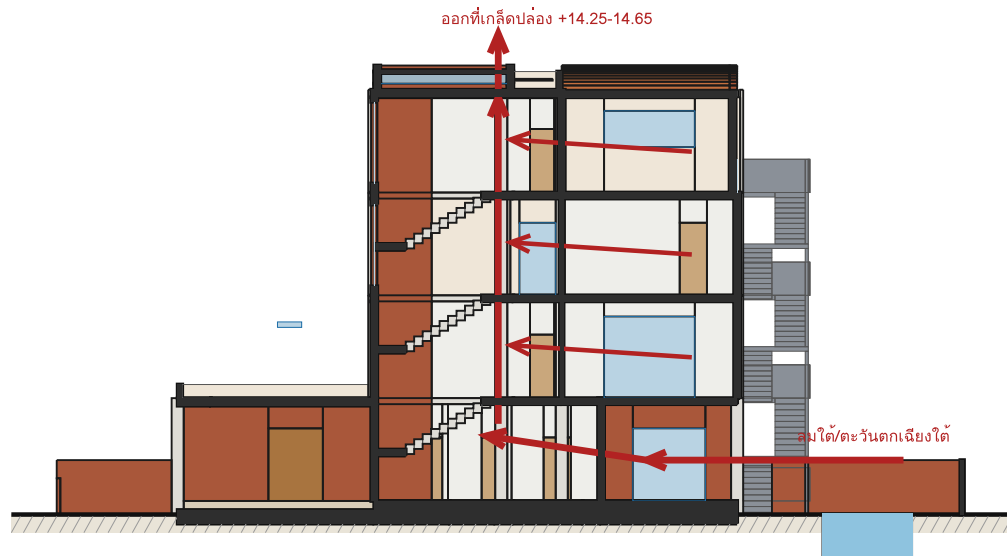

ลูกศร = เจตนารการออกแบบ (ลมปะจำกรุงเพทฯ ฤดูร้อน S/SW, ทวนำ NE) — ยังไม่ได้พิสูจน์ด้วย CFD/การจำลองความร้อน

Intrinsic — ข้อเท็จจริงที่ตรวจได้

หัวข้อ	ข้อเท็จจริงจากแหล่งที่เผยแพร่ (Architizer / Global Design News)
ผู้ออกแบบ	Chain10 Architecture & Interior Design Institute (หัวหน้าสถาปนิก Keng Fu Lo)
ที่ตั้ง / ประเภท	เกาะยว ใต้หวัน · โซว์รูมสุขุมวิท (ภาษาไทย) ไม่ใช่บ้านพักอาศัย
ลูกค้า	แบรนด์เซรามิกใต้หวันที่ก่อตั้งปี 1966 (แหล่งข้อมูลไม่ระบุชื่อ — เราไม่ระบุ)
แนวคิด	จำลองบรรยากาศการนำเสนอเซรามิก "1966": ทางเข้าโคมรูปเตาเผา ไฟส่องเป็นแสงเตา ความรู้สึก "ถ้าธรรมชาติ"
วัสดุ	ผนังลอยอิฐทนไฟ · ผนังฉาบ calce · พื้นกระเบื้องสีเส้นโค้ง · เซรามิกดินเผา ไฟส่องเป็นแสงเตา ความรู้สึก "ถ้าธรรมชาติ"
รายละเอียด	เซรามิก/ดินเผาคำนี้ ห้าปีในโมเดล · กระเบื้องตัว U ตะแกรง กระเบื้องเล็ก เป็นตัวต่อพื้นที่
รางวัล (ตามข่าว)	2026 International Architecture Honourable Mention (The Chicago Athenaeum) · ภาพ YHLAA

การตีความ -> แบบบ้านหลังนี้

องค์ประกอบ	การตีความของมร (ไม่ใช่คำอธิบายของสถาปนิก)
โดมเตาเผา	โดมอิฐ Ø5.60 ม. ยอด +6.25 = โถงก่อนขึ้น (โปรแกรม 24 ตร.ม.) ช่องแสง oculus Ø0.80 แทน "แสงเตา"
ปล่องเตา	หอบันได+ลิฟต์อิฐ 4.00 x 4.80 ม. สูง +14.85 ช่องแสงหลังคา + เกสรระบอบอากาศ (เจตนา stack effect)
อิฐทนไฟ / calce	ฐานอิฐชั้น 1 + ผนังปูนฉาบ calce สีดินอ่อน ชั้น 2-4 (ปูนขาวหายใจได้)
พื้นเส้นโค้ง	พื้นโมเสกเซรามิกกริเซิลแนวเส้นโค้ง ที่ลานใต้ถุน โถงกลาง โถงทางเข้า และในโถง
กระจุก U + ตะแกรง	ฉากกระจุกตัว U ที่ช่องเย็บทิศเหนือชั้น 3 · คริบดินเผา 115x80 @300 ทิศตะวันตก ชั้น 2-4
เก้าอี้	ห้องนั่งเล่นครอบครัวชั้น 4 ใต้หลังคาโค้งดินเผา หน้าต่างโค้ง "ปากเตา" ทิศใต้
ไม่นำมาใช้	ความมืด/ปิดพื้นที่แบบโซว์รูม — ชุด WELL R-L01, R-T06 และอากาศร้อนชื้นกรุงเทพ

รายงานข้อจำกัด (ตรงไปตรงมา)

- งานอ้างอิงเป็นงานตกแต่งภายในโซว์รูม ไม่ใช่บ้าน — มวลอาคาร โดม ปล่อง หลังคาโค้ง ทั้งหมดเป็นการตีความของเรา
- โปรแกรมซัดกัน: Master ชั้น 3 แต่ Closet 36 + Terrace 28 ชั้น 4 -> Master duplex มีบันไดส่วนตัว; Pantry ชั้น 3 ย้ายไปชั้น 2 ติดครัว (ตามที่เลือก)
- ยอดปล่องและยอดหลังคาโค้ง +14.85 ต่ำกว่า 15.00 ม. แต่ 0.15 ม. (ห้ามเพิ่มถึงน้ำท่วมบนหลังคา)
- CFA 1173.30 vs โปรแกรม 984.70 (+19.2%): ลานใต้ถุนศาลา 58.0 (โปรแกรม 35), ลอยเซาะกระเบื้องชั้น 3 80.9, สัญจร 239.1, บันไดหนีไฟไม้บัน
- ห้องเล็กกว่าโปรแกรมเกิน 10%: ครัว -34%, Powder -33%, Pantry -20%, ซักรีด -15%, ห้องนั่งเล่นครอบครัว -13%, BBQ -12%, Junior Suite -11% (A-11)
- บันไดหนีไฟภายนอก (ถ.55 ข้อ 27) — ต้องยืนยันว่าบ้านเดี่ยว 4 ชั้นต้องมีหรือไม่; ทางลาด 1:12 โรงรถ +0.15 -> โถง +0.45 ยาว 3.60 ม. ยังไม่ได้เขียน
- ความกว้างถนนไม่ทราบ — สมมติ 8.00 ม. (รัน 1/10 = 0.80 ม.; แบบรัน 4.00 ม.)
- ห้องสีกเกิน 4.20 ม. (ยกเว้นพร้อมเหตุผล): ครัวโชว์ ห้องอาหาร ห้องนั่งเล่น Master เฮียเตอร์; ห้องแม่บ้าน 2 ห้องเปิดด้านเดียว (ตะวันตก)
- ห้องที่ช่องปิดไม่ถึง 10% ไซ้พัดลมระบาย (ถ.39 ข้อ 6 วรรคสอง): 14 ห้อง (รายชื่อใน A-12)
- โดมอิฐ หลังคาโค้ง และปล่อง ต้องเป็นเปลือก ค.ส.ล. กรูอิฐ/ดินเผา + กั้นซีม; ห้องทำงานบนหลังคาโรงรถต้องมีคานาถ้ำแยง (เสา 2 ต้นในโรงรถ ระหว่างช่องจอด)
- ไม่ทราบผังเมืองรวม/ข้อบัญญัติท้องถิ่น (FAR/OSR/ความสูง) — ต้องตรวจสอบยื่น

แหล่งข้อมูลอ้างอิง Intrinsic

- architizer.com/projects/intrinsic (ลิงก์ที่ใช้ในหน้า)
- globaldesignnews.com — A Cave of Fire and Clay: Chain10 Intrinsic Showroom

ไม่ได้รับแบบจริงของโครงการ — ไม่มีขนาด/พื้นที่ของงานต้นแบบ ทุกมิติในชุดคือออกแบบใหม่

H3A DESIGN AND BUILD

X-UNIT Architecture Lab

โครงการ

WELL-KILN 30x30

Executive Luxury Villa

บ้านเดี่ยว 4 ชั้น ผ่านเกณฑ์

WELL for Residential (เจตนา)

ที่ดิน 30.00 x 30.00 ม. = 225 ตร.ว.
ถนนสาธารณะทิศเหนือ (สมมติ 8.00 ม.)

แนวคิด

ตีความจาก Intrinsic (Chain10):

โดมอิฐ "เตาเผา" Ø5.60 เป็นโถงก่อนรับ

+ ปล่องอิฐ (บันได+ลิฟต์) +14.85

+ หลังคาโค้งดินเผา + คริบดินเผา

ระดับ

±0.00 ถนน · F1 +0.45 · F2 +3.85
F3 +7.25 · F4 +10.65 · โดม +6.25

หลังคา +14.05 · parapet +14.65

ยอดปล่องหลังคาโค้ง +14.85

หมายเหตุ

- หน่วยเป็นมิลลิเมตร เว้นแต่ระบุ
- ระดับอ้างอิงถนนหน้าที่ดิน ±0.00
- ห้ามวัดขนาดจากแบบ ใช้ตัวเลขกำกับ

· แบบระดับ Design Development

ต้องให้สถาปนิกและวิศวกรผู้ได้รับ

ใบอนุญาตตรวจสอบและลงนาม

ก่อนยื่นขออนุญาต

ชื่อแผ่น

แนวคิด Intrinsic -> บ้านเตาเผา

+ รายงานข้อจำกัด

มาตราส่วน: ไม่มีมาตราส่วน

วันที่ 6 ต.ค. 2569 ฉบับ v1 / DD



ข้อ	รายการ	คำนวณแบบ	เกณฑ์	ผล
ข้อ 20	ห้องแบบบ้าน 2	11.31 ตร.ม. (คำนวณ 2.90)	≥ 8.00 ตร.ม.	ผ่าน
ข้อ 20	ห้องแบบบ้าน 1	9.75 ตร.ม. (คำนวณ 2.50)	≥ 8.00 ตร.ม.	ผ่าน
ข้อ 20	ห้องนอนแยก/ห้องอายุ	20.70 ตร.ม. (คำนวณ 4.50)	≥ 8.00 ตร.ม.	ผ่าน
ข้อ 20	ห้องนอน Junior Suite 2	20.16 ตร.ม. (คำนวณ 4.20)	≥ 8.00 ตร.ม.	ผ่าน
ข้อ 20	ห้องนอน Junior Suite 1	20.16 ตร.ม. (คำนวณ 4.20)	≥ 8.00 ตร.ม.	ผ่าน
ข้อ 20	ห้องนอน Master Suite	48.14 ตร.ม. (คำนวณ 5.80)	≥ 8.00 ตร.ม.	ผ่าน
ข้อ 22	ความสูงฝ้าเพดาน (FF 3.40 - พื้น 0.20 - มัฟฟาง	2.80 ม.	≥ 2.60 ม.	ผ่าน
ข้อ 22	โถงโถงลิฟต์ (ผนังโถง / ผนัง)	3.00 / 5.80 ม.	≥ 2.60 ม.	ผ่าน
ข้อ 22	ห้องนั่งเล่นหรือครัว (หลังคาโถง): ผนัง / ผนัง	3.15 / 4.00 ม.	≥ 2.60 ม.	ผ่าน
ข้อ 23	บันไดหลัก (ในโถงลิฟต์): ลูกดี / ลูกนอน	170 / 280 มม.	≤ 200 / ≥ 220	ผ่าน
ข้อ 23	บันไดหลัก (ในโถงลิฟต์): ความกว้าง	1000 มม.	≥ 800	ผ่าน
ข้อ 23	บันไดหลัก (ในโถงลิฟต์): ความลึก (ลิ้น)	1000 มม.	≥ ความกว้าง 1000	ผ่าน
ข้อ 23	บันไดวนด้าน Master ขึ้น 3-4: ลูกดี / ลูกนอน	170 / 280 มม.	≤ 200 / ≥ 220	ผ่าน
ข้อ 23	บันไดวนด้าน Master ขึ้น 3-4: ความกว้าง	1000 มม.	≥ 800	ผ่าน
ข้อ 23	บันไดวนด้าน Master ขึ้น 3-4: ความลึก (ลิ้น)	1000 มม.	≥ ความกว้าง 1000	ผ่าน
ข้อ 23	บันไดวนด้าน Master ขึ้น 3-4: ลูกดี / ลูกนอน	170 / 280 มม.	≤ 200 / ≥ 220	ผ่าน
ข้อ 23	บันไดวนด้าน Master ขึ้น 3-4: ความกว้าง	1100 มม.	≥ 800	ผ่าน
ข้อ 23	บันไดวนด้าน Master ขึ้น 3-4: ความลึก (ลิ้น)	1200 มม.	≥ ความกว้าง 1100	ผ่าน
ข้อ 23	ช่วงบันไดต่อเนื่อง	1.70 ม. (10 ขั้น)	≤ 3.00 ม.	ผ่าน
ข้อ 23	ระยะบันไดต่อเนื่องขึ้นบันได	≥ 3.03 ม.	≥ 1.90 ม.	ผ่าน
ข้อ 23	2R+T	620 มม.	600-650	ผ่าน
ข้อ 27	อาคาร 4 ชั้น: บันไดโถงลิฟต์ที่ไม่ใช่แบบลิฟต์	บันไดลิฟต์ลักษณะกว้าง 1.10 ม. ขึ้นๆ	ถ / กว้าง ≥ 0.80 / ขึ้น <	ผ่าน
ข้อ 27	อาคารเข้าบันไดลิฟต์ให้สูงขึ้น	ขั้น 2: ห้องลิฟต์แบบ-ประตูเปิด, ขึ้น	เข้าใช้งานพื้นที่ส่วนกลาง	ผ่าน
ข้อ 33	ตัววาง (บนประตูลิฟต์)	53.9% (ประตูลิฟต์ 414.91 ตร.ม.)	≥ 30%	ผ่าน
ข้อ 33	ตัววาง (ในลิฟต์ในอาคาร)	53.9%	≥ 30%	ผ่าน
ข้อ 50	ขนาดเปิดลิฟต์แบบลิฟต์ (อาคารสูง 14.65 ม.)	3.50 ม. (D05 F1 ครึ่งลิฟท์ (ครึ่งหน้าลิฟท์))	≥ 3.00 ม.	ผ่าน
ข้อ 50	ประตูลิฟต์แบบลิฟต์ในลิฟต์ ลิฟต์แบบลิฟต์	3.50 ม.	≥ 3.00 ม.	ผ่าน
ข้อ 50	ขนาดลิฟต์/ลิฟต์ในลิฟต์ ลิฟต์แบบลิฟต์	3.03 ม.	≥ 0.50 ม.	ผ่าน
ข้อ 50	ผนังอาคารลิฟต์แบบลิฟต์ (ตัวลิฟต์)	3.50 ม.	≥ 3.00 ม. (มีข้อเปิด. สูง	ผ่าน
รวมคะแนน	อาคาร (ลิฟต์/ลิฟต์) ลิฟต์แบบลิฟต์ (บนถนนลิฟต์ 8.00 ม.)	4.00 ม.	≥ 1/10 ความกว้างถนน = 0.8	ผ่าน

* ร่นแนวถนน: อาคารสูงไม่เกิน 15 ม. ถนนกว้าง 6-20 ม. ร่น 1/10 ของความกว้างถนน (ความกว้างถนนเป็นค่าสมมติ — ตรวจสอบกับข้อบัญญัติท้องถิ่น)

ชื่อ	ปีต่อหน้า	ปีถัดมา	ปีถัดมา	ปีถัดมา	รวม
ชื่อ 1	253.63	58.05	84.50	12.00	396.18
ชื่อ 2	286.26	15.66	-	12.00	301.92
ชื่อ 3	156.70	80.90	-	12.00	237.60
ชื่อ 4	170.32	67.28	-	12.00	237.60
รวม	866.91	221.89	84.50	48.00	1173.30
โปรแกรม					864.70
ส่วนต่าง					+188.60 (+19.2%)

* ชั้น 1 รวมโดมอิฐ 24.63 ตร.ม. (คิดเป็นวงกลม) · ลานใต้ถุน = ศาลาริมสระตามโปรแกรม (กึ่งภายนอก) · บันไดหนีไฟไม่รวม

รายการ	ค่า
พื้นที่ดิน	900.00 ตร.ม. (225 ตร.ว.)
พื้นที่อาคารดิน (รวมศาลา)	414.91 ตร.ม. (46 1/4%)
ที่ว่าง	53.9% (เกณฑ์ $\geq 30\%$)
FAR (GFA ใต้ถุน / พื้น)	0.96 : 1
ความสูงอาคาร	หลังคา 14.05 / parapet 14.65 / ยอดปล่องและหลังคาโดง 14.85 ม. (< 15.00)
ที่ดินขึ้นค่าตามโปรแกรม	113 ตร.ว. — ที่ดินขอ 225 ตร.ว.

วัสดุ	สูตร (บาท/ตร.ม.)	จำนวน
(ก) วัสดุงานเบรคฐาน	ปลั๊ก 866.91 x 22,000 + ที่กั้นเบรค 221.89 x 11,000 + ฉลตร 84.50 x 8,000	22.19
(ข) วัสดุงาน โคมูมิ	ปลั๊ก 30,000 + ที่กั้นเบรค 15,000 + ฉลตร 3,000	30.35
(ค) วัสดุเสาเข็ม (วิธีใช้ตามใบกำกับ)	GFA 1173.30 x 30,000	35.20
งานเสาอาคาร	เสา 42.0 ตร.ม. x 35,000 + PV 14.30 kWp x 45,000 + ภูมิทัศน์รั้ว 1.80 + ลิฟท์ 0.90 + ปันโดมไฟฟ้า 1.20 a.	6.01
ใบแทน ARCHSPACE	984.70 x 30,000 (ค่า 26.00-36.93 ล้าน)	29.54

อัตราแยก vs อัตราเดียว: (ก) 22.19 ล้าน ค่าวางบโปรแกรม; (ข) 30.35 ล้าน อยู่ในช่วง 26.00-36.93; (ค) 35.20 ล้าน และขอบบนของช่วง เพราะ GFA มากกว่าโปรแกรม 19.2%

รวมงานนอกอาคาร: (ข)+6.01 = 36.36 ล้าน · (ค)+6.01 = 41.21 ล้าน (เกินช่วงบนของโปรแกรม)

ยังไม่รวม: เสาเข็ม/ฐานราก (รอผลเจาะดิน), เพอร์นิเจอร์ลอยตัว, ภาษี/ค่าธรรมเนียม, ค่าออกแบบ

โครงการ

WELL-KILN 30x30

Executive Luxury Villa

บ้านเดี่ยว 4 ชั้น ผ่านเกณฑ์

WELL for Residential (เจตนา)

ที่ดิน 30.00 x 30.00 ม. = 225 ตร.ว.

ถนนสาธารณะทิศเหนือ (สมบัติ 8.00 ม.)

แนวคิด

ตีความจาก Intrinsic (Chain10):

โดมอิฐ "เตาเผา" Ø5.60 เป็นโรงต้อนรับ

 $+ \text{រង្វង់ស្រទាប់ខាងក្រៅ} + 14.85$

± หลัสดำโด้ดคิมแผา ± คฐำคิมแผ

ระดับ

$$\pm 0.00 \text{ มม.} \cdot F1 + 0.45 \cdot F2 + 3.85$$
$$F3 + 7.25 \cdot F4 + 10.65 \cdot \text{โคม} + 6.25$$

หลังคา +14.05 · parapet +14

หมายเหตุ:

- หน่วยเป็นมิลลิเมตร เว้นแต่ระบุ
ระดับอ้างอิงถนนหน้าที่ดิน ± 0.00
ห้ามวัดขนาดจากแบบ ใช้ตัวเลขกำกับ
แบบระดับ Design Development


ใบอนุญาตตรวจสอบและลงนาม
ก่อนยื่นขออนุญาต

ชื่อแผ่น

ผังบริเวณ + ตารางกฎหมาย
+ ประมาณราคา

มาตราส่วน 1:150

วันที่ 6 ต.ค. 2569 ฉบับ v1 / DD

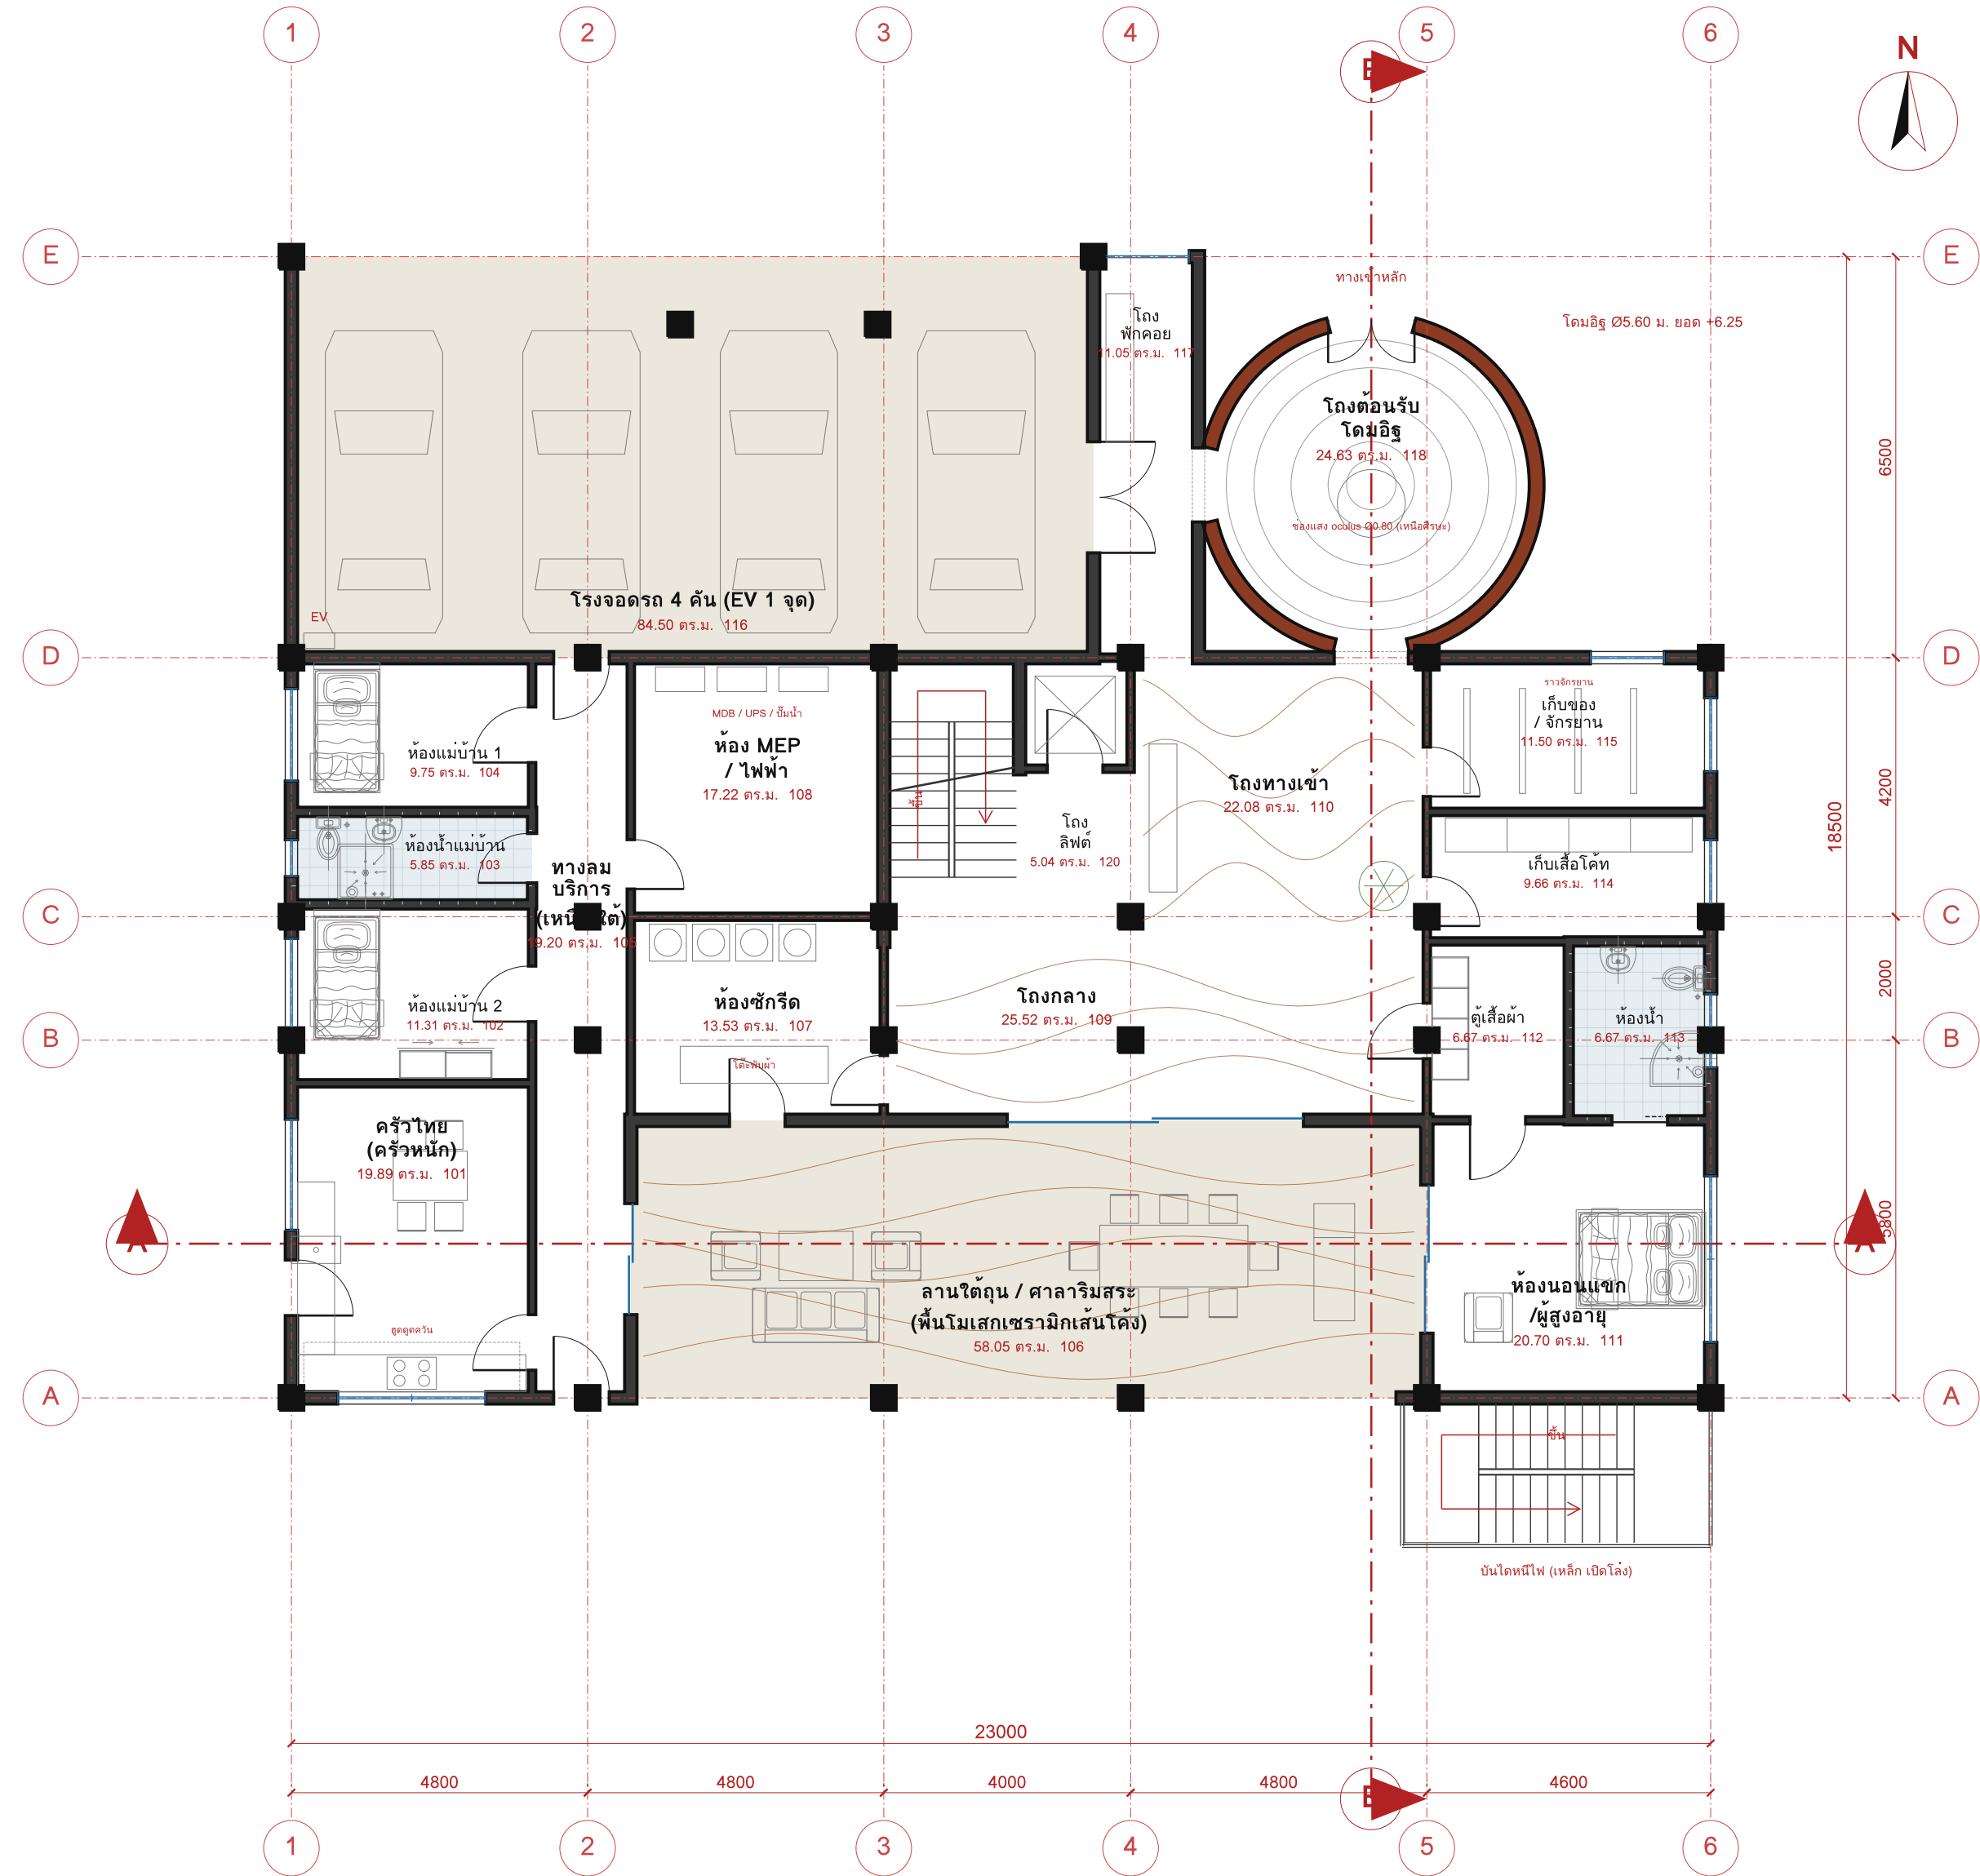

ผังพื้นชั้น 1 (FFL +0.45) 1:100

ตารางห้อง ชั้น 1

รหัส	ห้อง	ขนาด ม.	ตร.ม.	ประเภท
101	ครัวไทย (ครัวหลัก)	3.90 x 5.10	19.89	ห้องใช้งาน
102	ห้องแม่บ้าน 2	3.90 x 2.90	11.31	ห้องใช้งาน
103	ห้องน้ำแม่บ้าน	3.90 x 1.50	5.85	ห้องน้ำพิเศษ
104	ห้องแม่บ้าน 1	3.90 x 2.50	9.75	ห้องใช้งาน
105	ทางลมบริการ (เหนือ-ใต้)	1.60 x 12.00	19.20	สัญจร
106	ลานใต้ถุน / ศาลาริมสระ	12.90 x 4.50	58.05	พักผ่อน
107	ห้องซักผ้า	4.10 x 3.30	13.53	บริการ
108	ห้อง MEP / ไฟฟ้า / เครื่องขึ้นไฟ	4.10 x 4.20	17.22	บริการ
109	โถงกลาง	8.80 x 2.90	25.52	สัญจร
110	โถงทางเข้า (หลังโดม)	4.80 x 4.60	22.08	สัญจร
111	ห้องนอนแขก/ผู้สูงอายุ	4.60 x 4.50	20.70	ห้องใช้งาน
112	ตู้เสื้อผ้าห้องแขก	2.30 x 2.90	6.67	บริการ
113	ห้องน้ำห้องแขก	2.30 x 2.90	6.67	ห้องน้ำพิเศษ
114	ห้องเก็บเสื้อผ้า	4.60 x 2.10	9.66	บริการ
115	โรงจอดรถ 4 คัน	4.60 x 2.50	11.50	บริการ
116	โรงจอดรถ 4 คัน	13.00 x 6.50	84.50	จอดรถ
117	โถงพักคอย (จากโรงรถ)	1.70 x 6.50	11.05	สัญจร
118	โถงเชื่อมกับโดมอัฐ (เตาเผา)	Ø 5.60	24.63	โถง (วงกลม)
119	บันไดหลัก (ปล่องเตาเผา)	2.20 x 4.60	10.12	บันได
120	โถงลิฟต์	1.80 x 2.80	5.04	สัญจร
121	ลิฟต์บ้าน	1.80 x 1.80	3.24	ลิฟต์
122	บันไดหนีไฟภายนอก	5.00 x 2.40	12.00	บันไดหนีไฟ

ฐานชั้น 1	ตร.ม.
พื้นที่ใช้สอย (รวมโถง)	253.63
ที่ภายนอก	58.05
จอดรถ	84.50
รวม	396.18
บันไดหนีไฟภายนอก (ไม่รวม)	12.00

หมายเหตุ

- ทางเข้าหลักผ่านโดมอัฐ "เตาเผา" Ø5.60 ม. (พื้นโมเสกเซนเซอร์amikวงโค้ง ช่องแสง oculte) -> โถงทางเข้า -> โถงกลาง -> ปล่องบันได
- จากโรงจอดรถ -> โถง หรือ ทางลมบริการ (ประตูหลังโรงรถ); ทางลาด 1:12 ยาว 3.60 ม. ต้องเพิ่มบันไดแบบขยาย
- ทางลมบริการเหนือ-ใต้ กว้าง 1.60 ม. ประตูทั้งสองปลาย = ช่องลมผ่านตลอดความลึกอาคาร 12.00 ม.
- ลานใต้ถุน / ศาลาริมสระ 12.90 x 4.50 ม. ได้ชั้น 2 เปิดสู่สวนสระ (แทนศาลาริมสระแยกในโปรแกรม)
- ห้องนอนแขก (ผู้สูงอายุ) มุมตะวันตกเฉียงใต้ เช้าจากโถงกลางผ่านตู้เสื้อผ้า ใกล้ลิฟต์ ห้องน้ำบ้านเรือน
- จุดจอดรถไฟฟ้า (EV) 1 จุดในโรงรถ (WELL R-A09) · เส้า 2 ต้นในโรงรถรับห้องทำงานชั้น 2 (อยู่ระหว่างช่องจอดรถ)

H3A DESIGN AND BUILD

X-UNIT Architecture Lab

โครงการ

WELL-KILN 30x30

Executive Luxury Villa

บ้านเดี่ยว 4 ชั้น ผ่านเกณฑ์

WELL for Residential (เจดุนา)

ที่ดิน 30.00 x 30.00 ม. = 225 ตร.ว.
ถนนสาธารณะติดเหนือ (สมบัติ 8.00 ม.)

แนวคิด

ตีความจาก Intrinsic (Chain10):

โดมอัฐ "เตาเผา" Ø5.60 เป็นโถงต้อนรับ

+ ปล่องอัฐ (บันได+ลิฟต์) +14.85

+ หล่งคำโค้งดินเผา + คริบดินเผา

ระดับ

±0.00 ถนน · F1 +0.45 · F2 +3.85

F3 +7.25 · F4 +10.65 · โถง +6.25

หล่งคำ +14.05 · parapet +14.65

ยอดปล่องหลังคาโดม +14.85

หมายเหตุ

- หน่วยเป็นมิลลิเมตร เว้นแต่ระบุ
- ระดับอ้างอิงถนนหน้าที่ดิน ±0.00
- ห้ามวัดขนาดจากขอบ ใช้ตัวเลขกำกับ
- แบบระดับ Design Development
- ต้องให้สถาปนิกและวิศวกรผู้ได้รับใบอนุญาตตรวจสอบและลงนามก่อนยื่นขออนุญาต


ชื่อแผ่น

ผังพื้นชั้น 1

(FFL +0.45)

มาตราส่วน 1:100

วันที่ 6 ต.ค. 2569 ฉบับ v1 / DD

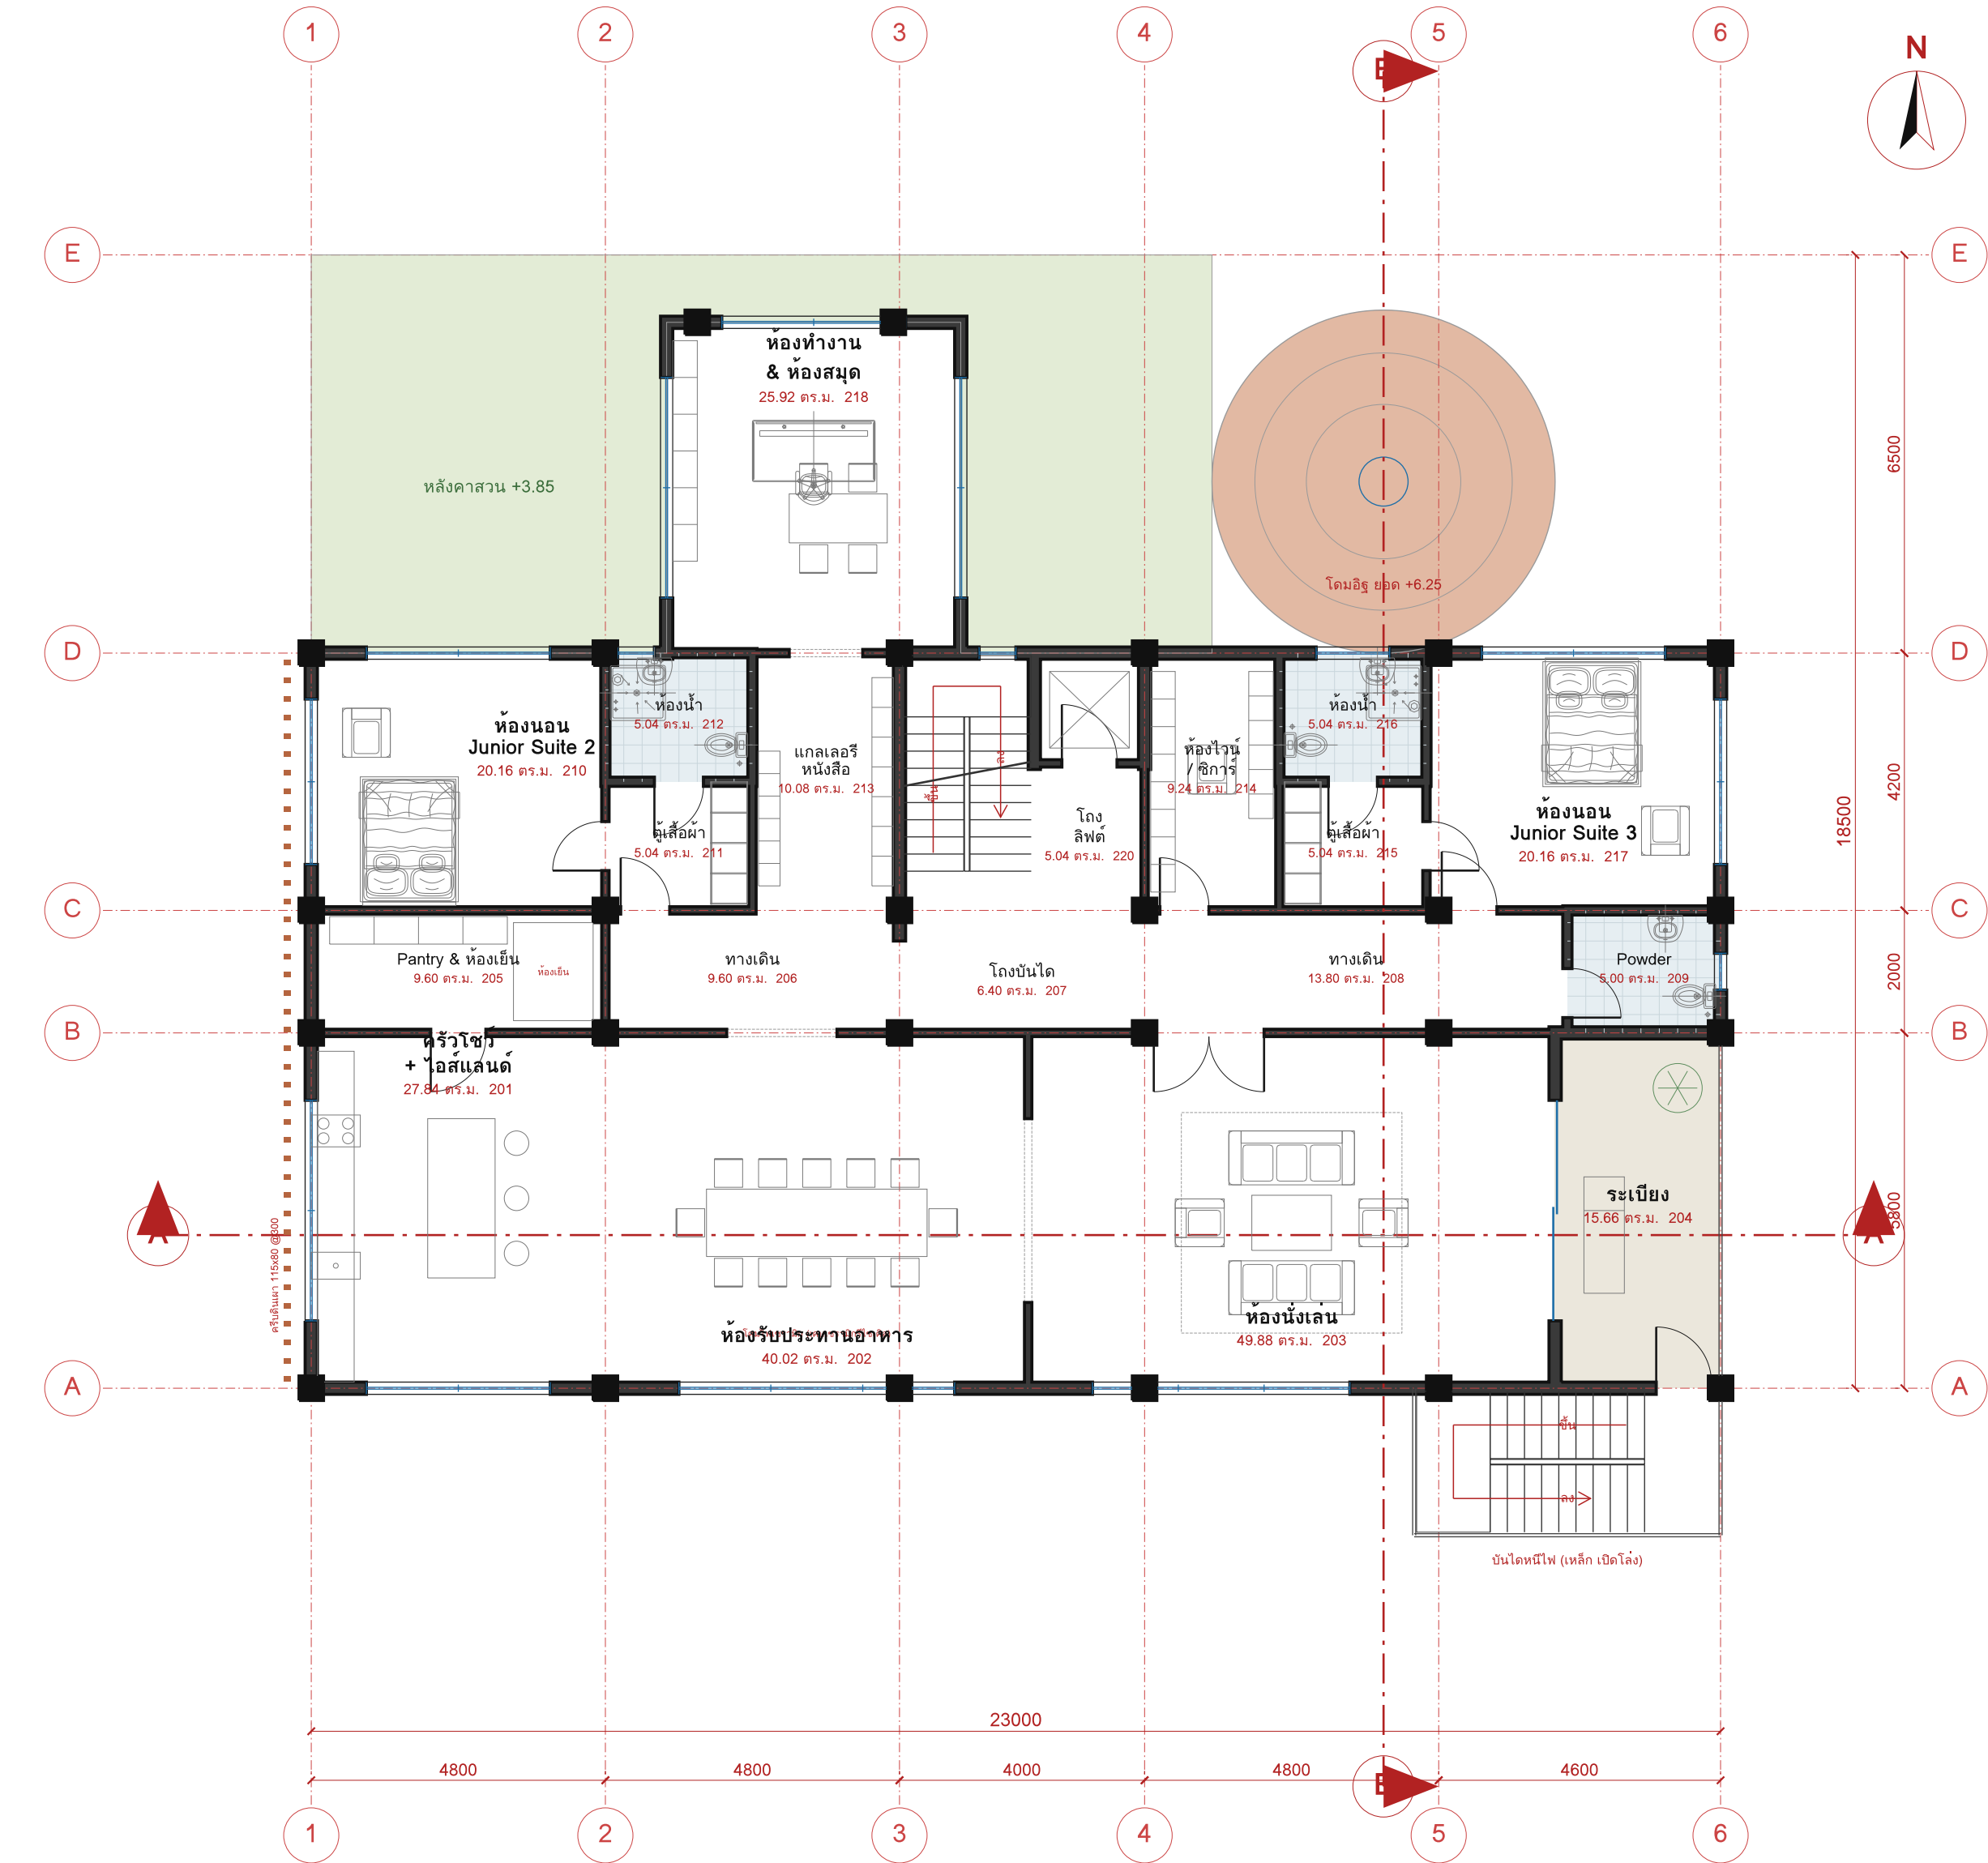

ผังพื้นชั้น 2 (FFL +3.85) 1:100



ตารางห้อง ชั้น 2

รหัส	ห้อง	ขนาด ม.	ตร.ม.	ประเภท
201	ครัว + ไอส์แลนด์	4.80 x 5.80	27.84	ห้องใช้งาน
202	ห้องรับประทานอาหาร	6.90 x 5.80	40.02	ห้องใช้งาน
203	โถงนั่งเล่น	8.60 x 5.80	49.88	ห้องใช้งาน
204	ระเบียงหน้าออกเฉียงใต้ ชั้น 2	2.70 x 5.80	15.66	ที่ภายนอก
205	Walk-in Pantry & ห้องเย็น	4.80 x 2.00	9.60	บริการ
206	ทางเดินชั้น 2 ตะวันตก	4.80 x 2.00	9.60	สัญจร
207	โถงบันได ชั้น 2	4.00 x 1.60	6.40	สัญจร
208	ทางเดินชั้น 2 ตะวันออก	6.90 x 2.00	13.80	สัญจร
209	ห้องน้ําแช่ (Powder)	2.50 x 2.00	5.00	ห้องโ้ง่อก
210	ห้องนอน Junior Suite 2	4.80 x 4.20	20.16	ห้องใช้งาน
211	ตู้เสื้อผ้า Junior Suite 2	2.40 x 2.10	5.04	บริการ
212	ห้องน้ํา Junior Suite 2	2.40 x 2.10	5.04	ห้องโ้ง่อก
213	แกลเลอรีหนังสือ	2.40 x 4.20	10.08	สัญจร
214	ห้องไวน์ / ศึกษาร	2.20 x 4.20	9.24	บริการ
215	ตู้เสื้อผ้า Junior Suite 3	2.40 x 2.10	5.04	บริการ
216	ห้องน้ํา Junior Suite 3	2.40 x 2.10	5.04	ห้องโ้ง่อก
217	ห้องนอน Junior Suite 3	4.80 x 4.20	20.16	ห้องใช้งาน
218	ห้องทำงาน & ห้องสมุด	4.80 x 5.40	25.92	ห้องใช้งาน
219	บันไดหลัก (ปล้องเตาเผา)	2.20 x 4.60	10.12	บันได
220	โถงลิฟต์ ชั้น 2	1.80 x 2.80	5.04	สัญจร
221	ลิฟต์บ้าน	1.80 x 1.80	3.24	ลิฟต์
222	บันไดหนีไฟภายนอก	5.00 x 2.40	12.00	บันไดหนีไฟ

รายชื่อ	ตร.ม.
พื้นที่ใช้สอย	286.26
ที่ภายนอก	15.66
จอดรถ	0.00
รวม	301.92
บันไดหนีไฟภายนอก (ไม่รวม)	12.00

หมายเหตุ

- ส่วนรวมพื้นที่ได้: ครัว + ห้องอาหาร 12 ที่นั่ง -> ห้องนั่งเล่น -> ระเบียงหน้าออกเฉียงใต้ (ทางเข้าบันไดหนีไฟ)
- Pantry ย้ายจากชั้น 3 (โปรแกรม) มาติดครัว (ตามข้อสังเกต) · ห้องไวน์/ศึกษารไม่มีหน้าต่าง (ตั้งใจ) ใช้พัฒนา/ระบบปรับอากาศแยก
- Junior Suite 2-3 ติดเหนือ หน้าต่าง 2 ด้าน; ห้องทำงาน & ห้องสมุด เป็นศาลาแบบหลังคาส่วนโรงรถ เข้าทางแกลเลอรีหนังสือ
- ครีบนินเผา 115 x 80 @300 ทิศตะวันตก ท่างผนัง 0.34-0.45 ม. บังแดดบ้านครัว/Pantry/Junior Suite 2

H3A DESIGN AND BUILD

X-UNIT Architecture Lab

โครงการ

WELL-KILN 30x30

Executive Luxury Villa

บ้านเดี่ยว 4 ชั้น ผ่านเกณฑ์

WELL for Residential (เจดนา)

ที่ดิน 30.00 x 30.00 ม. = 225 ตร.ว.
ถนนสาธารณะติดเหนือ (สมมติ 8.00 ม.)

แนวคิด

ตีความจาก Intrinsic (Chain10):

โคมอิฐ "เตาเผา" Ø5.60 เป็นโคมคอนกรีต

+ ปล้องอิฐ (บันได+ลิฟต์) +14.85

+ หลังคาโค้งดินเผา + ครีบนินเผา

ระดับ

±0.00 ถนน · F1 +0.45 · F2 +3.85
F3 +7.25 · F4 +10.65 · โดม +6.25
หลังคา +14.05 · parapet +14.65
ยอดปล้องหลังคาโดม +14.85

หมายเหตุ


- ผนังเป็นอิฐลิมสเตอร์ เว้นแต่ระบุ
- ระดับล่างลิ้งถนนพื้นที่ดิน ±0.00
- ห้ามรั่วซึมจากบน ใช้ตัวเสกกับ
- แบบระดับ Design Development
- ต้องให้สถาปนิกและวิศวกรผู้ได้รับใบอนุญาตตรวจสอบและลงนามก่อนยื่นขออนุญาต

ชื่อแผ่น

ผังพื้นชั้น 2
(FFL +3.85)

มาตราส่วน 1:100

วันที่ 6 ต.ค. 2569 ฉบับ v1 / DD

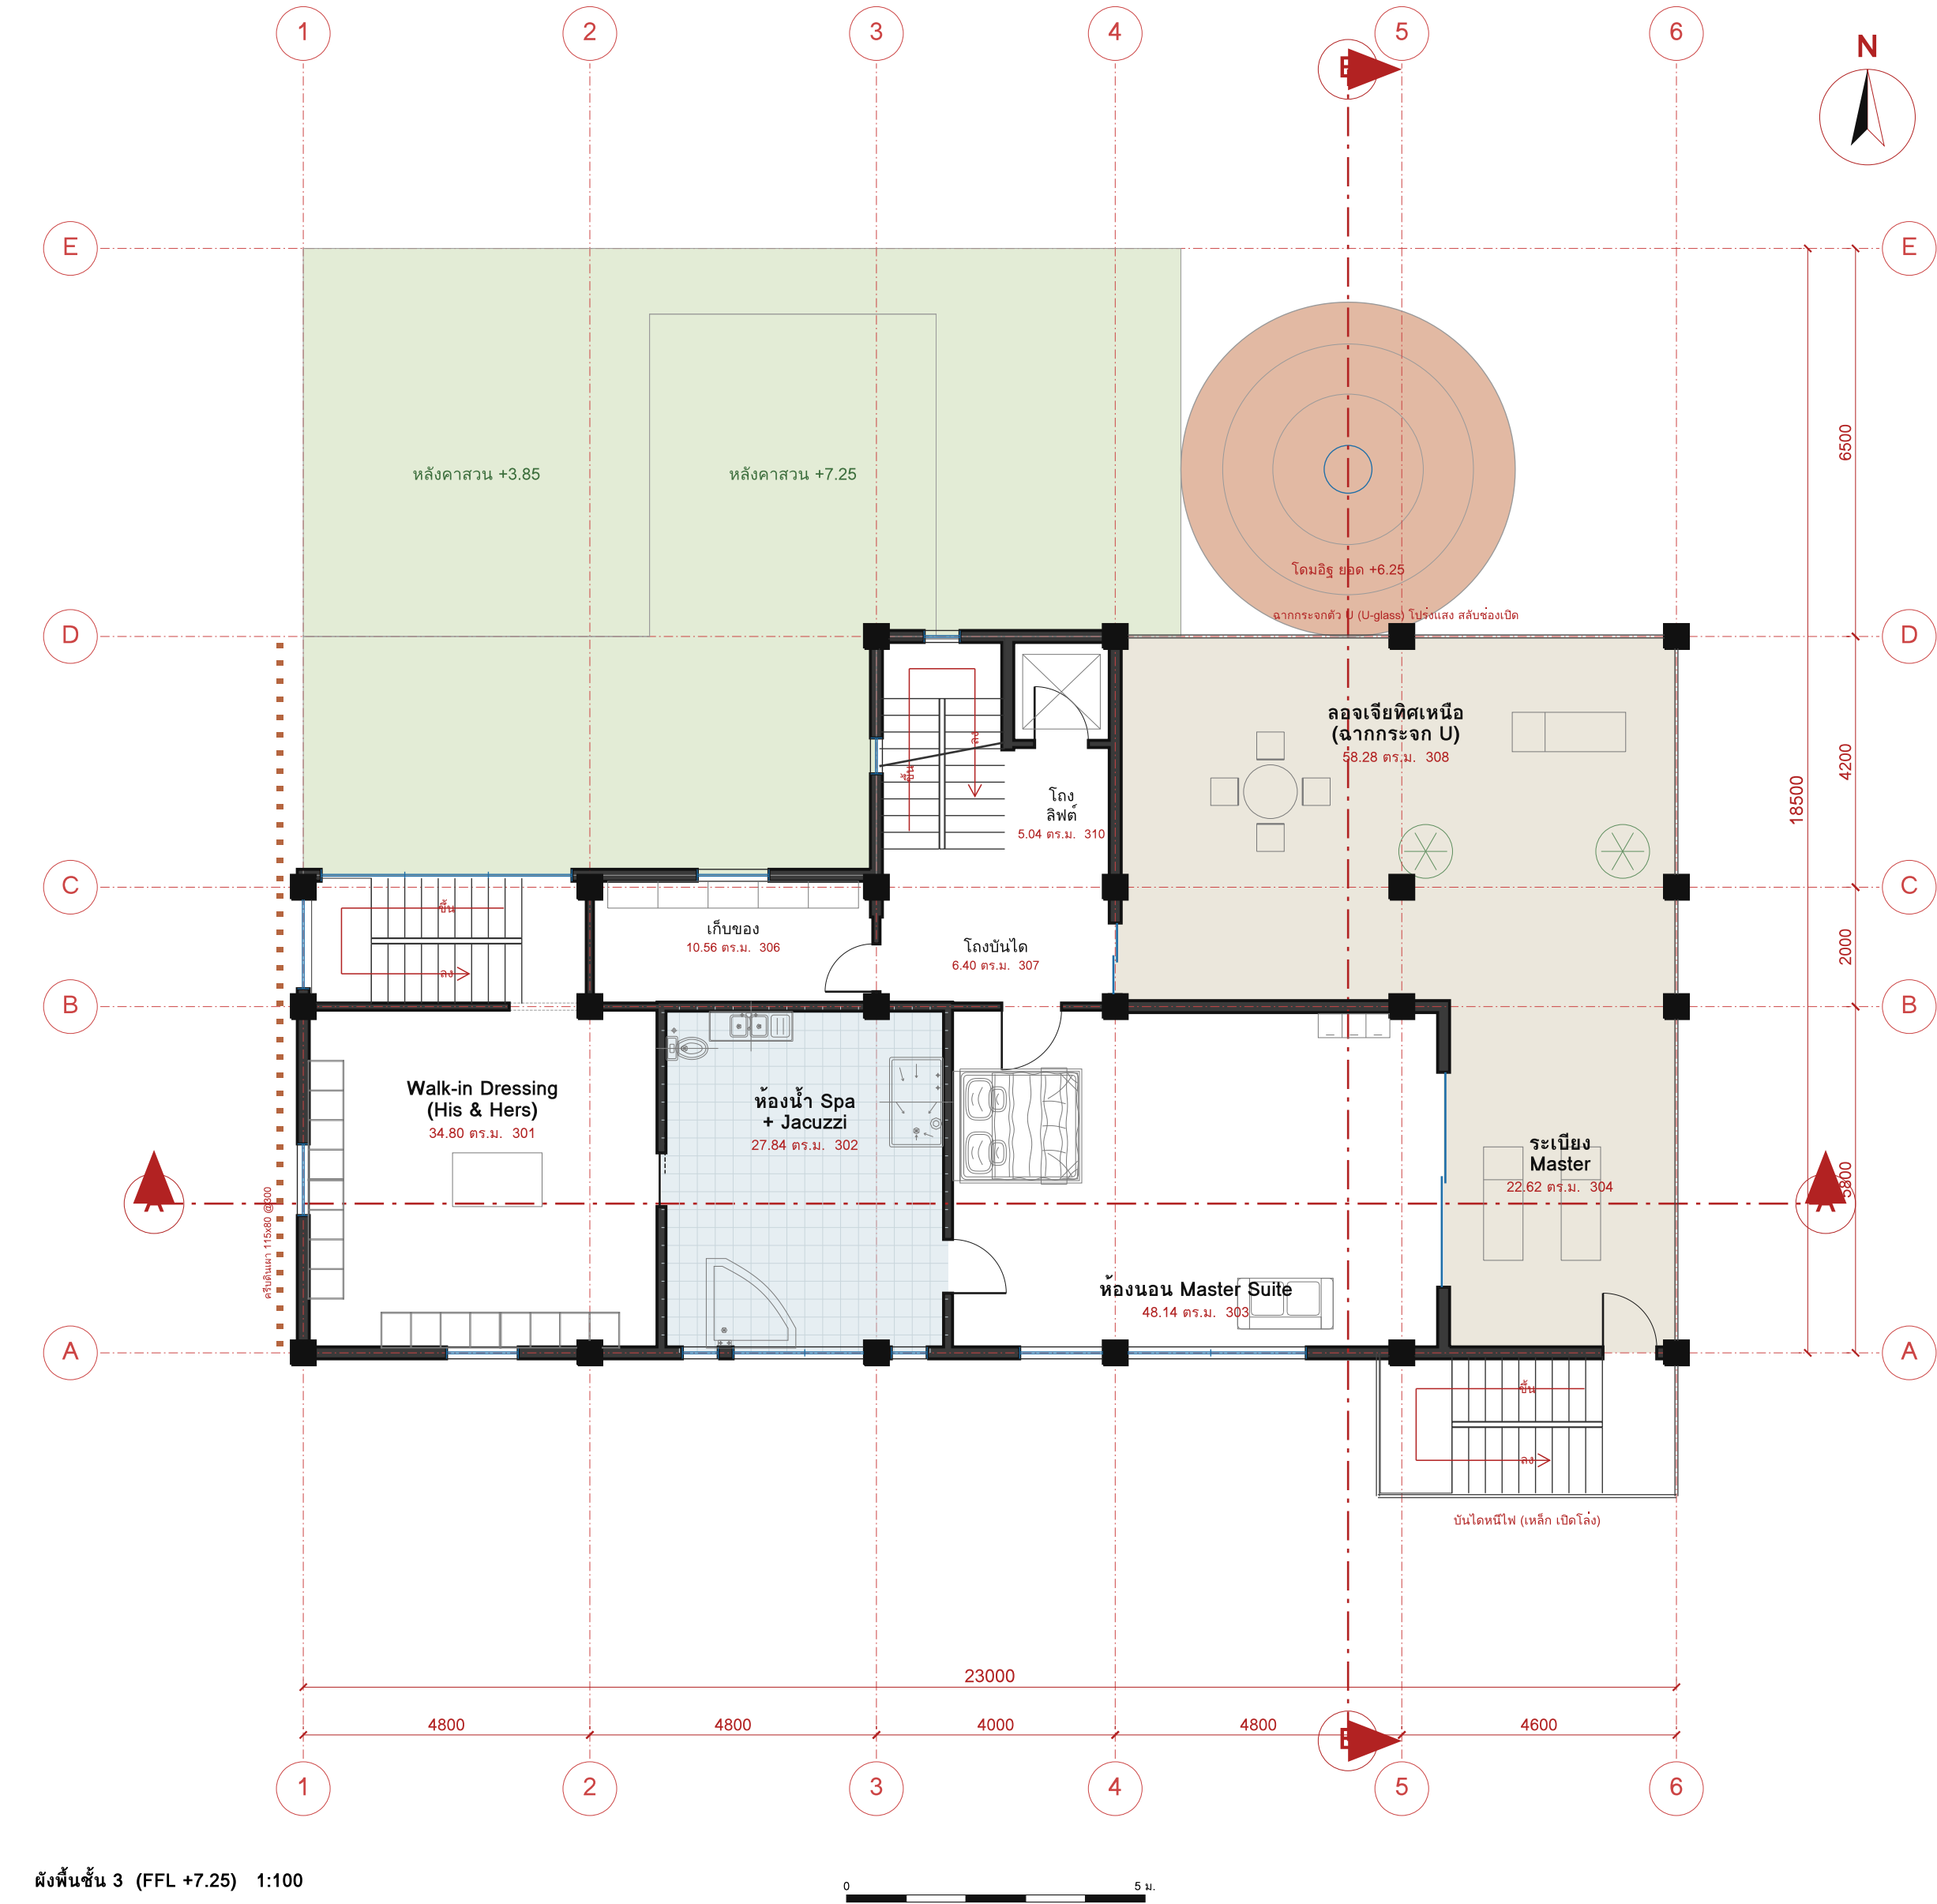

ผังพื้นชั้น 3 (FFL +7.25) 1:100

ตารางห้อง ชั้น 3

รหัส	ห้อง	ขนาด ม.	ตร.ม.	ประเภท
301	Walk-in Dressing (His & Hers)	6.00 x 5.80	34.80	บริการ
302	ห้องน้ำ Spa + Jacuzzi	4.80 x 5.80	27.84	ห้องน้ำ/สปา
303	ห้องนอน Master Suite	6.30 x 5.80	48.14	ห้องใช้งาน
304	ระเบียง Master ชั้น 3	3.90 x 5.80	22.62	ภายนอก
305	บันไดส่วนตัว Master	4.80 x 2.20	10.56	บันได
306	ห้องเก็บของชั้น 3	4.80 x 2.20	10.56	บริการ
307	โถงบันได ชั้น 3	4.00 x 1.60	6.40	สัญจร
308	โถงเจียหิดเหนือ (จากกระจก U)	9.40 x 6.20	58.28	ภายนอก
309	บันไดหลัก (บันไดเตาเผา)	2.20 x 4.60	10.12	บันได
310	โถงลิฟต์ ชั้น 3	1.80 x 2.90	5.04	สัญจร
311	ลิฟต์บ้าน	1.80 x 1.80	3.24	ลิฟต์
312	บันไดหนีไฟภายนอก	5.00 x 2.40	12.00	บันไดหนีไฟ

สรุปชั้น 3

	ตร.ม.
พื้นที่ปิดล้อม	156.70
ที่ภายนอก	80.90
จอดรถ	0.00
รวม	237.60
บันไดหนีไฟภายนอก (ไม่รวม)	12.00

หมายเหตุ

- ชั้นส่วนตัว Master: ห้องนอน -> ห้องน้ำ Spa + Jacuzzi -> Walk-in -> บันไดส่วนตัวขึ้นชั้น 4 (Master duplex ตามที่เลือก)
- โถงเจียหิดเหนือ 9.40 x 6.20 ม. จากกระจกตัว U ไปห้องแสงสว่างช่องเปิด (แสงนุ่ม + ความเป็นส่วนตัวจากถนน) ต่อถึงระเบียง Master
- ทางหนีไฟชั้น 3: โถงบันได -> โถงเจีย -> ระเบียง -> บันไดหนีไฟ
- หลังคาสวน +7.25 เหนือ Junior Suite 2 / แกลเลอรี / ห้องทำงาน

H3A DESIGN AND BUILD

X-UNIT Architecture Lab

โครงการ

WELL-KILN 30x30

Executive Luxury Villa

บ้านเดี่ยว 4 ชั้น ผ่านเกณฑ์

WELL for Residential (เจ็ดนา)

ที่ดิน 30.00 x 30.00 ม. = 225 ตร.ว.
ถนนสาธารณะติดเหนือ (สมบัติ 8.00 ม.)

แนวคิด

ตีความจาก Intrinsic (Chain10):

โคมอิฐ "เตาเผา" Ø5.60 เป็นโคมคอนกรีต

+ ปล้องอิฐ (บันได+ลิฟต์) +14.85

+ หลังคาโค้งดินเผา + ครีบนินนา

ระดับ

±0.00 ถนน · F1 +0.45 · F2 +3.85
F3 +7.25 · F4 +10.65 · โดม +6.25
หลังคา +14.05 · parapet +14.65
ยอดปล้องหลังคาโค้ง +14.85

หมายเหตุ

- หน่วยเป็นมิลลิเมตร เว้นแต่ระบุ
- ระดับอ้างอิงถนนหน้าที่ดิน ±0.00
- ห้ามวัดขนาดจากแบบ ใช้ตัวเลขกำกับ
- แบบระดับ Design Development
- ต้องให้สถาปนิกและวิศวกรผู้ได้รับใบอนุญาตตรวจสอบและลงนามก่อนยื่นขออนุญาต

ชื่อแผ่น

ผังพื้นชั้น 3
(FFL +7.25)

มาตราส่วน 1:100

วันที่ 6 ต.ค. 2569 ฉบับ v1 / DD



รหัส	ห้อง	ขนาด ม.	ตร.ม.	ประเภท
401	Master Walk-in Closet ชั้น 4	6.00 x 5.80	34.80	บริการ
402	ระเบียง Master (อาจฟ้า)	4.80 x 5.80	27.84	พักผ่อน
403	ห้องนั่งเล่นเคาน์เตอร์ (ห้องครัว)	5.40 x 5.80	31.32	ห้องใช้งาน
404	ระเบียง & BBQ (หลังคาถั่ว)	6.80 x 5.80	39.44	พักผ่อน
405	บันไดวนตัว Master	4.80 x 2.20	10.56	บันได
406	ห้องอุปกรณ์ AV / เก็บของ	4.80 x 2.20	10.56	บริการ
407	โถงบันได ชั้น 4	4.00 x 1.60	6.40	สุขุม
408	ทางเดินชั้น 4	6.90 x 2.00	13.80	สุขุม
409	ห้องนั่งเล่น 4	2.50 x 2.00	5.00	ห้องนั่ง/พักผ่อน
410	ห้องโถงมียอเนอร์	9.40 x 4.20	39.48	ห้องใช้งาน
411	บันไดหลัก (ต่อเนื่องมา)	2.20 x 4.60	10.12	บันได
412	โถงลิฟต์ ชั้น 4	1.80 x 2.80	5.04	สุขุม
413	ลิฟต์บ้าน	1.80 x 1.80	3.24	ลิฟต์
414	บันไดหนีไฟภายนอก	5.00 x 2.40	12.00	บันไดหนีไฟ

ลำดับที่ 4	ค.ร.บ.
พื้นที่ปิดล้อม	170.32
กังขายนอก	67.28
จ่อตรง	0.00
รวม	237.60
บันไดหนีไฟภายนอก (ไม่รวม)	12.00

ห้องเก็บของบนครัวมีทั้งตู้หัวเตียงนอน (สเปค +13.80 หอย +14.85) หน้าต่างโล่ง "ปากเตา" หิดไม้ ประดาน้ำชั้นสูงเรียบ BBQ
Master Walk-in Closet ต่อบันไดส่วนตัวและเรียบ Master (เปิดฟ้า (pergola)) ห้องนั่งเล่นมอระเบียง Master ม่านหน้าต่างสูง (ขอบล่าง 1.50 ม.)
ห้องโฮมเธียเตอร์หิดหนัง หน้าต่าง + ม่านหิน + ห้องน้ชา + 4 ปาลายทางเดิน
หลังคา +14.05 แฉงโซลาร์ 26 แผง = 14.30 KWp (พื้นที่จอดรถหลังคาดีและปลอด)

X-UNIT Architecture Lab

โครงการ

Executive Luxury Villa

WELL for Residential (๔

ที่ดิน 30.00 x 30.00 ม. = 225 ตร.ว.
ถนนสาธารณะทิศเหนือ (สมบัติ 8.00 ม.)

แนวคิด

ตีความจาก Intrinsic (Chain10):

โคมอิฐ "เตาเผา" Ø5.60 เป็นโถงต้อนรับ

+ ปล่องอิฐ (บันได+ลิฟต์) +14.85

+ หลังกาโคลงดินเผา + ครีbsdินเผา

ระดับ

±0.00 ถนน · F1 +0.45 · F2 +3.85
F3 +7.25 · F4 +10.65 · โดม +6.25
หลังคา +14.05 · parapet +14.65
ยอดปล่อง/หลังคาโค้ง +14.85

หมายเหตุ:


- หน่วยเป็นมิลลิเมตร เว้นแต่ระบุ
ระดับอ้างอิงบนหน้าที่ยื่น ± 0.00
ห้ามวัดขนาดจากแบบ ใช้ตัวเลขกำกับ
แบบระดับ Design Development
ต้องให้สถาปนิกและวิศวกรผู้ได้รับ
ใบอนุญาตตรวจสอบและลงนาม
ก่อนยื่นขออนุญาต

ชื่อแผ่น

ผังพื้นที่ชั้น 4
(FFL +10.65)

มาตราส่วน 1:100

วันที่ 6 ต.ค. 2569 ฉบับ v1 / DD

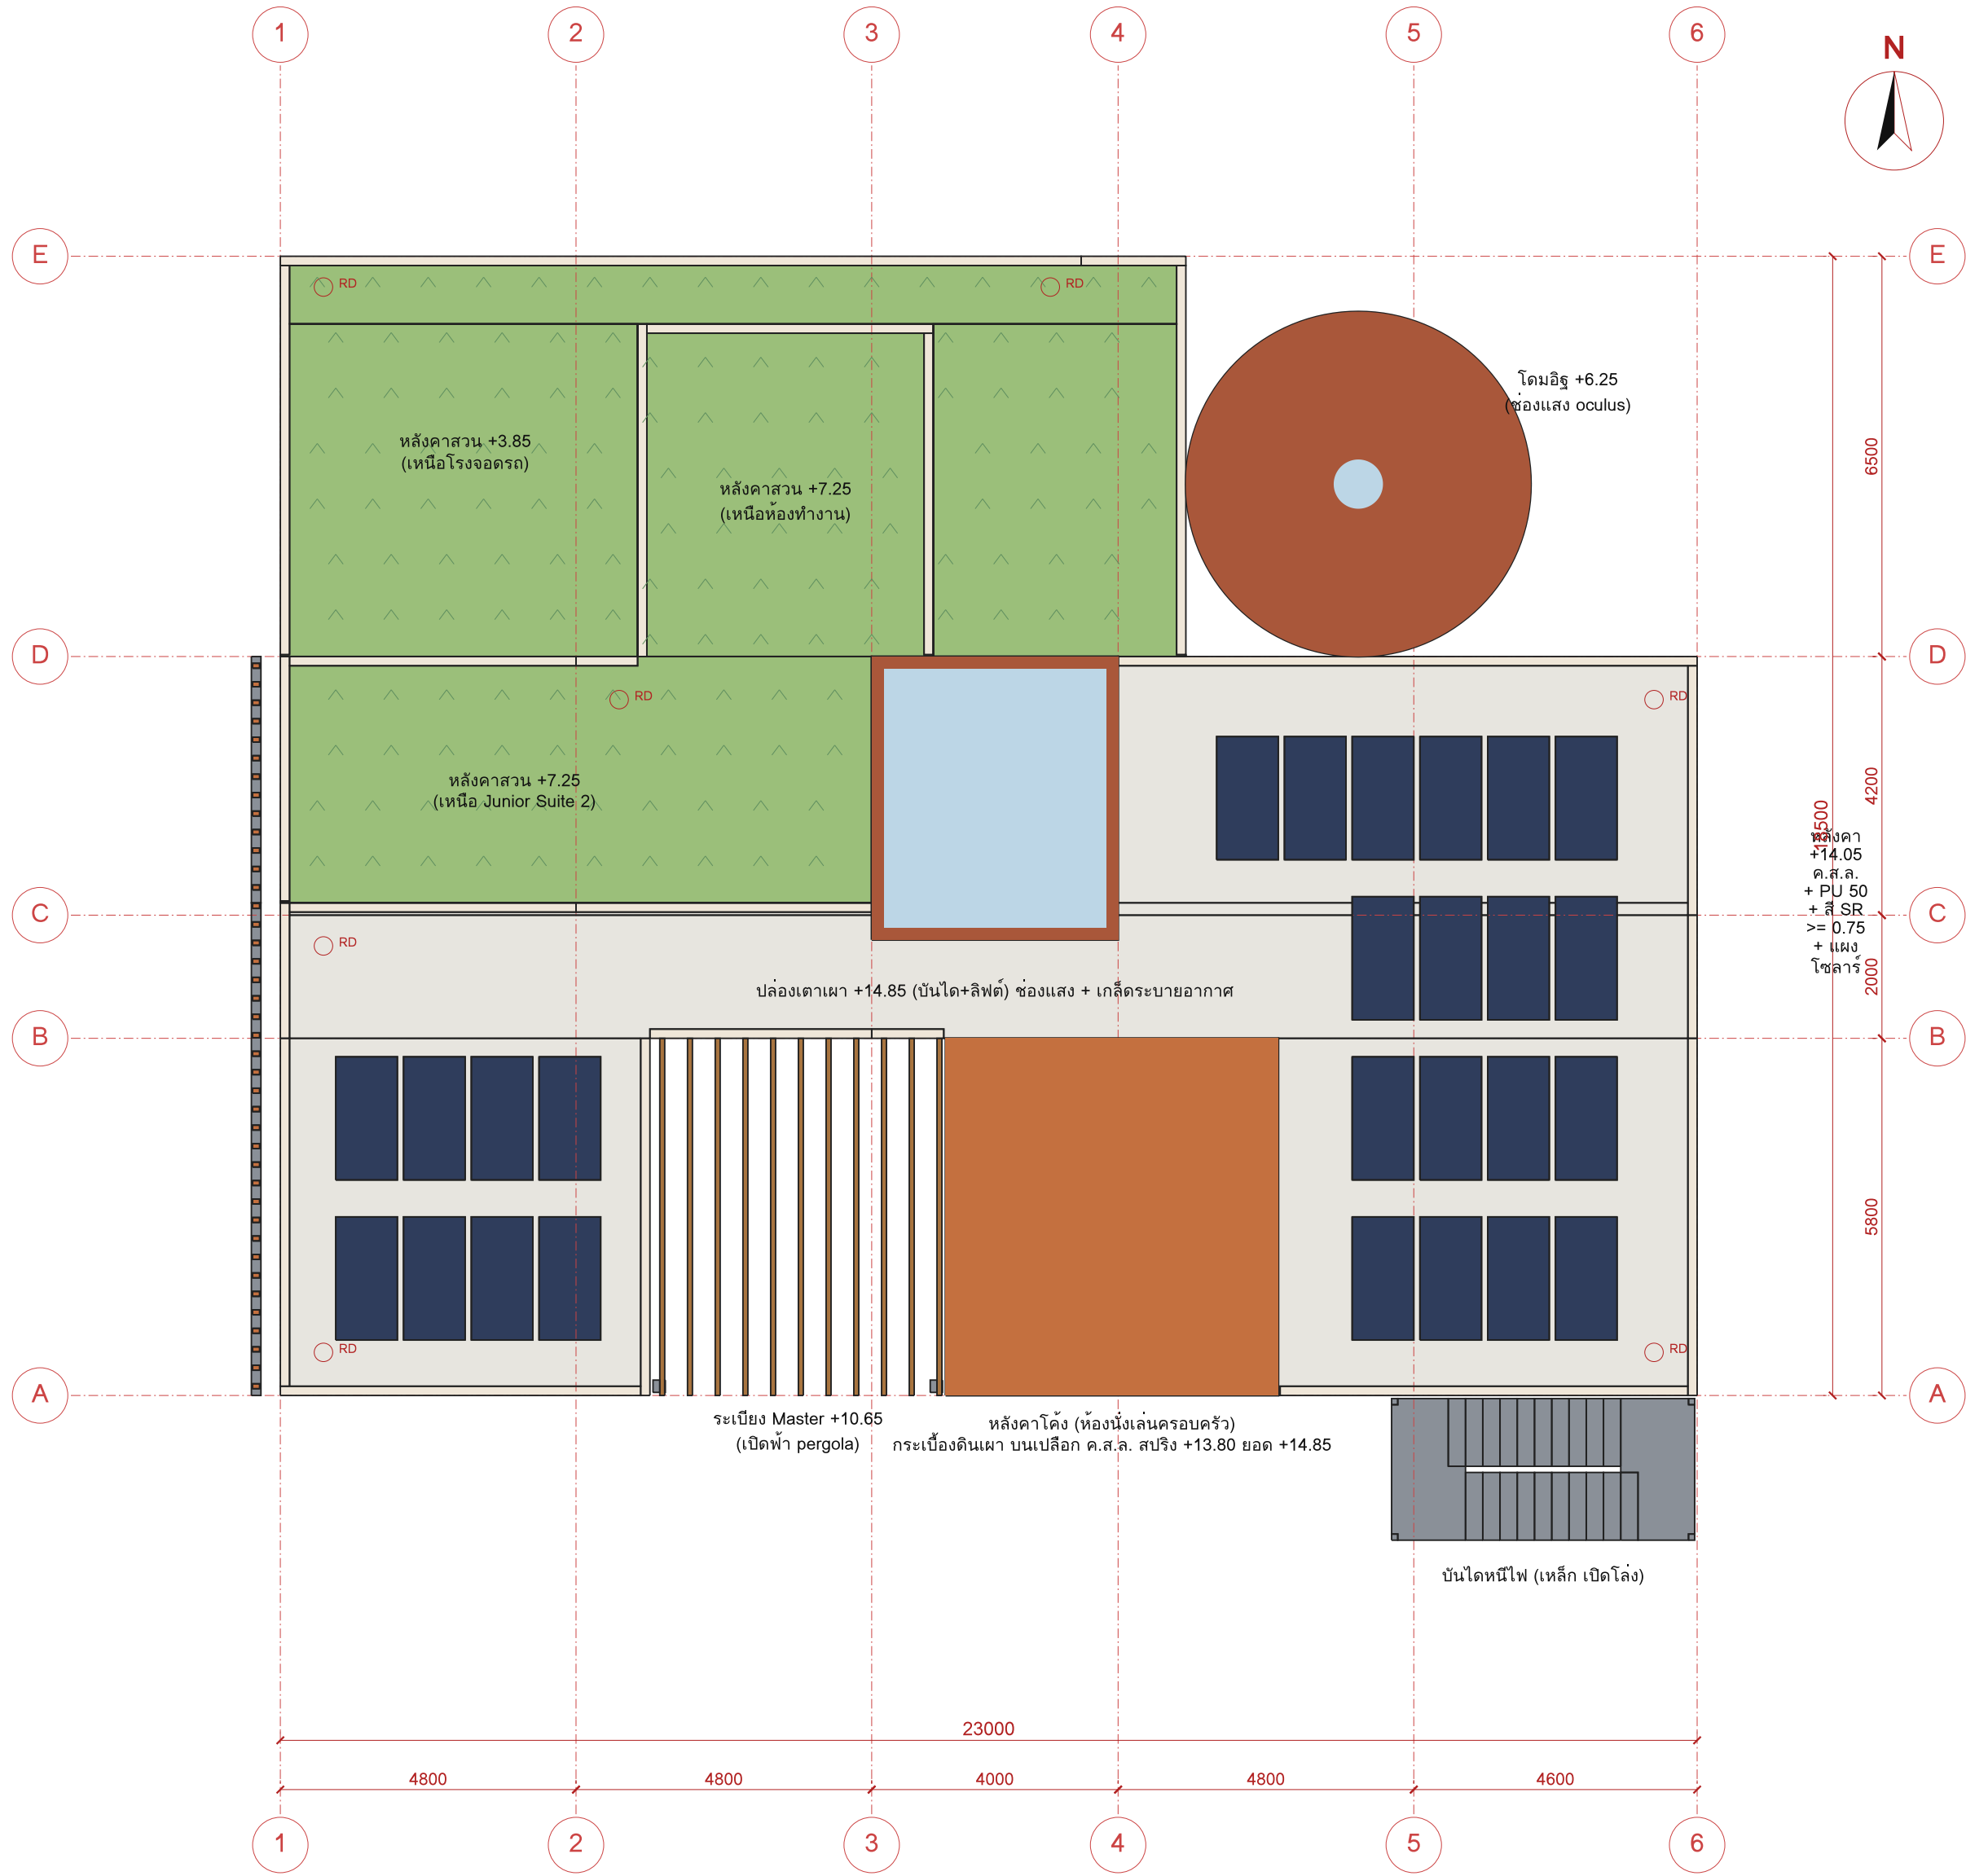

แปลนหลังคา ROOF PLAN 1:100



พื้นที่หลังคา

หลังคา	ค.ร.ม.
หลังคาสวน +3.85 / +7.25 (โอรุ, ห้องทำงาน, ชั้น 2)	133.85
หลังคาหลัก +14.05 (ค.ส.ล. ขาว SR)	178.44
หลังคาโค้งดินเผา (แป้น)	31.32
โอมอิฐ (แป้น)	24.63
รวม	368.34
สัดส่วนหลังคาเขียว	36%

น้ำฝน และพลังงาน

รายการ	ค่า
สมรณิกการองพทพ (ประมณ)	~1,500 มม./ปี
น้ำฝนเก็บได้ (น้ช้ง C=0.9, สวณ C=0.4)	321 ลบ.ม./ปี
กักเก็บน้ำฝนใต้ดิน 2.50 x 2.50 ม.	~12 ลบ.ม. (รดน้ำ/ซักโอร)
แปงโอราร 26 x 550 Wp	14.30 kWp ~ 17,900 kWh/ปี
ปล่องอิฐ +14.85	ช่องแสงหลังคา + เกล็ดระบายอากศ
โอมอิฐ +6.25	ช่องแสง oculus 20.80 ม.

ชั้นหลังคา

- หลังคาสวน: สึชดุมดิน + สันปลูก 150 มม. + แปงโอรอง + แปงระบายน้ำ 20 มม. + แปงกันรท + กันซึม 2 ชั้น + ค.ส.ล. ลาด 1:100
- หลังคาหลัก: สึชดุมแสง SR >= 0.75 + PU foam 50 มม. + กันซึม + ค.ส.ล. 200
- ระเบียง Master ชั้น 4 (เปิดฟ้า): พื้นไม้เทียมบนขนำค้ง + pergola; ระเบียง BBQ; หลังคา ค.ส.ล. ดุม
- หลังคาโค้ง: แปงคค ค.ส.ล. 120 + กันซึมหลว + กระเบียงดินเผา (ค้ SR ค้ก่วหลังคาขาว — ไม่นับใน R-T07)
- โอมอิฐ: แปงคค ค.ส.ล. + อิฐารุ + กันซึมโอมอิฐ + ขอบกันน้ำรอบ oculu
- Parapet สูง 0.60 ม.
- RD = หาระบายน้ำฝน ลระบายอากศาร -> ค้หน้าฝน
- พลังงาน PV ประมณ ~1,250 kWh/kWp/ปี — ค้องคำนวณจรวมณวปล่องหลังคาโค้งpergola

H3A DESIGN AND BUILD

X-UNIT Architecture Lab

โครงการ

WELL-KILN 30x30

Executive Luxury Villa
บ้านเดี่ยว 4 ชั้น ผ่านเกณฑ์
WELL for Residential (เจดณา)

ที่ดิน 30.00 x 30.00 ม. = 225 ตร.ว.
ถนนสาธารณะติดเหนือ (สมบัติ 8.00 ม.)

แนวคิด

ส้ค้จาก Intrinsic (Chain10):
โอมอิฐ "เตาเผา" Ø5.60 เป็นโอรค้ันรับ
+ ปล่องอิฐ (บันได+ลิฟต์) +14.85
+ หลังคาโค้งดินเผา + ครับดินเผา

ระดับ

±0.00 ถนน · F1 +0.45 · F2 +3.85
F3 +7.25 · F4 +10.65 · โอม +6.25
หลังคา +14.05 · parapet +14.65
ยอดปล่องหลังคาโค้ง +14.85

หมายเหตุ

- หน้เป็นมิลลิเมตร เว้นแต่ระบุ
- ระบ้ค้ถึงถนนหน้าที่ดิน ±0.00
- หารัค้ค้ดจากแบบ ใช้ตัวเลขกำกับ
- แบบระบ้ Design Development
- ค้องให้สถาปนิกและวิศวกรผู้ได้รับ
- ใบอนุญาตตรวจสอบและลงนาม
- ก่อนยื่นขออนุญาต


ชื่อแผ่น

แปลนหลังคา

มาตราส่วน 1:100

วันที่ 6 ค.ศ. 2569 ฉบับ v1 / DD

รูปด้านทิศใต้ (สวน/สระ — หน้าต่างโค้งปากเตา) 1:100

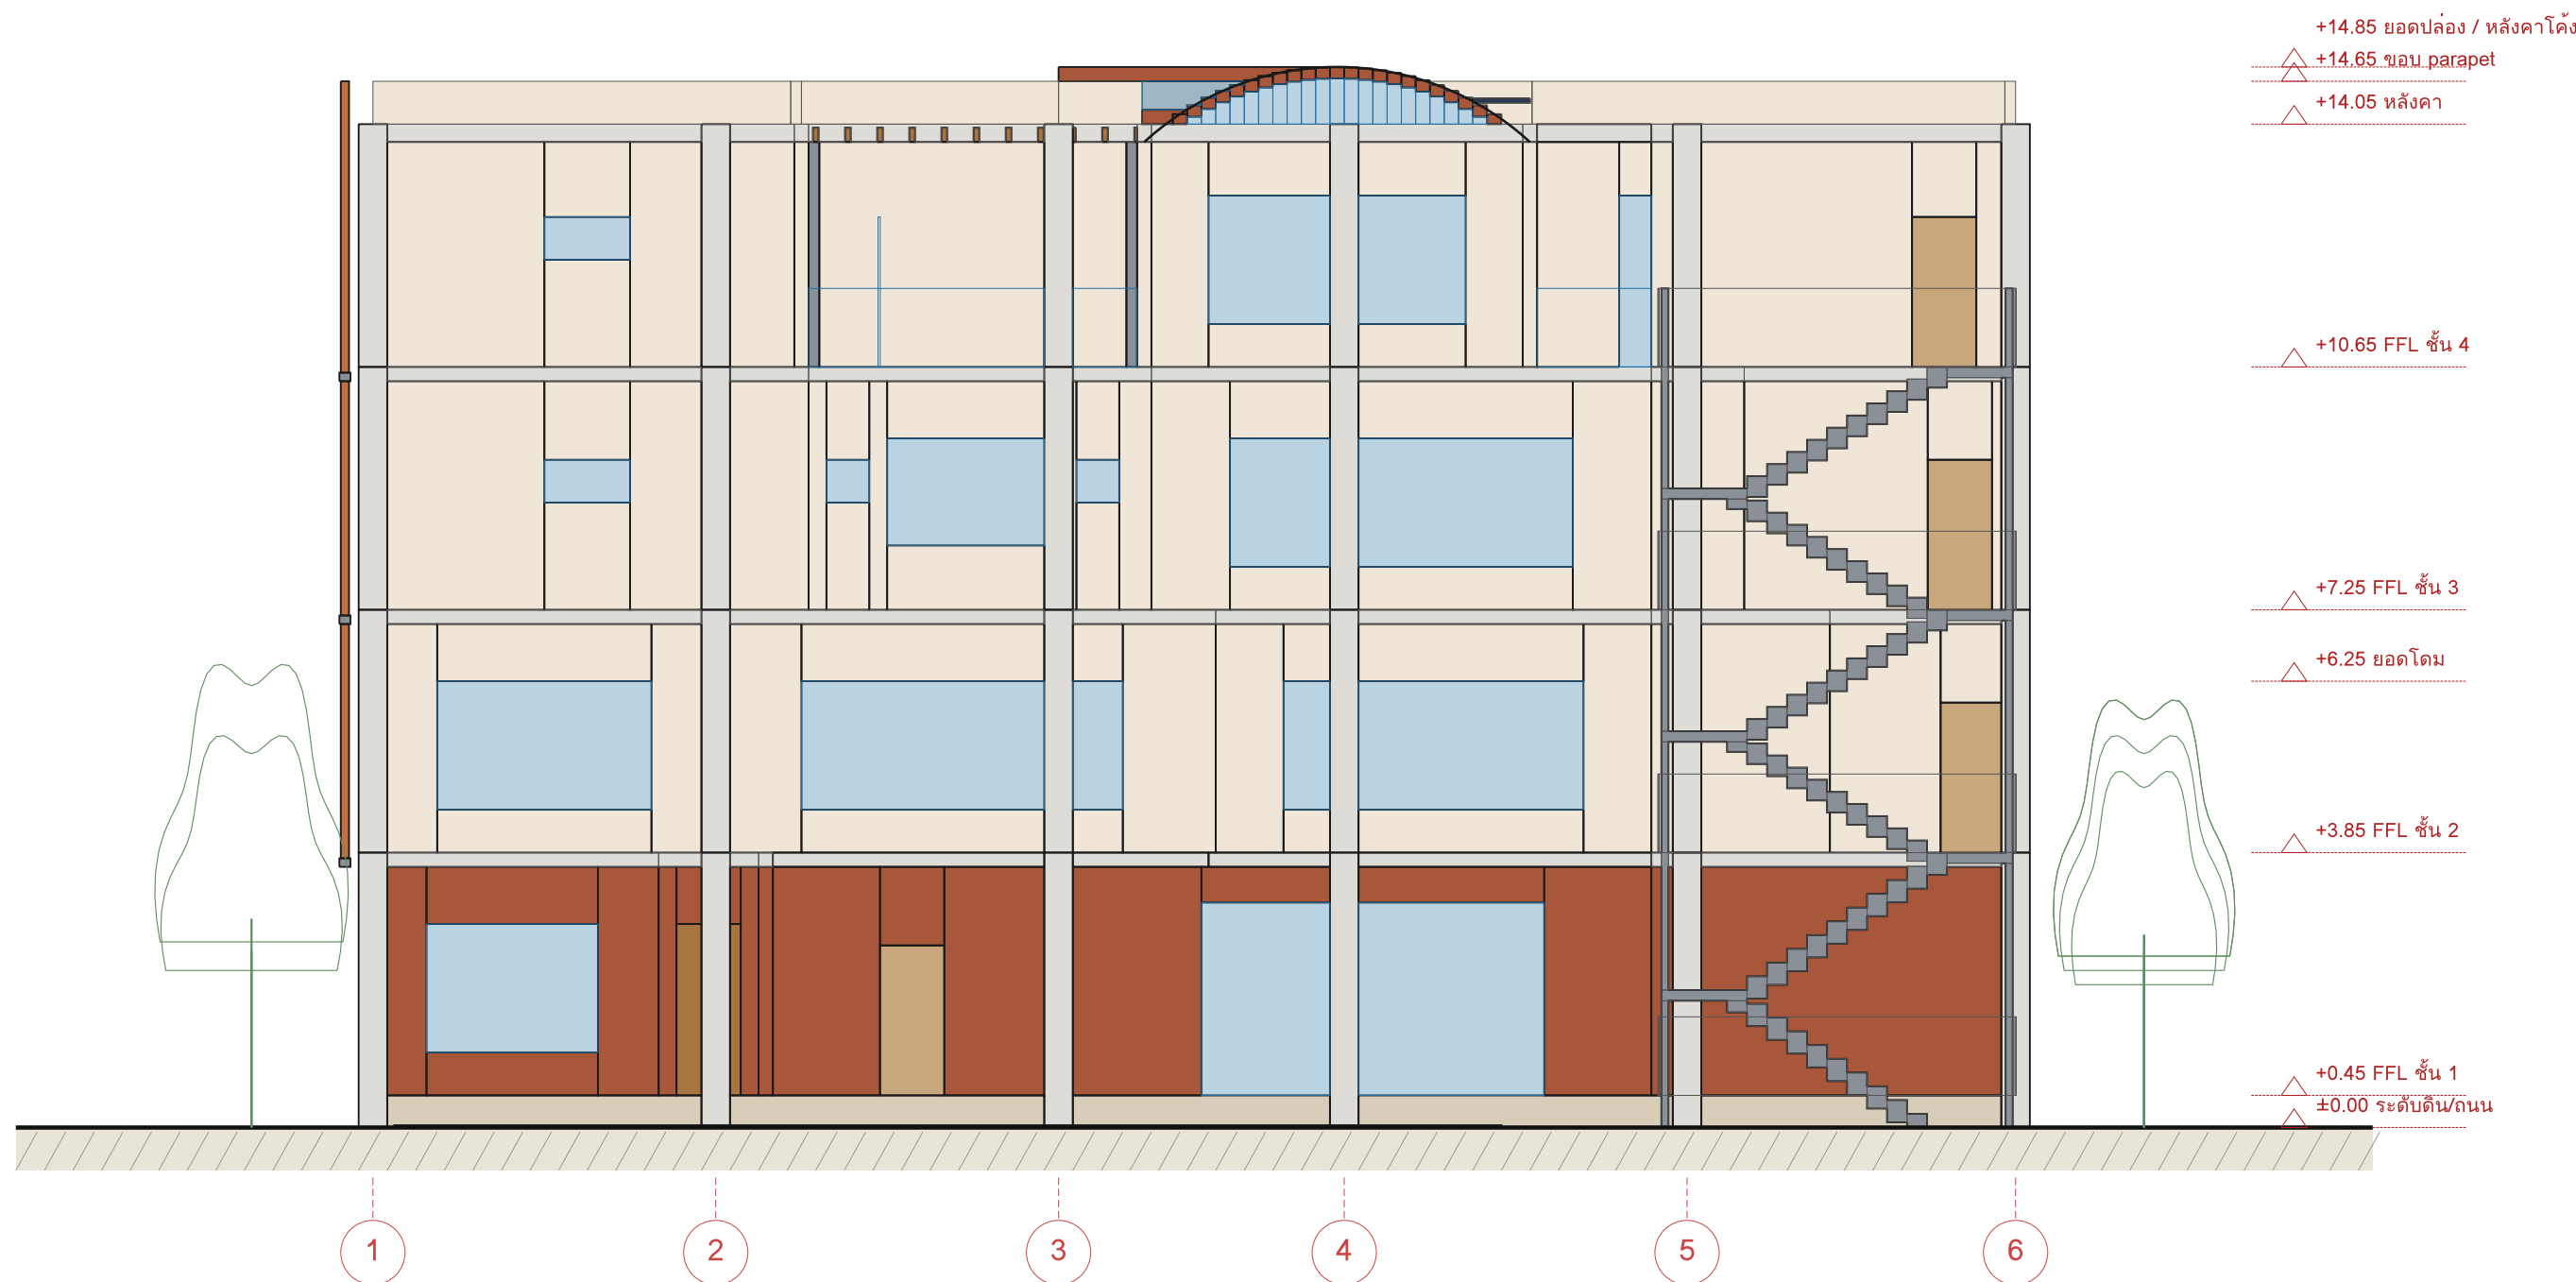

รูปด้านทิศเหนือ (ถนน — โดมอิฐ / ปล่องอิฐ) 1:100



- ชั้น 1: ฐานอิฐฉาบผิวทาสี (firebrick) สีแดงเข้ม
- ชั้น 2-4: ปูนฉาบ calce (ปูนขาว) สีนวล
- คม + ปลอก: อิฐโขนาน บนเปลือก คมอ่อน
- หลังคาโค้ง: กระเบื้องดินเผา + ชุมอิฐ สลับหน้าท้าวโค้งกระชอก
- ผนังหน้าคา 115 x 80 (x) 300 บนโครงเหล็กกลาขาว (สีสดระยัด)
- ลงเฉยชั้น 3: ฉากกระเบื้องตัว U โปร่งแสง
- กระเบื้อง Low-E laminated กระเบื้องเคลือบสีเทาเข้ม + ราวกระจก 1.10 ม.
- ปันโดใหม่ใต้: เหล็กกลาขาวชุบสี ราว 1.10 ม.

0 5 μm

H3A DESIGN AND BUILD

X-UNIT Architecture Lab

โครงการ

WELL-KILN 30x30

Executive Luxury Villa
บ้านเดี่ยว 4 ชั้น ผ่านเกณฑ์
WELL for Residential (เจตนา)

ที่ดิน 30.00 x 30.00 ม. = 225 ตร.ว.
ถนนสาธารณะทิศเหนือ (สมมติ 8.00 ม.)

แนวคิด

ตีความจาก Intrinsic (Chain10):

โคมอิฐ "เตาเผา" Ø5.60 เป็นโถงตันรับ
 + ปล่องอิฐ (บันได+ลิฟต์) +14.85
 + หลังคาโค้งดินเผา + ครีบทินเผา

ระดับ

±0.00 ถนน · F1 +0.45 · F2 +3.85
F3 +7.25 · F4 +10.65 · โดม +6.25
หลังคา +14.05 · parapet +14.65
ยอดปล่อง/หลังคาโดง +14.85

หมายเหตุ

- หน่วยเป็นมิลลิเมตร เว้นแต่ระบุ
- ระบุอ้างอิงถนนหน้าที่ดิน ±0.00
- ห้ามวัดขนาดจากแบบ ใช้ตัวเลขกำกับ
- แบบระดับ Design Development
ต้องให้สถาปนิกและวิศวกรผู้ได้รับ
ใบอนุญาตตรวจสอบและลงนาม
ก่อนยื่นขออนุญาต

ชื่อแผ่น

รูปด้านทิศใต้
+ รูปด้านทิศเหนือ

มาตราส่วน 1:100

วันที่ 6 ต.ค. 2569 ฉบับ v1 / DD

รูปด้านทิศตะวันตก (ครีبدินเผา) 1:100



- ชั้น 1: ฐานอิฐฉาบสีทึบไฟ (firebrick) สีแดงเข้ม
- ชั้น 2-4: ปูนฉาบ calce (ปูนขาว) สีนิลอม
- โคม + ปลอก: อิฐโชว์แนว บนเปลือก ค.ส.ล.
- หลังคาโค้ง: กระเบื้องดินเผา + ฐานอิฐ ขอบบนทำดอกรอก
- ครอบดินเผา 115 x 80 @300 บนโครงสร้างภายใน (ศิลปะรัตนโก)
- ลงเจียขึ้นชั้น 3: ฉากกระจกด้าน U ไปริมฝั่ง
- กระเบื้อง Low-E laminated กระจกสีนิลเข้มสีฟ้าเข้ม + ราวกระจก 1.10 ม.
- บันไดหนีไฟ: เหล็กกล้าชุบสังกะสี ราว 1.10 ม.

X-UNIT Architecture Lab

โครงการ

WELL-KILN 30x30

Executive Luxury Villa
บ้านเดี่ยว 4 ชั้น ผ่านเกณฑ์
WELL for Residential (เจตนา)

ที่ดิน 30.00 x 30.00 ม. = 225 ตร.ว.
ถนนสาธารณะทิศเหนือ (สมบัติ 8.00 ม.)

แนวคิด

+ ปล่องอิฐ (บันได+ลิฟต์) +14.85
 + หลังคาโค้งดินเผา + ครัวดินเผา

ระดับ

±0.00 ถนน · F1 +0.45 · F2 +3.85
F3 +7.25 · F4 +10.65 โดม +6.25
หลังคา +14.05 · parapet +14.65
ยอดปล่อง/หลังคาโค้ง +14.85

หมายเหตุ

- หน่วยเป็นมิลลิเมตร เว้นแต่ระบุ
ระดับอ้างอิงถนนหน้าที่ดิน ± 0.00
ห้ามวัดขนาดจากแบบ ใช้ตัวเลขกำกับ
แบบระดับ Design Development
ต้องให้สถาปนิกและวิศวกรผู้ได้รับ
ใบอนุญาตตรวจสอบและลงนาม
ก่อนยื่นขออนุญาต


ชื่อแผ่น

รูปด้านทิศตะวันออก
+ รูปด้านทิศตะวันตก

มาตราส่วน 1:100

วันที่ 6 ต.ค. 2569 ฉบับ v1 / DD

รูปตัด A-A (ตัดแนวตะวันออก-ตะวันตก ผ่านครัวไทย-ลานใต้ถุน-ห้องแขก / ครัว-ห้องอาหาร-ห้องนั่งเล่น / Walk-in-Spa-Master / Closet-ระเบียง-ห้องนั่งเล่นหลังคาโค้ง-BBQ มองไปทิศเหนือ) 1:100

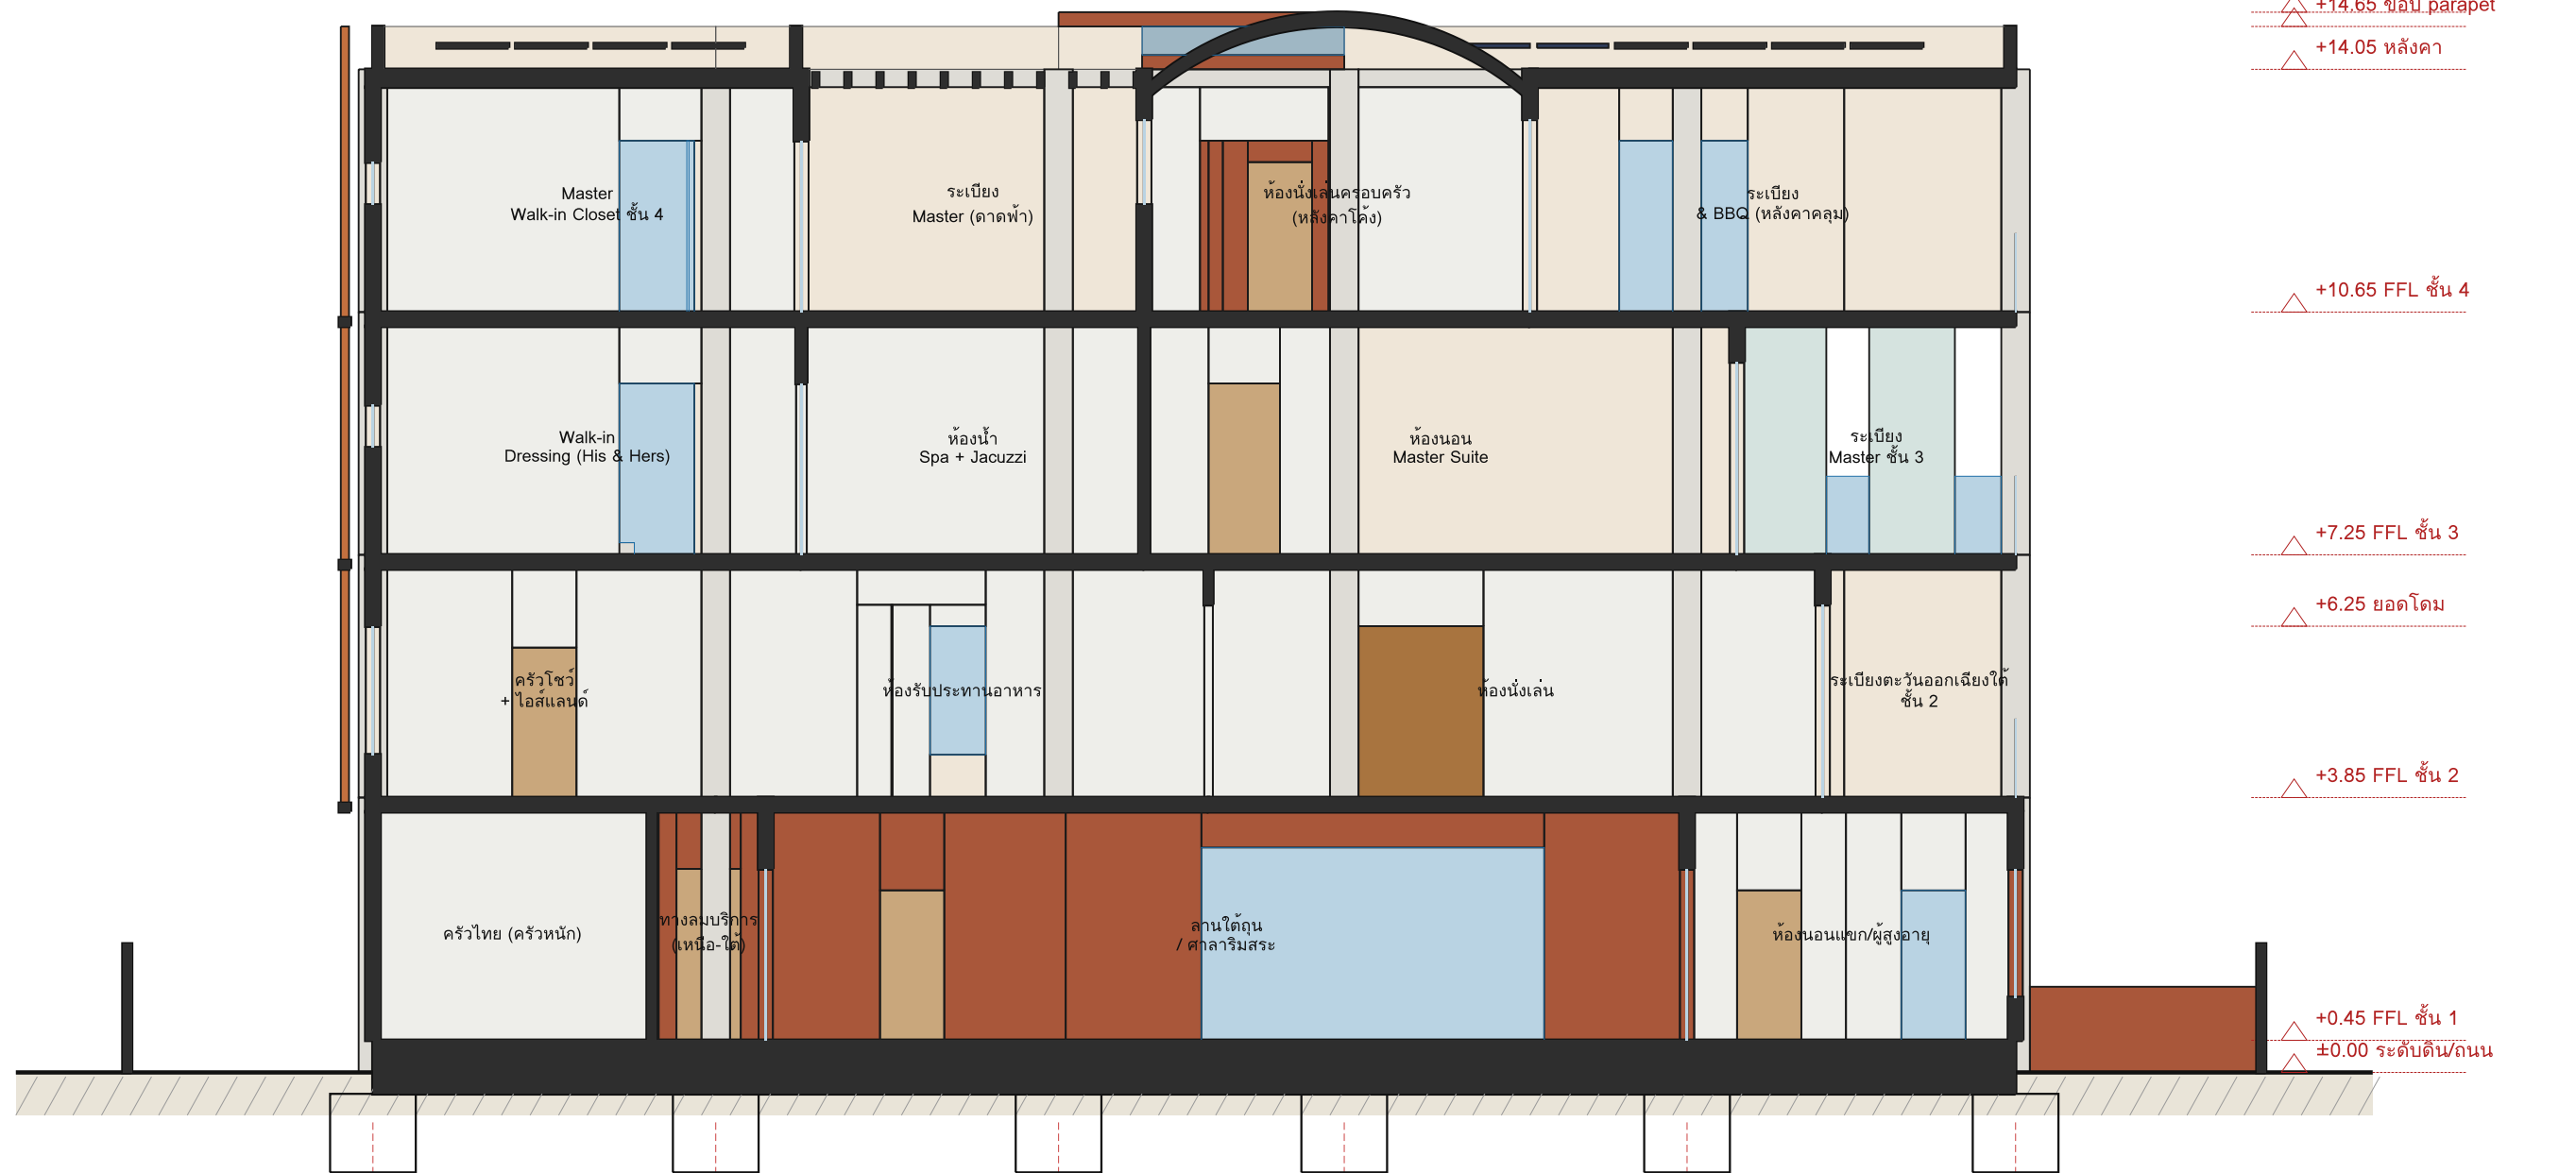

รูปตัด B-B (ตัดแนวเหนือ-ใต้ ผ่านโดมอิฐ-โก่งทางเข้า-โก่งกลาง-ลานใต้ถุน / ห้องนั่งเล่น-ทางเดิน-ห้องไวน์ / ห้องนอน Master-ลงเจีย / BBQ-ห้องเสิร์ฟเตอร์ มองไปทิศตะวันออก) 1:100



หมายเหตุรูปตัด

- พื้นถึงพื้น 3.40 ม. = พื้น 0.20 + ผัง/งานระบบ 0.40 + โปรง 2.80 ม. (ตามความสูงในโปรแกรม)
- เสาค้ำ/ฐานรากเขียนเป็นสัญลักษณ์ — ขนาดจริงตามวิศวกรโครงสร้าง
- รูปตัด A-A คัดผ่านหลังคาโค้ง (ภาคตัดเปลือก) • รูปตัด B-B คัดผ่านกลางโถมอิฐ (ผนัง 0.24 + oculus)
- หลังคาสวน +3.85 / +7.25: ดินปลูก 150 มม. น้ำหนักขึ้นน้ำ ~250-300 กก./ตร.ม.

H3A DESIGN AND BUILD

K-UNIT Architecture Lab

โครงการ

WELL-KILN 30x30

Executive Luxury Villa
บ้านเดี่ยว 4 ชั้น ผ่านเกณฑ์
WELL for Residential (เจตนา)

ที่ดิน 30.00 x 30.00 ม. = 225 ตร.ว.
ถนนสาธารณะทิศเหนือ (สมบัติ 8.00 ม.)

แนวคิด

ค่าความจาก Intrinsic (Chain10):

ปล่องอิฐ (บันไดลิฟต์) +14.85

ระดับ

หลังคา +14.05 · parapet +14.65
ขอบปล่อง/หลังคาโค้ง +14.85

หมายเหตุ

- หน่วยเป็นมิลลิเมตร เว้นแต่ระบุ
ระดับอ้างอิงถนนหน้าที่ดิน ± 0.00
ห้ามวัดขนาดจากแบบ ใช้ตัวเลขกำกับ
แบบระดับ Design Development
ต้องให้สถาปนิกและวิศวกรผู้ได้รับ
ใบอนุญาตตรวจสอบและลงนาม
ก่อนยื่นขออนุญาต

ชื่อแผ่น

รูปตัด A-A
รูปตัด B-B

มาตราส่วน 1:100

วันที่ 6 ต.ค. 2569 ฉบับ v1 / DD

WELL-KILN 30x30 · Executive Luxury Villa · บ้านเดี่ยว 4 ชั้น "บ้านเตาเผา" — โคมอิฐ + ปล้องอิฐ + หงคาโค้งดินเผา (แนวคิดจาก Intrinsic / Chain10)

ที่ดิน 30.00 x 30.00 ม. (225 ตร.ว.) · ถนน (สมมติ 8.00 ม.) ที่ดินเดิม · โปรแกรม ARCHSPACE 6 ต.ค. 2569

ตารางของเปิด (97 รายการ) — หน่วย มม. วัดจาก FFL

รหัส	ชั้น	ชนิด	กว้าง	ขอมล้น	ขอมบน	ค่าผนัง
D01	F1	ประตูลิฟต์	900	0	2100	โถงลิฟต์ ลิฟต์บ้าน
D02	F1	ประตูบานเปิดคู่	1800	0	2400	โรงแรงรถ 4 คัน โถงลิฟต์รอบ (จาก
SD01	F1	ประตูบานเลื่อนกระจก	4800	0	2700	ลานใต้ถุน / ศาลา โถงกลาง
D03	F1	ประตูบานเปิดเดี่ยว	900	0	2400	ทางวนบริการ (บน) ภายนอก-S
D04	F1	ประตูบานเปิดเดี่ยว	900	0	2400	ทางวนบริการ (บน) โรงแรงรถ 4 คัน
SD02	F1	ประตูบานเลื่อนกระจก	1800	0	2400	ทางวนบริการ (บน) ลานใต้ถุน / ศาลา
D05	F1	ประตูบานเปิดเดี่ยว	900	0	2100	ครัวไทย (ครัวห่อ) ภายนอก-W
D06	F1	ประตูบานเปิดเดี่ยว	900	0	2100	ลานใต้ถุน / ศาลา ห้องซักผ้า
D07	F1	ประตูบานเปิดเดี่ยว	900	0	2100	โถงกลาง ตู้เสื้อผ้า
D08	F1	ประตูบานเปิดเดี่ยว	900	0	2100	ห้องนอนแขกตู้เสื้อผ้า ตู้เสื้อผ้า
SD03	F1	ประตูบานเลื่อนกระจก	900	0	2100	ห้องนอนแขกตู้เสื้อผ้า ห้องครัวห้องแขก
SD04	F1	ประตูบานเลื่อนกระจก	2400	0	2400	ลานใต้ถุน / ศาลา ห้องนอนแขกตู้เสื้อผ้า
D09	F1	ประตูบานเปิดเดี่ยว	800	0	2100	ห้องซักผ้า โถงกลาง
D10	F1	ประตูบานเปิดเดี่ยว	800	0	2100	โถงทางเข้า (หลัง) ห้องเก็บของ B
D11	F1	ประตูบานเปิดเดี่ยว	800	0	2100	โถงทางเข้า (หลัง) ห้องเก็บของ /
D12	F1	ประตูบานเปิดเดี่ยว	900	0	2400	ครัวไทย (ครัวห่อ) ทางวนบริการ (
D13	F1	ประตูบานเปิดเดี่ยว	900	0	2400	ห้องนอน 2 ทางวนบริการ (
D14	F1	ประตูบานเปิดเดี่ยว	800	0	2100	ห้องนอนบ้าน ทางวนบริการ (
D15	F1	ประตูบานเปิดเดี่ยว	900	0	2400	ห้องนอน 1 ทางวนบริการ (
D16	F1	ประตูบานเปิดเดี่ยว	800	0	2100	ทางวนบริการ (บน) ห้อง MEP / T&H
W01	F1	หน้าต่าง	2400	600	2400	ครัวไทย (ครัวห่อ) ภายนอก-S
W02	F1	หน้าต่าง	1800	600	2400	ครัวไทย (ครัวห่อ) ภายนอก-W
W03	F1	หน้าต่าง	1800	600	2400	ห้องนอน 2 ภายนอก-W
W04	F1	หน้าต่าง	600	1500	2100	ห้องนอนบ้าน ภายนอก-W
W05	F1	หน้าต่าง	1500	600	2400	ห้องนอน 1 ภายนอก-W
W06	F1	หน้าต่าง	2700	600	2400	ห้องนอนแขกตู้เสื้อผ้า ภายนอก-E
W07	F1	หน้าต่าง	1200	1500	2100	ห้องครัวห้องแขก ภายนอก-E
W08	F1	หน้าต่าง	1200	1500	2100	ห้องเก็บเสื้อผ้า ภายนอก-E
W09	F1	หน้าต่าง	1200	1500	2100	ห้องเก็บของ / S ภายนอก-N
W10	F1	หน้าต่าง	1200	1500	2100	ห้องเก็บของ / S ภายนอก-E
W11	F1	ผนังกระจก	1400	0	2700	โถงลิฟต์รอบ (จากโรง) ภายนอก-N
D17	F2	ประตูลิฟต์	900	0	2100	โถงลิฟต์ ชั้น 2 ลิฟต์บ้าน
D18	F2	ประตูบานเปิดคู่	1800	0	2400	ห้องลิ้นชัก ทางเดินชั้น 2
D19	F2	ประตูบานเปิดเดี่ยว	900	0	2100	ครัวไทย + ไลต์ Walk-in Pantry
D20	F2	ประตูบานเปิดเดี่ยว	800	0	2100	ห้องนอน Junior S ตู้เสื้อผ้า Jb
D21	F2	ประตูบานเปิดเดี่ยว	800	0	2100	ตู้เสื้อผ้า Junior ห้องนอน Junior
D22	F2	ประตูบานเปิดเดี่ยว	800	0	2100	ตู้เสื้อผ้า Junior ห้องนอน Junior
D23	F2	ประตูบานเปิดเดี่ยว	800	0	2100	ตู้เสื้อผ้า Junior ห้องนอน Junior
SD05	F2	ประตูบานเลื่อนกระจก	3600	0	2700	ห้องลิ้นชัก ระเบียงระเบียง
D24	F2	ประตูบานเปิดเดี่ยว	900	0	2100	ระเบียงระเบียงนอก อินโดนีเซียภายนอก
D25	F2	ประตูบานเปิดเดี่ยว	800	0	2100	ทางเดินชั้น 2 ซ ตู้เสื้อผ้า Jb
D26	F2	ประตูบานเปิดเดี่ยว	800	0	2100	ทางเดินชั้น 2 ซ ห้องโถง / ซีก
D27	F2	ประตูบานเปิดเดี่ยว	900	0	2400	ทางเดินชั้น 2 ซ ห้องนอน Junior
D28	F2	ประตูบานเปิดเดี่ยว	800	0	2100	ทางเดินชั้น 2 ซ ห้องน้ำจาก (Po
W12	F2	หน้าต่าง	3000	600	2400	ครัวไทย + ไลต์ ภายนอก-S
W13	F2	หน้าต่าง	3600	600	2400	ครัวไทย + ไลต์ ภายนอก-W
W14	F2	หน้าต่าง	4500	600	2400	ห้องรับประทานอาหาร ภายนอก-S
W15	F2	หน้าต่าง	4200	600	2400	ห้องลิ้นชัก ภายนอก-S
W16	F2	หน้าต่าง	600	1500	2100	ห้องน้ำจาก (Powd ภายนอก-E

รหัส	ชั้น	ชนิด	กว้าง	ขอมล้น	ขอมบน	ค่าผนัง
W17	F2	หน้าต่าง	3000	600	2400	ห้องนอน Junior S ภายนอก-N
W18	F2	หน้าต่าง	2700	600	2400	ห้องนอน Junior S ภายนอก-W
W19	F2	หน้าต่าง	600	1500	2100	ห้องน้ำ Junior S ภายนอก-N
W20	F2	หน้าต่าง	1200	1500	2100	ห้องน้ำ Junior S ภายนอก-N
W21	F2	หน้าต่าง	3000	600	2400	ห้องนอน Junior S ภายนอก-N
W22	F2	หน้าต่าง	2700	600	2400	ห้องนอน Junior S ภายนอก-E
W23	F2	หน้าต่าง	3000	600	2400	ห้องทำงาน & ห้อง ภายนอก-N
W24	F2	หน้าต่าง	3600	600	2400	ห้องทำงาน & ห้อง ภายนอก-W
W25	F2	หน้าต่าง	3600	600	2400	ห้องทำงาน & ห้อง ภายนอก-E
W26	F2	หน้าต่าง	600	300	3000	อินโดนีเซีย (ปล่อง) ภายนอก-N
D29	F3	ประตูลิฟต์	900	0	2100	โถงลิฟต์ ชั้น 3 ลิฟต์บ้าน
D30	F3	ประตูบานเปิดเดี่ยว	1000	0	2400	ห้องนอน Master S โถงบันได ชั้น
D31	F3	ประตูบานเปิดเดี่ยว	900	0	2400	ห้องน้ำ Spa + Ja ห้องนอน Master
SD06	F3	ประตูบานเลื่อนกระจก	900	0	2400	Walk-in Dressing ห้องน้ำ Spa +
SD07	F3	ประตูบานเลื่อนกระจก	3600	0	2700	ห้องนอน Master S ระเบียง Master
W27	F3	หน้าต่าง	2400	900	2400	ห้องน้ำ Spa + Ja ภายนอก-S
SD08	F3	ประตูบานเลื่อนกระจก	1200	0	2400	โถงบันได ชั้น 3 ล็อบลิ้นชัก
D32	F3	ประตูบานเปิดเดี่ยว	900	0	2100	ระเบียง Master S อินโดนีเซียภายนอก
D33	F3	ประตูบานเปิดเดี่ยว	800	0	2100	ห้องเก็บของชั้น โถงบันได ชั้น
W28	F3	หน้าต่าง	1200	1500	2100	Walk-in Dressing ภายนอก-S
W29	F3	หน้าต่าง	1200	1500	2100	Walk-in Dressing ภายนอก-W
W30	F3	หน้าต่าง	600	1500	2100	ห้องน้ำ Spa + Ja ภายนอก-S
W31	F3	หน้าต่าง	600	1500	2100	ห้องน้ำ Spa + Ja ภายนอก-S
W32	F3	หน้าต่าง	4800	600	2400	ห้องนอน Master S ภายนอก-S
W33	F3	ผนังกระจก	4200	0	3000	อินโดนีเซีย Mas ภายนอก-N
W34	F3	ผนังกระจก	1600	0	3000	อินโดนีเซีย Mas ภายนอก-W
W35	F3	หน้าต่าง	1200	1500	2100	ห้องเก็บของชั้น ภายนอก-N
W36	F3	หน้าต่าง	600	300	3000	อินโดนีเซีย (ปล่อง) ภายนอก-N
W37	F3	หน้าต่าง	600	300	3000	อินโดนีเซีย (ปล่อง) ภายนอก-W
D34	F4	ประตูลิฟต์	900	0	2100	โถงลิฟต์ ชั้น 4 ลิฟต์บ้าน
SD09	F4	ประตูบานเลื่อนกระจก	2400	0	2400	Master Walk-in C ระเบียง Master
SD10	F4	ประตูบานเลื่อนกระจก	3600	0	2700	ห้องลิ้นชักจากบน ระเบียง & BBQ
W38	F4	หน้าต่าง	3000	1500	2700	ระเบียง Master (ห้องลิ้นชัก
SD11	F4	ประตูบานเลื่อนกระจก	1800	0	2400	ระเบียง & BBQ (พ) ทางเดินชั้น 4
D35	F4	ประตูบานเปิดเดี่ยว	900	0	2100	ระเบียง & BBQ (พ) อินโดนีเซียภายนอก
W39	F4	หน้าต่าง	3000	600	2400	ห้องโถงลิ้นชัก ภายนอก-N
D36	F4	ประตูบานเปิดเดี่ยว	800	0	2100	ห้องอุปกรณ์ AV // โถงบันได ชั้น
D37	F4	ประตูบานเปิดเดี่ยว	900	0	2400	ทางเดินชั้น 4 ห้องโถงลิ้นชัก
D38	F4	ประตูบานเปิดเดี่ยว	800	0	2100	ทางเดินชั้น 4 ห้องน้ำชั้น 4
W40	F4	หน้าต่าง	1200	1500	2100	Master Walk-in C ภายนอก-S
W41	F4	หน้าต่าง	1200	1500	2100	Master Walk-in C ภายนอก-W
W42	F4	หน้าต่าง	3600	600	2400	ห้องลิ้นชักรอบ ภายนอก-S
W43	F4	ผนังกระจก	4200	0	3000	อินโดนีเซีย Mas ภายนอก-N
W44	F4	ผนังกระจก	1600	0	3000	อินโดนีเซีย Mas ภายนอก-W
W45	F4	หน้าต่าง	1200	1500	2100	ห้องอุปกรณ์ AV // ภายนอก-N
W46	F4	หน้าต่าง	600	1500	2100	ห้องน้ำชั้น 4 ภายนอก-E
W47	F4	หน้าต่าง	600	300	3000	อินโดนีเซีย (ปล่อง) ภายนอก-N
W48	F4	หน้าต่าง	600	300	3000	อินโดนีเซีย (ปล่อง) ภายนอก-W

0.39 ข้อ 6 ของเปิด >= 10% ของพื้นที่ห้อง

ห้อง	ข้อเปิดพื้นที่ห้อง	ผล
F1 ครัวไทย (ครัวห่อ)	49.9% (8.13/19.89)	ผ่าน
F1 ห้องนอน 2	28.6% (3.24/11.31)	ผ่าน
F1 ห้องน้ำบ้าน	6.2% (0.36/5.85) -> พัดลมระบายอากาศ (ข้อ 6 วรร	ผ่าน
F1 ห้องนอน 1	27.7% (2.70/9.75)	ผ่าน
F1 ห้องซักผ้า	14.0% (1.89/13.53)	ผ่าน
F1 ห้อง MEP / ไฟฟ้า / เครื่องปรับอากาศ	0.0% (0.00/17.22) -> พัดลมระบายอากาศ (ข้อ 6 วรร	ผ่าน
F1 ห้องนอนแขกตู้เสื้อผ้า	51.3% (10.62/20.70)	ผ่าน
F1 ตู้เสื้อผ้าห้องแขก	0.0% (0.00/6.67) -> พัดลมระบายอากาศ (ข้อ 6 วรร	ผ่าน
F1 ห้องน้ำห้องแขก	10.8% (0.72/6.67)	ผ่าน
F1 ห้องเก็บเสื้อผ้า	7.5% (0.72/9.66) -> พัดลมระบายอากาศ (ข้อ 6 วรร	ผ่าน
F1 ห้องเก็บของ / อีกราย	12.5% (1.44/11.50)	ผ่าน
F2 ครัวไทย + ไลต์	42.7% (11.88/27.84)	ผ่าน
F2 ห้องรับประทานอาหาร	29.2% (8.10/40.02)	ผ่าน
F2 ห้องลิ้นชัก	34.6% (17.28/49.88)	ผ่าน
F2 Walk-in Pantry & ห้องเก็บ	0.0% (0.00/9.00) -> พัดลมระบายอากาศ (ข้อ 6 วรร	ผ่าน
F2 ห้องน้ำจาก (Powder)	7.2% (0.36/5.00) -> พัดลมระบายอากาศ (ข้อ 6 วรร	ผ่าน
F2 ห้องนอน Junior Suite 2	50.9% (10.26/20.16)	ผ่าน
F2 ตู้เสื้อผ้า Junior Suite 2	0.0% (0.00/5.04) -> พัดลมระบายอากาศ (ข้อ 6 วรร	ผ่าน
F2 ห้องน้ำ Junior Suite 2	7.1% (0.36/5.04) -> พัดลมระบายอากาศ (ข้อ 6 วรร	ผ่าน
F2 ห้องโถง / ซีก	0.0% (0.00/9.24) -> พัดลมระบายอากาศ (ข้อ 6 วรร	ผ่าน
F2 ตู้เสื้อผ้า Junior Suite 3	0.0% (0.00/5.04) -> พัดลมระบายอากาศ (ข้อ 6 วรร	ผ่าน
F2 ห้องน้ำ Junior Suite 3	14.3% (0.72/5.04)	ผ่าน
F2 ห้องนอน Junior Suite 3	50.9% (10.26/20.16)	ผ่าน
F2 ห้องทำงาน & ห้องนอน	79.8% (18.36/25.92)	ผ่าน
F3 Walk-in Dressing (His & Hers)	4.1% (1.44/34.80) -> พัดลมระบายอากาศ (ข้อ 6 วรร	ผ่าน
F3 ห้องน้ำ Spa + Jacuzzi	15.5% (4.32/27.84)	ผ่าน
F3 ห้องนอน Master Suite	38.1% (18.36/48.14)	ผ่าน
F3 ห้องเก็บของชั้น 3	6.8% (0.72/10.56) -> พัดลมระบายอากาศ (ข้อ 6 วรร	ผ่าน
F4 Master Walk-in Closet ชั้น 4	29.7% (7.20/34.80)	ผ่าน
F4 ห้องลิ้นชักเครื่องครัว (หลังคาไม้	72.9% (22.83/31.32)	ผ่าน
F4 ห้องอุปกรณ์ AV / เก็บของ	6.8% (0.72/10.56) -> พัดลมระบายอากาศ (ข้อ 6 วรร	ผ่าน
F4 ห้องน้ำชั้น 4	7.2% (0.36/5.00) -> พัดลมระบายอากาศ (ข้อ 6 วรร	ผ่าน
F4 ห้องโถงลิ้นชัก	13.7% (5.40/39.48)	ผ่าน

ระบายอากาศ >= 2 แนวหนึ่ง (เกณฑ์ภายใน สบสนน R-T06) / ลึก <= 4.20 ม.

ห้อง/ใช้งานประจำ	ข้อเปิด	ลึกจากผนังนอก	ผล
F1 ครัวไทย (ครัวห่อ)	2 แนวหนึ่ง	3.75 ม.	ผ่าน
F1 ห้องนอน 2	1 แนวหนึ่ง -> ยกเว้น: ม	3.75 ม.	ผ่าน
F1 ห้องนอน 1	1 แนวหนึ่ง -> ยกเว้น: ม	3.75 ม.	ผ่าน
F1 ห้องนอนแขกตู้เสื้อผ้า	2 แนวหนึ่ง	2.25 ม.	ผ่าน
F2 ครัวไทย + ไลต์	2 แนวหนึ่ง	4.65 ม. -> ยกเว้น: หน้าต่าง 2	ผ่าน
F2 ห้องรับประทานอาหาร	2 แนวหนึ่ง	5.55 ม. -> ยกเว้น: กระจกเก็บสน	ผ่าน
F2 ห้องลิ้นชัก	2 แนวหนึ่ง	5.55 ม. -> ยกเว้น: เปิด 2 ด้าน	ผ่าน
F2 ห้องนอน Junior Suite 2	2 แนวหนึ่ง	4.05 ม.	ผ่าน
F2 ห้องนอน Junior Suite 3	2 แนวหนึ่ง	4.05 ม.	ผ่าน
F2 ห้องทำงาน & ห้องนอน	3 แนวหนึ่ง	2.25 ม.	ผ่าน
F3 ห้องนอน Master Suite	2 แนวหนึ่ง	3.45 ม.	ผ่าน
F4 ห้องลิ้นชักเครื่องครัว (หลังคาไม้	3 แนวหนึ่ง	2.55 ม.	ผ่าน
F4 ห้องโถงลิ้นชัก	1 แนวหนึ่ง -> ยกเว้น: พ	4.05 ม.	ผ่าน

ตารางขนาดเปิดเปิด (ลบยกเว้นจากนอก) 18 รายการ: ผ่าน 18

เทียบโปรแกรม ARCHSPACE (ตร.ม.)

รายการโปรแกรม	ชั้น	โปรแกรม	ชั้นบน	แบบ	ค่า
Grand Double-Height Foyer	F1	24.00	F1	24.63	+0.63
Formal Living Room	F2	50.00	F2	49.88	-0.12
Dining Room (10-12 Seats)	F2	40.00	F2	40.02	+0.02
Powder Room	F2	6.00	F2	5.00	-1.00
Home Theater / AV Lounge	F4	36.00	F4	39.48	+3.48
Wine Cellar / Cigar Room	F2	14.00	F2	9.24	-4.76
Master Suite Bedroom	F3	48.00	F3	48.14	+0.14
Master Walk-in (His & Hers)	F3	32.00	F3	34.80	+2.80
Spa Master Bath + Jacuzzi	F3	28.00	F3	27.84	-0.16
Junior Suite 2 (bath+closet)	F2	34.00	F2	30.24	-3.76
Junior Suite 3 (bath+closet)	F2	34.00	F2	30.24	-3.76
Guest Suite (CF / elderly)	F1	30.00	F1	34.04	+4.04
Family Lounge & Upper Gallery	F4	36.00	F4	31.32	-4.68
Executive Home Office & Library	F2	26.00	F2	25.92	-0.08
Master Walk-in Closet (UL)	F4	36.00	F4	34.80	-1.20
Show Kitchen & Island Bar	F2	28.00	F2	27.84	-0.16
Heavy Thai Kitchen	F1	20.00	F1	19.89	-0.11
Walk-in Pantry & Cold Storage	F3	12.00	F2	9.60	-2.40
Laundry & Utility Room	F1	16.00	F1	13.53	-2.47
Maid Bedroom 1 & 2	F1	22.00	F1	21.06	-0.94
Maid Bathroom	F1	6.00	F1	5.85	-0.15
MEP / Electrical / Generator	F1	14.00	F1	17.22	+3.22
Covered Garage 3-4 cars	F1	85.00	F1	84.50	-0.50
Covered Veranda & BBQ	F4	45.00	F4	39.44	-5.56
Upper Master Terrace	F4	28.00	F4	27.84	-0.16
Poolside Pavilion	F1	35.00	F1	58.05	+23.05
รวม NJA		785.00		790.41	+5.41

แบบชุด = ชั้นในแบบต่างๆจากโปรแกรม (Pantry ชั้น 3 -> 2 ตามที่เลือก ถึง A-01 ข้อ 2) · ศาลารับแขก = ลานใต้ถุนชั้น 1 ส่วนล่างพื้นที่คือ: ห้องตามีขนาด 15.00 ม. ดินชั้นล่าง 10-15% -> พื้นที่ต่ำกว่าโปรแกรมเกิน 10% คูณค่า "ค่า" คูณ

H3A DESIGN AND BUILD

X-UNIT Architecture Lab

โครงการ

WELL-KILN 30x30

Executive Luxury Villa

บ้านเดี่ยว 4 ชั้น ผ่านเกณฑ์

WELL for Residential (เจดนา)

ที่ดิน 30.00 x 30.00 ม. = 225 ตร.ว.
ถนนสาธารณะติดเหนือ (สมมติ 8.00 ม.)

แนวคิด

ตีความจาก Intrinsic (Chain10):

โดยมี "เตาเผา" Ø5.60 เป็นใจกลางรับ

+ ปล้องอิฐ (บันได+ลิฟต์) +14.85

+ หงคาโค้งดินเผา + ครึ่งดินเผา

ระดับ

±0.00 ถนน · F1 +0.45 · F2 +3.85
F3 +7.25 · F4 +10.65 · โดม +6.25
หลังคา +14.05 · parapet +14.65
ยอดปล้องหลังคาโค้ง +14.85

หมายเหตุ

- หน่วยงานเป็นผลิตภัณฑ์ เว้นแต่ระบุ
- ระดับอ้างอิงถนนพื้นที่ดิน ±0.00
- ห้ามวัดขนาดจากแบบ ใช้ตัวเลขกำกับ
- มาตรฐาน Design Development

ต้องให้สถาปนิกและวิศวกรผู้ได้รับ

ใบอนุญาตตรวจสอบและลงนาม

ก่อนยื่นขออนุญาต

ชื่อแผ่น

ตารางประตู-หน้าต่าง

+ ตารางของเปิด + เทียบโปรแกรม

มาตรฐาน: ไม่มีมาตรฐาน

วันที่ 6 ค.ค. 2569 ฉบับ v1 / DD

กลยุทธ์ WELL for Residential (รหัสตาม Guidebook ก.พ. 2026)

Feature (WELL for Residential)	การตอบสนองในรูปแบบ	สถานะ	หลักฐานที่ต้องมี
R-A01 ระบบระบายอากาศ	พัดลมดูดเฉพาะจุดครัว/ห้องน้ำห้องไม่มีหน้าต่าง 14 ห้อง + ERV ห้องนอน	ระบุในแบบงานระบบ	ต้องวัด
R-A05 ลดการเผาไหม้	ครัวโซว์ชั้น 2 เตาไฟฟ้าเหนี่ยวนำ; ครัวไทยชั้น 1 แก๊ส ยึดถ + หน้าต่าง 2 ด้าน	ในแบบ	เอกสาร
R-A09 จุดชาร์จ EV	1 จุดในโรงจอดรถ (ต่อเมื่อ 4 ช่อง)	ในแบบ	ภาพถ่าย
R-W03 น้ำที่มิใช่ น้ำดื่ม	ถังน้ำฝนใต้ดิน ~12 ลบ.ม. สำหรับรดน้ำ/ซักโครก	ในแบบ	แบบสุขาภิบาล
R-L01 แสงธรรมชาติ	39.4% (143.8/364.6 ตร.ม.) -> ระดับ 3	คำนวณแล้ว	ต้องตรวจแสงจ้า
R-L02 ควบคุมแสง	วงจรแยกทุกห้อง + ม่านปิดห้องนอน/เฮียเตอร์	ระบุ	แบบไฟฟ้า
R-T06 หน้าต่างเปิดได้	13/13 ห้อง	คำนวณแล้ว	มั่งควด/ตัวล็อก
R-T07 ความร้อนภายนอก	หลังคาสวน 3 ส่วน + หลังคาขาว SR >= 0.75 + ครีบลินเผาที่ตะวันตก + ต้นไม้ร่ม	ในแบบ	ค่า SR วัสดุ
R-V04 พื้นที่กิจกรรมกลางแจ้ง	สระ 14.00 x 3.00 ม. + ลานใต้ถุน + ลอดเจีย + ระเบียงทุกชั้น	ในแบบ	-
R-V07 ออกแบบบันได	บันไดในปล่องอิฐ ช่องแสงหลังคา + ช่องหน้าต่างแนวตั้ง อยู่หน้าโรงทุกชั้น (ใช้ก้อนลิฟต์)	ในแบบ	ภาพถ่าย
R-M01 ธรรมชาติและสถานที่	วัสดุดิน (อิฐ ดินเผา ปูนขาว เศษเซรามิก) + มอสสวนสระทิศใต้	ในแบบ	-
R-M04 พื้นที่จัดเก็บ	Walk-in 2 ชั้น (Master) + ตู้ทุกห้องนอน + ห้องเก็บของทุกชั้น	ในแบบ	-
R-N01 การปรุงอาหาร	ครัว 2 ส่วน (โซว์/ไทย) + Pantry ห้องเย็นติดครัวโซว์	ในแบบ	-
R-S01 แนวกันเสียง	ห้องนอน Master ทิศใต้ไกลถนน; Junior Suite ทิศเหนือ -> กระจก 2 ชั้น	ต้องระบุ STC	ทดสอบ
R-C01 ออกแบบเพื่อทุกคน	ลิฟต์บ้านทุกชั้น + ห้องแขกชั้น 1; ทางลาด 1:12 ยังต้องเพิ่ม	บางส่วน	ดู A-01 ข้อ 6
R-C06 กายพิบัตื	ยกพื้น +0.45 + บันไดหนีไฟ + เครื่องบันไฟ	ในแบบ	ระดับน้ำท่วมจริง?
R-X02 วัสดุ	ปูน calceo/สี VOC ต่ำ ไม้รับรอง FSC เซรามิกไร้ไซเคิล	สเปก	ใบสั่งซื้อ

สถานะ = เจตนาการออกแบบ ยังไม่ใช่คะแนนรับรอง: WELL Residence ต้องลงทะเบียน JWBI ส่งเอกสาร และตรวจวัดจริงหลังก่อสร้าง
ห้องที่ใช้พัฒนาะบาย: ห้องน้ำแม่บ้าน, ห้อง MEP / ไฟฟ้า / เครื่องขึ้นไฟ, ตู้เสื้อผ้าห้องแขก, ห้องกันเสียงใต้ท, Walk-in Pantry & ห้องเย็น, ห้องน้ำแขก (Powder), ตู้เสื้อผ้า Junior Suite 2, ห้องน้ำ Junior Suite 2, ห้องโถงไม้ / ซิการ์, ตู้เสื้อผ้า Junior Suite 3, Walk-in Dressing (His & Here), ห้องเก็บของชั้น 3, ห้องอุปกรณ์ AV / เก็บของ, ห้องน้ำชั้น 4

มุมมองทิศตะวันตกเฉียงเหนือ — ห้องทำงานบนหลังคาสวนโรงรถ ปล่องอิฐ ครีบลินเผา โคมอิฐ



วัสดุหลัก

หมวด	ข้อกำหนด (ระดับแนวคิด)
โครงสร้าง	ค.ส.ล. เสา 0.40x0.40 กริด 6 x 4 แนว · พื้นคานแบน 0.20 · คานถ่ายแรงห้องทำงานเหนือโรงรถ · เสาเข็มเจาะ (รพผลเจาะดิน)
โคม / ปล่อง	เปลือก ค.ส.ล. รับแรง + อิฐโซว์แนวกรู (แบบแสดงหนา 240 / 200 — ต้องยื่นยื่น) · บันได ค.ส.ล.
หลังคาโค้ง	เปลือก ค.ส.ล. 120 ช่วง 5.40 ม. + กันซึม + กระเบื้องดินเผา · ซุ้มอิฐหัวท้าย · หน้าต่างโค้ง Low-E
ผนังภายนอก	ชั้น 1 อิฐทนไฟ/อิฐโซว์ · ชั้น 2-4 บล็อกมวลเบา 200 + ปูนฉาบ calce · ผนังภายใน 120 / ห้องน้ำ 150
ฉาก / ครีบล	ครีบลินเผา 115 x 80 @300 บนโครงเหล็กกล้าวโนซ์ · กระจกตัว U (channel glass) ลอดเจียชั้น 3
กระจก	Low-E laminated · SHGC <= 0.25 ทิศ ตก/ออก · กรอบอะลูมิเนียมสีเทาเข้ม
พื้น	โมเสกเซรามิกไร้ไซเคิลเส้นโค้ง (ชั้น 1 โถง/ลานใต้ถุน/โคม) · ไม้เอ็นจิเนียร์ (ชั้น 2-4) · กระเบื้องกันสั่น R11
ภายนอก	สระน้ำเกลือ 14.00 x 3.00 ลึก 1.40 ม. · พื้น WPC รอบสระ · บันไดหนีไฟเหล็กกล้าวโนซ์

สิ่งที่ต้องทำต่อ

- วิศวกรโครงสร้าง: เปลือกโคม หลังคาโค้ง ปล่องอิฐ คานถ่ายแรงห้องทำงาน หลังคาสวน เสาเข็ม
- วิศวกรงานระบบ: VRF + ERV, พัฒาระบาย, ระบบน้ำฝน, เครื่องขึ้นไฟ, โซลาร์ 14.30 kWp
- ยื่นยื่นกับสำนักงานเขต: บันไดหนีไฟ (ข้อ 27) สำหรับบ้านเดี่ยว 4 ชั้น, ความกว้างถนนจริง, ผังเมืองรวม
- จำลอง CFD/ความร้อน: ทางลมเหนือ-ใต้ และ stack effect ในปล่องอิฐ (ยังเป็นสมมติฐาน); จำลองแสงจ้าห้องหลัก
- แบบขยาย: ทางลาด 1:12, โคม/oculus กันน้ำ, หลังคาโค้ง, ครีบลินเผา, ฉากกระจก U, บันไดส่วนตัว, สระ
- ลงทะเบียน WELL Residence และเตรียมเอกสารตามตาราง
- ประมาณราคาละเอียด (BOQ) หลังได้แบบโครงสร้าง-งานระบบ

สรุปการตรวจ

ผลตรวจทั้งหมด 111 รายการ: ผ่าน 111 / ไม่ผ่าน 0 (รายการ "ยกเว้น" มีเหตุผลกำกับ ดู A-11)
แบบระดับ design development ต้องให้สถาปนิกและวิศวกรผู้ได้รับใบอนุญาตตรวจสอบและลงนามก่อนยื่นขออนุญาต

จากสวนทิศใต้ — ลานใต้ถุน ฐานอิฐ หน้าต่างโค้งปากเตาชั้น 4 บันไดหนีไฟ



H3A DESIGN AND BUILD

X-UNIT Architecture Lab

โครงการ

WELL-KILN 30x30

Executive Luxury Villa
บ้านเดี่ยว 4 ชั้น ผ่านเกณฑ์
WELL for Residential (เจตนา)

ที่ดิน 30.00 x 30.00 ม. = 225 ตร.ว.
ถนนสาธารณะทิศเหนือ (สมมติ 8.00 ม.)

แนวคิด

ตีความจาก Intrinsic (Chain10):
โคมอิฐ "เตาเผา" Ø5.60 เป็นโถงต้อนรับ
+ ปล่องอิฐ (บันได+ลิฟต์) +14.85
+ หลังคาโค้งดินเผา + ครีบลินเผา

ระดับ

±0.00 ถนน · F1 +0.45 · F2 +3.85
F3 +7.25 · F4 +10.65 · โคม +6.25
หลังคา +14.05 · parapet +14.65
ยอดปล่องหลังคาโค้ง +14.85

หมายเหตุ

- หน่วยงานเป็นผลิตภัณฑ์ เว้นแต่ระบุ
 - ระดับล่างลิฟต์ถนนพื้นที่ดิน ±0.00
 - ห้ามวัดขนาดจากแบบ ใช้ตัวเลขกำกับ
 - แบบระดับ Design Development
- ต้องให้สถาปนิกและวิศวกรผู้ได้รับ
ใบอนุญาตตรวจสอบและลงนาม
ก่อนยื่นขออนุญาต

ชื่อแผ่น

WELL for Residential
+ วัสดุ + สิ่งที่ต้องทำต่อ

มาตราส่วน: ไม่มีมาตราส่วน

วันที่ 6 ต.ค. 2569 ฉบับ v1 / DD